

GENERAL NOTES AS APPLICABLE

GENERAL NOTE

DO NOT SCALE OFF DRAWINGS, ONLY USE FIGURED DIMENSION. BUILDER IS TO VERIFY ALL DIMENSIONS PRIOR TO COMMENCING AND WORK/CONSTRUCTION & ORDERING OF MATERIALS. BUILDER TO CONFIRM RL'S ON SITE PRIOR TO COMMENCEMENT OF EARTHWORKS.

ALL WORK PERFORMED SHALL ADHERE TO THE MINIMUM STANDARDS SETOUT & PRESCRIBED BY THE RELEVANT AUSTRALIAN STANDARDS, THE NATIONAL CONSTRUCTION CODE'S BUILDING CODE OF AUSTRALIA, AND THE REQUIREMENTS & REGULATIONS SETOUT BY ANY FEDERAL, STATE & REGIONAL GOVERNMENT.

ALL BUILDING WORKS TO COMPLY WITH LOCAL AUTHORITIES EROSION AND SEDIMENT CONTROL STANDARDS. ALL SEDIMENT FENCING TO BE ERECTED ON SITE PRIOR TO COMMENCEMENT OF WORK.

ALL PLUMBING & DRAINAGE TO COMPLY WITH STANDARD SEWERAGE BY-LAWS & REQUIREMENTS OF LOCAL AUTHORITY.

BUILDER TO CONFIRM EXACT SITING AND ORIENTATION PRIOR TO CONSTRUCTION SETOUT. ALL BUILDING SETOUT AND CONFIRMATION OF SETBACKS AND HEIGHT TO BE CARRIED OUT BY A LICENSED SURVEYOR. NO FOOTING, OR WALL TO ENCROACH THE TITLE BOUNDARY.

ALL WET AREAS TO BE CONSTRUCTED IN ACCORDANCE WITH NCC 2019 BCA - VOL 2, PART 3.8.1 WET AREAS AND EXTERNAL WATERPROOFING.

WATER CLOSETS WITH DOOR CIRCULATION SPACES LESS THAN 1.2m FROM THE HINGE OF THE DOOR MUST BE PROVIDED WITH LIFT-OFF HINGES THAT ALLOW THE DOOR TO BE REMOVED WHEN IN THE CLOSED POSITION IN ACCORDANCE WITH NCC 2019 BCA - VOL 2, PART 3.8.3.3 CONSTRUCTION OF SANITARY COMPARTMENTS. WATER CLOSETS TO HAVE A MINIMUM CLEAR WIDTH OF 900mm.

PROVIDE APPROVED SMOKE ALARMS INSTALLED IN ACCORDANCE WITH NCC 2019, BCA - VOL 2, PART 3.7.5 SMOKE ALARMS AND EVACUATION LIGHTING, BE INTERCONNECTED & TO COMPLY AUSTRALIAN STANDARD AS 3786.

ALL GLAZING TO COMPLY WITH NCC 2019 BCA - VOL 2, PART 3.6 GLAZING & MUST BE DESIGNED FOR THE WIND LOADS SPECIFIC TO THE BUILDING.

ALL STAIRS & STEPS ARE DESIGNED & ARE TO BE CONSTRUCTED IN ACCORDANCE WITH NCC 2019 BCA - VOL 2, PART 3.9.1 STAIRWAY AND RAMP CONSTRUCTION.

ALL BALUSTRADES & HANDRAILS REQUIRED SHALL BE 1000 MINIMUM ABOVE FINISHED FLOOR LEVEL (ie TOP OF TILES, CARPET ETC) & HAVE NO OPENINGS GREATER THAN 125mm, IN ACCORDANCE WITH NCC 2019 BCA - VOL 2, PART 3.9.2 BARRIERS AND HANDRAILS.

REFER TO STRUCTURAL ENGINEERS DRAWINGS & SPECIFICATIONS FOR SOILS REPORTS, FOOTING & SLAB DOCUMENTATION & OTHER REQUIRED STRUCTURAL DOCUMENTATION.

ALL WORKS ARE TO BE CARRIED OUT IN ACCORDANCE WITH THE CURRENT BUILDING CODE OF AUSTRALIA (NATIONAL CONSTRUCTION CODE), LOCAL COUNCIL REQUIREMENTS, QUEENSLAND DEVELOPMENT CODE GUIDLINES AND ALL OTHER RELEVANT BY LAWS AND AUTHORITIES INCLUDING AUSTRALIAN STANDARDS, IN PARTICULAR:
-AS 3798 SITE PREPARATION
-AS 2870 CONCRETE CONSTRUCTION
-AS 1684.3 RESIDENTIAL TIMBER FRAMED CONSTRUCTION - CYCLONIC
-AS 4100, AS1111 AND AS 1112 STEELWORK
-AS3660.1 TERMITE PROTECTION
ALL DRAWINGS ARE TO BE READ IN CONJUNCTION WITH ENGINEERING DETAILS, DRAWINGS AND COMPUTATIONS.

SITE NOTE

BUILDER TO CONFIRM LOCATIONS OF ALL EXISTING SERVICES BELOW & ABOVE GROUND LEVEL ON & ADJACENT TO THE SITE, PRIOR TO ANY BUILDING WORKS.

THE FINISHED SURFACE IMMEDIATELY SURROUNDING THE BUILDING FOR A MINIMUM WIDTH OF 1000mm, SHALL BE PROVIDED WITH A MINIMUM SLOPE OF 1 in 20 AWAY FROM THE BUILDING TO AN APPROVED DRAINAGE SYSTEM AS PER NCC 2019 BCA - VOL 2, PART 3.1.3.3 SURFACE WATER DRAINAGE.

SURFACE DRAINAGE IS TO DISCHARGE EVENLY WITHIN THE SITE & WITHOUT NUISANCE TO ADJOINING PROPERTIES.

ALL SUBFLOOR AREAS MUST BE GRADED TO AVOID THE PONDING OF WATER BENEATH THE BUILDING.

CUT & FILL BATTERS ARE NOT TO EXCEED A MAXIMUM SLOPE AS PER NCC 2019 BCA - VOL 2, PART 3.1.1 EARTHWORKS TABLE 3.1.1.1 FOR THE SITE SPECIFIC SOIL TYPE. REFER TO NCC 2019 BCA - VOL 2, PART 3.2.2.4 FOR SLAB EDGE SUPPORT ON SLOPING SITES.

TIMBER RETAINING WALLS TO HAVE 1000mm MAXIMUM HEIGHT. PROVIDE 65mm DIA. AGG. DRAINS WITH GRANULAR BACKFILL. RETAINING WALLS & DRAINAGE SYSTEMS TO BE WHOLLY CONTAINED ON THE SUBJECT SITE. RETAINING WALLS GREATER THAN 1000mm IN HEIGHT SHALL BE DESIGNED BY THE STRUCTURAL ENGINEER.

BOUNDARY FENCES, INCLUDING HEIGHT OF ANY RETAINING WALLS UNDER, MUST NOT EXCEED 2000mm IN HEIGHT ABOVE EXISTING GROUND LEVEL. REFER TO LOCAL AUTHORITY REGULATIONS PRIOR TO COMMENCING ANY WORKS & SEEK ANY REQUIRED APPROVALS.

TERMITE PROTECTION

ALL NEW BUILDING WORK AND/OR ALTERATIONS OF EXISTING BUILDING WORK IS TO BE TERMITE PROTECTED VIA PHYSICAL & CHEMICAL BARRIERS AS PER NCC 2019 BCA - VOL 2, PART 3.1.4.3 TERMITE MANAGEMENT SYSTEMS, TABLE 3.1.4.1 ACCEPTABLE TERMITE MANAGEMENT SYSTEMS AND COMPONENTS, AS 3660.1 TERMITE MANAGEMENT NEW BUILDING WORK & AS 3660.2 TERMITE MANAGEMENT IN AND AROUND EXISTING BUILDINGS AND STRUCTURES. A 75mm INSPECTION ZONE ON ALL NEW SLABS AS REQUIRED BY AS 3660.1.

A DURABLE NOTICE IS REQUIRED AND MUST BE INSTALLED IN A PROMINENT LOCATION SUCH AS THE METER BOX & IS TO BE PERMANENTLY FIXED. THE INFORMATION TO BE DISPLAYED ON THE NOTICE IS AS PER NCC 2019 BCA - VOL 2, PART 3.1.4.4 DURABLE NOTICE.

THEREAFTER THE OWNER TAKES ON THE RESPONSIBILITY TO ORGANISE REGULAR INSPECTIONS WHICH MUST BE CARRIED OUT BY A QBCC-LICENSED CONTRACTOR WITH THE APPROPRIATE TERMITE MANAGEMENT LICENCE TO ENSURE TERMITES HAVE NOT BRIDGED THE BARRIER. IT IS RECOMMENDED THAT INSPECTIONS BE AT LEAST EVERY 12 MONTHS, OR MORE OFTEN IN HIGH RISK AREAS. IT SHALL ALSO BE ADVISED THAT CAUTION BE TAKEN TO ENSURE THAT ALL PHYSICAL TERMITE BARRIERS BE CLEAR OF GARDEN BED &/OR SOIL BUILD UP & THAT ANY CHEMICAL BARRIERS INSTALLED REMAIN

BRICK / BLOCKWORK ARTICULATION JOINTS

BRICKWORK ARTICULATION JOINTS ARE TO BE INSTALLED AT LOCATIONS OUTLINED IN NCC 2019 BCA - VOL 2, PARK 3.3.5.13 VERTICAL ARTICULATION JOINTS. BOTH BRICK & BLOCKWORK ARTICULATION JOINTS ARE TO BE IN AS PER AS 4773.2 MASONRY IN SMALL BUILDINGS CONSTRUCTION OR AS PER ENGINEER.

ROOFWATER DRAINAG

ALL ROOFWATER DRAINAGE SYSTEMS MUST BE CONNECTED TO A STORMWATER DRAINAGE SYSTEM COMPLYING WITH NCC 2019 BCA - VOL 2, PART 3.1.3 DRAINAGE & AUSTRALIAN STANDARD AS/NZ 3500.

THE ROOF DRAINAGE SYSTEM MUST BE PROVIDED WITH AN OVERFLOW TO PREVENT THE BACKFLOW OF WATER INTO THE BUILDING.

THE AREA SPECIFIC RAINFALL INTENSITY MUST BE SELECTED FROM NCC 2019 BCA - VOL 2, PART 3.5.3.1, FROM AUSTRALIAN STANDARD AS/NZ3500.3 OR FROM THE BUREAU OF METEOROLOGY 2016 RAINFALL DATA.

GUTTERS & DOWNPIPES MUST BE SELECTED FROM NCC 2019 BCA - VOL 2, PART 3.5.3.5 TABLE 3.5.3.2 OR FROM AUSTRALIAN STANDARD AS/NZ3500.3.

EAVES GUTTERS MUST BE INSTALLED AT A FALL NOT LESS THAN 1 in 500 WITH SUPPORT BRACKETS AT 1200mm MAXIMUM CENTRES.

BOX GUTTERS MUST BE INSTALLED AT A FALL NOT LESS THAN 1 in 100, IN ACCORDANCE WITH AUSTRALIAN STANDARD AS/NZ3500.3.

THE WIDTH OF VALLEY GUTTERS SHALL BE IN ACCORDANCE WITH AUSTRALIAN STANDARD AS/NZ3500.3 & BUILDING CODE OF AUSTRALIA PART 3.5.2. REFER TO ROOF SHEETING MANUFACTURERS SPECIFICATIONS FOR LIMITATIONS ON SHEET OVERHANGS INTO VALLEY GUTTERS. THE MAXIMUM ROOF CATCHMENT AREA FOR VALLEY GUTTERS IS 20sq.m. VALLEY GUTTERS ON ROOF PITCHED LOWER THAN 12.5 DEGREES MUST BE DESIGNED AS BOX GUTTERS.

DOWNPIPES MUST SERVE NOT MORE THAN 12 METRES OF GUTTER LENGTH FOR EACH DOWNPIPE WHICH MUST BE LOCATED AS CLOSE AS POSSIBLE TO VALLEY GUTTERS.

EAVES GUTTERS MUST BE PROVIDED WITH AN OVERFLOW SYSTEM WHERE DOWNPIPES ARE LOCATED MORE THAN 1200mm FROM A VALLEY GUTTER.

BUSHFIRE NOTE:

EXTERNAL WALLS
EXPOSED COMPONENTS FOR AND EXTERNAL WALL THAT ARE LESS THEN 400MM FROM THE GROUND OR LESS THEN 400MM ABOVE DECKS CARPORT ROOFS AWNINGS OR SIMILAR MUST HAVE A ANGLE LESS THEN 18° TO THE HORIZONTAL AND EXTENDING MORE THEN 110 IN WIDTH FROM THE WALL. WALL ARE TO BE CONSTRUCTED OF A NON COMBUSTIBLE MATERIAL .

VENTS AND WEEPHOLES
VENTS AND WEEPHOLES TO EXTERNAL WALLS TO BE SCREENED WITH MESH WITH A MAXIMUM APERTURE OF 2MM MADE OF CORROSION RESISTANT STEEL EXCEPT WITH THE WEEPHOLES ARE LESS THEN 3MM .

SCREENS FOR WINDOWS
WHERE SCREENS ARE FITTED TO WINDOWS OR DOORS SHALL HAVE MESH OR PERFORATED SHEET WITH A MAXIMUM APERTURE OF 2MM MADE OF CORROSION-RESISTANT STEEL BRONZE OR ALUMINUM. GAPS BETWEEN PERIMETER OF THE SCREEN ASSEMBLY AND BUILDING ELEMENT TO WHICH IT IS FITTED SHALL NOT EXCEED 3MM. THE FRAME SUPPORTING THE MESH SHALL BE MADE FROM METAL OR FIRE RESISTANT MATERIAL.

MANUFACTURERS SPECIFICATIONS (MS)

ALL BUILDING PRODUCTS & MATERIALS THAT ARE USED ON SITE MUST BE STORED CORRECTLY AS PER MS. REFER TO MS FOR ALL DETAILS REGARDING INSTALLATION . REFER TO MS FOR MATERIAL AND PRODUCTS RECOMMENDED TO USE FOR ALL SITES THAT ARE LOCATED WITHIN PROXIMITY TO SALT ENVIRONMENTS.

DRIVEWAY & PATH NOTE

ALL SITE PAVING TO BE CONSTRUCTED IN ACCORDANCE WITH THE PUBLICATIONS CEMENT, CONCRETE & AGGREGATE AUSTRALIA - GUIDE TO CONCRETE HOUSING 2007, PATHS & DRIVEWAYS & RESIDENTIAL CONCRETE DRIVEWAYS & PATHS - JULY 2005.

THE AREA BENEATH & ADJACENT TO DRIVEWAYS & PATHS TO BE CLEARED OF ALL TOPSOIL & ORGANIC MATTER.

PROVIDE A COMPACTED & LEVELLED LAYER OF 20mm MINIMUM SAND: & AN OPTIONAL 0.2UM POLYETHYLENE MOISTURE BARRIER MAY BE PROVIDED UNDER THE SLAB IN SALINE AREAS, LAPPED & TAPED 200mm AT JOINTS.

ALL PATHS & DRIVEWAYS SHALL HAVE A MINIMUM FALL OF 1 in 100 (1%).

THE MAXIMUM GRADE OF PAVEMENTS SHALL NOT EXCEED 1 in 5 (20%). WHERE GRADES ARE NEAR THE MAXIMUM, A TRANSITION ZONE AT EITHER END MAY BE REQUIRED. REFER TO BUILDING CODE OF AUSTRALIA - VOLUME 1 PART D2.10 FOR GRADES TO REQUIRED EXIT RAMPS.

ALL DRIVEWAYS, PATHS & CROSSTOVS BETWEEN THE PROPERTY BOUNDARY & THE KERBLINE ARE DESIGNED TO BE CONSTRUCTED AS PER THE ALOCAL

ARCADIA

Made for Memories

HOMES

(07) 5325 1857

| admin@arcadiahomesqld.com.au

| QBCC 15085900

CLIENT: PETER & SUZIE CROGAN				SITE ADDRESS: LOT 16 POWERS STREET, EUMUNDI QLD							
				ORIENTATION	AREA CALCULATIONS		REAL PROPERTY DESCRIPTION		FOR APPROVAL		
REVISION	DATE	AMENDMENTS	TECH	N WIND CLASS: N4, SOIL TYPE: M	RESIDENCE	193.24 m²	LOT: 16 PLAN: SP325615				
A	9/02/26	FOR APPROVAL	NB		ALFRESCO	28.10 m²	LOCAL AUTHORITY: SUNSHINE COAST COUNCIL				
B	25/02/26	BAL 12.5 & BUSHFIRE NOTES ADDED	NB		PORCH	3.02 m²					
C	13/05/26	FRONT RETAINING REV	DD		TOTAL:	224.36 m²	PROJECT NO: J1377	DRAWN BY: NB			
D	20/07/26	CONSTRUCTION REVISIONS	DD				HOUSE DESIGN:	FACADE:	DATE: 28/07/26	SHEET NO.	REV.
E	28/07/26	CONSTRUCTION REVISIONS	DD			ARLO 185 - MOD	GRANDE	SCALE : As indicated @A3	1	E	

1. **NOTES:**
1. DIMENSIONS ARE TO BE VERIFIED PRIOR TO COMMENCEMENT OF WORK.

2. GIVEN DIMENSIONS ARE TO HAVE PRIORITY TO SCALED DIMENSIONS.

3. ALL GROUND LEVELS ARE APPROXIMATE ONLY.

4. ALL PLUMBING AND DRAINING IS TO COMPLY WITH STANDARD SEWERAGE BY-LAWS AND REQUIREMENTS OF THE LOCAL AUTHORITY.

5. ALL STAIRS ARE TO HAVE 190MM MAX RISERS AND 240MM MIN. GOINGS.

6. ALL WORKS ARE TO BE CONSTRUCTED IN ACCORDANCE WITH THE CURRENT AUSTRALIAN STANDARDS AND ALL RELEVANT CURRENT TRADE AND TECHNICAL MANUALS.

7. DISCLAIMER: DRIVEWAY, PATHS, CLOTHES LINES, STORMWATER LINES, LANDSCAPING, LETTER BOX, HOT WATER SYSTEM AND GROUND PITS ARE DIAGRAMMATIC ONLY.

8. ALL DOWNPIPES TO BE INSTALLED IN ACCORDANCE WITH THE CURRENT NCC VOLUME 2 ABCB HOUSING PROVISIONS PART 7.4.5. EACH DOWNPIPE MUST NOT SERVE MORE THAN 12M OF GUTTER LENGTH.


9. SITE EXCAVATION SHALL BE SUCH THAT 1000MM WIDE BY 1:20 GRADE EXISTS AROUND PERIMETER OF BUILDING AS PER THE CURRENT NCC - ABCB HOUSING PROVISIONS PART 3.3.3 SURFACE WATER DRAINAGE.

10. OWNER TO PROVIDE/INSTALL SITE DRAINAGE AFTER HANDOVER AS REQUIRED.

11. LAND TO BE LEVELLED TO SITE HOUSE. SLAB TO BE 200MM MINIMUM ABOVE FINISHED GROUND LEVEL.

12. STORMWATER SYSTEM TO LOCAL COUNCIL REQUIREMENTS.

BUSHFIRE OVERLAY:
BAL 12.5
REFER CONSTRUCTION NOTES PAGE 1

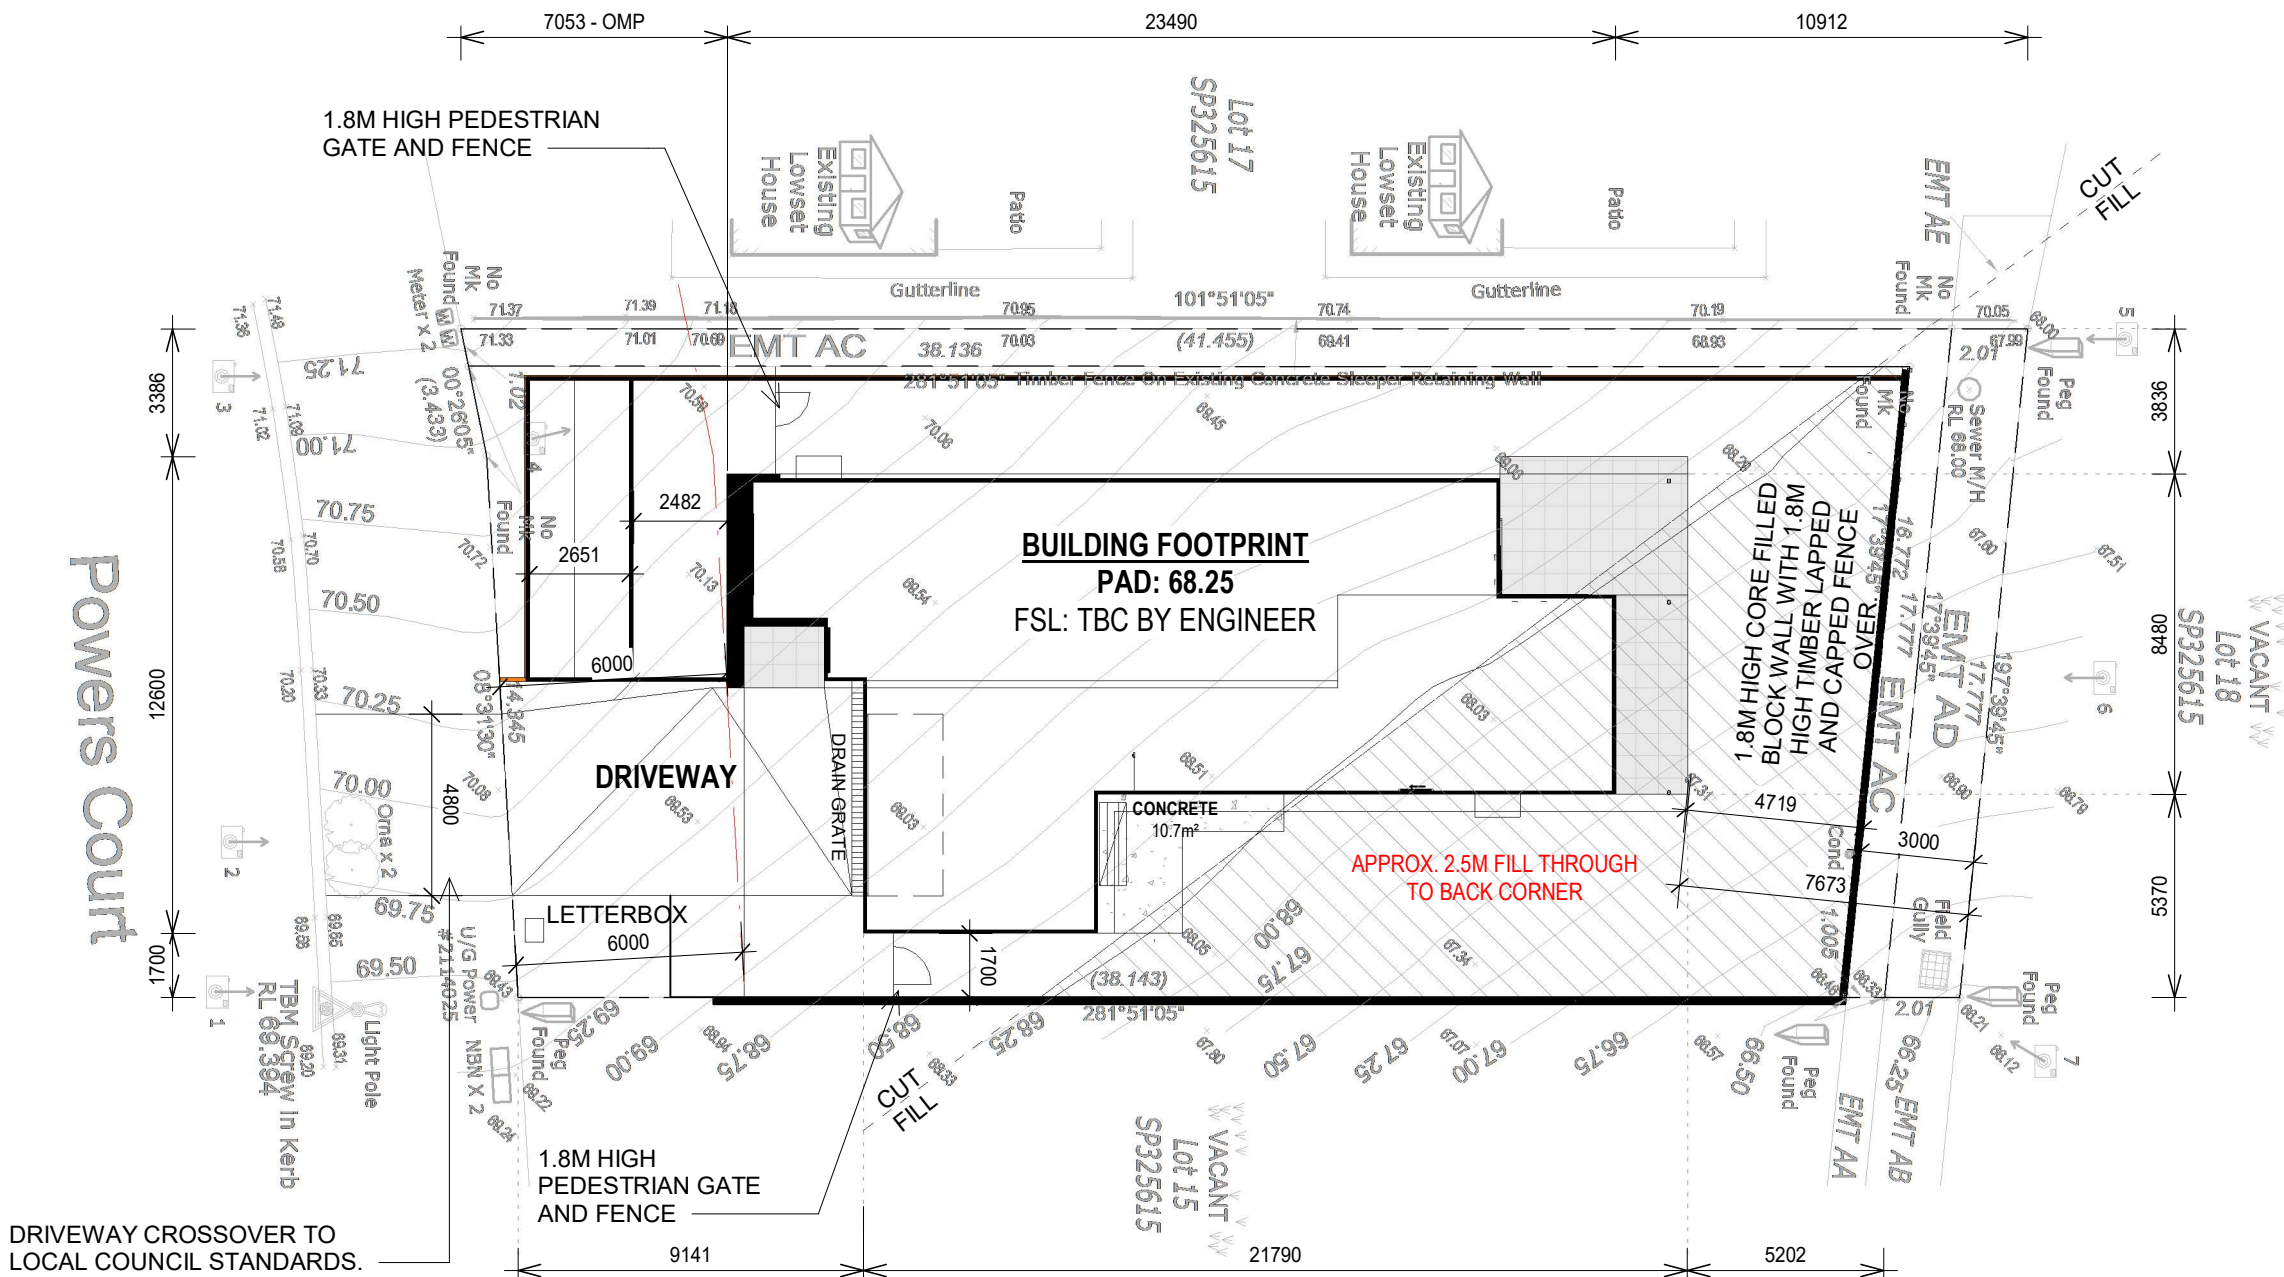


SPECIAL CONDITIONS - CLASS 1-10 (NCC 22)
25. BUSHFIRE CONSTRUCTION
IF THE PROPOSED BUILDING WORK HAS BEEN IDENTIFIED AS BEING LOCATED WITHIN A PRESCRIBED BUSHFIRE PRONE AREA AND A BAL HAS BEEN ESTABLISHED (REFER TO APPROVED DOCUMENTS), ALL BUILDING WORK MUST COMPLY WITH THE CONDITIONS OF THE DEVELOPMENT APPROVAL FOR BUILDING WORK, AUSTRALIAN STANDARD (AS3959), AND/OR ANY OTHER APPLICABLE LOCAL GOVERNMENT PLANNING SCHEME REQUIREMENT/S.

ARCADIA

Made for Memories

HOMES

(07) 5325 1857 | admin@arcadiahomesqld.com.au | QBCC 15085900

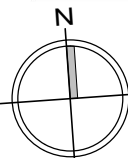CLIENT: PETER & SUZIE CROGAN				SITE ADDRESS: LOT 16 POWERS STREET, EUMUNDI QLD								
				ORIENTATION		AREA CALCULATIONS		REAL PROPERTY DESCRIPTION		FOR APPROVAL		
REVISION	DATE	AMENDMENTS	TECH.			RESIDENCE	193.24 m²	LOT: 16 PLAN: SP325615				
A	9/02/26	FOR APPROVAL	NB			ALFRESCO	28.10 m²	LOCAL AUTHORITY: SUNSHINE COAST COUNCIL				
B	25/02/26	BAL 12.5 & BUSHFIRE NOTES ADDED	NB							PORCH	3.02 m²	
C	13/05/26	FRONT RETAINING REV	DD					TOTAL:	224.36 m²	PROJECT NO: J1377	DRAWN BY: NB	
D	20/07/26	CONSTRUCTION REVISIONS	DD							HOUSE DESIGN:	FACADE:	
E	28/07/26	CONSTRUCTION REVISIONS	DD					ARLO 185 - MOD	GRANDE	DATE: 28/07/26	SHEET NO.	REV.
										SITE PLAN		
				WIND CLASS		SOIL TYPE				2		
				N4		M						
										SCALE 1 : 200 @A3		
										E		

NOTES

-SPECIFICATION OVERRIDES PLAN DETAILS

-DOWNPIPES AS PER BUILDER'S SPECIFICATION

-PROVIDE NOGGINGS FOR TOWEL RAILS @ 1200MM AND TOILET ROLL HOLDERS (TR-H) @ 800MM.

-PROVIDE REINFORCED WALL TO SHOWER SURROUND OF THE MAIN BATH TO COMPLY WITH NCC 2022, PART H8 VOLUME 2.

-VANITY UNIT SIZES AS INDICATED

-SHOWER SIZES AS INDICATED ON SLAB PLAN.

-LIFT OFF HINGES TO W/C & BATHROOM

LEGEND

DH	DOUBLE HUNG WINDOW
AW	AWNING WINDOW
FG	FIXED GLASS
DP	DOWNPIPE
FW	FLOOR WASTE
HWS	HOT WATER SYSTEM
DW	DISHWASHER
AC	AIR CONDITIONER
SGD	SLIDING GLASS DOOR
OH	OVERHEAD CUPBOARD
OBS	OBSCURE GLASS
S	SMOKE DETECTOR
UBO	UNDER BENCH OVEN
FFL	FINISHED FLOOR LEVEL
MH	MANHOLE TO CEILING
TR	TOWEL RAIL
TH	TOWEL HOOK
TR-H	TOILET ROLL HOLDER
LBW	LOAD BEARING WALL

ENERGY EFFICIENCY

REFER TO NOTES PAGE 7

QDC PART MP 4.1 SUSTAINABLE BUILDINGS


-AAA RATED SHOWER ROSES (AS.6400-2005)

-WATER SERVICE PRESSURE NOT TO EXCEED LEVELS AS STATED IN AS 3500-2003

-4.5/3 DUAL FLUSH TOILET SYSTEMS

-GAS HOT WATER SUPPLY WITH 5 STAR RATING

BUSHFIRE OVERLAY:
BAL 12.5

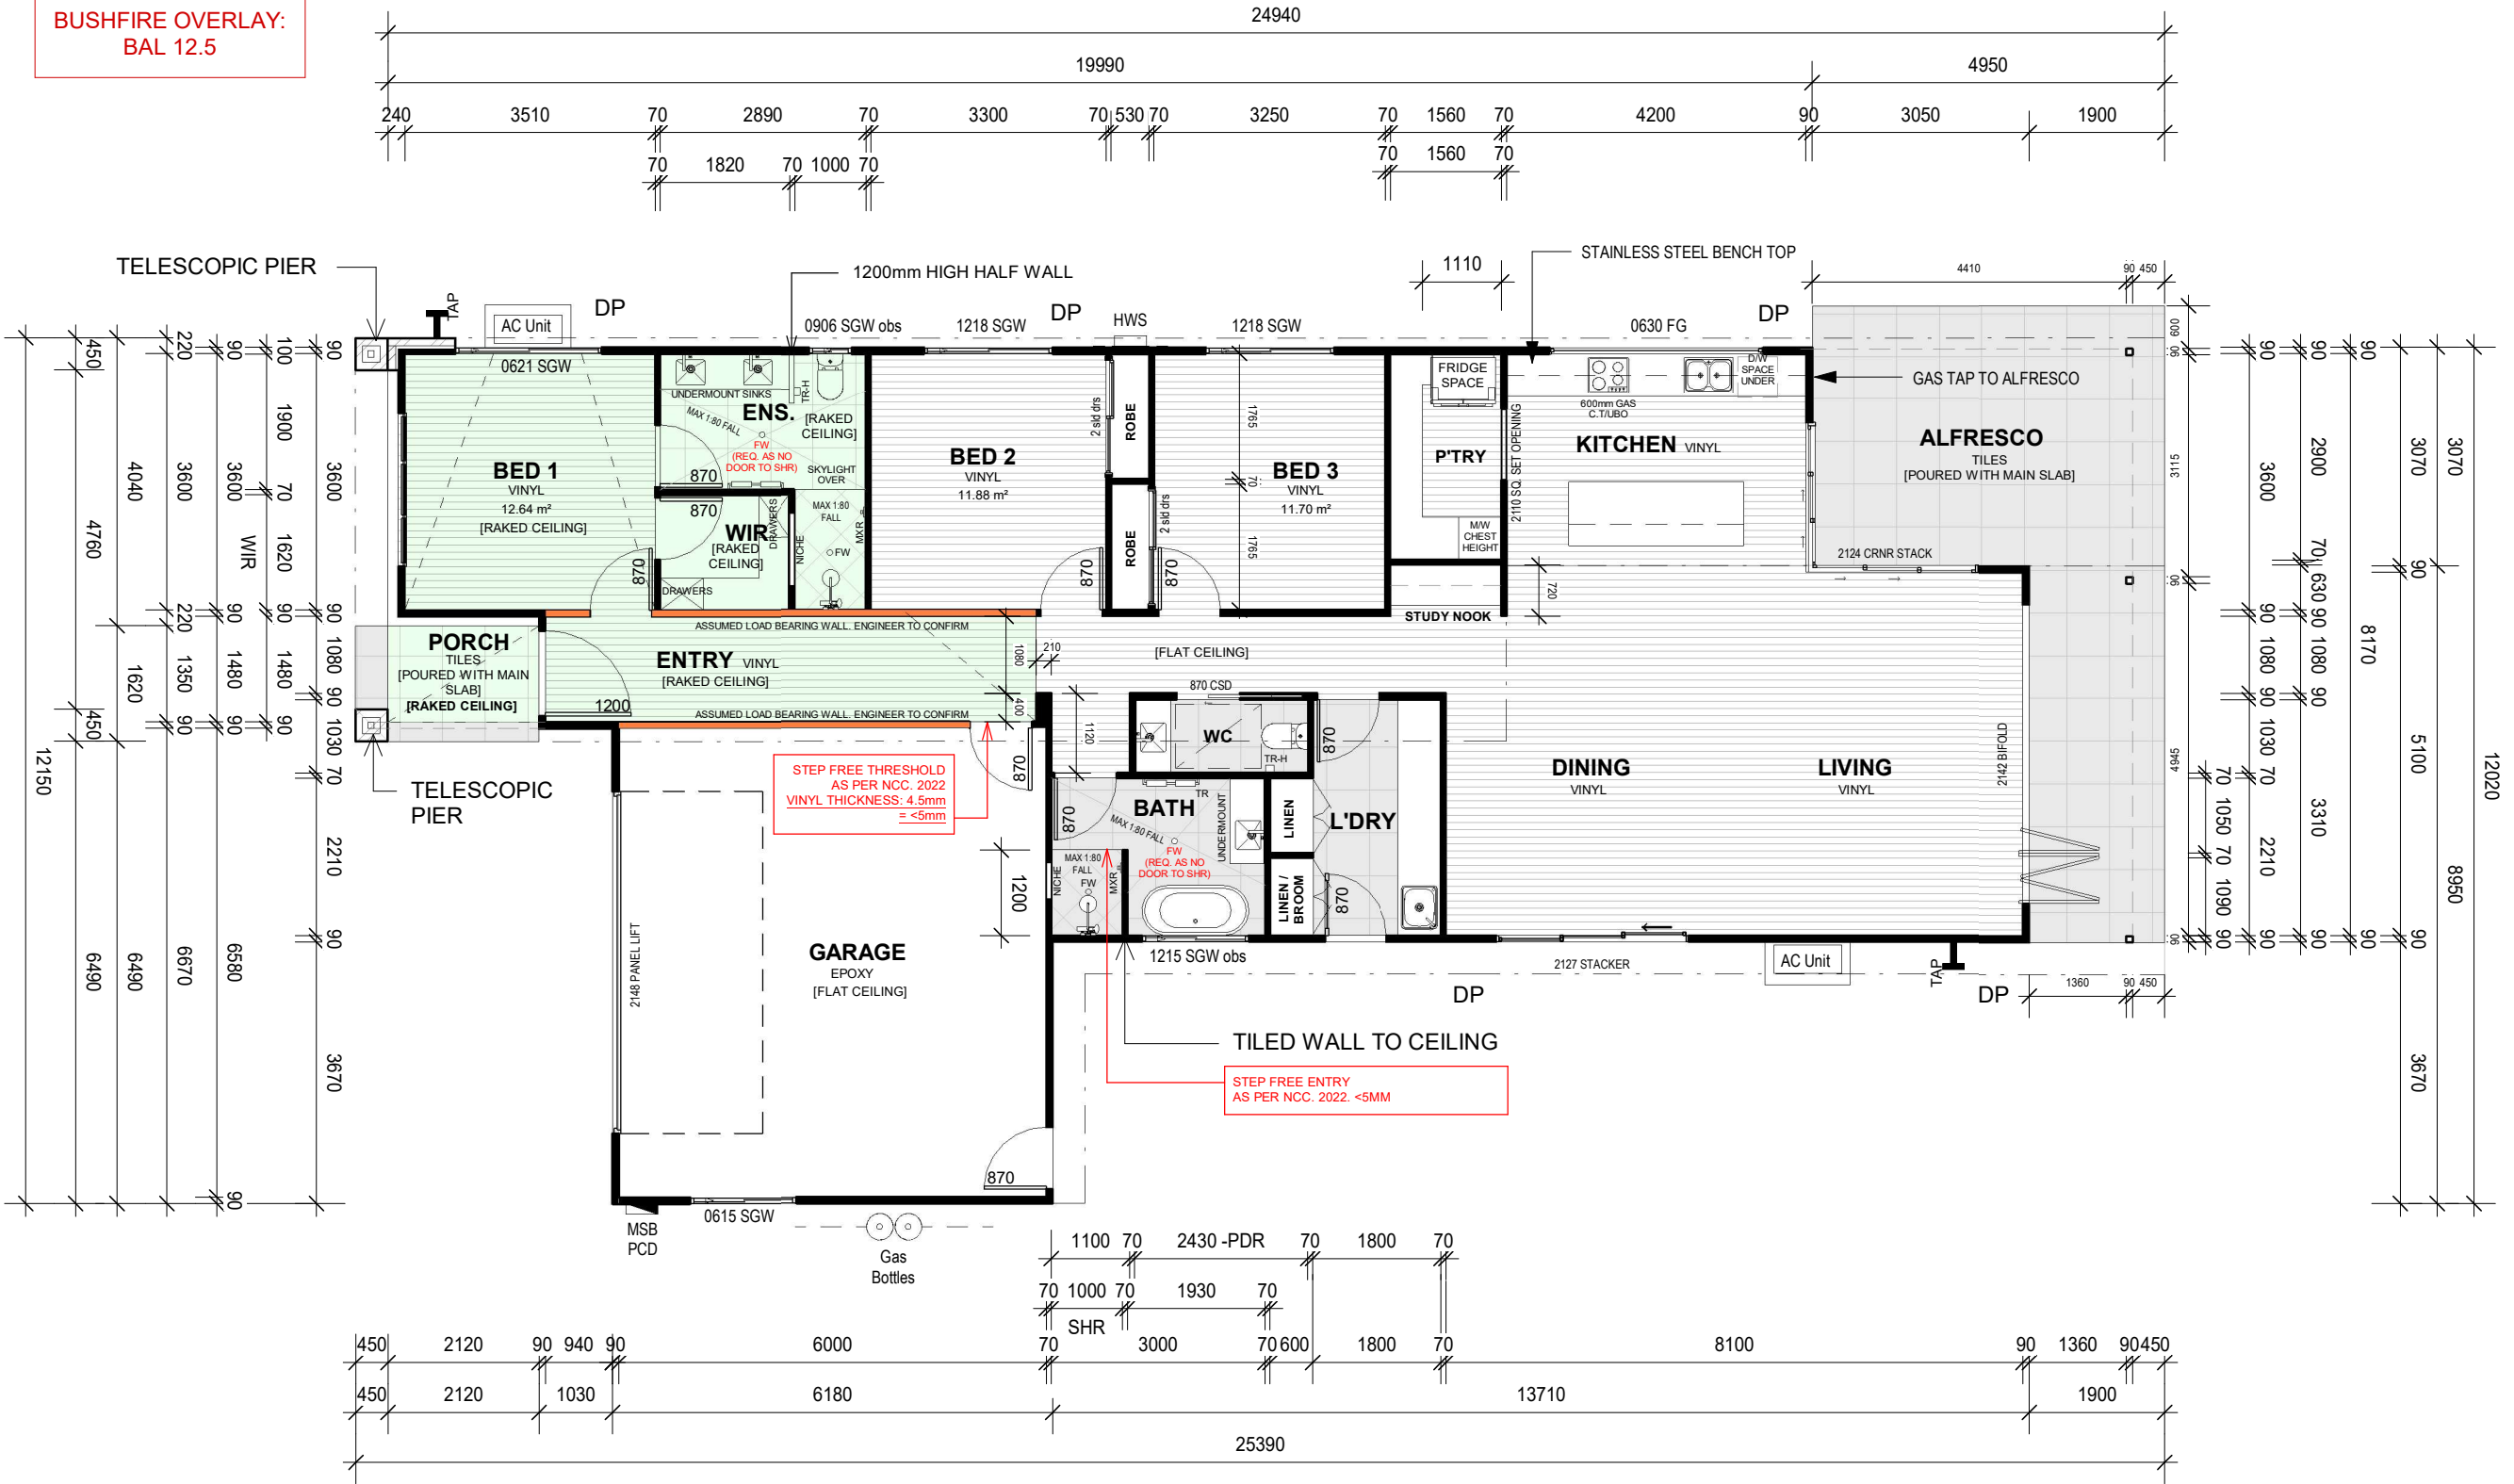

ARCADIA
HOMES
Made for Memories


(07) 5325 1857 | admin@arcadiahomesqld.com.au | QBCC 15085900

CLIENT: PETER & SUZIE CROGAN

SITE ADDRESS: LOT 16 POWERS STREET, EUMUNDI QLD

REVISION	DATE	AMENDMENTS	TECH.
A	9/02/26	FOR APPROVAL	NB
B	25/02/26	BAL 12.5 & BUSHFIRE NOTES ADDED	NB
C	13/05/26	FRONT RETAINING REV	DD
D	20/07/26	CONSTRUCTION REVISIONS	DD
E	28/07/26	CONSTRUCTION REVISIONS	DD

ORIENTATION

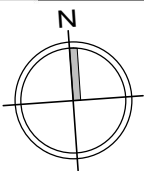

WIND CLASS	SOIL TYPE
N4	M

AREA CALCULATIONS

RESIDENCE	193.24 m²
ALFRESCO	28.10 m²
PORCH	3.02 m²
TOTAL:	224.36 m²

REAL PROPERTY DESCRIPTION

LOT: 16 PLAN: SP325615

LOCAL AUTHORITY:
SUNSHINE COAST COUNCIL

PROJECT NO: J1377

DRAWN BY: NB

HOUSE DESIGN:

FACADE:

ARLO 185 - MOD

GRANDE

FOR APPROVAL

DRAWING TITLE:

FLOOR PLAN

DATE: 28/07/26

SCALE 1 : 100


SHEET NO.

3

REV.

E


BUSHFIRE OVERLAY:
BAL 12.5

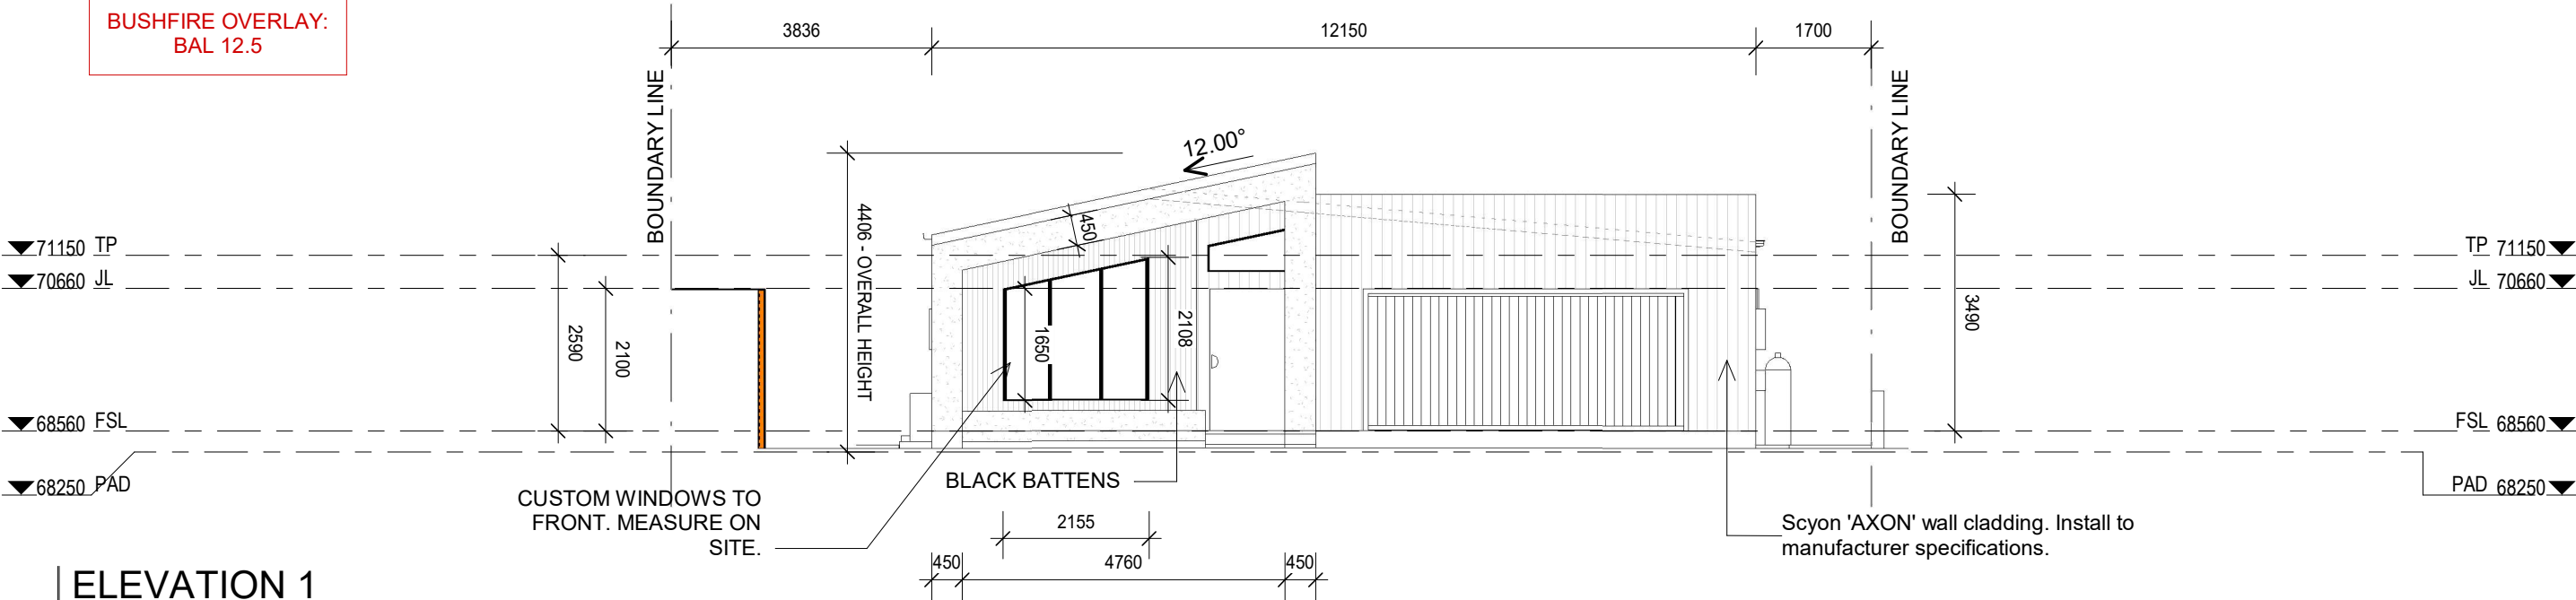

ELEVATION 1

1 : 100

SELECTED COLORBOND ROOF SHEETING @ 12°
PITCH. INSTALL TO MANUFACTURER
SPECIFICAITONS.

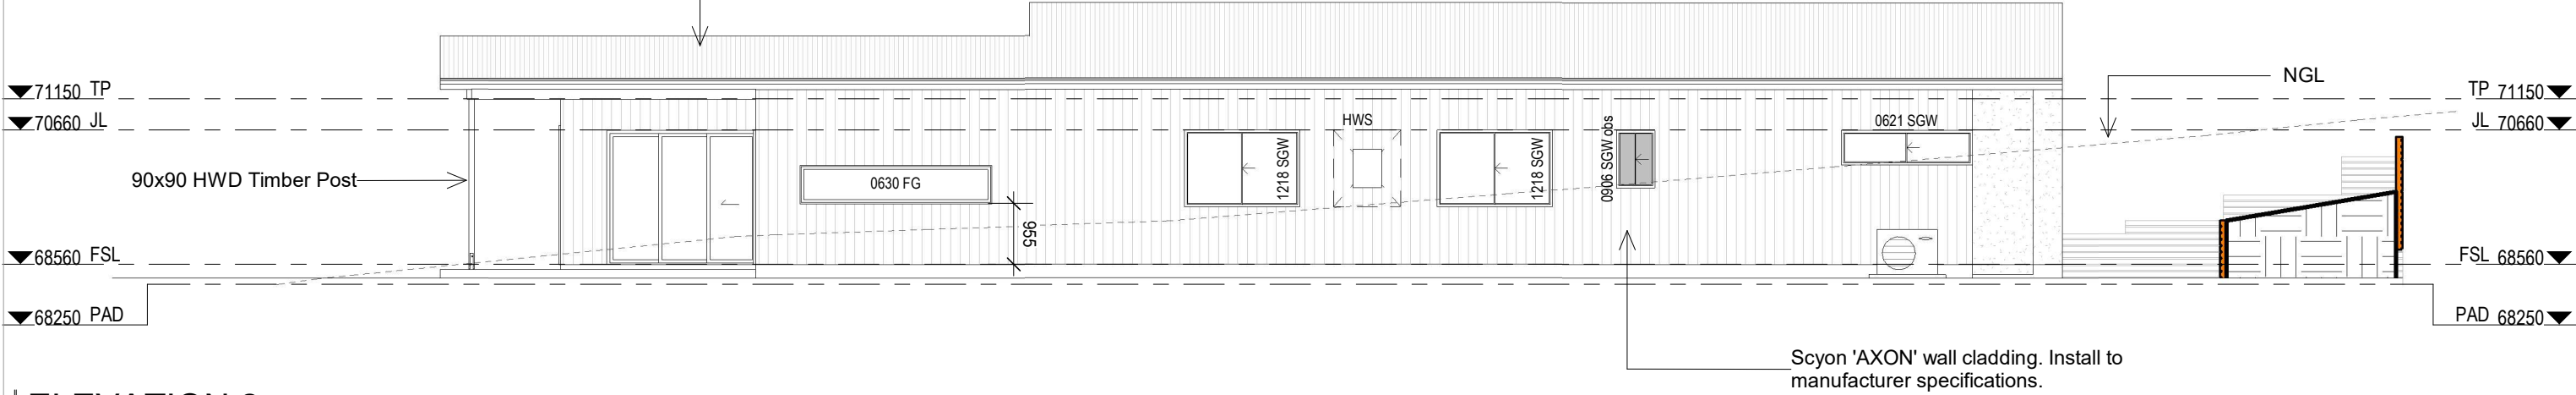

ELEVATION 2

1 : 100

ARCADIA
HOMES

Made for Memories


(07) 5325 1857 | admin@arcadiahomesqld.com.au | QBCC 15085900

CLIENT: PETER & SUZIE CROGAN

SITE ADDRESS: LOT 16 POWERS STREET, EUMUNDI QLD

REVISION	DATE	AMENDMENTS	TECH.
A	9/02/26	FOR APPROVAL	NB
B	25/02/26	BAL 12.5 & BUSHFIRE NOTES ADDED	NB
C	13/05/26	FRONT RETAINING REV	DD
D	20/07/26	CONSTRUCTION REVISIONS	DD
E	28/07/26	CONSTRUCTION REVISIONS	DD

ORIENTATION

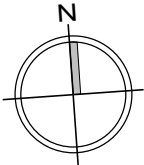

WIND CLASS	SOIL TYPE
N4	M

AREA CALCULATIONS

RESIDENCE	193.24 m ²
ALFRESCO	28.10 m ²
PORCH	3.02 m ²
TOTAL:	224.36 m ²

REAL PROPERTY DESCRIPTION

LOT: 16 PLAN: SP325615

LOCAL AUTHORITY:
SUNSHINE COAST COUNCIL

PROJECT NO: J1377 DRAWN BY: NB

HOUSE DESIGN: FACADE:

ARLO 185 - MOD GRANDE

FOR APPROVAL

DRAWING TITLE:

ELEVATIONS

DATE:	28/07/26	SHEET NO.	REV.
SCALE	1 : 100	4	E

BUSHFIRE OVERLAY:
BAL 12.5

Selected Colorbond roof sheeting @ 5° Pitch. Install to manufacturer specifications.

SELECTED COLORBOND ROOF SHEETING @ 12° PITCH. INSTALL TO MANUFACTURER SPECIFICAITONS.

▼71150 TP

▼70660 JL

Scyon 'AXON' wall cladding. Install to manufacturer specifications.

▼68560 FSL

▼68250 PAD

TP 71150▼

JL 70660▼

FSL 68560▼

PAD 68250▼

ELEVATION 3

1 : 100

▼71150 TP

▼70660 JL

▼68560 FSL

▼68250 PAD

TP 71150▼

JL 70660▼

FSL 68560▼

PAD 68250▼

ELEVATION 4

1 : 100

Selected Colorbond roof sheeting @ 5° Pitch. Install to manufacturer specifications.

Scyon 'AXON' wall cladding. Install to manufacturer specifications.

ARCADIA
HOMES
Made for Memories


(07) 5325 1857 | admin@arcadiahomesqld.com.au | QBCC 15085900

CLIENT: PETER & SUZIE CROGAN

SITE ADDRESS: LOT 16 POWERS STREET, EUMUNDI QLD

REVISION	DATE	AMENDMENTS	TECH.
A	9/02/26	FOR APPROVAL	NB
B	25/02/26	BAL 12.5 & BUSHFIRE NOTES ADDED	NB
C	13/05/26	FRONT RETAINING REV	DD
D	20/07/26	CONSTRUCTION REVISIONS	DD
E	28/07/26	CONSTRUCTION REVISIONS	DD

ORIENTATION

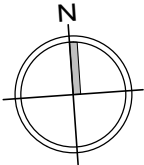

WIND CLASS	SOIL TYPE
N4	M

AREA CALCULATIONS

RESIDENCE	193.24 m²
ALFRESCO	28.10 m²
PORCH	3.02 m²
TOTAL:	224.36 m²

REAL PROPERTY DESCRIPTION

LOT: 16 PLAN: SP325615

LOCAL AUTHORITY:
SUNSHINE COAST COUNCIL

PROJECT NO: J1377 DRAWN BY: NB

HOUSE DESIGN: FACADE:

ARLO 185 - MOD GRANDE

FOR APPROVAL


DRAWING TITLE:

ELEVATIONS

DATE: 28/07/26 SHEET NO. REV.

SCALE 1 : 100 @A3 5 E

NOTES:
DOWNPIPES ARE TO SERVICE 12m MAXIMUM GUTTER LENGTH & BE LOCATED AS CLOSE AS POSSIBLE TO VALLEY GUTTERS AND BE SELECTED IN ACCORDANCE WITH THE APPROPRIATE EAVES GUTTER SELECTION AS SHOWN IN (NCC VOL 2. TABLE 7.4.3a) GUTTERS, DOWNPIPES & FLASHINGS FABRICATED WITH METAL ARE TO MEET AS/NZ2179 REQUIREMENTS WHILE UPVC COMPONENTS ARE TO COMPLY WITH AS1273 ALL SARKING MATERIAL TO BE INSTALLED ACCORDING TO MANUFACTURER'S INSTALLATION INSTRUCTIONS & AS/NZS4200 INSTALLATION OF PLIABLE MEMBRANE AND UNDERLAY (NCC VOL 2. ABCB HOUSING PROVISIONS PART 7) & HAVE A MAXIMUM 5 FLAMMABILITY INDEX (NCC 2022 Part H3D2) ANY FLEXIBLE DUCTING THAT HAS A SOURCE FROM A FLAME HAZARD MUST MEET AS4254 HAZARD PROPERTIES DOWNPIPES ARE TO BE PROTECTED FROM POTENTIAL MECHANICAL DAMAGE, BE INSTALLED NO LESS THAN 100mm FROM ELECTRICAL CABLES & GAS PIPES & NO LESS THAN 50mm FROM OTHER SERVICES (AS/NZS3500.3.2 S4.11) CONNECT STORMWATER DRAINAGE TO LEGAL POINT OF DISCHARGE TO THE SATISFACTION OF THE RESPONSIBLE LOCAL AUTHORITY CALCULATED ROOF CATCHMENTS & ROOFING TO BE INSTALLED AS PER AS/NZS3500.3 OVERFLOW MEASURERS IN ACCORDANCE WITH (NCC 2022 VOL. 2 ABCB HOUSING PROVISIONS PART 7.4.6) ROOF PLAN PROVIDED IS A GUIDE ONLY. TO BE READ IN CONJUNCTION WITH ENGINEER'S STORMWATER DRAINAGE PLAN.

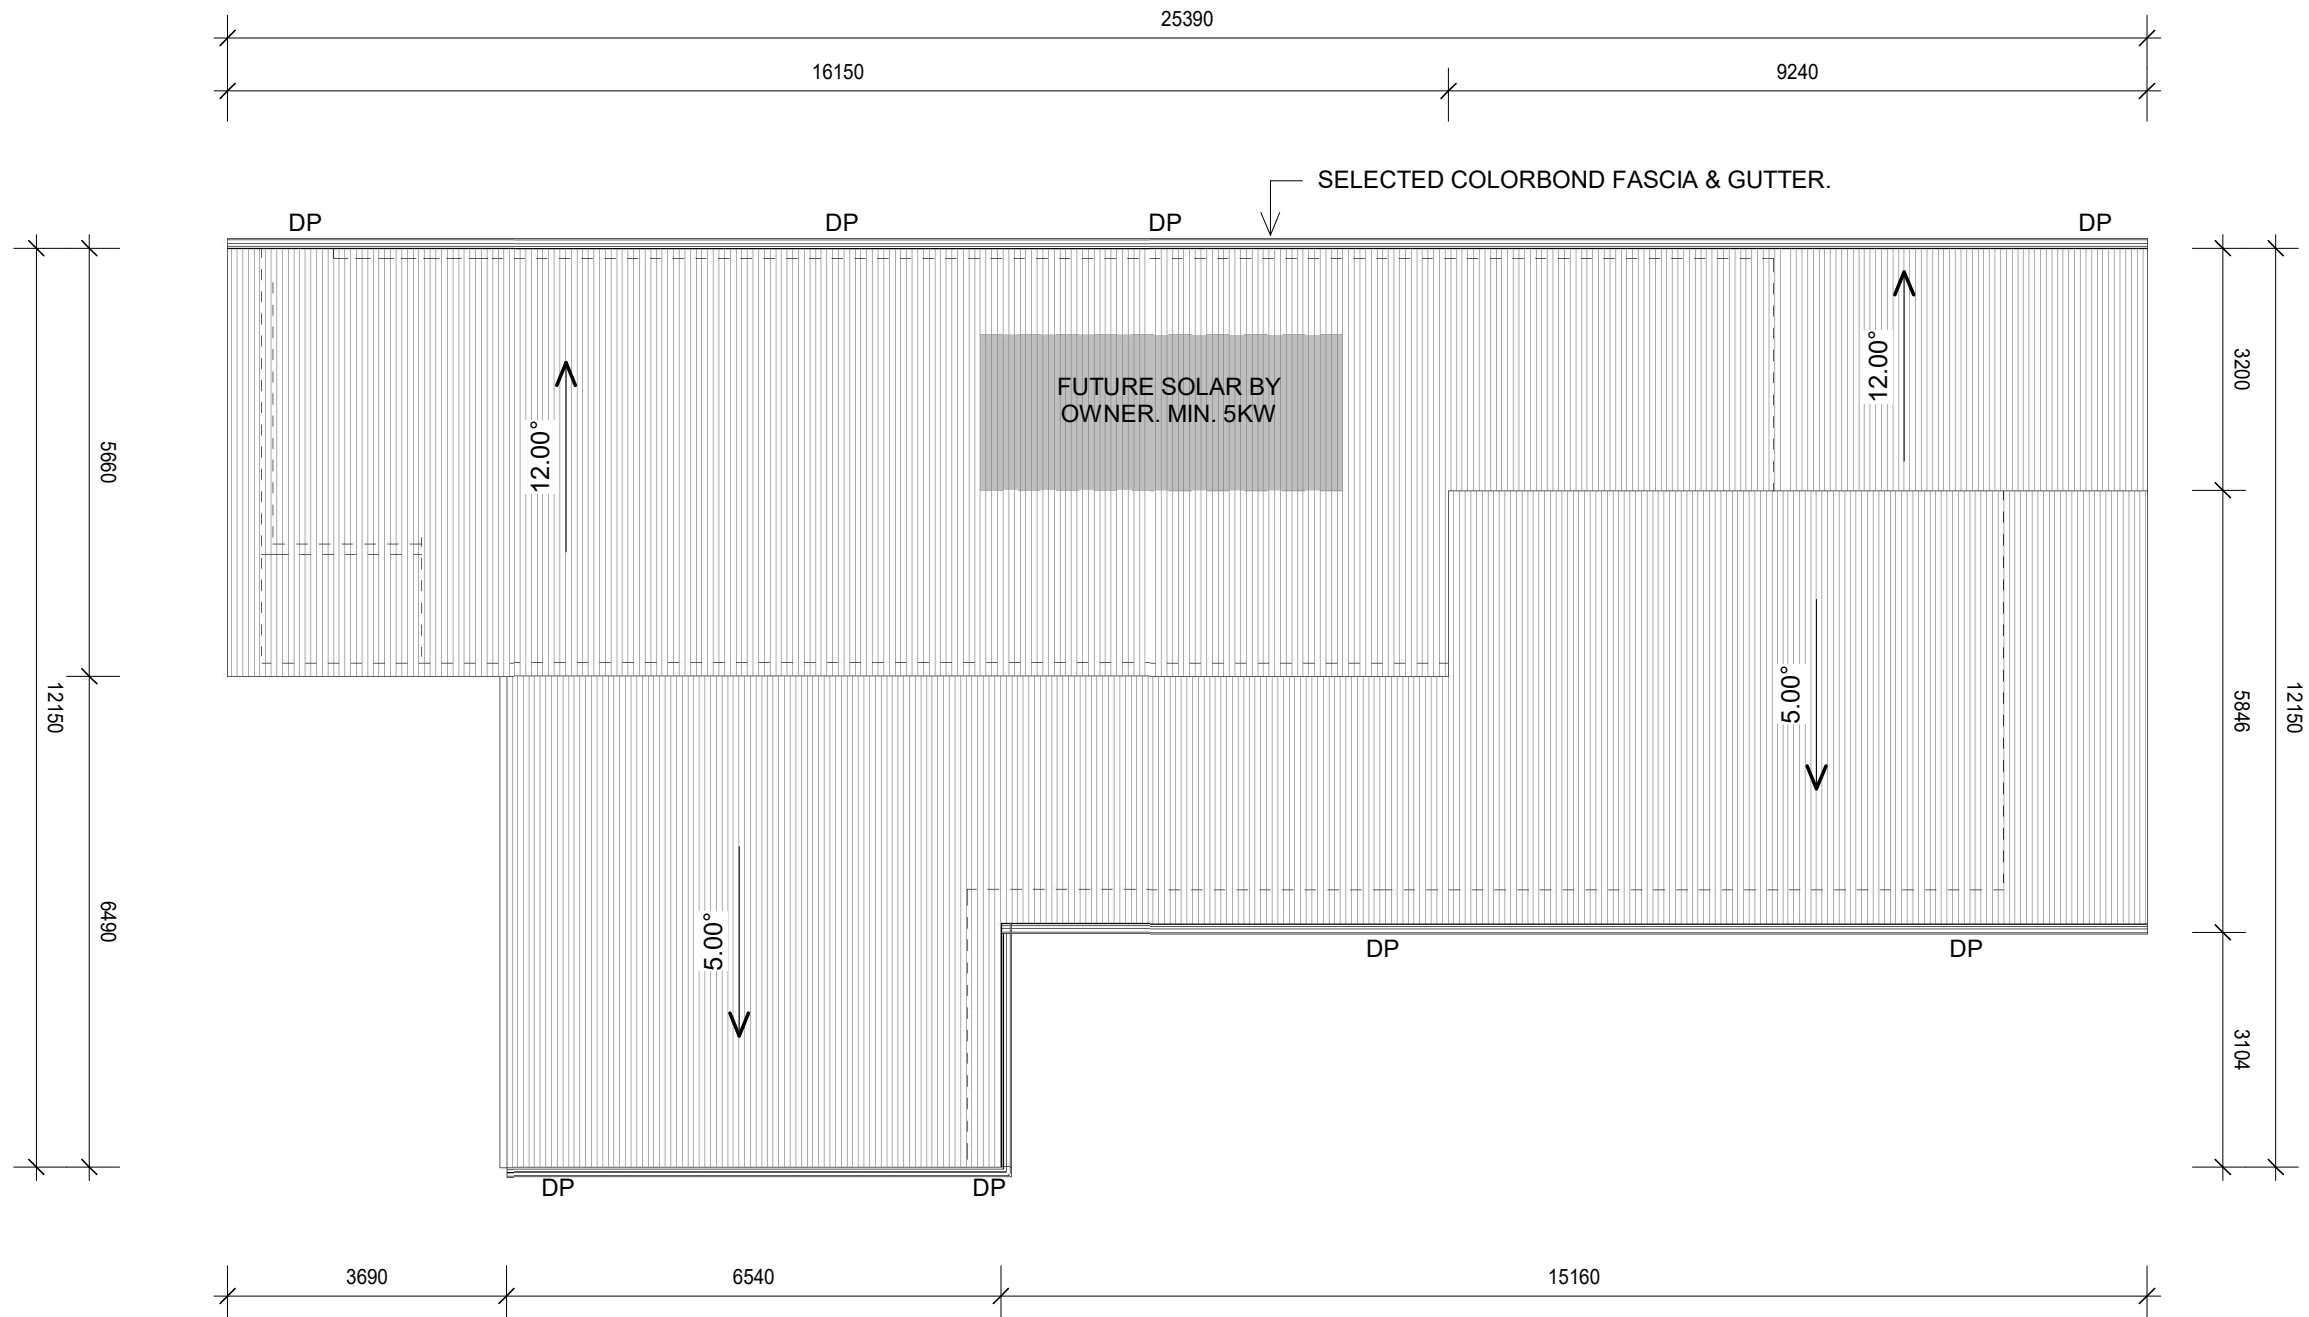



ARCADIA

Made for Memories

(07) 5325 1857 | admin@arcadiahomesqld.com.au | QBCC 15085900

HOMES

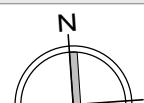CLIENT: PETER & SUZIE CROGAN				SITE ADDRESS: LOT 16 POWERS STREET, EUMUNDI QLD								
				ORIENTATION		AREA CALCULATIONS		REAL PROPERTY DESCRIPTION		FOR APPROVAL		
REVISION	DATE	AMENDMENTS	TECH.			RESIDENCE	193.24 m²	LOT: 16 PLAN: SP325615				
A	9/02/26	FOR APPROVAL	NB			ALFRESCO	28.10 m²	LOCAL AUTHORITY: SUNSHINE COAST COUNCIL				
B	25/02/26	BAL 12.5 & BUSHFIRE NOTES ADDED	NB			PORCH	3.02 m²					
C	13/05/26	FRONT RETAINING REV	DD			TOTAL:	224.36 m²					
D	20/07/26	CONSTRUCTION REVISIONS	DD					PROJECT NO: J1377	DRAWN BY: NB	DRAWING TITLE: ROOF PLAN		
E	28/07/26	CONSTRUCTION REVISIONS	DD			HOUSE DESIGN:	FACADE:	DATE: 28/07/26	SHEET NO.			REV.
						ARLO 185 - MOD	GRANDE	SCALE 1 : 100 @A3	6			E

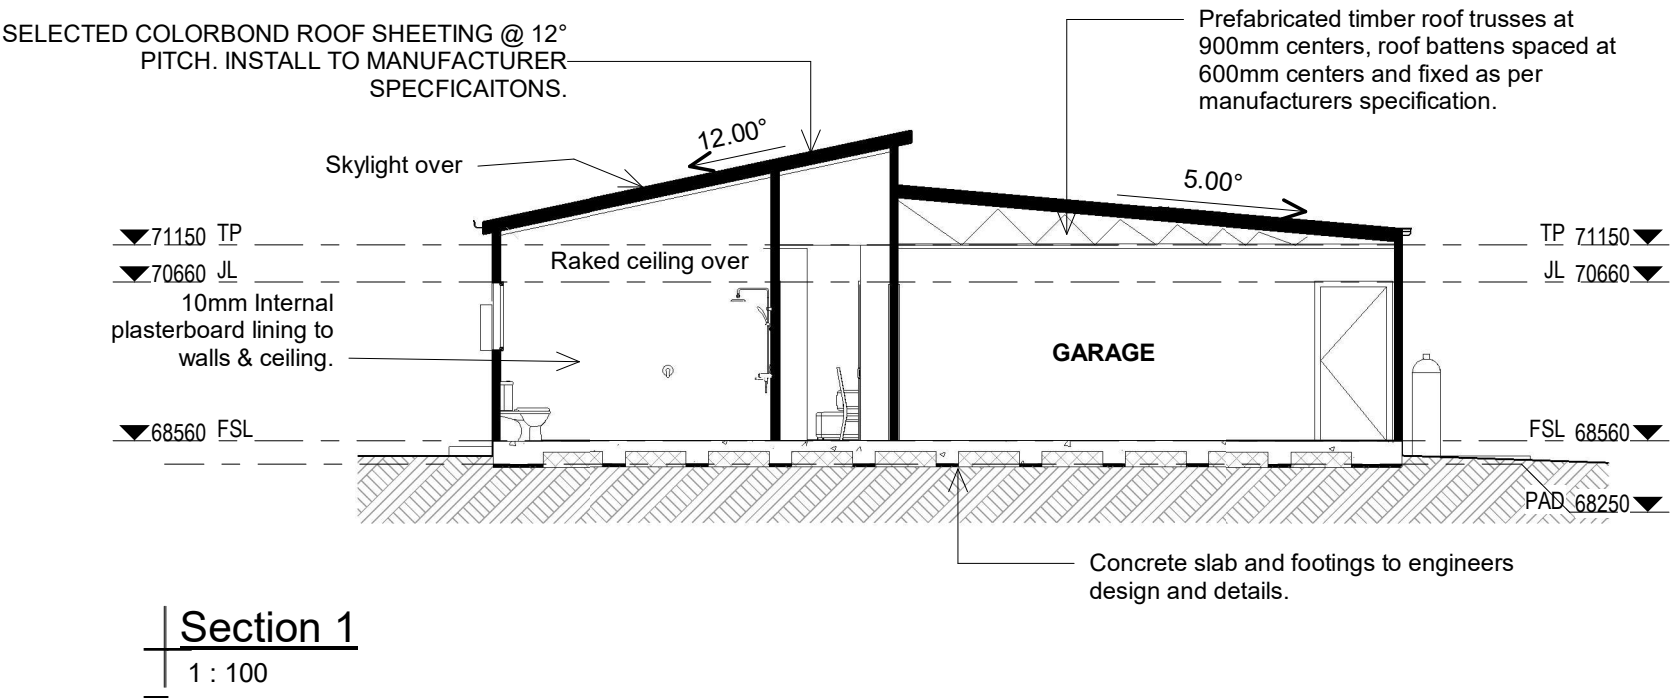

ENERGY EFFICIENCY
REQUIREMENTS SUMMARY

ENERGY REQUIREMENTS:

Please note - All ceiling, roof, external wall & floor insulation nominated in the below summary, has been applied only to areas that are connected to external elements (ie. earth or outside air)

CEILING/ROOF (EXC. GARAGE)

- R4.0 insulation to ceilings
- R1.3 sisalation blanket to underside of roof

EXTERNAL WALLS (EXC. GARAGE)

- R2.0 insulation to all external walls

INTERNAL WALLS

- R2.0 insulation to all external walls
- R2.0 insulation to all walls connecting to roof space

FLOOR

- Waffle pod slab with min. 175mm void and 85mm concrete cover

WINDOWS / GLAZED DOORS / SKYLIGHTS

Glazing – Single

FRAMES – Aluminium

WINDOW MANUFACTURER

- Bradnams Windows and Doors

WHOLE OF HOME

- Gas HWS
- Min. 5kW PV Solar system (future by owner)

ADDITIONAL RQUIREMENTS:


- Outdoor living to have a minimum of 1 x ceiling fan installed.
- Outdoor living roof to have R1.5 insulation added.


General notes:

Down lights to be sealed led units
All exhaust fans to be self-closing. max 250mm dia.
All window frames to be weather stripped.
All gaps and cracks sealed.
All glazing to refer to NatHERS certificate for minimum U & SHGC values.
Please note R values noted represent added insulation and not total r value.
R3.0 (R2.5 under NCC 2019) insulation allowed to ceiling perimeter due to height restrictions (where applicable)
R2.5 insulation to all skylight shafts (where applicable)
Min. R1.0 rigid insulation to vertical edge of concrete slab on ground (required only with any slab heating system)
All insulation to be installed in accordance with AS.3999
Refer to Page 5 of the NatHERS certificate for all other NCC energy efficiency requirements



(07) 5325 1857 | admin@arcadiahomesqld.com.au | QBCC 15085900

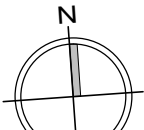
CLIENT: PETER & SUZIE CROGAN				SITE ADDRESS: LOT 16 POWERS STREET, EUMUNDI QLD								
				ORIENTATION		AREA CALCULATIONS		REAL PROPERTY DESCRIPTION		FOR APPROVAL		
REVISION	DATE	AMENDMENTS	TECH.									
A	9/02/26	FOR APPROVAL	NB		RESIDENCE	193.24 m²	LOT: 16	PLAN: SP325615				
B	25/02/26	BAL 12.5 & BUSHFIRE NOTES ADDED	NB		ALFRESCO	28.10 m²	LOCAL AUTHORITY:					
C	13/05/26	FRONT RETAINING REV	DD		PORCH	3.02 m²	SUNSHINE COAST COUNCIL					
D	20/07/26	CONSTRUCTION REVISIONS	DD		TOTAL:	224.36 m²	PROJECT NO: J1377	DRAWN BY: NB				
E	28/07/26	CONSTRUCTION REVISIONS	DD			HOUSE DESIGN:	FACADE:	DATE:	28/07/26	SHEET NO.	REV.	
						ARLO 185 - MOD	GRANDE	SCALE 1 : 100	@A3	7	E	

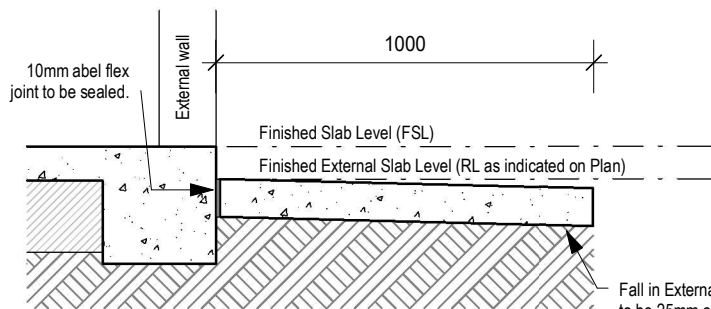

SURFACE WATER DRAINAGE DETAIL

D03 1:20
8

IMPORTANT NOTE:
-No step down to garage.
-Confirm all Details with Engineering plan.

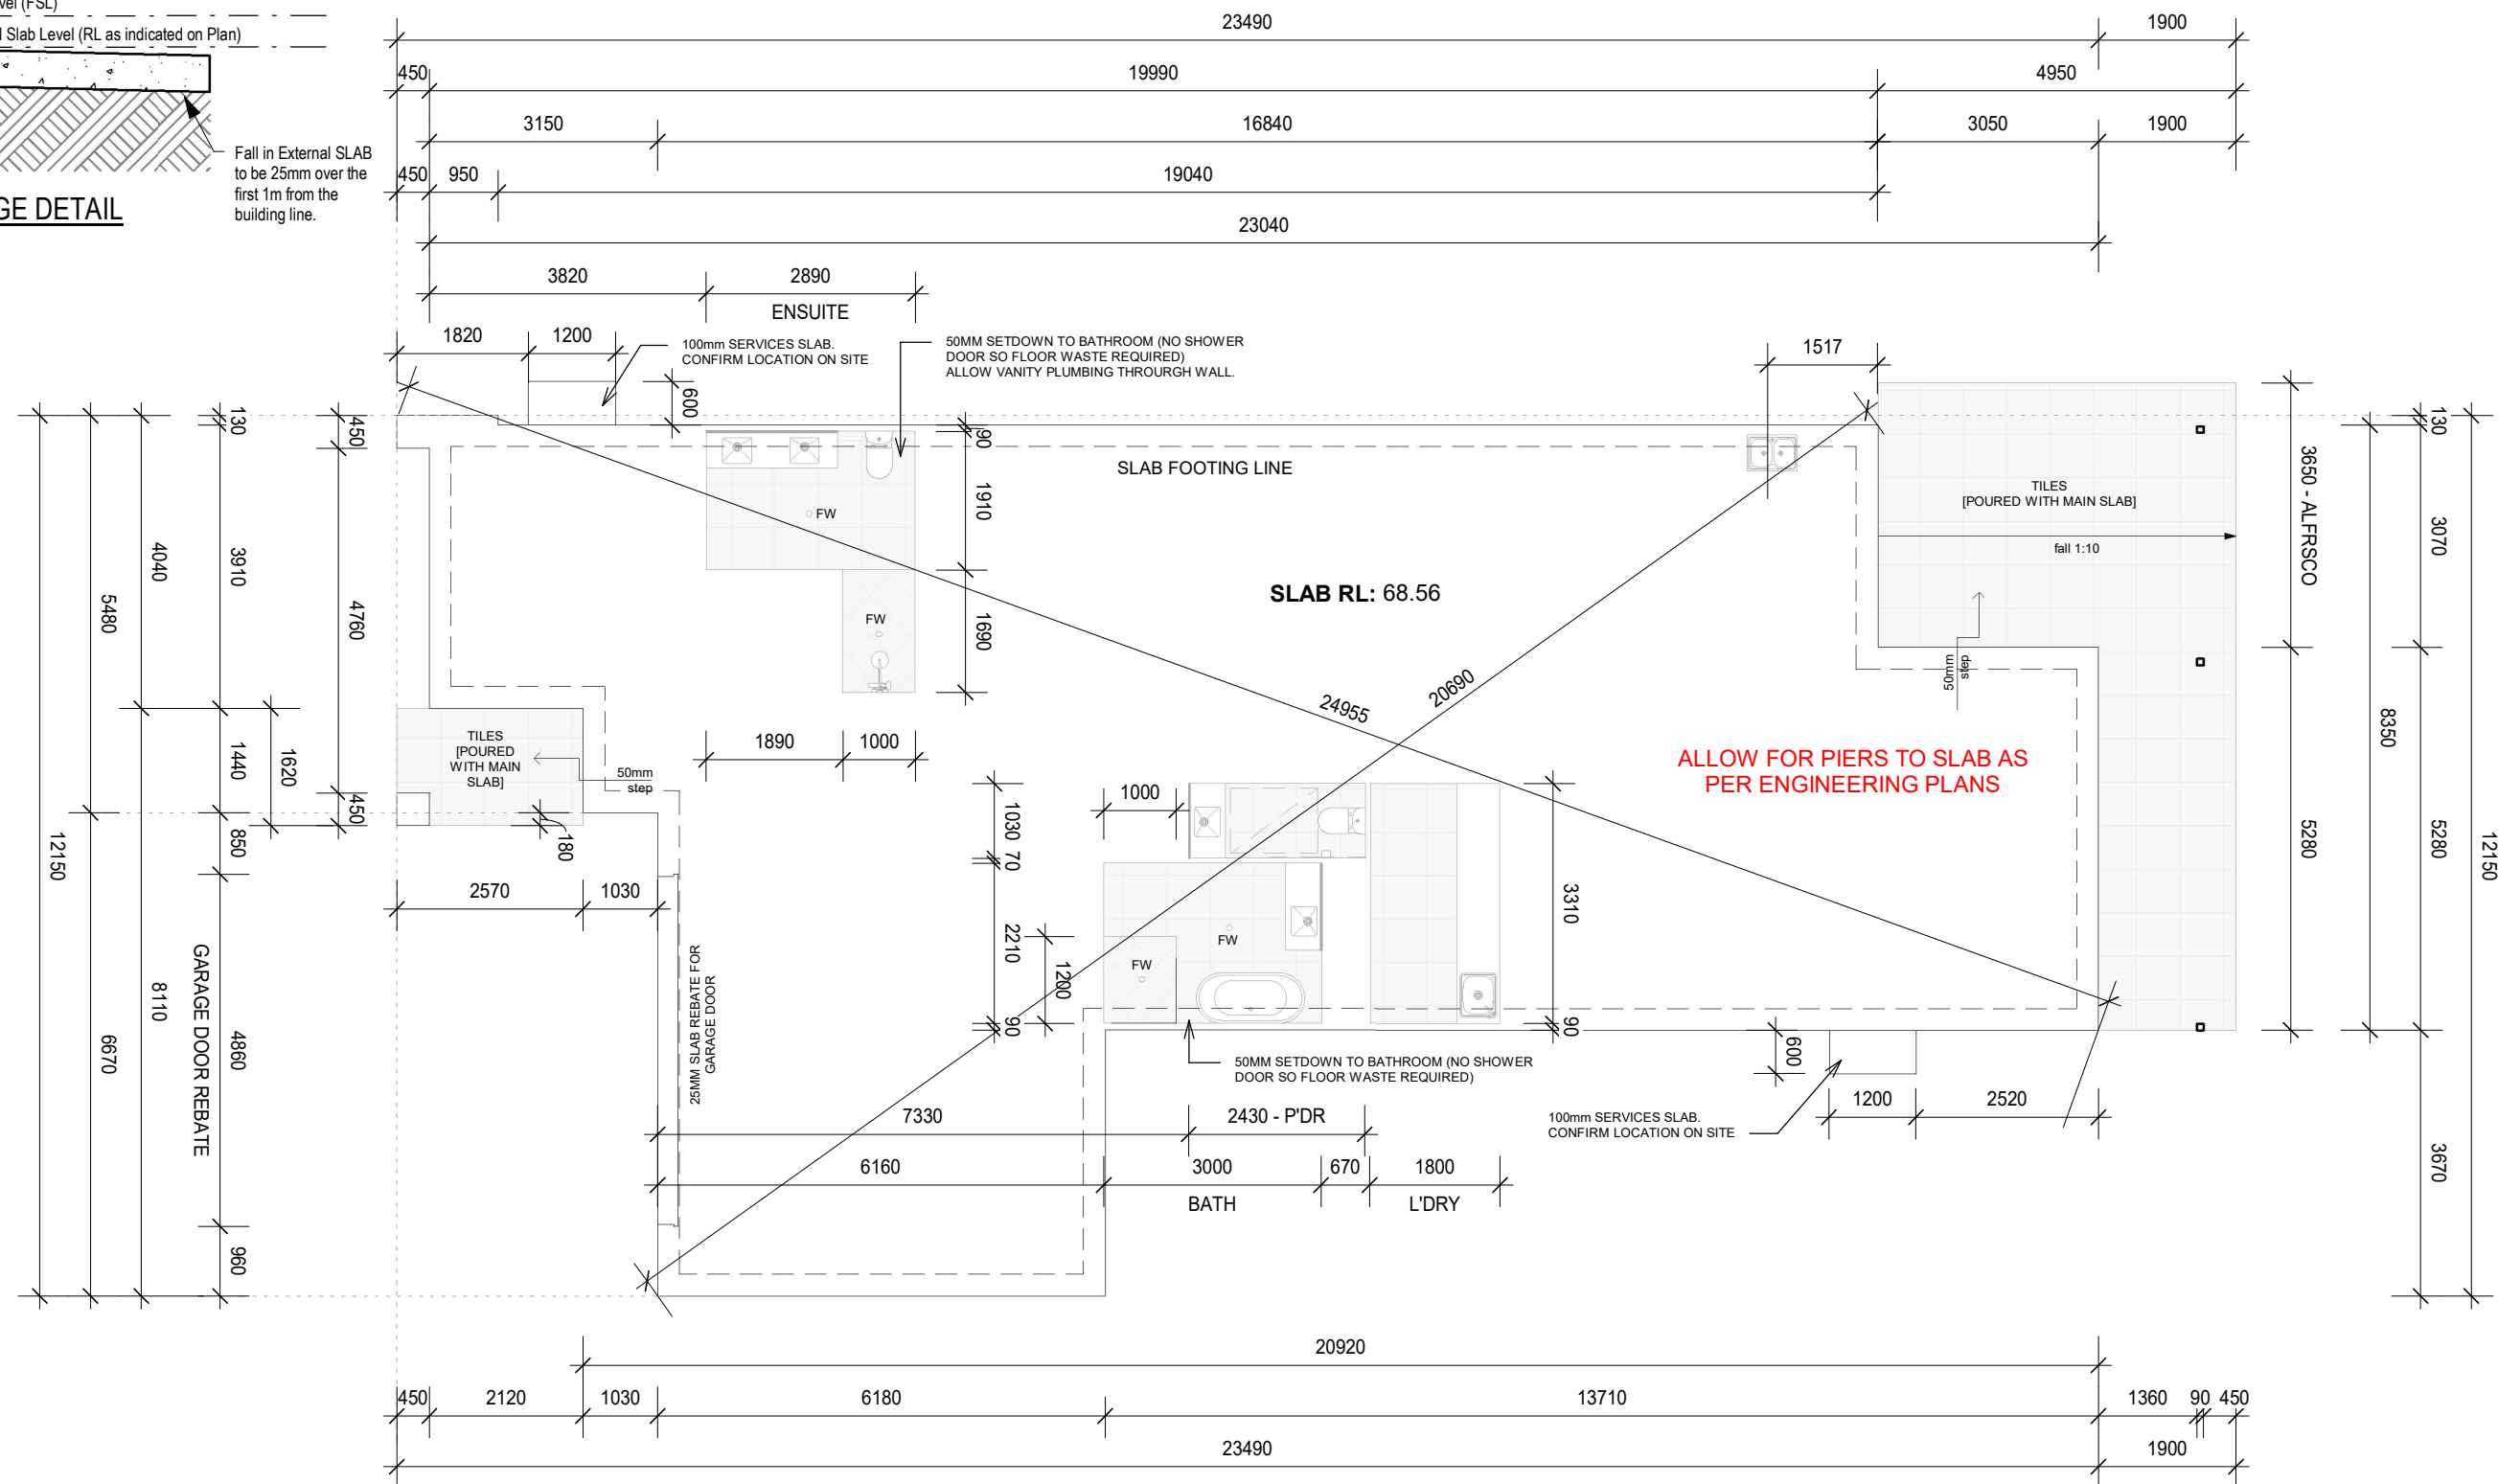


ARCADIA
Made for Memories
HOMES

(07) 5325 1857 | admin@arcadiahomesqld.com.au | QBCC 15085900

CLIENT: PETER & SUZIE CROGAN

SITE ADDRESS: LOT 16 POWERS STREET, EUMUNDI QLD

REVISION	DATE	AMENDMENTS	TECH.
A	9/02/26	FOR APPROVAL	NB
B	25/02/26	BAL 12.5 & BUSHFIRE NOTES ADDED	NB
C	13/05/26	FRONT RETAINING REV	DD
D	20/07/26	CONSTRUCTION REVISIONS	DD
E	28/07/26	CONSTRUCTION REVISIONS	DD

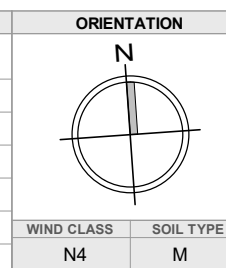


AREA CALCULATIONS		REAL PROPERTY DESCRIPTION	
RESIDENCE	193.24 m²	LOT: 16	PLAN: SP325615
ALFRESCO	28.10 m²	LOCAL AUTHORITY: SUNSHINE COAST COUNCIL	
PORCH	3.02 m²		
TOTAL:	224.36 m²	PROJECT NO: J1377	DRAWN BY: NB
		HOUSE DESIGN:	FACADE:
		ARLO 185 - MOD	GRANDE


FOR APPROVAL			
DRAWING TITLE:			
SLAB PLAN			
DATE:	28/07/26	SHEET NO.	REV.
SCALE	As indicated @A3	8	E

ELECTRICAL LEGEND		
2D Symbol	Quantity	Library Part Name
OPEN CENTRE	2	CEILING FAN 3 BLADE
FILLED CENTRE	3	CEILING FAN LIGHT
	12	DOUBLE GPO
	18	DOWNLIGHT POINT
	3	EXHAUST FAN LIGHT
	1	FLUORO - SINGLE LAMP
	2	INTERNAL AC UNIT
	1	NATIONAL BROADBAND POINT
	1	NBN PATCH PANEL
	2	PENDANT LIGHT
	5	SINGLE GPO
	5	SMOKE ALARM
	1	TV POINT
	1	WEATHERPROOF SGPO


NOTES:
- **ALL DOWNLIGHTS ARE IC/IC-F RATED**
ALL ELECTRICAL WIRING & ELECTRICAL INSTALLATIONS ARE TO COMPLY WITH AS/NZS3000:2007 WIRING RULES
AIR CONDITIONING UNITS ARE TO MEET THE RELEVANT MEPs OF AS/NZS3823.1, AS/NZS3823.2 OR AS/NZS3823.3-2011 FOR BOTH SINGLE AND THREE PHASE
(<http://www.energyrating.gov.au>)
AS/NZS3000:2007 S6.2.4.2 REQUIRES NO ELECTRICAL SOCKET OUTLETS, SWITCHES OR ELECTRICAL ACCESSORIES TO BE INSTALLED WITHIN 300mm FROM A WET PLACE.
ALLOWANCE FOR NBN TO BE CONFIRMED
ALL ELECTRICAL DRAWINGS ARE PRELIMINARY. FINAL ARRANGEMENTS TO OWNERS REQUIREMENTS. ALL EXHAUST FANS TO BE DUCTED EXTERNALLY.
ALL SMOKE ALARMS TO BE INTERCONNECTED AND HARDWIRED.

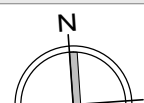

CLIENT: PETER & SUZIE CROGAN				SITE ADDRESS: LOT 16 POWERS STREET, EUMUNDI QLD								
				ORIENTATION		AREA CALCULATIONS		REAL PROPERTY DESCRIPTION		FOR APPROVAL		
REVISION	DATE	AMENDMENTS	TECH.		RESIDENCE 193.24 m² ALFRESCO 28.10 m² PORCH 3.02 m² TOTAL: 224.36 m²		LOT: 16 PLAN: SP325615 LOCAL AUTHORITY: SUNSHINE COAST COUNCIL					
A	9/02/26	FOR APPROVAL	NB		PROJECT NO: J1377 DRAWN BY: NB							
B	25/02/26	BAL 12.5 & BUSHFIRE NOTES ADDED	NB		HOUSE DESIGN: FACADE:							
C	13/05/26	FRONT RETAINING REV	DD		ARLO 185 - MOD GRANDE							
D	20/07/26	CONSTRUCTION REVISIONS	DD		SCALE 1 : 100 @A3							
E	28/07/26	CONSTRUCTION REVISIONS	DD									
				WIND CLASS SOIL TYPE						DRAWING TITLE: ELECTRICAL & LIGHTING PLAN		
				N4 M								

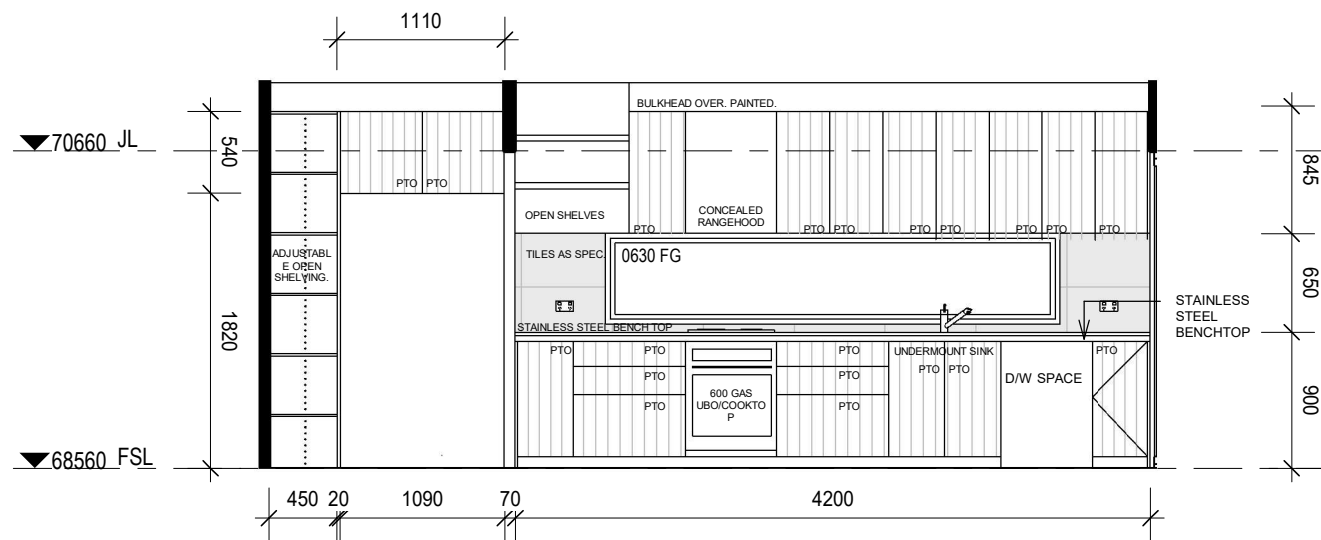


KITCHEN/PANTRY ELEVATION 1
1 : 50

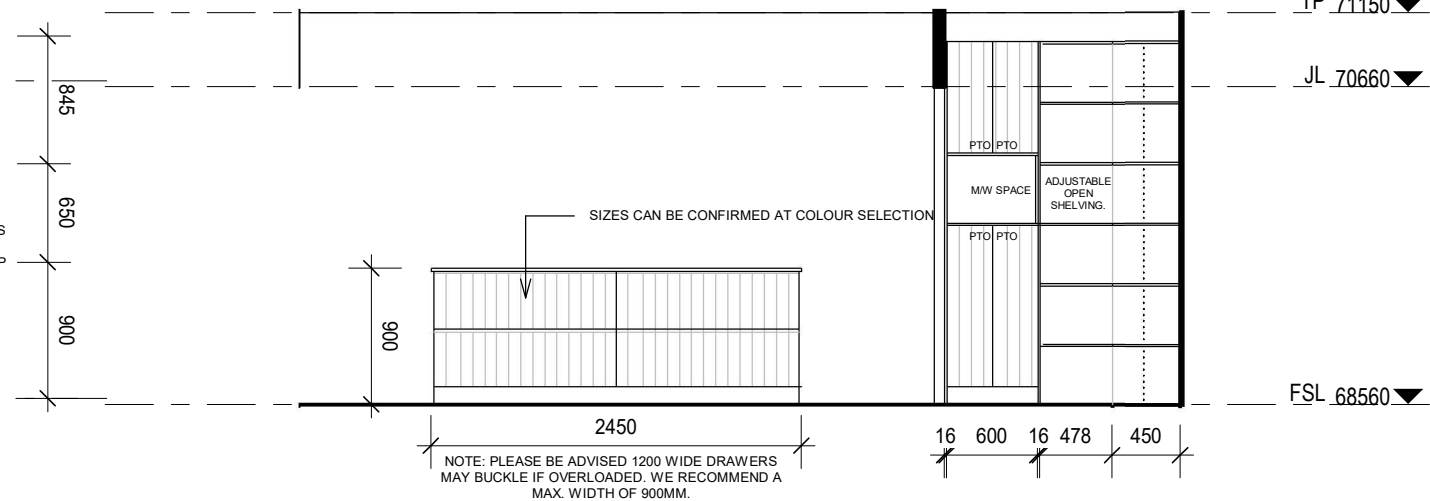


KITCHEN/PANTRY ELEVATION 2
1 : 50


NOTE: ALL CABINETRY TO BE CONFIRMED WITH CABINET MAKER DRAWINGS.

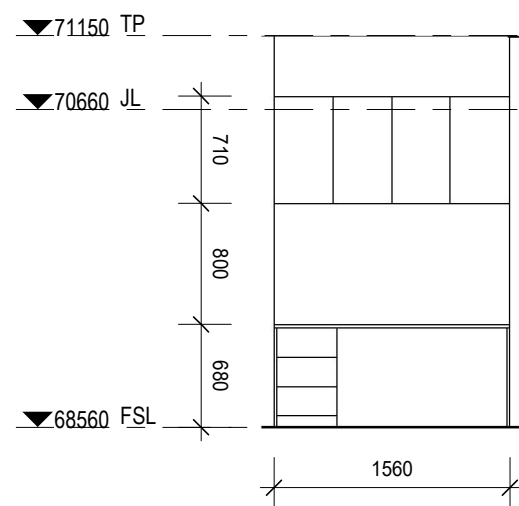

STUDY NOOK ELEVATION
1 : 50

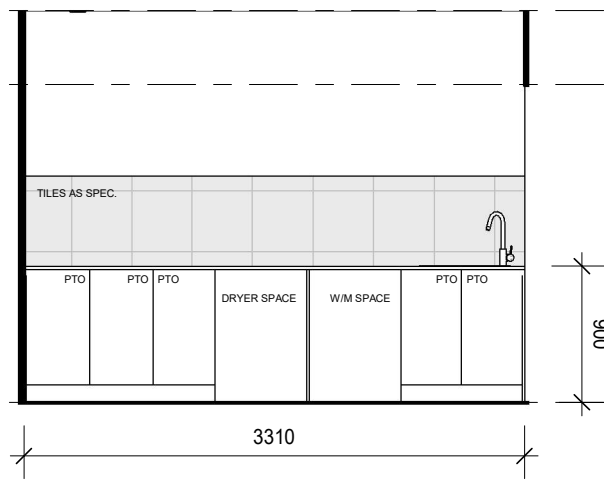


LAUNDRY ELEVATION 1
1 : 50

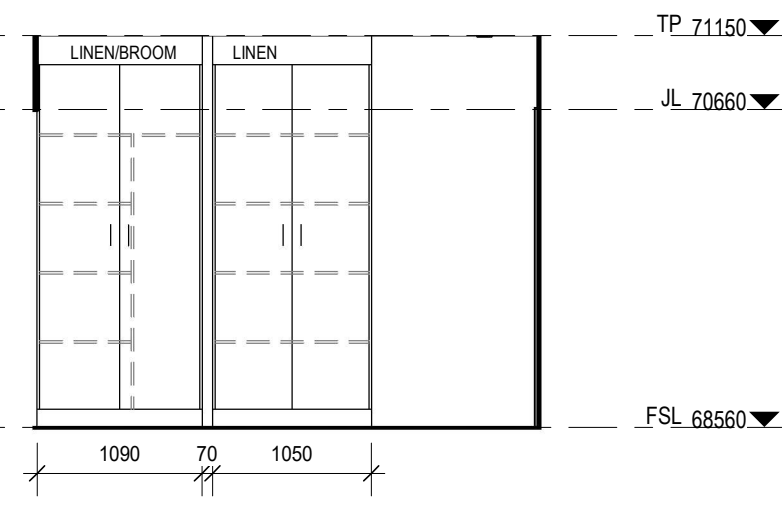


LAUNDRY ELEVATION 2
1 : 50

CLIENT: PETER & SUZIE CROGAN				SITE ADDRESS: LOT 16 POWERS STREET, EUMUNDI QLD			
REVISION	DATE	AMENDMENTS	TECH.	ORIENTATION	AREA CALCULATIONS		REAL PROPERTY DESCRIPTION
					RESIDENCE 193.24 m ² ALFRESCO 28.10 m ² PORCH 3.02 m ² TOTAL: 224.36 m ²		LOT: 16 PLAN: SP325615 LOCAL AUTHORITY: SUNSHINE COAST COUNCIL PROJECT NO: J1377 DRAWN BY: NB
A	9/02/26	FOR APPROVAL	NB		HOUSE DESIGN: ARLO 185 - MOD		FACADE: GRANDE
B	25/02/26	BAL 12.5 & BUSHFIRE NOTES ADDED	NB		DATE: 28/07/26		SHEET NO. 10
C	13/05/26	FRONT RETAINING REV	DD		SCALE 1 : 50 @A3		REV. E
D	20/07/26	CONSTRUCTION REVISIONS	DD				
E	28/07/26	CONSTRUCTION REVISIONS	DD				

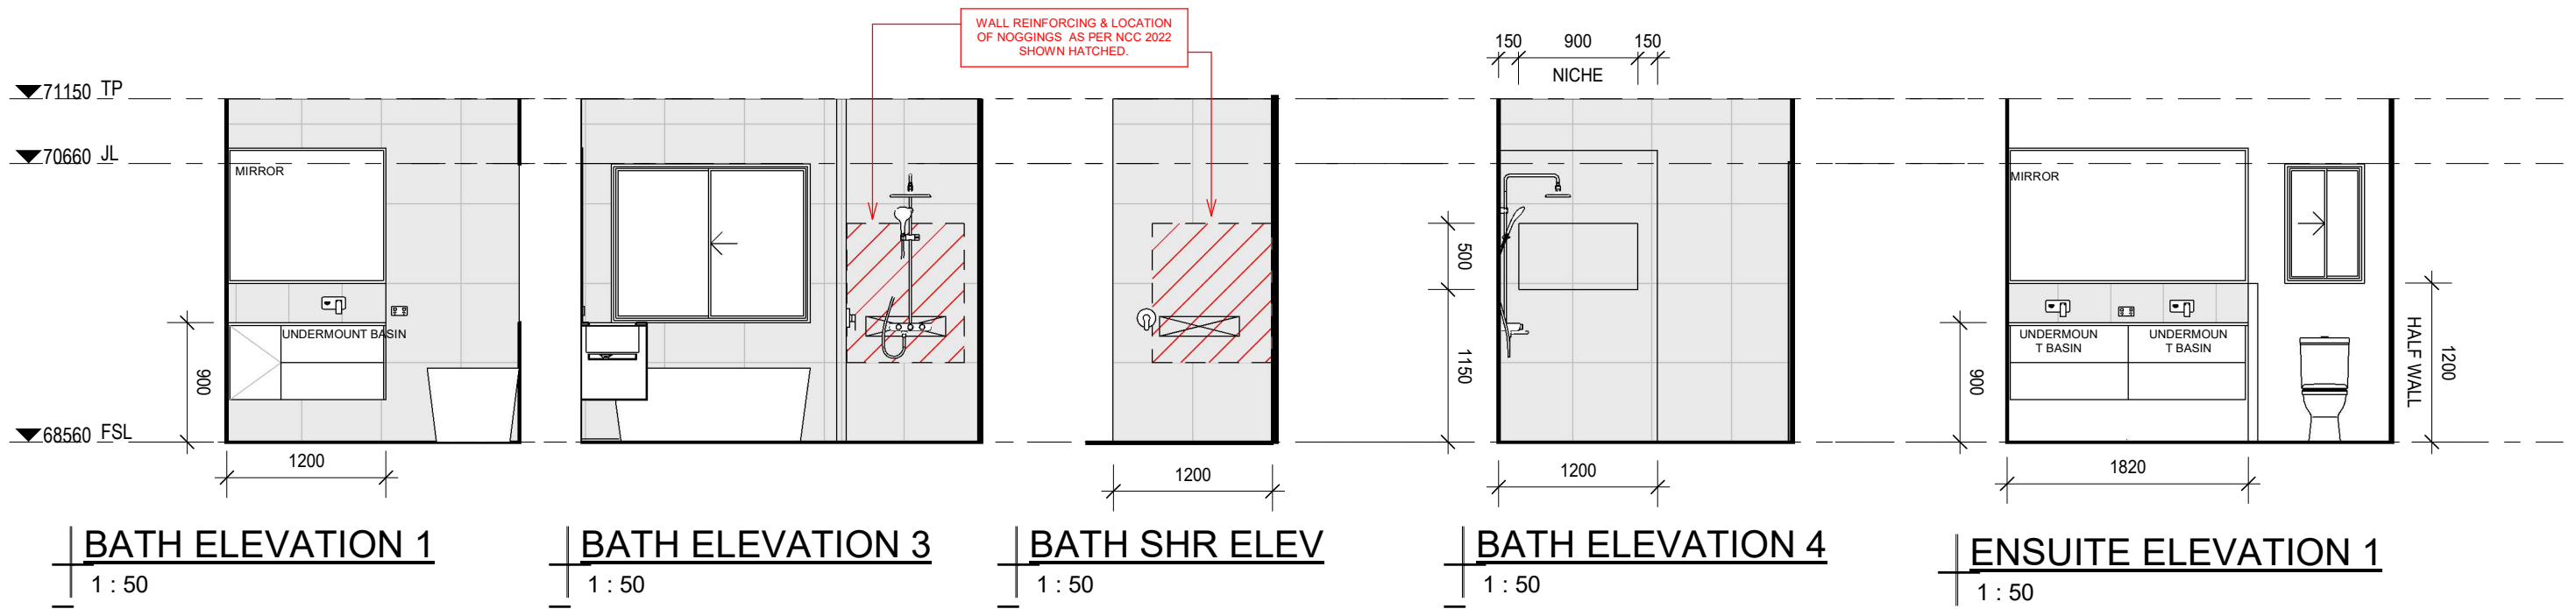


NOTE: ALL CABINETRY TO BE CONFIRMED WITH CABINET MAKER DRAWINGS.

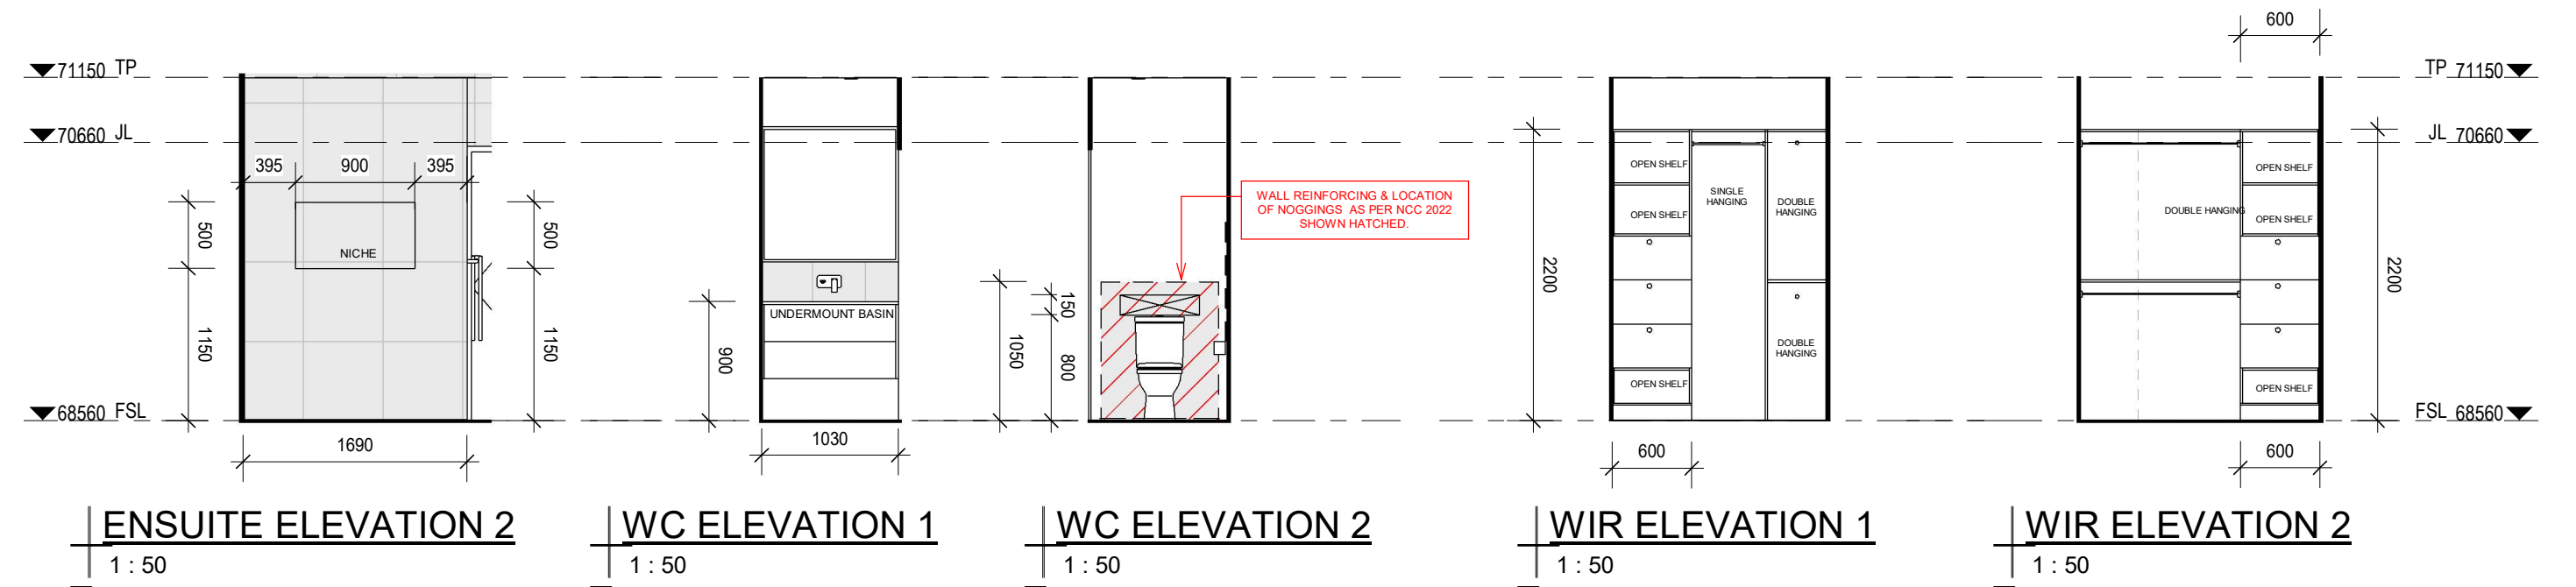


WIR FITOUT TO BE CONFIRMED

ARCADIA
HOMES
Made for Memories




(07) 5325 1857 | admin@arcadiahomesqld.com.au | QBCC 15085900

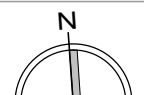CLIENT: PETER & SUZIE CROGAN				SITE ADDRESS: LOT 16 POWERS STREET, EUMUNDI QLD										
				ORIENTATION		AREA CALCULATIONS		REAL PROPERTY DESCRIPTION		FOR APPROVAL				
REVISION	DATE	AMENDMENTS		TECH.			RESIDENCE 193.24 m²		LOT: 16 PLAN: SP325615					
A	9/02/26	FOR APPROVAL		NB			ALFRESCO 28.10 m²		LOCAL AUTHORITY: SUNSHINE COAST COUNCIL					
B	25/02/26	BAL 12.5 & BUSHFIRE NOTES ADDED		NB			PORCH 3.02 m²		PROJECT NO: J1377 DRAWN BY: NB					
C	13/05/26	FRONT RETAINING REV		DD			TOTAL: 224.36 m²		HOUSE DESIGN: FACADE:					
D	20/07/26	CONSTRUCTION REVISIONS		DD					DATE: 28/07/26					
E	28/07/26	CONSTRUCTION REVISIONS		DD	WIND CLASS SOIL TYPE		ARLO 185 - MOD GRANDE		SCALE 1: 50 @A3		SHEET NO. 11		REV. E	
					N4 M									

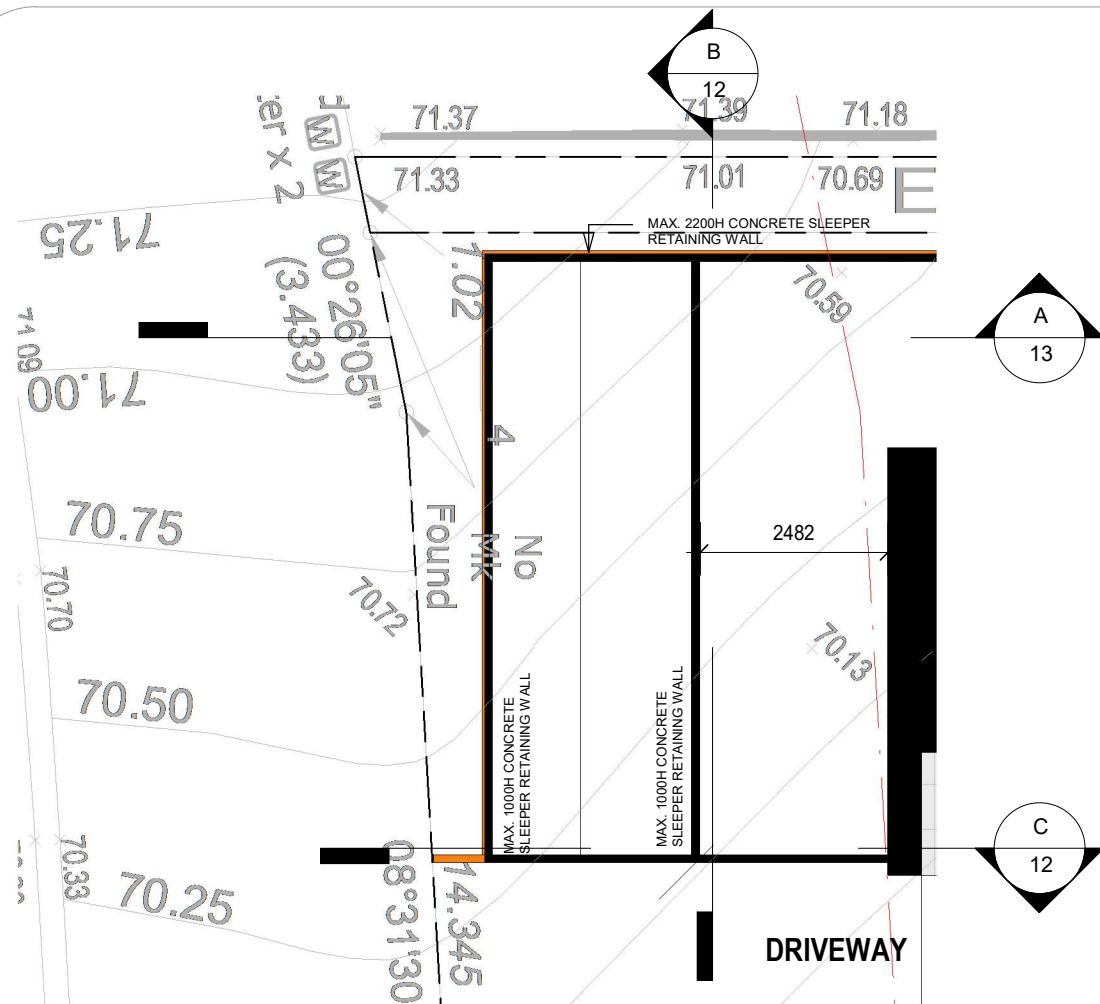


RETAINING PLAN

1 : 100

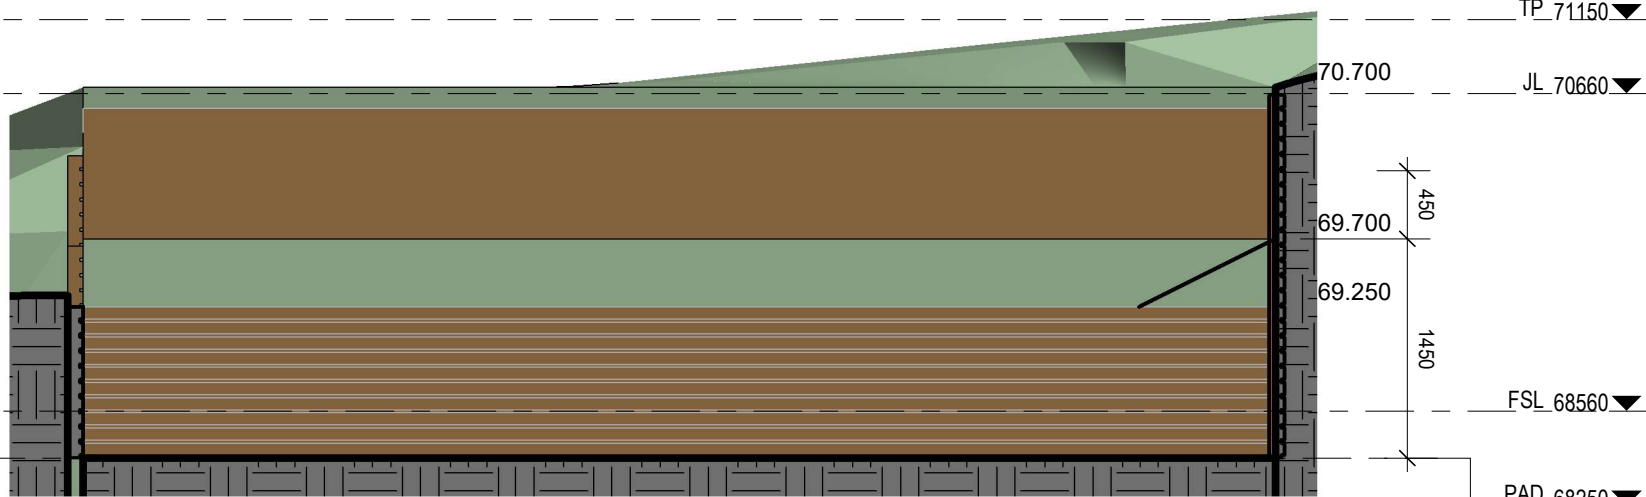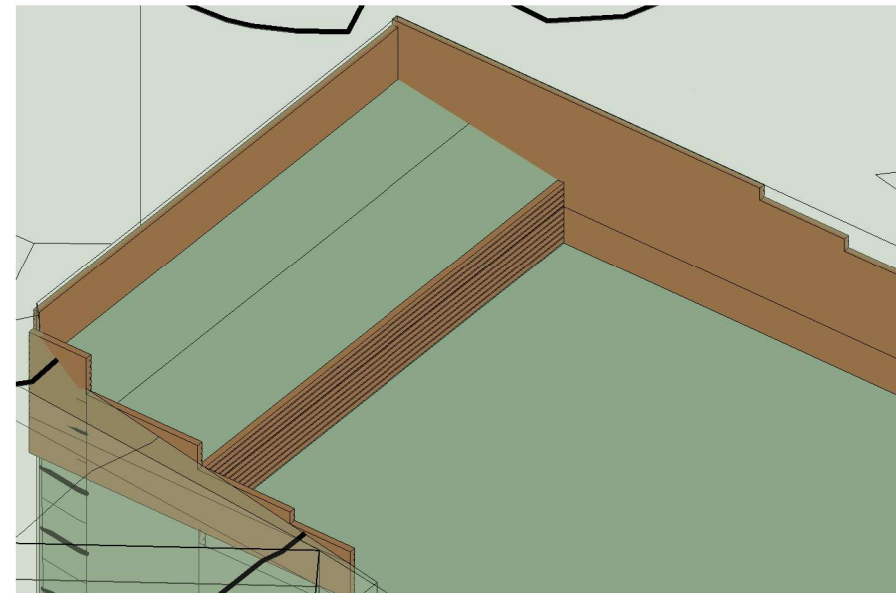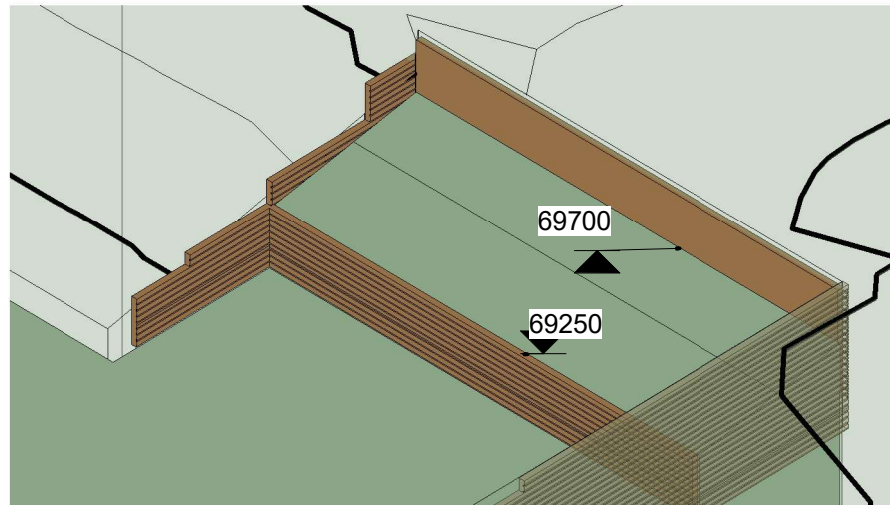

RETAINING B

1 : 50

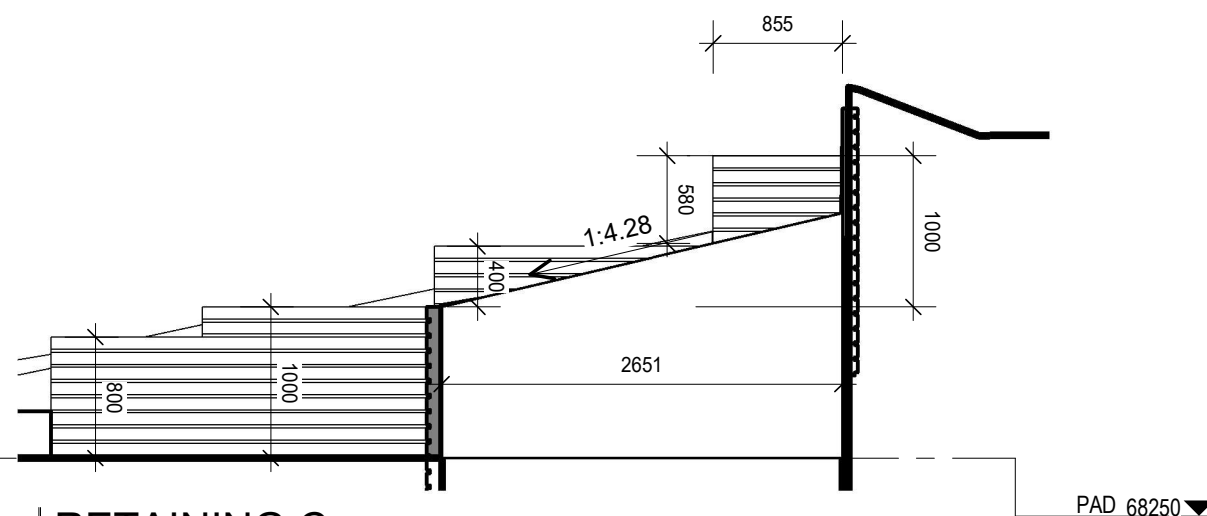

RETAINING C

1 : 50


ARCADIA
Made for Memories **HOMES**

(07) 5325 1857 | admin@arcadiahomesqld.com.au | QBCC 15085900

CLIENT: PETER & SUZIE CROGAN

SITE ADDRESS: LOT 16 POWERS STREET, EUMUNDI QLD

REVISION	DATE	AMENDMENTS	TECH.
A	9/02/26	FOR APPROVAL	NB
B	25/02/26	BAL 12.5 & BUSHFIRE NOTES ADDED	NB
C	13/05/26	FRONT RETAINING REV	DD
D	20/07/26	CONSTRUCTION REVISIONS	DD
E	28/07/26	CONSTRUCTION REVISIONS	DD

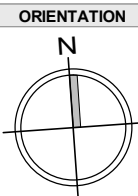

WIND CLASS	SOIL TYPE
N4	M



AREA CALCULATIONS	
RESIDENCE	193.24 m ²
ALFRESCO	28.10 m ²
PORCH	3.02 m ²
TOTAL:	224.36 m ²

REAL PROPERTY DESCRIPTION	
LOT: 16 PLAN: SP325615	
LOCAL AUTHORITY:	SUNSHINE COAST COUNCIL
PROJECT NO: J1377	DRAWN BY: NB
HOUSE DESIGN:	FACADE:
ARLO 185 - MOD	GRANDE

FOR APPROVAL

DRAWING TITLE:
RETAINING DETAILS

DATE:	28/07/26	SHEET NO.	REV.
SCALE	As indicated @A3	12	E

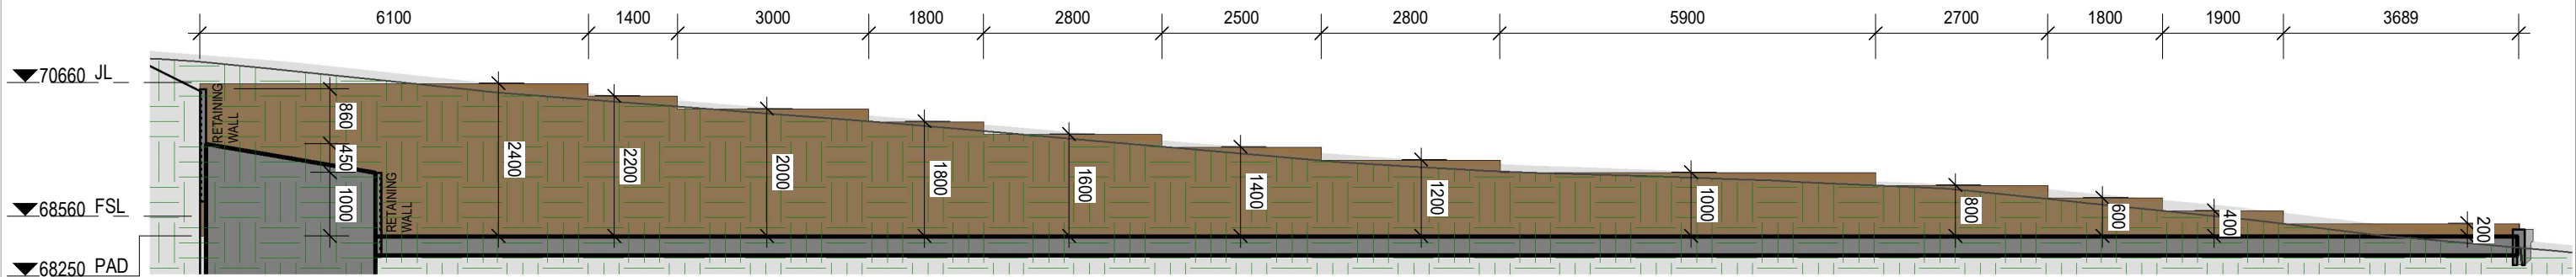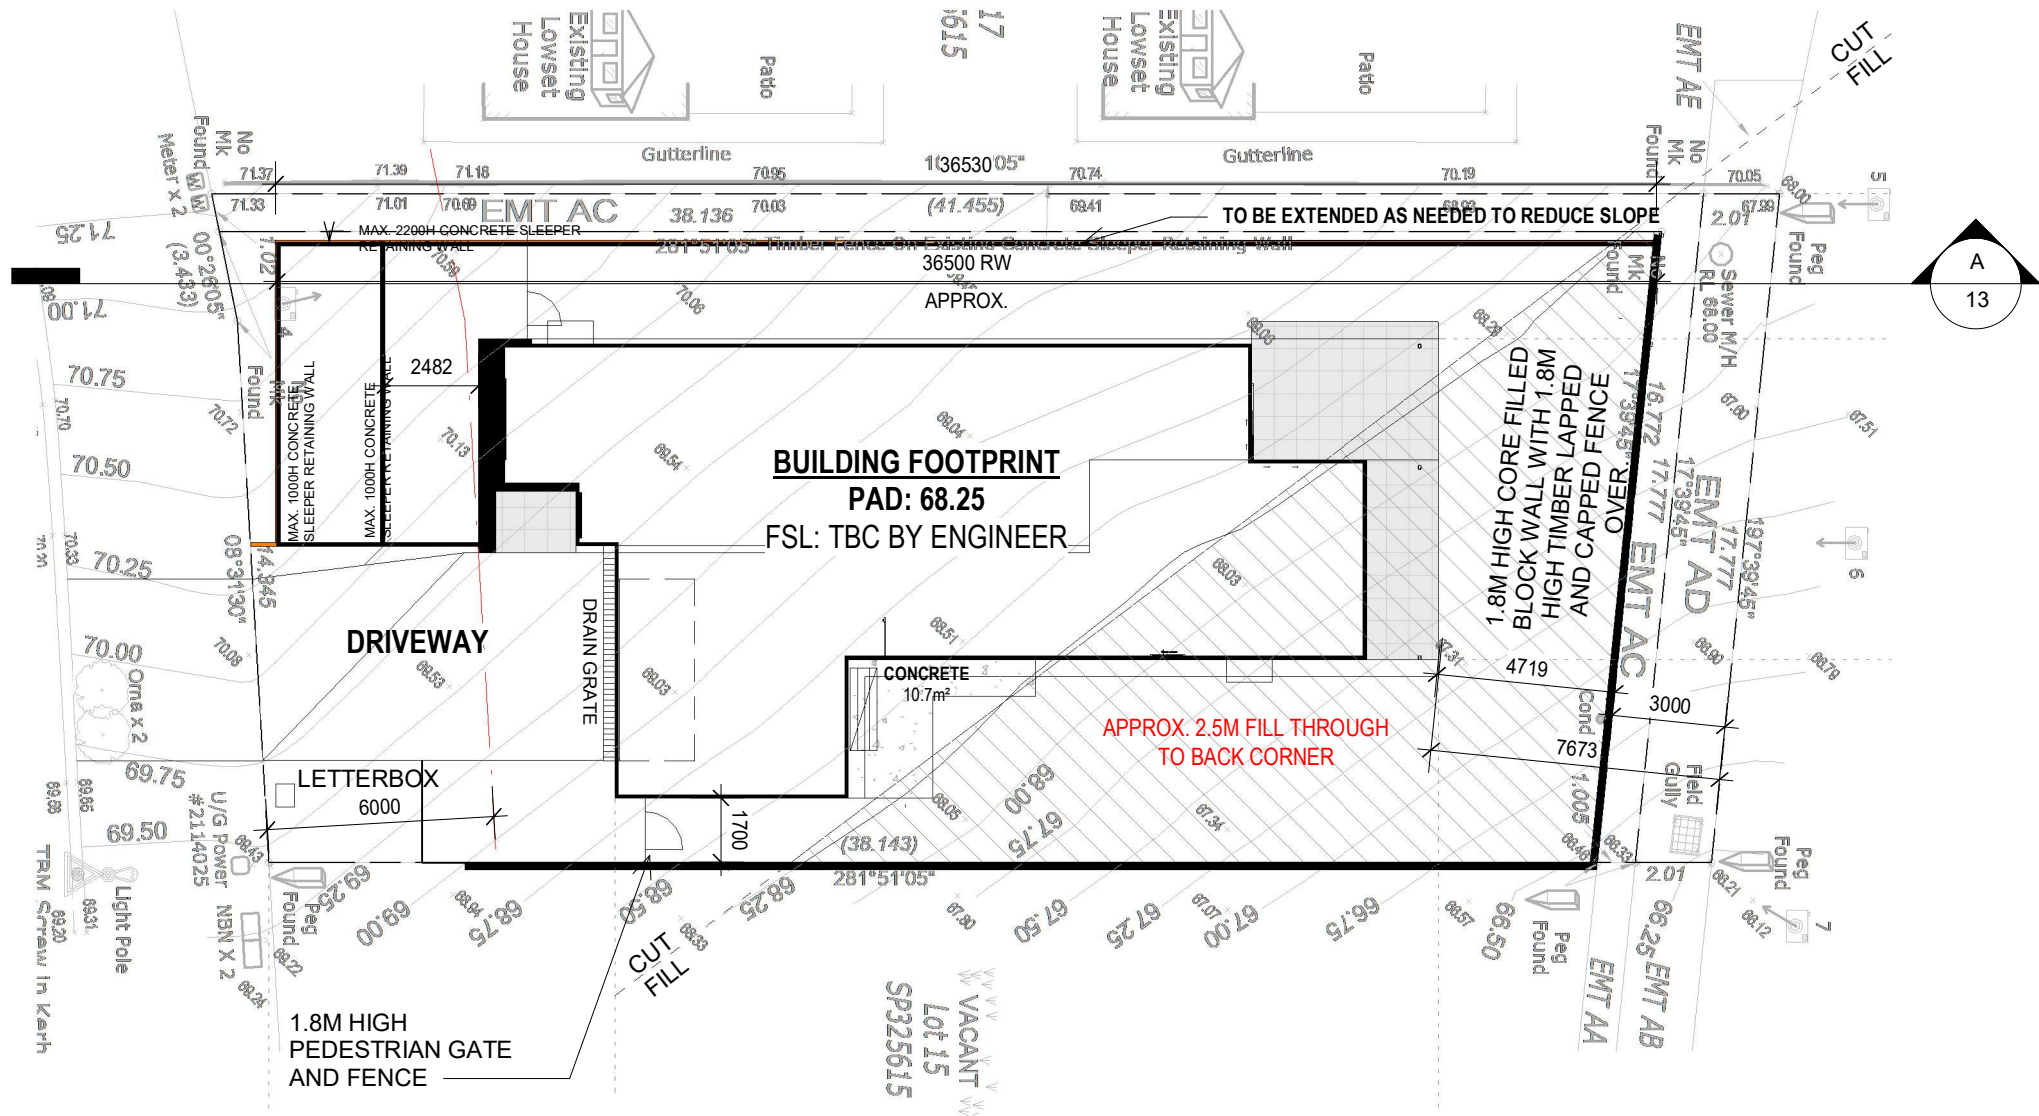

RETAINING A

1 : 100




(07) 5325 1857 | admin@arcadiahomesqld.com.au | QBCC 15085900

CLIENT: PETER & SUZIE CROGAN

SITE ADDRESS: LOT 16 POWERS STREET, EUMUNDI QLD

REVISION	DATE	AMENDMENTS	TECH.
A	9/02/26	FOR APPROVAL	NB
B	25/02/26	BAL 12.5 & BUSHFIRE NOTES ADDED	NB
C	13/05/26	FRONT RETAINING REV	DD
D	20/07/26	CONSTRUCTION REVISIONS	DD
E	28/07/26	CONSTRUCTION REVISIONS	DD

ORIENTATION

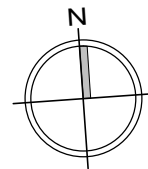

WIND CLASS	SOIL TYPE
N4	M

AREA CALCULATIONS

RESIDENCE	193.24 m ²
ALFRESCO	28.10 m ²
PORCH	3.02 m ²
TOTAL:	224.36 m ²

REAL PROPERTY DESCRIPTION

LOT: 16 PLAN: SP325615

LOCAL AUTHORITY:
SUNSHINE COAST COUNCIL

PROJECT NO: J1377 DRAWN BY: NB

HOUSE DESIGN: FACADE:

ARLO 185 - MOD GRANDE

FOR APPROVAL

DRAWING TITLE:

RETAINING DETAILS

DATE: 28/07/26 SHEET NO. REV. 13 E

SCALE As indicated @A3