


ARCHITECTURAL DRAWINGS

PROPOSED SERVICE STATION DEVELOPMENT

22 ENTERPRISE CIRCUIT, MARYBOROUGH WEST, QLD 4650

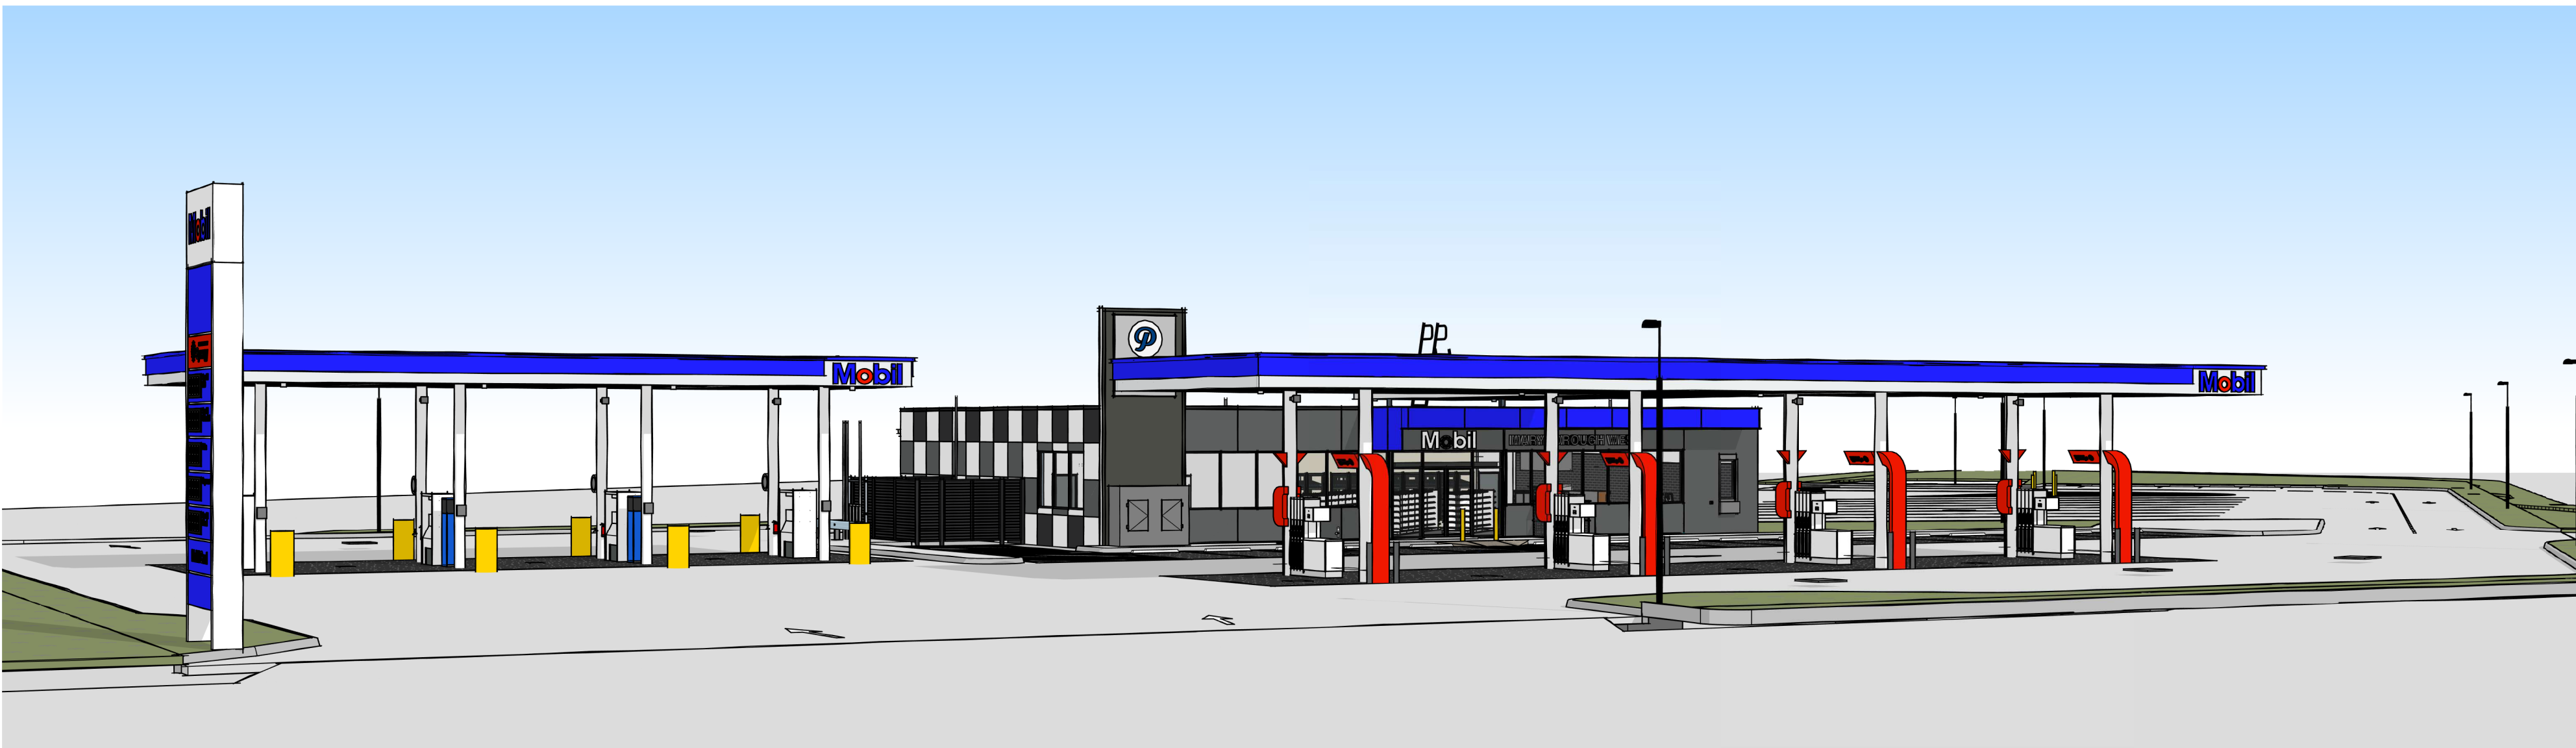

3D PERSPECTIVE FOR ILLUSTRATION ONLY

ARCHITECTURAL DRAWINGS	
DRG No.	DRAWING TITLE
A000	TITLE SHEET & DRAWING SCHEDULE
A001	NOTES
A050	GRID SETOUT PLAN
A100	PROP. OVERALL SITE PLAN
A101	PART SITE PLAN - A
A102	PART SITE PLAN - B
A110	PROP. FLOOR PLAN
A115	PROP. ROOF PLAN
A120	PROP. REFLECTED CEILING PLAN
A130	PROP. SLAB SETOUT PLAN
A140	PROP. FLOOR FINISHES & PARTITIONS PLAN
A200	PROP. BUILDING ELEVATIONS
A201	PROP. BUILDING ELEVATIONS
A210	PROP. BUILDING SECTIONS

ARCHITECTURAL DRAWINGS	
DRG No.	DRAWING TITLE
A250	PROP. CAR & TRUCK FORECOURT CANOPY PLANS
A251	PROP. TRUCK FORECOURT CANOPY ROOF & RCP
A252	PROP. CAR FORECOURT CANOPY ROOF
A253	PROP. CAR FORECOURT CANOPY RCP
A260	PROP. CAR FORECOURT CANOPY ELEVATIONS
A261	PROP. TRUCK FORECOURT CANOPY ELEVATIONS
A262	PROP. FORECOURT TRUCK CANOPY SECTIONS
A263	PROP. FORECOURT CAR CANOPY SECTIONS
A500	INTERNAL ELEVATIONS - AMENITIES
A501	INTERNAL ELEVATIONS - AMENITIES
A502	INTERNAL ELEVATIONS - AMENITIES
A503	INTERNAL ELEVATIONS - AMENITIES
A600	DOOR SCHEDULE
A610	WINDOW ELEVATIONS

GENERAL NOTES

- THESE DRAWINGS TO BE READ IN CONJUNCTION WITH ALL OF THE CONSULTANT DRAWINGS, SCOPES OF WORK, AND REPORTS FOR THE PROJECT
- DO NOT SCALE DRAWINGS – FIGURED DIMENSIONS ARE TO TAKE PRECEDENCE AT ALL TIMES.
- ALL DIMENSIONS TO BE CONFIRMED ON SITE AND/OR VERIFIED PRIOR TO CONSTRUCTION OR FABRICATION.
- ALL MATERIALS AND WORKMANSHIP SHALL BE IN ACCORDANCE WITH CURRENT AND RELEVANT SAA CODES, NATIONAL CONSTRUCTION CODE, THE BUILDING ACT, AND LOCAL AUTHORITIES BY-LAWS.
- ALL STAIRS, RAMPS, HANDRAILS AND BALUSTRADES ARE TO COMPLY WITH NATIONAL CONSTRUCTION CODE, SECTION D & AS1428.1.
- THE CONTRACTOR SHALL BE RESPONSIBLE FOR THE STRUCTURE DURING ERECTION AND PROVIDE ADEQUATE PROPPING AND SUPPORT
- ANY REFERENCE TO THE 'NCC' REFERS TO THE NATIONAL CONSTRUCTION CODE **2022**
- THE CONTRACTOR SHALL CARRY OUT A TRIAL SET-OUT OF THE BUILDING & VERIFY ALL SET-OUT DIMENSIONS PRIOR TO; ORDERING, COMMENCEMENT OF FABRICATION & CONSTRUCTION OF THE WORKS.
- ALL TOILET AND AIRLOCK WALLS TO BE 45 STC SOUND RATED.
- INSULATION TO THE BUILDING ENVELOPE TO BE PROVIDED IN ACCORDANCE WITH THE REQUIREMENTS OF THE SECTION J REPORT.
- WHERE NEW SURFACE MATERIALS ARE APPLIED OVER EXISTING SUBSTRATES, THE CONTRACTOR SHALL ENSURE THAT ALL NEW MATERIALS ARE APPLIED IN STRICT ACCORDANCE WITH THE MANUFACTURER'S SPECIFICATIONS.
- BUILDER/HEAD CONTRACTOR & SUBCONTRACTORS, INCLUDING ALL RELEVANT TRADES, TO CONFIRM ALL LEAD TIMES DURING TENDER PHASE AND ORDER ACCORDINGLY ON AWARD OF CONTRACT TO THE HEAD CONTRACTOR. ALL SPECIFIED MATERIALS/FINISHES HAVE LEAD TIMES WHICH VARY BETWEEN SUPPLIERS.
- ALL ELEMENTS IDENTIFIED IN AS1170.4 SECTIONS 2 & 8 ARE TO BE DESIGNED, SUPPLIED & INSTALLED BY THE BUILDER/ CONTRACTOR TO ENSURE COMPLIANCE WITH THE REQUIREMENTS OF AS1170.4

ASBESTOS

REFER TO ASBESTOS REGISTER. ANY KNOWN OR SUSPECTED ASBESTOS IN THE AREA OF WORK SHALL BE HANDLED AS FOLLOWS:

- ALL REMOVAL, REPAIR AND RENOVATION OF PRODUCTS CONTAINING ASBESTOS SHALL BE CARRIED OUT IN ACCORDANCE WITH THE NOHSC ASBESTOS CODE OF PRACTICE & GUIDANCE NOTES AND WORK HEALTH INFORMATION BULLETINS PUBLISHED BY THE RELEVANT NATIONAL AND STATE/TERRITORY WH&S AUTHORITIES.
- REMOVAL OF ASBESTOS SHALL BE BY SPECIALIST SUBCONTRACTORS.
- THE SPECIALIST CONTRACTOR WILL ENSURE WORKMEN ARE PROVIDED WITH APPROPRIATE SAFETY APPAREL AND BREATHING APPARATUS AS APPLICABLE IN ACCORDANCE WITH AS1715 AND AS1716.
- THE SUPERINTENDENT IS TO ENGAGE AND MANAGE AN INDEPENDENT ASBESTOS HYGIENIST TO MONITOR REMOVAL WORKS

DEMOLITION

- ALL DEMOLITION WORKS TO BE CARRIED OUT IN ACCORDANCE WITH AS2601.
- DEMOLITION CONTRACTOR TO CONFIRM LOCATIONS & MAKE THEMSELVES AWARE OF ALL EXTERNAL SERVICES BEFORE COMMENCEMENT OF ANY WORKS ON SITE
- ANY POTENTIAL ISSUES OR DISRUPTION TO SERVICES TO ADJOINING PROPERTIES TO BE NOTIFIED IMMEDIATELY TO THE SUPERINTENDENT
- SERVICES AFFECTED BY DEMOLITION WORKS ARE TO BE MADE GOOD OR CAPPED OFF AS REQUIRED. REMOVAL ALL REDUNDANT FITTINGS, FIXTURES AND SERVICES BACK TO THEIR SOURCE.
- WHERE EXISTING SERVICES ARE DAMAGED BY DEMOLITION WORKS, THEY SHALL BE MADE GOOD TO MATCH EXISTING ADJACENT SURFACES.
- ALLOW FOR TEMPORARY DUST PROOFING / HOARDING & SECURITY AROUND WORK AREAS & PROVIDE SUITABLE EGRESS & ACCESS FOR OCCUPIED AREAS OF THE SITE AS REQUIRED.
- REGULARLY REMOVE ALL DEMOLISHED MATERIALS FROM SITE & MAINTAIN A CLEAN & TIDY SITE THROUGHOUT CONSTRUCTION. ALLOW FOR REMOVAL OF ALL DEMOLITION MATERIALS FROM SITE UNLESS NOTED BY CIVIL ENGINEER AS SUITABLE FOR SITE FILL. REFER TO CIVIL ENGINEER'S DRAWINGS
- MAKE GOOD TO ALL SITE LEVELS FOR NEW WORKS
- PROTECT ALL EXISTING RETAINED ADJACENT BUILDINGS, PAVING AND OTHER EXTERNAL STRUCTURES THROUGHOUT DEMOLITION & CONSTRUCTION WORKS.
- ALL EXTERNAL BUILDING FINISHES THAT ARE BEING RETAINED AND NOT RECEIVING A NEW FINISH SHOULD BE THOROUGHLY CLEANED. ANY VISIBLE DAMAGE TO THOSE SURFACES SHOULD BE REPORTED TO THE SITE SUPERVISOR.
- WHEN WALLS/ROOF ARE OPEN FOR INSTALLATION OF NEW WORKS, PROVIDE WEATHER PROTECTION AND SECURITY FROM UNAUTHORIZED ENTRY INTO THE BUILDING.
- REMOVE ALL REDUNDANT SURFACE MOUNTED EXPOSED DUCTS, CONDUITS & FIXINGS.
- REFER ALSO TO ELECTRICAL & MECHANICAL SERVICES DOCUMENTATION FOR ANY ADDITIONAL DEMOLITION WORK.
- RESTRICT DUST CAUSED BY WORKS TO A MINIMUM. TAKE ALL PRACTICAL STEPS TO MINIMIZE NOISE RESULTING FROM WORKS.

STRUCTURE – SLABS & FALLS

- ALL SLAB SET DOWNS REFER TO SLAB SETOUT PLANS
- ALL OUTDOOR SLABS TO FALL AWAY FROM BUILDING
- ALL GRADES TO COMPLY WITH AS1428.1
- IN A BUILDING REQUIRED TO BE ACCESSIBLE BY PART D4, A DOORWAY THAT OPENS TO A ROAD OR OPEN SPACE, MUST BE PROVIDED WITH A THRESHOLD RAMP OR STEP RAMP IN ACCORDANCE WITH AS1428.1 IF A CHANGE IN LEVEL APPLIES.

TERMITE PROTECTION

- TERMITE PROTECTION SYSTEM TO BE PROVIDED TO ALL NEW BUILDING WORKS AND SERVICE PENETRATIONS IN ACCORDANCE WITH AS3600.
- SYSTEM TO BE INSTALLED BY A LICENSED AND MANUFACTURER APPROVED CONTRACTOR. THE CONTRACTOR WILL PROVIDE CERTIFICATION AS OUTLINED IN THE AUSTRALIAN STANDARD
- ALL TIMBERS USED ARE TO BE TREATED FOR SUBTERRANEAN TERMITE ATTACK TO A HAZARD LEVEL OF H2 OR BETTER FOR NON- EXPOSED CONDITIONS.
- A 10 YEAR WARRANTY SHALL BE PROVIDED ON THE INSTALLATION.

FIRE RATING & EMERGENCY EGRESS

- FIRE HAZARD PROPERTIES OF LININGS, MATERIALS AND ASSEMBLIES MUST COMPLY WITH SPECIFICATION 7 OF THE NCC.
- ALL SERVICES PASSING THROUGH FIRE RATED WALLS AND/OR FLOORS TO BE TREATED WITH FIRE RATED PRODUCTS SO AS TO MAINTAIN THE FRL OF THE WALL OR FLOOR SYSTEM.
- FIRE DOOR CONTRACTOR TO PROVIDE DOORS AND FRAMES THAT COMPLY WITH AS1905.1
- DOORS TO THE FIRE STAIRS TO BE PROVIDED WITH PUBLIC SAFETY HARDWARE SYSTEM, LOCATED BETWEEN 900-1100MM ABOVE FLOOR LEVEL.
- ALL CONSTRUCTION JOINTS BETWEEN FIRE RESISTING BUILDING ELEMENTS MUST BE FIRE STOPPED.
- PROVIDE FIRE EXTINGUISHERS AS DETERMINED BY FIRE SERVICES

BUILDING SERVICES

- EXIT SIGNS AND EMERGENCY LIGHTS TO COMPLY WITH AS2293. EXIT SIGNS TO BE MOUNTED AS DETAILED IN THE ELECTRICAL DRAWINGS OR AS OTHERWISE APPROVED BY THE RELEVANT BUILDING SURVEYOR.
- PORTABLE FIRE EXTINGUISHERS TO COMPLY WITH AS2444.
- ARTIFICIAL LIGHTING TO COMPLY WITH AS1680.
- MECHANICAL VENTILATION SYSTEM TO COMPLY WITH AS1668.2 AND AS3666.

WINDOWS & DOORS

- PROTECTION OF OPENABLE WINDOWS: ALL OPENABLE WINDOWS MUST BE PROVIDED WITH PROTECTION IN ACCORDANCE WITH CLAUSE D3D29 OF THE NCC. THE OPENABLE PORTION OF THE WINDOW MUST BE PROTECTED WITH EITHER A DEVICE TO RESTRICT THE OPENING OR A SCREEN WITH SECURE FITTINGS AND MUST NOT PERMIT A 125MM SPHERE TO PASS THROUGH, HAVE A CHILD RESISTANT RELEASE IF ABLE TO BE REMOVED OR OVERRIDDEN AND RESIST ANY OUTWARD PRESSURE OF 250N.
- DESIGN WIND PRESSURES: REFER TO STRUCTURAL DRAWINGS. THE PROJECT STRUCTURAL ENGINEER'S DOCUMENTATION INDICATES THE DESIGN CRITERIA FOR THE FACADE DESIGN. THE BUILDER IS TO CONFIRM ALL PRESSURES WITH THE PROJECT ENGINEER PRIOR TO ORDERING AND FABRICATION.
- DIMENSIONS ARE NOMINAL ONLY, ALL MEASUREMENTS SHOULD BE TAKEN FROM SITE PRIOR TO FABRICATION.
- IN THE EVENT OF A NOMINATED WINDOW/DOOR SIZE NOT BEING ABLE TO MEET THE DESIGN CRITERIA REQUIREMENTS OF THE LISTED AUSTRALIAN STANDARD CODES AND/OR THE NCC, THE BUILDER/MANUFACTURER ARE TO ADVISE VDG PRIOR TO PROCEEDING WITH PRICING OR FABRICATION.
- WINDOW MANUFACTURER TO DETERMINE LOCATION AND THICKNESS OF ALL SAFETY AND TOUGHENED GLASS TO THE REQUIREMENTS OF AS2047.
- ALL WINDOW & SLIDING DOOR FRAMES, GLAZING, FIXING & INSTALLATION TO BE CERTIFIED BY THE MANUFACTURER AS COMPLYING WITH;
- AS1288 – GLASS IN BUILDINGS – SELECTION AND INSTALLATION
- AS1170 PART 2 – WIND LOADS
- AS2047 – WINDOWS IN BUILDINGS – SELECTION & INSTALLATION
- ALL ALUMINIUM TO HAVE POWDERCOATED/ANODISED FINISH AS SCHEDULED. PRESSED METAL DOOR FRAMES TO HAVE SELECTED SEMI-GLOSS PAINT FINISH.
- PRESSED METAL DOOR FRAMES TO HAVE RECESSED HINGE ACCEPTOR PLATES.
- ALL DOORS REQUIRED TO BE ACCESSIBLE ARE REQUIRED TO HAVE A MINIMUM 850MM WIDE CLEAR OPENING AS PER AS1428
- ALL EXTERNAL WINDOWS ARE VIEWED FROM OUTSIDE AND ALL INTERNAL WINDOWS ARE VIEWED FROM OUTSIDE OF ROOM.
- ALL GLASS WITHIN 1000MM OF FFL SHALL BE GRADE 'A' SAFETY GLASS IN ACCORDANCE WITH AS1288.
- ALL GLASS DOORS, SIDELIGHTS OR ANY GLASS CAPABLE OF BEING MISTAKEN AS AN UNIMPEDED PATH OF TRAVEL MUST BE MARKED WITH A 75MM WIDE CONTRASTING BAND WITHIN 900-1000MM OF FFL IN ACCORDANCE WITH AS 1428.1
- ALL SHOWER SCREENS TO BE GRADE A SAFETY GLASS.
- GLAZING IN BATHROOMS GENERALLY BELOW 2000MM TO BE GRADE 'A' SAFETY GLASS.
- REFER TO FLOOR PLANS TO DETERMINE DIRECTION OF DOOR SWING AND HANDING OF DOORS.
- REFER MECHANICAL DRAWINGS FOR LOCATIONS AND SIZES OF DOOR GRILLES. ADVISE VDG OF ANY DISCREPANCIES PRIOR TO MANUFACTURE OR ORDERING.
- EXIT DOORS AND DOORS IN THE PATH OF TRAVEL TO AN EXIT ARE REQUIRED TO BE OPENABLE FROM WITHIN, WITHOUT A KEY, AND A HANDLE LEVER LOCATED BETWEEN 900-1100 ABOVE FLOOR LEVEL.
- ALL NON-FIRE RATED DOORS WITH ACOUSTIC SEALS TO HAVE FRAMES PACKED WITH 38KG/M3 ROCKWOOL.
- ALL EXTERNAL DOORS TO HAVE THRESHOLD SEALS AGAINST WEATHER AND VERMIN AND COMPLY WITH AS1428 FOR ACCESSIBILITY IN COMMON AREAS.
- PROVIDE AT LEAST 30% MIN LUMINANCE CONTRAST (BETWEEN DOOR LEAF & DOOR FRAME OR DOOR LEAF & ADJACENT WALL) AT ALL DOORWAYS WHERE ACCESSIBILITY IS REQUIRED IN ACCORDANCE WITH AS1428.1.
- ALL DOOR CONTROLS TO DOORWAYS REQUIRED TO BE ACCESSIBLE SHALL BE IN ACCORDANCE WITH FIG 35(A) OF AS1428.1
- AUTOMATIC DOORS TO COMPLY WITH CLAUSE D3D24 OF THE NCC.

ROOFING

- ALL FLASHINGS, CAPPINGS & GUTTERS TO BE COLORBOND FINISH
- REFER TO MECHANICAL & HYDRAULICS DRAWINGS FOR ROOF PENETRATIONS & EQUIPMENT LOCATIONS.
- MINIMUM FALL TO GUTTERS TO BE 1:100.
- ALL EXPOSED DUCTWORK TO BE PAINTED WHITE U.N.O
- PROVIDE FOLDED METAL CAP OVER JUNCTION OF BOX GUTTERS AT HIGH POINT.
- PROVIDE CONTINUOUS 12MM BMT METAL OVER-FLASHING FROM RIDGE OR CHANGE IN ROOF PITCH TO ROOF PENETRATION.
- SUPPLY AND INSTALL REMOVABLE LEAF GUARD OVER DOWNPIPES AS REQUIRED.
- SUPPLY AND INSTALL REMOVABLE GRATES OVER RAIN WATER HEADS AND SUMPS AS REQUIRED.
- TURN UP SHEET ENDS UNDER FLASHINGS & DOWN INTO GUTTERS.
- PROVIDE PROFILED FILLERS TO ENDS OF SHEETING, (BETWEEN SHEET & PURLIN AND SHEET & FLASHING).
- SCRIBE ALL FLASHINGS AND CAPPINGS ACCORDINGLY TO PROFILES. UPSTANDS TO BE MIN. 100MM(H). OVER FLASHINGS TO BE MIN. 200MM(W) AND COVER 2 ROOF PROFILES. VERTICAL LAPS TO BE MIN 100MM. HORIZONTAL LAPS TO BE MIN 150MM.
- INSTALL SOAKERS ON HIGH SIDE OF ALL ROOF PENETRATIONS UNDER ROOF SHEETING AND APRON FLASHINGS TO OTHER THREE SIDES.
- ALL EXTERNAL STEELWORK TO BE HOT DIPPED GALVANISED UNLESS OTHERWISE NOTED.
- PROVIDE BLANKET INSULATION ON WIRE MESH UNDER ROOF SHEETING TO COMPLY WITH THE REQUIREMENTS OF THE SECTION J REPORT. INSTALL TO ALL UNDER ROOFED AREAS, EXCEPT AWNINGS.
- ALL SERVICE LINES AND POST PENETRATIONS THROUGH ROOF TO HAVE DEKTITE FLASHINGS.
- OVERFLASHINGS AND SOAKER FLASHINGS ARE TO BE SAW CUT AND SEALED IN TO BLOCK WALLS & CONCRETE PANELS WHERE APPLICABLE.

ROOF ACCESS

WHERE REQUIRED INSTALL A PROPRIETARY ROOF ACCESS LANYARD SYSTEM TO ASSIST IN THE SAFE ACCESS AND MAINTENANCE OF THE WHOLE OF THE ROOFED AREAS OF THE BUILDING AT ROOF LEVEL.
THE SYSTEM IS TO COMPLY TO AS/NZS 1891.1/1891.2
SUPPLIER/INSTALLER TO PROVIDE PERMANENT LADDER BRACKET, SAFETY GATE, ROOF WALKWAY & APPROPRIATE ROOF MOUNTED HANDRAILS AS REQUIRED.
· PROPRIETARY ROOF ACCESS SYSTEM INDICATED ON PLAN IS DIAGRAMMATIC ONLY. SUPPLIER/INSTALLER TO DESIGN, INSTALL & CERTIFY SYSTEM.
· SUPPLIER/INSTALLER TO PROVIDE APPROPRIATE ROOF ACCESS SYSTEM AND SAFETY WARNING SIGNS (AS PER AS1657). SUPPLIER/INSTALLER TO CONFIRM COMPLIANCE OF ROOF SAFETY SYSTEM WITH RELEVANT STANDARDS PRIOR TO INSTALLATION

SLIP RESISTANCE

PAVEMENT & FLOOR FINISHES TO ACHIEVE SLIP RESISTANCE IN COMPLIANCE WITH PART D1 OF THE NCC & TABLE 3A + TABLE 3B WITHIN STANDARDS AUSTRALIA HANDBOOK 198:2014 (SA HB 198:2014).

RAMP, PATHWAY & STAIR SLIP RATINGS TO BE ACHIEVED:

- | | |
|------------------------|------------------|
| · RAMP UP TO 1:4 | · P4 SLIP RATING |
| · STEP RAMP UP TO 1:10 | · P5 SLIP RATING |
| · KERB RAMP UP TO 1:8 | · P5 SLIP RATING |
| · EXTERNAL ENTRY/ PATH | · P3 SLIP RATING |
| · EXTERNAL STAIRS | · P4 SLIP RATING |
| · INTERNAL STAIRS | · P3 SLIP RATING |

CEILINGS

- THE CONTRACTOR SHALL CARRY OUT A TRIAL SET-OUT OF ALL CEILING AND SOFFIT TYPES AND VERIFY WITH THE SUPERINTENDENT PRIOR TO CONSTRUCTION PROCEEDING.
- WHERE NO SET-OUT SHOWN ASSUME SET-OUT TO BE CENTRED BETWEEN WALLS.
- "EQUAL" RELATES ONLY TO OPPOSING DIMENSION IN THAT DIMENSION LINE.
- CHECK ALL DIMENSIONS ON SITE WITHIN ROOMS PRIOR TO INSTALLATION OF FITTINGS. NOTIFY SUPERINTENDENT OF ANY DISCREPANCIES PRIOR TO PROCEEDING.
- CEILING HEIGHTS SHOWN ARE TAKEN FROM THE TOP OF THE INTERNAL STRUCTURAL FLOOR LEVEL.
- FOR MECHANICAL AND ELECTRICAL EQUIPMENT TYPES AND MODELS, REFER TO ENGINEERS DRAWINGS.
- SET-OUT OF ALL ELECTRICAL AND MECHANICAL FIXTURES AND FITTINGS TO BE CONFIRMED ON SITE WITH THE PROJECT MANAGER PRIOR TO FRAMING, CUTTING ETC. OF THE CEILING LINING.

WATERPROOFING & TANKING

- INSTALL A PROPRIETARY MEMBRANE SYSTEM TO ALL BALCONIES AND WET AREAS, HAVING ONE OF THE FOLLOWING STATING THAT THE SYSTEM IS SUITABLE FOR THE INTENDED PURPOSE, AS FOLLOWS:
1. A CURRENT AUSTRALIAN BUILDING PRODUCT AND SYSTEMS CERTIFICATION SCHEME CERTIFICATE ISSUED BY ABCB (AUSTRALIAN BUILDING CODES BOARD).
2. A CURRENT APPRAISAL REPORT ISSUED BY CSIRO BUILDING PRODUCTS AND SYSTEMS APPRAISALS.
- PROVIDE WET AREA WATERPROOFING SYSTEMS WHICH COMPLY WITH AS3740, NCC PART F2 AND ARE GRADED TO FLOOR WASTES TO DISPOSE OF WATER WITHOUT PONDING AND PREVENT MOISTURE ENTERING THE SUBSTRATE OR ADJACENT AREAS.
- PROVIDE WATERPROOFING MEMBRANE TO ALL AREAS WITH A FLOOR WASTE AS PER THE CURRENT EDITIONS OF AUSTRALIAN STANDARDS AS3740 – 'WATERPROOFING OF DOMESTIC WET AREAS' AND AS4654 PARTS 1 & 2 – 'WATERPROOFING MEMBRANES FOR EXTERNAL ABOVE-GROUND USE' AND THE NCC.
- SUPPLY, INSTALL AND CERTIFY TANKING SYSTEM TO BASEMENT WALLS, SUBTERRANEAN WALLS, ALL BALCONIES AND PLANTERS STRICTLY IN ACCORDANCE WITH MANUFACTURERS RECOMMENDATIONS AND MUST COMPLY WITH AS4654 PARTS 1 & 2.
- BUILDER TO SELECT & PROVIDE DETAILS OF SYSTEM FOR CLIENT APPROVAL AND INSTALLATION CERTIFICATE ON COMPLETION.

FINISHES

- FINISHES SUCH AS CARPET, VINYL, LAMINATE ETC. TO COMPLY WITH SPECIFICATION 7 OF THE NCC.

ACCESSIBLE FACILITIES

- ACCESSIBLE AND AMBULANT FACILITIES TO COMPLY WITH AS1428. ALL DIMENSIONS SHOWN ARE CLEAR INTERNAL U.N.O., BUILDER TO ENSURE ALLOWANCES FOR ALL LININGS & FINISHES.
- FLOOR GRADIENTS IN ACCESSIBLE FACILITIES TO BE BETWEEN 1:60 & 1:80 FOR SHOWERS AND 1:80 FOR GENERAL AREAS.
- SET-OUT DIMENSIONS OF ALL FIXTURES & FITTINGS TO BE FROM FINISHED FLOOR AND WALL SURFACES AND MUST COMPLY WITH AS1428. ALLOW FOR THESE FINISHES WHEN SETTING OUT FROM BASE (UNFINISHED) WALLS & FLOORS.
- ACCESSIBLE FACILITIES SHALL BE IDENTIFIED WITH BRAILLE & TACTILE SIGNAGE COMPLYING WITH NCC D4D7. ENSURE INTERNATIONAL SYMBOLS FOR ACCESS COMPLYING WITH AS1428.1 ARE PROVIDED ON THE LATCH SIDE OF DOORS & MOUNTED BETWEEN 1250-1350MM AFFL.
- SWITCH & POWER POINTS IN ACCESSIBLE FACILITIES TO BE MOUNTED 1000 AFFL AND NOT LESS THAN 500MM FROM INTERNAL CORNERS.
- DOORS TO ACCESSIBLE FACILITIES TO HAVE AN 'IN-USE' INDICATOR.
- DOORS TO ACCESSIBLE FACILITIES TO BE REMOVABLE FROM OUTSIDE.
- PROVIDE AT LEAST 30% MIN LUMINANCE CONTRAST (BETWEEN DOOR LEAF & DOOR FRAME OR DOOR LEAF & ADJACENT WALL) AT ALL DOORWAYS WHERE ACCESSIBILITY IS REQUIRED IN ACCORDANCE WITH AS1428.1.

STAIRS & RAMPS

- HANDRAILS AND BALUSTRADING THROUGHOUT TO BE IN ACCORDANCE WITH NCC PART D3D22 AND AS1428.1
- CONTINUOUS HANDRAILS REQUIRED TO BOTH SIDES OF ALL INTERNAL STAIRS FOR PUBLIC ACCESS TO COMPLY WITH NCC PART D3D22, LOCATED ALONG THE FULL LENGTH, WITH A MINIMUM 865MM HEIGHT AND MAXIMUM HEIGHT OF 1M ABOVE STAIR NOSING AND HAVE NO OBSTRUCTION ON OR ABOVE THEM THAT WILL BREAK A HAND HOLD. 300MM EXTENSION TO HANDRAILS AT TOP LANDING, & 300MM + 1 TREAD WIDTH EXTENSION TO HANDRAIL AT BOTTOM LANDING
- TGSIS AND STAIR NOSINGS TO BE PROVIDED TO ALL STAIRS AND RAMPS IN ACCORDANCE WITH AS1428.4
- ALL STAIRWAYS, RAMPS AND OVERHEAD OBSTRUCTIONS LESS THAN 2000MM IN HEIGHT MUST BE PROVIDED WITH TACTILE INDICATORS IN ACCORDANCE WITH AS1428 OR OTHER SUITABLE BARRIER.

COOL ROOM & FREEZER ROOM


COOL ROOMS & FREEZER ROOMS TO COMPLY WITH NCC CLAUSE G1D3. A COOL ROOM WHICH IS OF SUFFICIENT SIZE FOR A PERSON TO ENTER MUST HAVE:

- A DOOR WHICH IS CAPABLE OF BEING OPENED BY HAND FROM INSIDE WITHOUT A KEY.
- INTERNAL LIGHTING CONTROLLED ONLY BY A SWITCH WHICH IS LOCATED ADJACENT TO THE ENTRANCE DOORWAY.
- INDICATOR LAMP POSITIONED OUTSIDE THE COOLROOM ILLUMINATED WHEN THE INTERIOR LIGHTS.
- AN EXTERNAL ALARM WHICH IS OPERATED INTERNALLY THAT ACHIEVES A SOUND PRESSURE LEVEL OF 90dB(A) WHEN MEASURED AT 3M.
- PORTABLE FIRE EXTINGUISHERS TO COMPLY WITH AS2444
- ALL COOLROOM AND FREEZER INTERNAL FLOOR TO CEILING HEIGHTS TO BE 2.7M UNLESS OTHERWISE SPECIFIED ON RCP AND RELEVANT SECTIONS / ELEVATIONS.
- BLOWER UNITS TO BE PLACED DIRECTLY ABOVE THE DOORS TO MAXIMISE SHELVING HEIGHTS ALONG ALL PERIMETER WALLS.

FITOUT LOOSE ITEMS

- ANY SHELVING, BOOKCASES OR THE LIKE INSTALLED BY THE END USER SHALL BE SECURED TO COMPLY WITH AS1170.4 SECTION 8.

VERVE SCHEDULES DISCLAIMER: 1. ALL SCHEDULES SHOULD BE CHECKED WITH THE REMAINDER OF THE DRAWING SET. 2. SCHEDULED RATES AND AREAS ARE INTENDED FOR ASSISTANCE ONLY. NO RESPONSIBILITY IS TAKEN FOR THE ACCURACY OF QUANTITIES. 3. ANY DISCREPANCIES IN SCHEDULES SHOULD BE IDENTIFIED TO THE AUTHOR NOTED. 4. ALL AREAS ARE GROSS AREAS, UNLESS NOTED OTHERWISE		CONSULTING ENGINEER	 imagine create deliver commercial mixed-use self storage industrial service stations quick service restaurants child care centres large format retail © 2011 copyright, all rights reserved. This drawing is the © copyright & property of VERVE DESIGN GROUP and must not be used or duplicated without authorisation. Do not scale this drawing. Check all dimensions on site prior commencement of works	<table><tr><th colspan="5">Revision and approvals</th></tr><tr><th>Rev</th><th>Date</th><th>Drn</th><th>Description</th><th>Appr</th></tr><tr><td>P1</td><td>12.02.2026</td><td>PC</td><td>PRELIMINARY ISSUE</td><td>SS</td></tr><tr><td>A</td><td>19.06.2026</td><td>PC</td><td>BA ISSUE</td><td>SS</td></tr><tr><td> </td><td> </td><td> </td><td> </td><td> </td></tr><tr><td> </td><td> </td><td> </td><td> </td><td> </td></tr><tr><td> </td><td> </td><td> </td><td> </td><td> </td></tr><tr><td> </td><td> </td><td> </td><td> </td><td> </td></tr></table>	Revision and approvals					Rev	Date	Drn	Description	Appr	P1	12.02.2026	PC	PRELIMINARY ISSUE	SS	A	19.06.2026	PC	BA ISSUE	SS																					<table><tr><td colspan="2">Project Description</td><td colspan="2">Drawing Title</td></tr><tr><td colspan="2">PROPOSED SERVICE STATION</td><td colspan="2">NOTES</td></tr><tr><td colspan="2">22 ENTERPRISE CCT., MARYBOROUGH W.</td><td colspan="2"></td></tr><tr><td>Scale @A1 1 : 100</td><td>Date FEBRUARY 2026</td><td>Job Number - Drawing Number</td><td>Revision</td></tr><tr><td>Drawn PC</td><td>Approved By SS</td><td>26024 A001</td><td>A</td></tr></table>	Project Description		Drawing Title		PROPOSED SERVICE STATION		NOTES		22 ENTERPRISE CCT., MARYBOROUGH W.				Scale @A1 1 : 100	Date FEBRUARY 2026	Job Number - Drawing Number	Revision	Drawn PC	Approved By SS	26024 A001	A
Revision and approvals	
Rev	Date	Drn	Description	Appr	
P1	12.02.2026	PC	PRELIMINARY ISSUE	SS	
A	19.06.2026	PC	BA ISSUE	SS	
Project Description		Drawing Title	
PROPOSED SERVICE STATION		NOTES	
22 ENTERPRISE CCT., MARYBOROUGH W.	
Scale @A1 1 : 100	Date FEBRUARY 2026	Job Number - Drawing Number	Revision	
Drawn PC	Approved By SS	26024 A001	A	

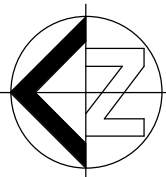


REAL PROPERTY DESCRIPTION

RPD: LOT 53 ON SP200102
PARISH: MARYBOROUGH
COUNTY: MARCH
LOCAL AUTHORITY: FRASER COAST REGIONAL COUNCIL

GENERAL NOTES

1. THESE DRAWINGS SHALL BE READ IN CONJUNCTION WITH ALL OTHER CONSULTANTS DRAWINGS AND SPECIFICATIONS.
2. DO NOT SCALE DRAWINGS - FIGURED DIMENSIONS ARE TO TAKE PRECEDENCE AT ALL TIMES.
3. ALL DIMENSIONS TO BE CONFIRMED ON SITE AND/OR VERIFIED PRIOR TO CONSTRUCTION OR FABRICATION.
4. ALL MATERIALS AND WORKMANSHIP SHALL BE IN ACCORDANCE WITH CURRENT AND RELEVANT SAA CODES, NCC OF AUSTRALIA, THE BUILDING ACT, AND LOCAL AUTHORITIES BY-LAWS.
5. ALL EXTERNALLY GLAZED WINDOWS AND DOORS TO BE DESIGNED AND CERTIFIED BY THE MANUFACTURER INCLUDING FIXINGS, AND SHALL COMPLY WITH AS1288 & AS1170.2.
6. ALL STAIRS, RAMPS, HANDRAILS AND BALUSTRADES ARE TO COMPLY WITH NCC OF AUSTRALIA, SECTION D & AS1428.1.
7. THE CONTRACTOR SHALL BE RESPONSIBLE FOR THE STRUCTURE DURING ERECTION AND PROVIDE ADEQUATE PROPPING AND SUPPORT
8. ALL INTERNAL NON-LOADBEARING WALLS, CEILINGS AND OTHER RELEVANT STRUCTURAL COMPONENTS SHALL BE DESIGNED & INSTALLED TO COMPLY WITH SECTION 2 OF AS1170.4 AS REQUIRED.

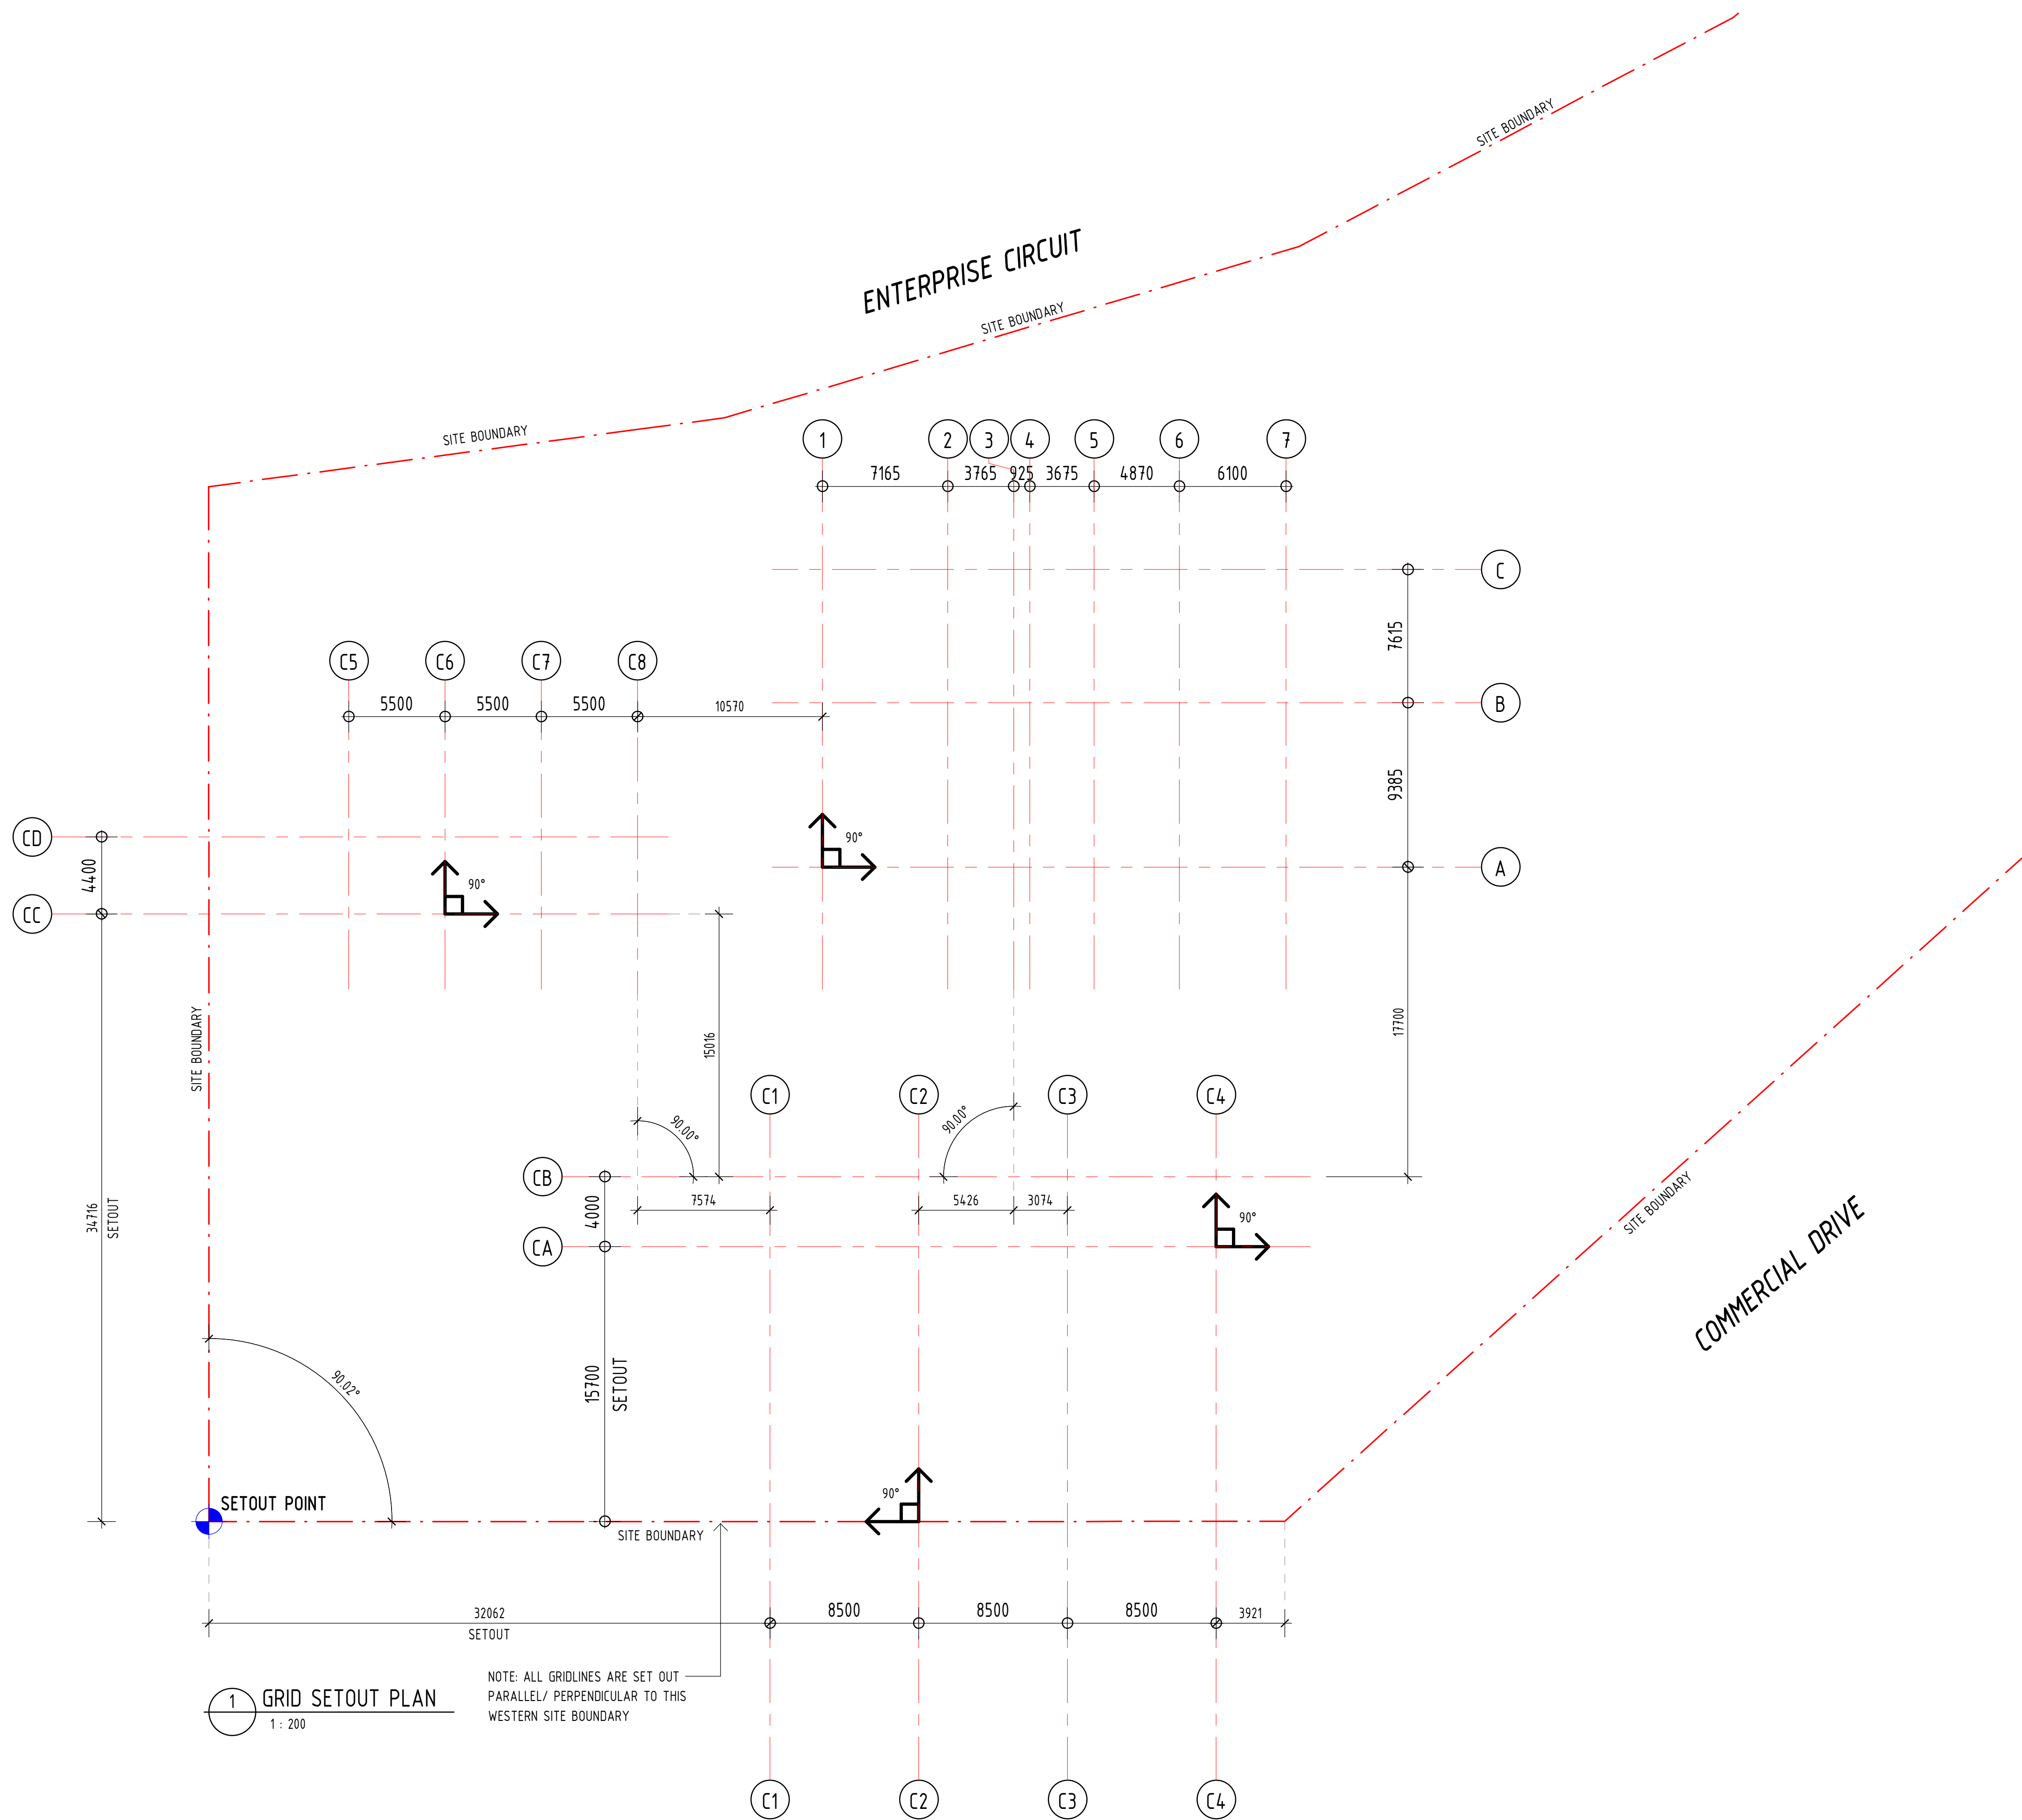

VERVE SCHEDULES DISCLAIMER:

1. ALL SCHEDULES SHOULD BE CHECKED WITH THE REMAINDER OF THE DRAWING SET.
2. SCHEDULED RATES AND AREAS ARE INTENDED FOR ASSISTANCE ONLY. NO RESPONSIBILITY IS TAKEN FOR THE ACCURACY OF QUANTITIES.
3. ANY DISCREPANCIES IN SCHEDULES SHOULD BE IDENTIFIED TO THE AUTHOR NOTED.
4. ALL AREAS ARE GROSS AREAS, UNLESS NOTED OTHERWISE

CONSULTING ENGINEER




- ☐ commercial
- ☐ mixed-use
- ☐ self storage
- ☐ industrial
- ☐ service stations
- ☐ quick service restaurants
- ☐ child care centres
- ☐ large format retail

© 2011 copyright, all rights reserved.
This drawing is the © copyright & property of VERVE DESIGN GROUP and must not be used or duplicated without authorisation.
Do not scale this drawing.
Check all dimensions on site prior commencement of works

Revision and approvals				
Rev	Date	Drn	Description	Appr
P1	12.02.2026	PC	PRELIMINARY ISSUE	SS
P2	09.03.2026	PC	REVISED PRELIMINARY ISSUE	SS
P3	01.05.2026	PC	REVISED PRELIMINARY ISSUE	SS
A	19.06.2026	PC	BA ISSUE	SS

Project Description	
PROPOSED SERVICE STATION	
22 ENTERPRISE CCT., MARYBOROUGH W.	
Scale @A1 As indicated	Date FEBRUARY 2026
Drawn PC	Approved By SS

Drawing Title	
GRID SETOUT PLAN	
Job Number - Drawing Number	Revision
26024 A050	A

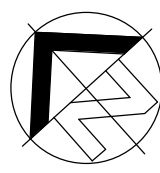


REAL PROPERTY DESCRIPTION

RPD: LOT 53 ON SP200102
PARISH: MARYBOROUGH
COUNTY: MARCH
LOCAL AUTHORITY: FRASER COAST REGIONAL COUNCIL

LEGEND

ADB	AD BLUE DISPENSER - REFER FUEL ENG. DETAILS
ARB	ARMCO VEHICLE BARRIER - REFER TO CIVIL ENG. FOR DETAILS
BOL-1	STEEL BOLLARD TYPE 1 - REFER DETAIL
EMHB	EMERGENCY MANIFEST/ HAZMAT BOX
EP	ELECTRICAL PIT - REFER ELEC. ENG. DETAILS
FEC	FUELS ELECTRICAL CONDUIT PIT
FFB	FUEL FILL BOX - REFER FUEL ENG. DETAILS
FVP	FUEL/SPEL VENT PIPES - REFER FUEL ENG. DETAILS
GA	GREASE ARRESTOR - REFER HYD. ENG. DETAILS
K	NEW CONCRETE KERB - REFER CIVIL ENG. DETAILS
KR	KERB RAMP TO COMPLY WITH AS1428.1
KY	NEW CONCRETE KERB PAINT FINISH SAFETY YELLOW - REFER CIVIL ENG. DETAILS
LM1	LINEMARKING - WHITE - REFER CIVIL ENG. DETAILS
LM2	LINEMARKING - SAFETY YELLOW - REFER CIVIL ENG. DETAILS
LS	LANDSCAPING - REFER LANDS. ARCH. DETAILS
MSB	ELECTRICAL MAIN SWITCHBOARD - REFER ELEC. ENG. DETAILS
PL	LIGHT POST - REFER ELECTRICAL ENG. DETAILS
SFFB	SECOND FUEL FILL BOX - REFER FUEL ENG. DETAILS
SGN-1	ILLUMINATED 10m SITE PYLON TO FUEL RETAILERS STANDARDS SUPPLIED & INSTALLED BY LESSEE CONTRACTOR. BUILDER TO PROVIDE FOOTING, POWER, & DATA SERVICES
SWG	STORMWATER GULLY - REFER CIVIL ENG. DETAILS
UFST	APPROXIMATE LOCATION FOR UNDERGROUND FUEL STORAGE TANK - REFER FUEL ENG. DETAILS
VP	VENT PIPE - REFER HYD. ENG. DETAILS
WS	CONCRETE WHEEL STOP. PAINT FINISH SAFETY YELLOW
WSM	WATER SUPPLY METER - REFER HYD. ENG. DETAILS

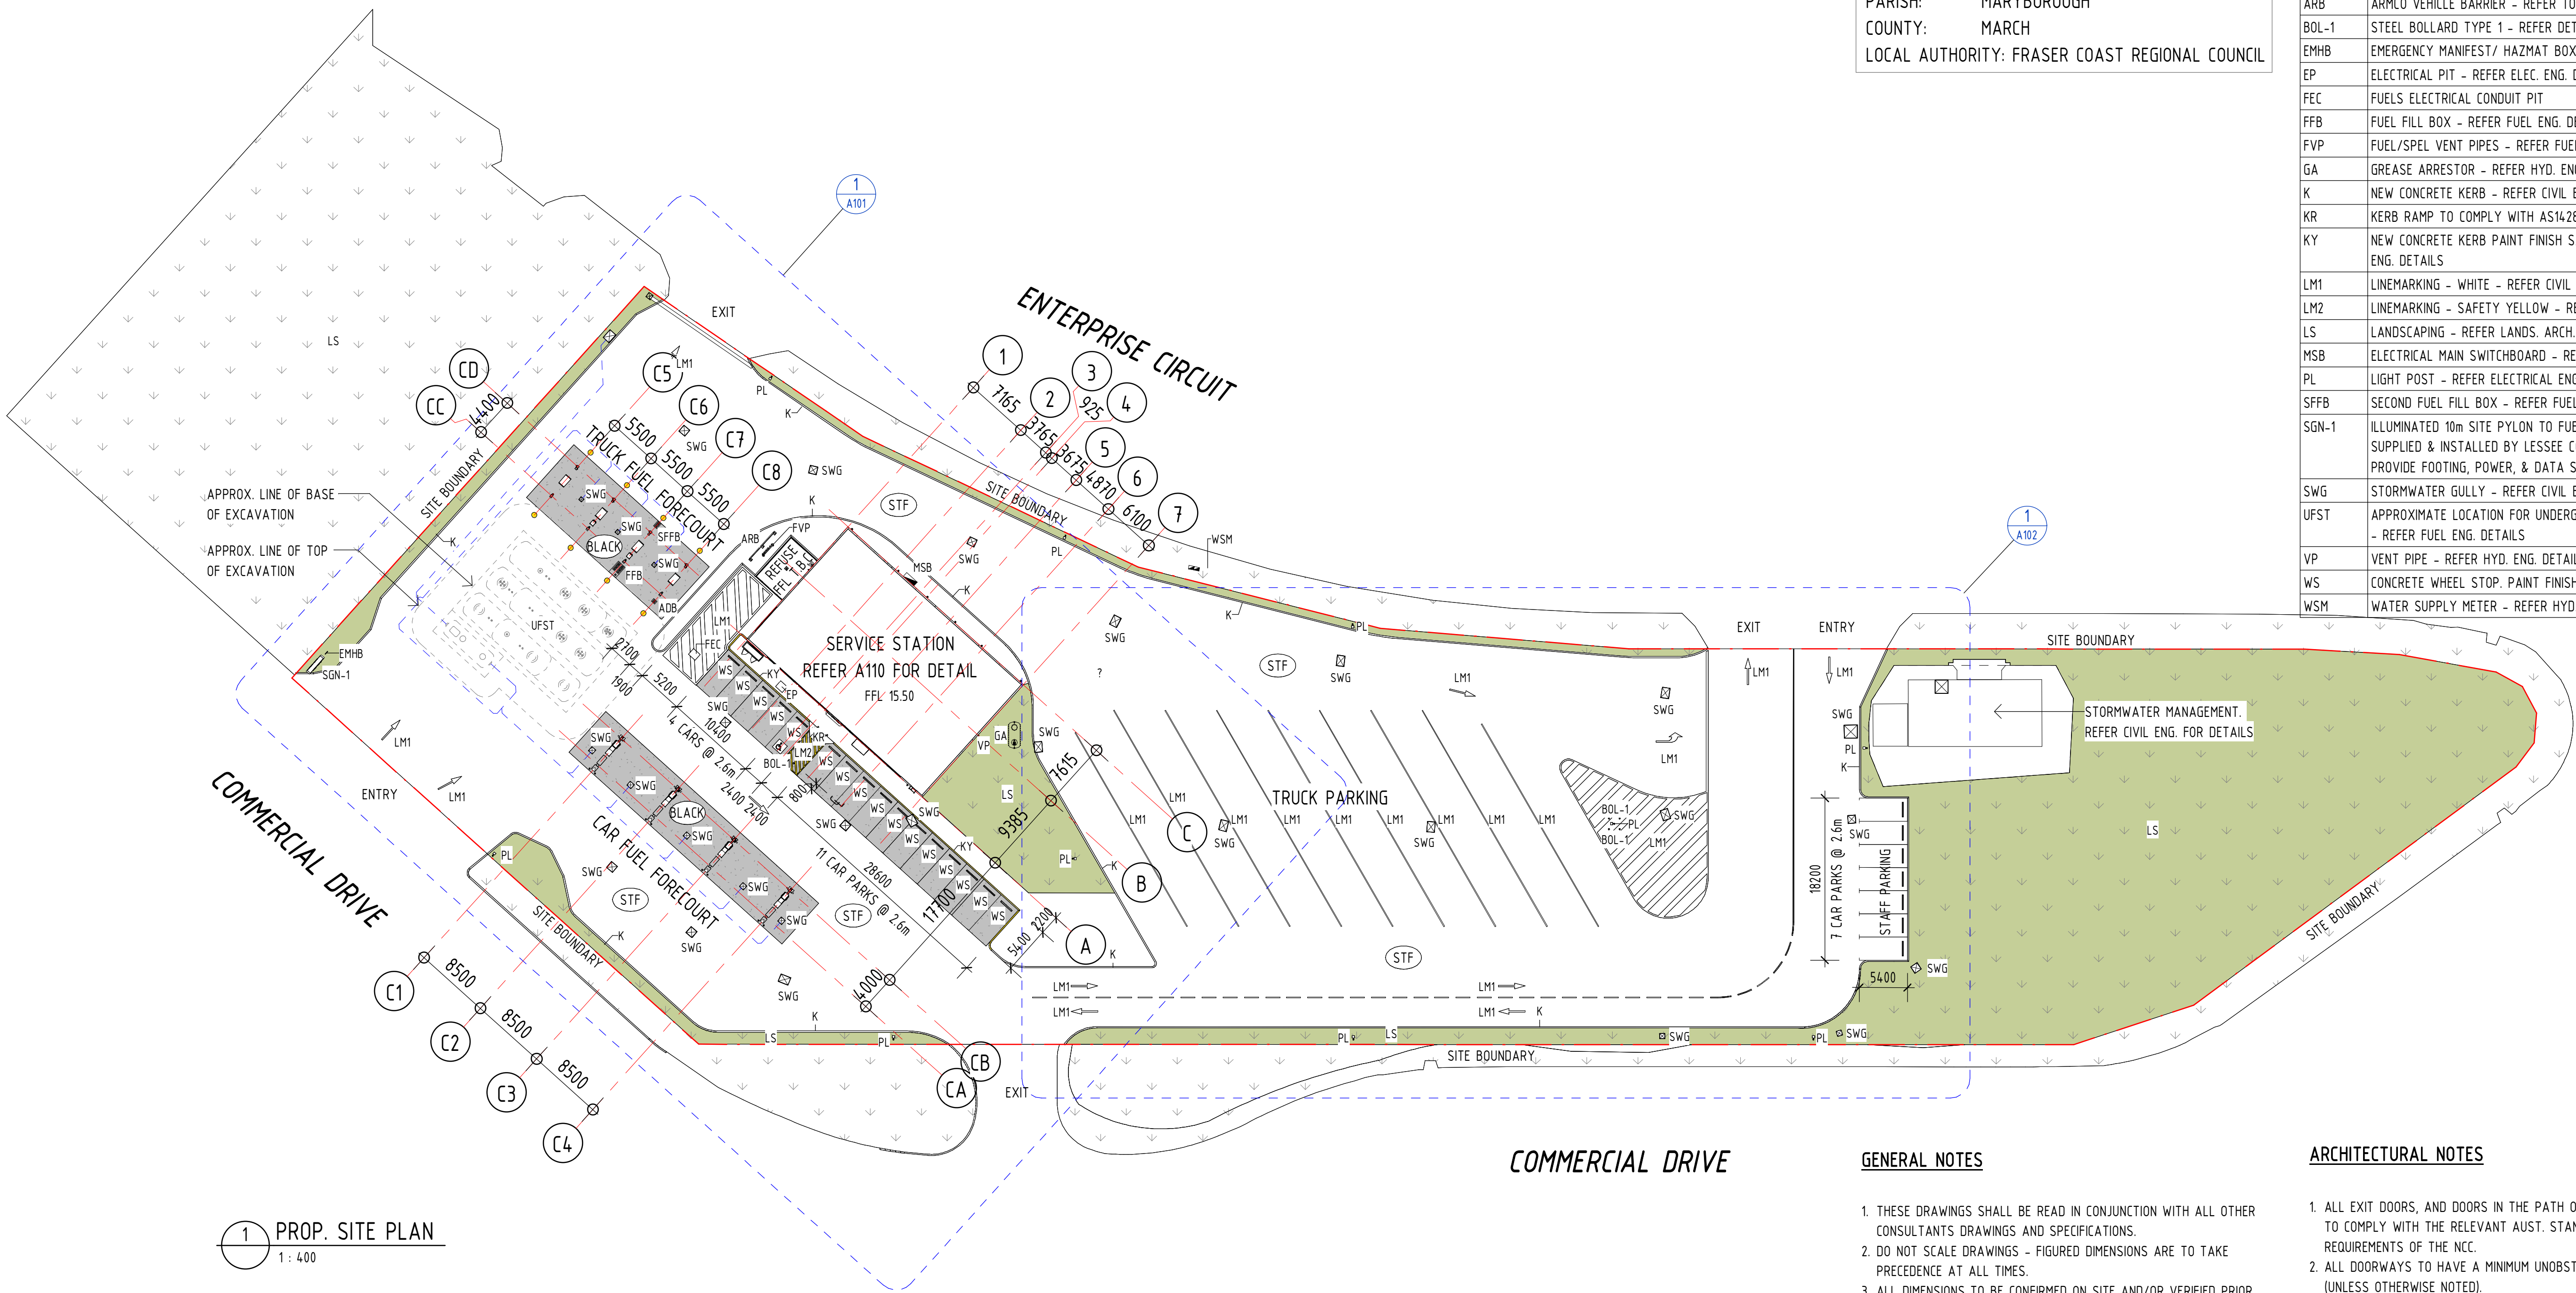

COMMERCIAL DRIVE

GENERAL NOTES

- THESE DRAWINGS SHALL BE READ IN CONJUNCTION WITH ALL OTHER CONSULTANTS DRAWINGS AND SPECIFICATIONS.
- DO NOT SCALE DRAWINGS - FIGURED DIMENSIONS ARE TO TAKE PRECEDENCE AT ALL TIMES.
- ALL DIMENSIONS TO BE CONFIRMED ON SITE AND/OR VERIFIED PRIOR TO CONSTRUCTION OR FABRICATION.
- ALL MATERIALS AND WORKMANSHIP SHALL BE IN ACCORDANCE WITH CURRENT AND RELEVANT SAA CODES, NCC OF AUSTRALIA, THE BUILDING ACT, AND LOCAL AUTHORITIES BY-LAWS.
- ALL EXTERNALLY GLAZED WINDOWS AND DOORS TO BE DESIGNED AND CERTIFIED BY THE MANUFACTURER INCLUDING FIXINGS, AND SHALL COMPLY WITH AS1288 & AS1170.2.
- ALL STAIRS, RAMPS, HANDRAILS AND BALUSTRADES ARE TO COMPLY WITH NCC OF AUSTRALIA, SECTION D & AS1428.1.
- THE CONTRACTOR SHALL BE RESPONSIBLE FOR THE STRUCTURE DURING ERECTION AND PROVIDE ADEQUATE PROPPING AND SUPPORT.
- ALL INTERNAL NON-LOADBEARING WALLS, CEILINGS AND OTHER RELEVANT STRUCTURAL COMPONENTS SHALL BE DESIGNED & INSTALLED TO COMPLY WITH SECTION 2 OF AS1170.4 AS REQUIRED.

ARCHITECTURAL NOTES

- ALL EXIT DOORS, AND DOORS IN THE PATH OF TRAVEL TO EXITS ARE TO COMPLY WITH THE RELEVANT AUST. STANDARDS AND THE REQUIREMENTS OF THE NCC.
- ALL DOORWAYS TO HAVE A MINIMUM UNOBSTRUCTED HEIGHT OF 2.0m (UNLESS OTHERWISE NOTED).
- EXIT SIGNS AND EMERGENCY LIGHTS TO COMPLY WITH AS 2293. EXIT SIGNS TO BE MOUNTED AS DETAILED IN THE ELECTRICAL DRAWINGS OR AS OTHERWISE APPROVED BY THE RELEVANT BUILDING SURVEYOR.
- PORTABLE FIRE EXTINGUISHERS TO COMPLY WITH AS 2444.
- ARTIFICIAL LIGHTING TO COMPLY WITH AS 1680.
- MECHANICAL VENTILATION SYSTEM TO COMPLY WITH AS 1668.2 AND AS 3666.
- ALL WET AREAS TO COMPLY WITH NCC PART F1.7 & ALL RELEVANT PARTS OF AS 3740.
- ALL WET AREAS TO HAVE BOTTOM PLATE FULLY WRAPPED WITH DAMP PROOF MEMBRANE. CONTINUE UP WALL FRAME MIN. 75mm AFFL.
- ALL TOILET AND AIRLOCK WALLS TO BE 45 STC SOUND RATED.
- ALL TIMBERS USED ARE TO BE TREATED FOR SUBTERRANEAN TERMITE ATTACK TO A HAZARD LEVEL OF H2 OR BETTER FOR NON-EXPOSED CONDITIONS.

NOTES:

- BUILDER TO ALLOW FOR ALL FOOTINGS & ELECTRICAL/DATA CONNECTIONS TO SITE SIGNAGE. REFER STRUCT. & ELEC. ENGINEER DRAWINGS FOR DETAIL.
- BUILDER TO COORDINATE WITH SITE SIGNAGE PLAN (DA APPROVED PLANS).
- REFER TO CIVIL ENG. DRAWINGS FOR EXTERNAL LEVELS, FALLS, RETAINING WALLS & LOCATING CIVIL SERVICES.
- BLACK CONCRETE HAND STIPPLE (ROUGH NON-SLIP) FINISH COLOUR: CCS BLACK OXIDE 8% DOSAGE RATE (4% DOSAGE RATE FOR FOOTPATH AND KERBS) SEALANT: NUTECH - PETROL RESISTANT PAVECOAT - PR210 BLACK COLOURED WITH NUTECH ANTI-SLIP ADDITIVE APPLIED AS PER MANUFACTURER'S INSTRUCTIONS.

LEGEND

- BFC BROOM FINISH NATURAL GREY CONCRETE
STF STEEL TROWEL FINISH NATURAL GREY CONCRETE
BLACK BLACK CONCRETE HAND STIPPLE FINISH (NON-SLIP)
COLOUR: CCS BLACK OXIDE 8% DOSAGE RATE
SEALANT: NUTECH - PETROL RESISTANT PAVECOAT - PR210 BLACK COLOURED WITH NUTECH ANTI-SLIP ADDITIVE APPLIED AS PER MANUFACTURER'S INSTRUCTIONS.

VERVE SCHEDULES DISCLAIMER:
1. ALL SCHEDULES SHOULD BE CHECKED WITH THE REMAINDER OF THE DRAWING SET.
2. SCHEDULED RATES AND AREAS ARE INTENDED FOR ASSISTANCE ONLY. NO RESPONSIBILITY IS TAKEN FOR THE ACCURACY OF QUANTITIES.
3. ANY DISCREPANCIES IN SCHEDULES SHOULD BE IDENTIFIED TO THE AUTHOR NOTED.
4. ALL AREAS ARE GROSS AREAS, UNLESS NOTED OTHERWISE

CONSULTING ENGINEER



- ☐ commercial ☐ service stations
☐ mixed-use ☐ quick service restaurants
☐ self storage ☐ child care centres
☐ industrial ☐ large format retail

© 2011 copyright, all rights reserved.
This drawing is the © copyright & property of VERVE DESIGN GROUP and must not be used or duplicated without authorisation.
Do not scale this drawing.
Check all dimensions on site prior commencement of works

Revision and approvals				
Rev	Date	Drn	Description	Appr
P1	12.02.2026	PC	PRELIMINARY ISSUE	SS
P2	09.03.2026	PC	REVISED PRELIMINARY ISSUE	SS
P3	01.05.2026	PC	REVISED PRELIMINARY ISSUE	SS
P4	12.06.2026	PC	REVISED PRELIMINARY ISSUE	SS
A	19.06.2026	PC	BA ISSUE	SS

Project Description	
PROPOSED SERVICE STATION	
22 ENTERPRISE CCT., MARYBOROUGH W.	
Scale @A1 As indicated	Date FEBRUARY 2026
Drawn PC	Approved By SS


Drawing Title	
PROP. OVERALL SITE PLAN	
Job Number - Drawing Number 26024 A100	Revision A

REAL PROPERTY DESCRIPTION

RPD: LOT 53 ON SP200102
PARISH: MARYBOROUGH
COUNTY: MARCH
LOCAL AUTHORITY: FRASER COAST REGIONAL COUNCIL

LEGEND

ADB	AD BLUE DISPENSER - REFER FUEL ENG. DETAILS
ARB	ARMCO VEHICLE BARRIER - REFER TO CIVIL ENG. FOR DETAILS
BOL-1	STEEL BOLLARD TYPE 1 - REFER DETAIL
EMHB	EMERGENCY MANIFEST/ HAZMAT BOX
EP	ELECTRICAL PIT - REFER ELEC. ENG. DETAILS
FEC	FUELS ELECTRICAL CONDUIT PIT
FFB	FUEL FILL BOX - REFER FUEL ENG. DETAILS
FVP	FUEL/SPEL VENT PIPES - REFER FUEL ENG. DETAILS
GA	GREASE ARRESTOR - REFER HYD. ENG. DETAILS
K	NEW CONCRETE KERB - REFER CIVIL ENG. DETAILS
KR	KERB RAMP TO COMPLY WITH AS1428.1
KY	NEW CONCRETE KERB PAINT FINISH SAFETY YELLOW - REFER CIVIL ENG. DETAILS
LM1	LINEMARKING - WHITE - REFER CIVIL ENG. DETAILS
LM2	LINEMARKING - SAFETY YELLOW - REFER CIVIL ENG. DETAILS
LS	LANDSCAPING - REFER LANDS. ARCH. DETAILS
MSB	ELECTRICAL MAIN SWITCHBOARD - REFER ELEC. ENG. DETAILS
PL	LIGHT POST - REFER ELECTRICAL ENG. DETAILS
SGN-1	ILLUMINATED 10m SITE PYLON TO FUEL RETAILERS STANDARDS SUPPLIED & INSTALLED BY LESSEE CONTRACTOR. BUILDER TO PROVIDE FOOTING, POWER, & DATA SERVICES
SWG	STORMWATER GULLY - REFER CIVIL ENG. DETAILS
UFST	APPROXIMATE LOCATION FOR UNDERGROUND FUEL STORAGE TANK - REFER FUEL ENG. DETAILS
WS	CONCRETE WHEEL STOP. PAINT FINISH SAFETY YELLOW

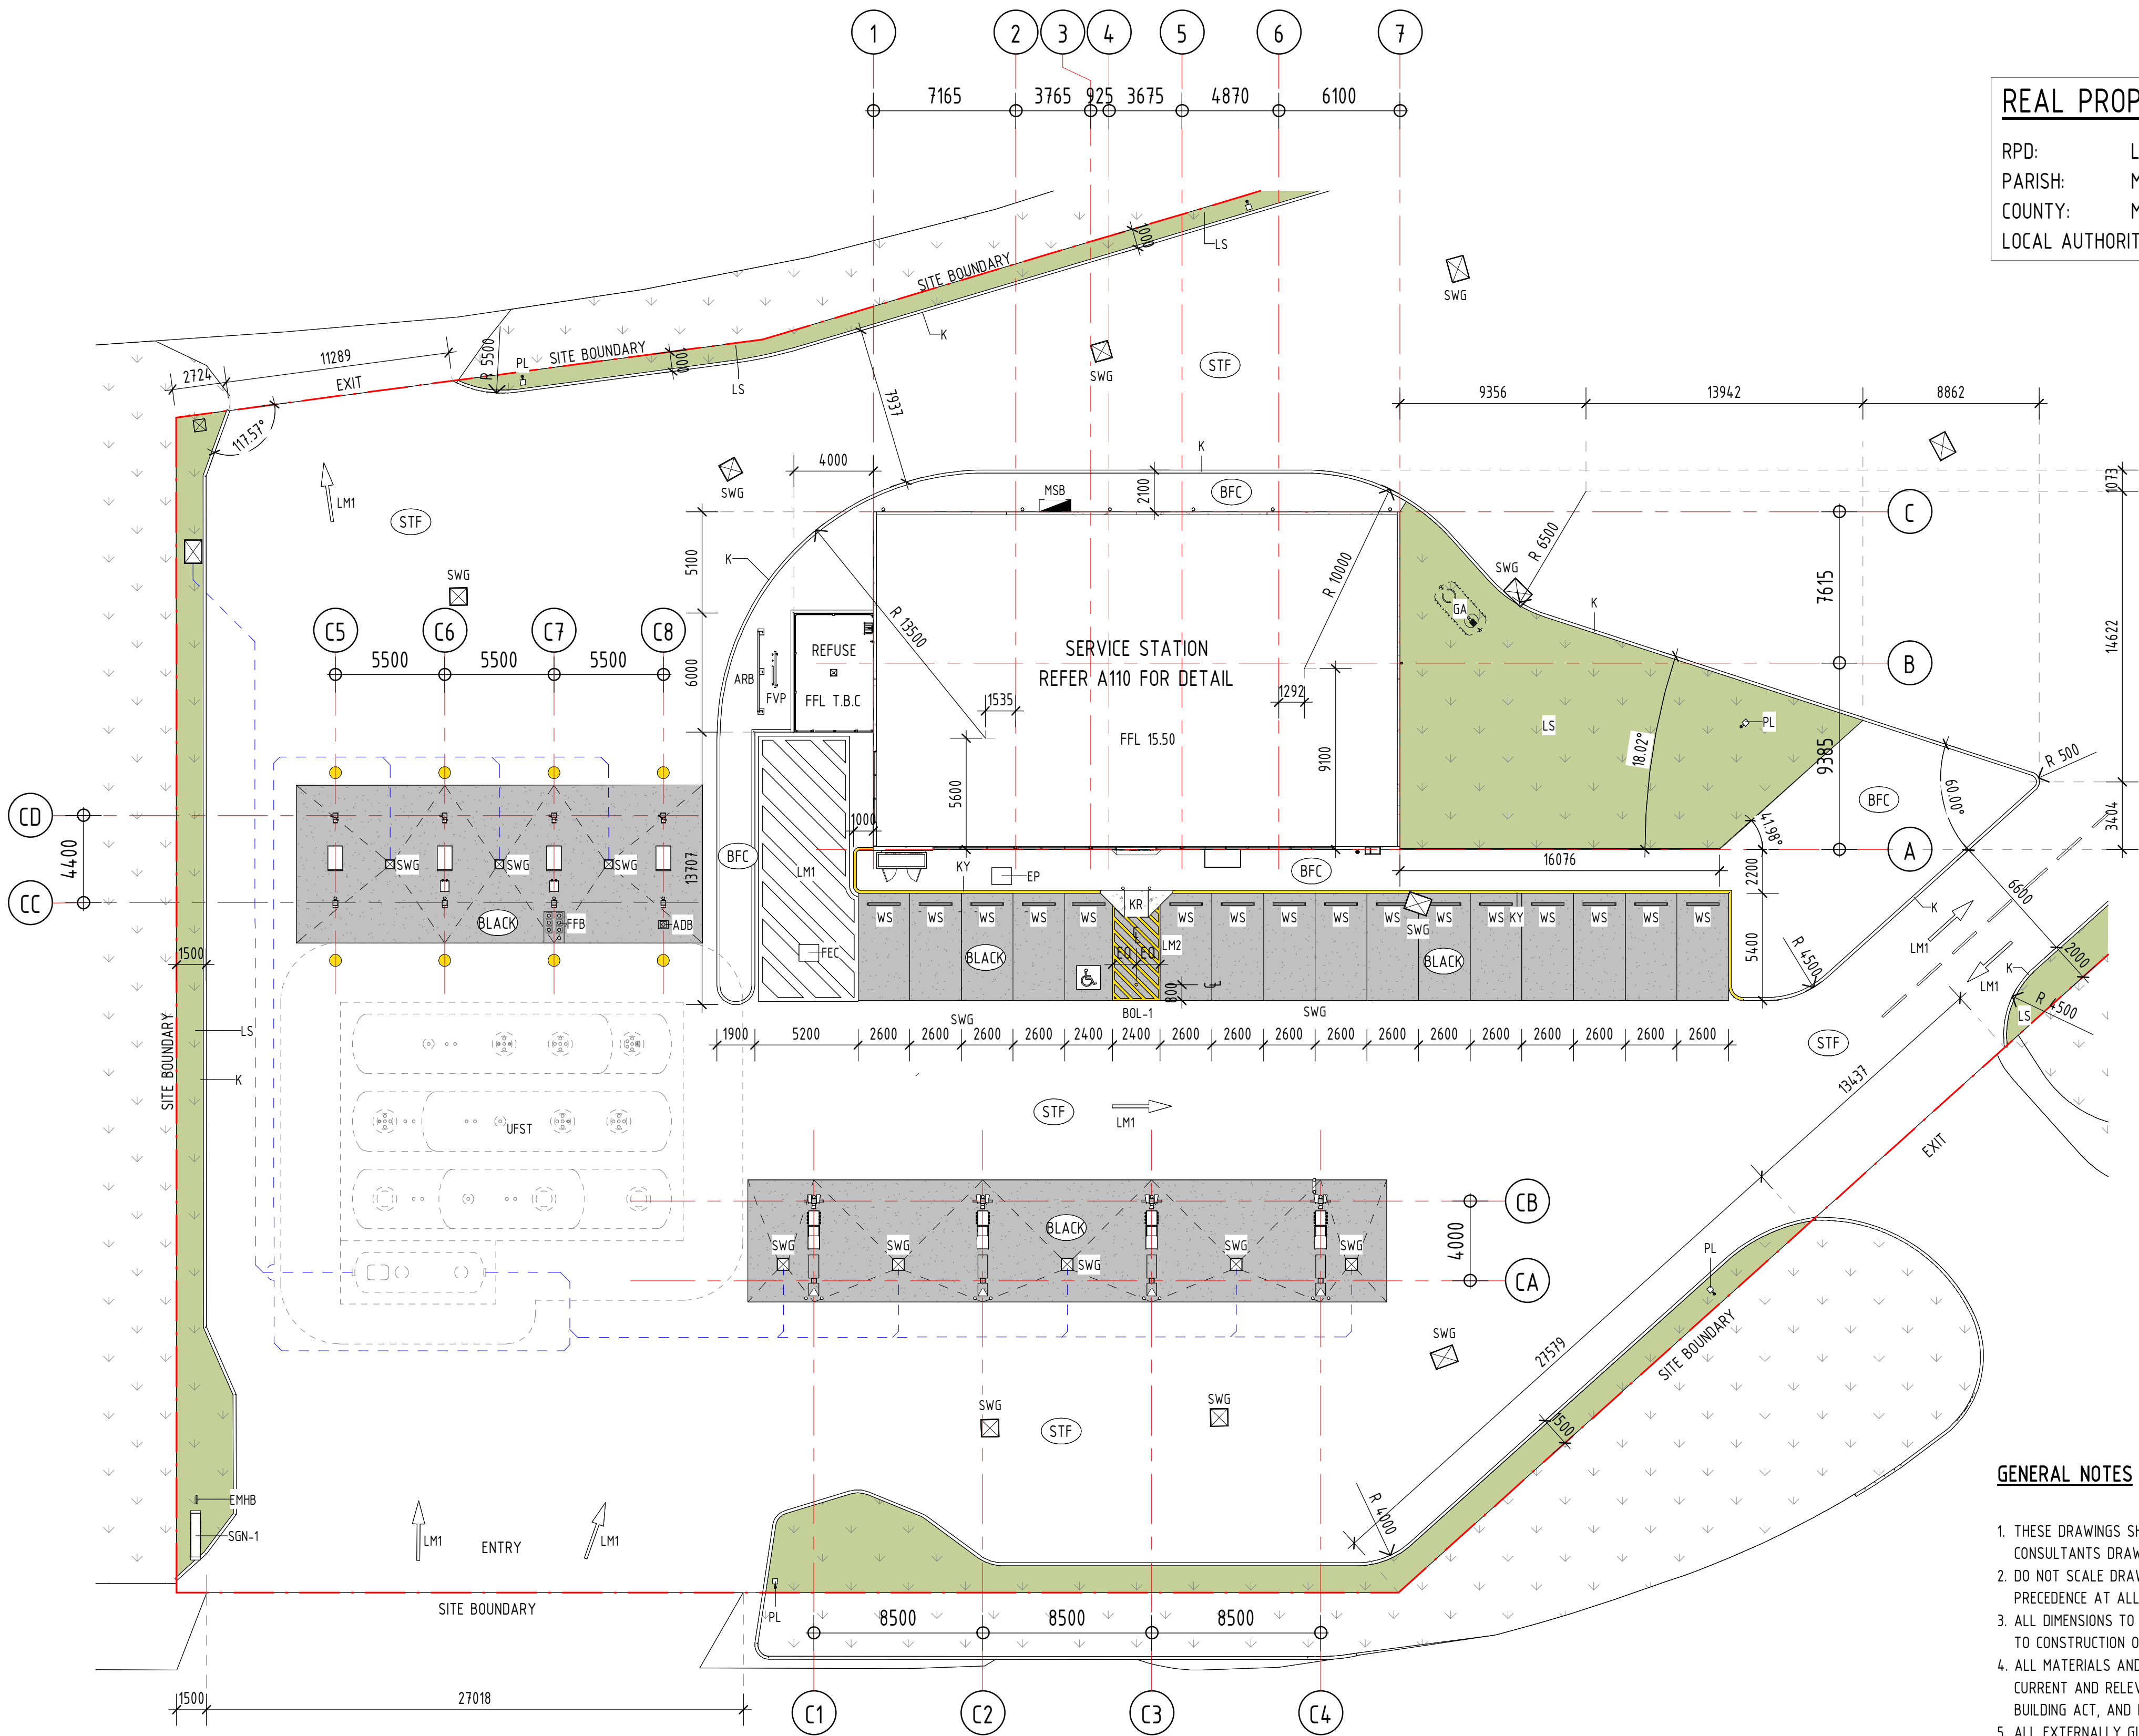

NOTES:

- BUILDER TO ALLOW FOR ALL FOOTINGS & ELECTRICAL/DATA CONNECTIONS TO SITE SIGNAGE. REFER STRUCT. & ELEC. ENGINEER DRAWINGS FOR DETAIL.
- BUILDER TO COORDINATE WITH SITE SIGNAGE PLAN (DA APPROVED PLANS).
- REFER TO CIVIL ENG. DRAWINGS FOR EXTERNAL LEVELS, FALLS, RETAINING WALLS & LOCATING CIVIL SERVICES.
- BLACK CONCRETE HAND STIPPLE (ROUGH NON-SLIP) FINISH
COLOUR: CCS BLACK OXIDE 8% DOSAGE RATE (4% DOSAGE RATE FOR FOOTPATH AND KERBS)
SEALANT: NUTECH - PETROL RESISTANT PAVECOAT - PR210 BLACK COLOURED WITH NUTECH ANTI-SLIP ADDITIVE APPLIED AS PER MANUFACTURER'S INSTRUCTIONS.

LEGEND

BFC BROOM FINISH NATURAL GREY CONCRETE
STF STEEL TROWEL FINISH NATURAL GREY CONCRETE
BLACK BLACK CONCRETE HAND STIPPLE FINISH (NON-SLIP)
COLOUR: CCS BLACK OXIDE 8% DOSAGE RATE
SEALANT: NUTECH - PETROL RESISTANT PAVECOAT - PR210 BLACK COLOURED WITH NUTECH ANTI-SLIP ADDITIVE APPLIED AS PER MANUFACTURER'S INSTRUCTIONS.

GENERAL NOTES

- THESE DRAWINGS SHALL BE READ IN CONJUNCTION WITH ALL OTHER CONSULTANTS DRAWINGS AND SPECIFICATIONS.
- DO NOT SCALE DRAWINGS - FIGURED DIMENSIONS ARE TO TAKE PRECEDENCE AT ALL TIMES.
- ALL DIMENSIONS TO BE CONFIRMED ON SITE AND/OR VERIFIED PRIOR TO CONSTRUCTION OR FABRICATION.
- ALL MATERIALS AND WORKMANSHIP SHALL BE IN ACCORDANCE WITH CURRENT AND RELEVANT SAA CODES, NCC OF AUSTRALIA, THE BUILDING ACT, AND LOCAL AUTHORITIES BY-LAWS.
- ALL EXTERNALLY GLAZED WINDOWS AND DOORS TO BE DESIGNED AND CERTIFIED BY THE MANUFACTURER INCLUDING FIXINGS, AND SHALL COMPLY WITH AS1288 & AS1170.2.
- ALL STAIRS, RAMPS, HANDRAILS AND BALUSTRADES ARE TO COMPLY WITH NCC OF AUSTRALIA, SECTION D & AS1428.1.
- THE CONTRACTOR SHALL BE RESPONSIBLE FOR THE STRUCTURE DURING ERECTION AND PROVIDE ADEQUATE PROPPING AND SUPPORT.
- ALL INTERNAL NON-LOADBEARING WALLS, CEILINGS AND OTHER RELEVANT STRUCTURAL COMPONENTS SHALL BE DESIGNED & INSTALLED TO COMPLY WITH SECTION 2 OF AS1170.4 AS REQUIRED.

ARCHITECTURAL NOTES

- ALL EXIT DOORS, AND DOORS IN THE PATH OF TRAVEL TO EXITS ARE TO COMPLY WITH THE RELEVANT AUST. STANDARDS AND THE REQUIREMENTS OF THE NCC.
- ALL DOORWAYS TO HAVE A MINIMUM UNOBSTRUCTED HEIGHT OF 2.0m (UNLESS OTHERWISE NOTED).
- EXIT SIGNS AND EMERGENCY LIGHTS TO COMPLY WITH AS 2293. EXIT SIGNS TO BE MOUNTED AS DETAILED IN THE ELECTRICAL DRAWINGS OR AS OTHERWISE APPROVED BY THE RELEVANT BUILDING SURVEYOR.
- PORTABLE FIRE EXTINGUISHERS TO COMPLY WITH AS 2444.
- ARTIFICIAL LIGHTING TO COMPLY WITH AS 1680.
- MECHANICAL VENTILATION SYSTEM TO COMPLY WITH AS 1668.2 AND AS 3666.
- ALL WET AREAS TO COMPLY WITH NCC PART F17 & ALL RELEVANT PARTS OF AS 3740.
- ALL WET AREAS TO HAVE BOTTOM PLATE FULLY WRAPPED WITH DAMP PROOF MEMBRANE. CONTINUE UP WALL FRAME MIN. 75mm AFFL.
- ALL TOILET AND AIRLOCK WALLS TO BE 45 STC SOUND RATED.
- ALL TIMBERS USED ARE TO BE TREATED FOR SUBTERRANEAN TERMITE ATTACK TO A HAZARD LEVEL OF H2 OR BETTER FOR NON-EXPOSED CONDITIONS.

1 PROP. SITE PLAN - PART A
A100 1 : 200

VERVE SCHEDULES DISCLAIMER:

- ALL SCHEDULES SHOULD BE CHECKED WITH THE REMAINDER OF THE DRAWING SET.
- SCHEDULED RATES AND AREAS ARE INTENDED FOR ASSISTANCE ONLY. NO RESPONSIBILITY IS TAKEN FOR THE ACCURACY OF QUANTITIES.
- ANY DISCREPANCIES IN SCHEDULES SHOULD BE IDENTIFIED TO THE AUTHOR NOTED.
- ALL AREAS ARE GROSS AREAS, UNLESS NOTED OTHERWISE

CONSULTING ENGINEER



- | | |
|---------------------------------------|--|
| ☐ commercial | ☐ service stations |
| ☐ mixed-use | ☐ quick service restaurants |
| ☐ self storage | ☐ child care centres |
| ☐ industrial | ☐ large format retail |

© 2011 copyright, all rights reserved.
This drawing is the © copyright & property of VERVE DESIGN GROUP and must not be used or duplicated without authorisation.
Do not scale this drawing.
Check all dimensions on site prior commencement of works

Revision and approvals				
Rev	Date	Drn	Description	Appr
P1	01.05.2026	PC	REVISED PRELIMINARY ISSUE	SS
A	19.06.2026	PC	BA ISSUE	SS


Project Description				
PROPOSED SERVICE STATION				
22 ENTERPRISE CCT., MARYBOROUGH W.				

Scale @A1		Date	
As indicated		APRIL 2026	
Drawn PC		Approved By SS	

Drawing Title
PART SITE PLAN - AJob Number - Drawing Number
26024

A101

Revision
A

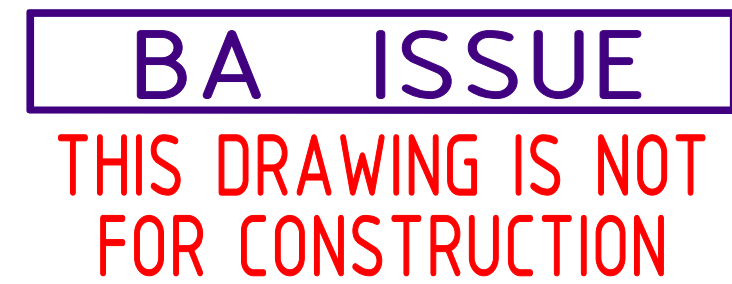

RPD: LOT 53 ON SP200102
PARISH: MARYBOROUGH
COUNTY: MARCH
LOCAL AUTHORITY: FRASER COAST REGIONAL COUNCIL

BOL-1	STEEL BOLLARD TYPE 1 - REFER DETAIL
K	NEW CONCRETE KERB - REFER CIVIL ENG. DETAILS
LM1	LINEMARKING - WHITE - REFER CIVIL ENG. DETAILS
LS	LANDSCAPING - REFER LANDS. ARCH. DETAILS
PL	LIGHT POST - REFER ELECTRICAL ENG. DETAILS
SWG	STORMWATER GULLY - REFER CIVIL ENG. DETAILS
WS	CONCRETE WHEEL STOP. PAINT FINISH SAFETY YELLOW



1. BUILDER TO ALLOW FOR ALL FOOTINGS & ELECTRICAL/DATA CONNECTIONS TO SITE SIGNAGE. REFER STRUCT & ELEC. ENGINEER DRAWINGS FOR DETAIL.
2. BUILDER TO COORDINATE WITH SITE SIGNAGE PLAN (DA APPROVED PLANS).
3. REFER TO CIVIL ENG. DRAWINGS FOR EXTERNAL LEVELS, FALLS, RETAINING WALLS & LOCATING CIVIL SERVICES.
4. BLACK CONCRETE HAND STIPPLE (ROUGH NON-SLIP) FINISH
 COLOUR: CCS BLACK OXIDE 8% DOSAGE RATE (4% DOSAGE RATE FOR FOOTPATH AND KERBS)
 SEALANT: NUTECH - PETROL RESISTANT PAVECOAT - PR210 BLACK COLOURED WITH NUTECH ANTI-SLIP ADDITIVE APPLIED AS PER MANUFACTURER'S INSTRUCTIONS.

BFC	BROOM FINISH NATURAL GREY CONCRETE
STF	STEEL TROWEL FINISH NATURAL GREY CONCRETE
BLACK	BLACK CONCRETE HAND STIPPLE FINISH (NON-SLIP) COLOUR: CCS BLACK OXIDE 8% DOSAGE RATE SEALANT: NUTECH - PETROL RESISTANT PAVECOAT - PR210 BLACK COLOURED WITH NUTECH ANTI-SLIP ADDITIVE APPLIED AS PER MANUFACTURER'S INSTRUCTIONS.

1. THESE DRAWINGS SHALL BE READ IN CONJUNCTION WITH ALL OTHER CONSULTANTS DRAWINGS AND SPECIFICATIONS.
2. DO NOT SCALE DRAWINGS - FIGURED DIMENSIONS ARE TO TAKE PRECEDENCE AT ALL TIMES.
3. ALL DIMENSIONS TO BE CONFIRMED ON SITE AND/OR VERIFIED PRIOR TO CONSTRUCTION OR FABRICATION.
4. ALL MATERIALS AND WORKMANSHIP SHALL BE IN ACCORDANCE WITH CURRENT AND RELEVANT SAA CODES, NCC OF AUSTRALIA, THE BUILDING ACT, AND LOCAL AUTHORITIES BY-LAWS.
5. ALL EXTERNALLY GLAZED WINDOWS AND DOORS TO BE DESIGNED AND CERTIFIED BY THE MANUFACTURER INCLUDING FIXINGS, AND SHALL COMPLY WITH AS1288 & AS1170.2.
6. ALL STAIRS, RAMPS, HANDRAILS AND BALUSTRADES ARE TO COMPLY WITH NCC OF AUSTRALIA, SECTION D & AS1428.1.
7. THE CONTRACTOR SHALL BE RESPONSIBLE FOR THE STRUCTURE DURING ERECTION AND PROVIDE ADEQUATE PROPPING AND SUPPORT
8. ALL INTERNAL NON-LOADBEARING WALLS, CEILINGS AND OTHER RELEVANT STRUCTURAL COMPONENTS SHALL BE DESIGNED & INSTALLED TO COMPLY WITH SECTION 2 OF AS1170.4 AS REQUIRED.

1. ALL EXIT DOORS, AND DOORS IN THE PATH OF TRAVEL TO EXITS ARE TO COMPLY WITH THE RELEVANT AUST. STANDARDS AND THE REQUIREMENTS OF THE NCC.
2. ALL DOORWAYS TO HAVE A MINIMUM UNOBSTRUCTED HEIGHT OF 2.0m (UNLESS OTHERWISE NOTED).
3. EXIT SIGNS AND EMERGENCY LIGHTS TO COMPLY WITH AS 2293. EXIT SIGNS TO BE MOUNTED AS DETAILED IN THE ELECTRICAL DRAWINGS OR AS OTHERWISE APPROVED BY THE RELEVANT BUILDING SURVEYOR.
4. PORTABLE FIRE EXTINGUISHERS TO COMPLY WITH AS 2444.
5. ARTIFICIAL LIGHTING TO COMPLY WITH AS 1680.
6. MECHANICAL VENTILATION SYSTEM TO COMPLY WITH AS 1668,2 AND AS 3666.
7. ALL WET AREAS TO COMPLY WITH NCC PART F1.7 & ALL RELEVANT PARTS OF AS 3740.
8. ALL WET AREAS TO HAVE BOTTOM PLATE FULLY WRAPPED WITH DAMP PROOF MEMBRANE. CONTINUE UP WALL FRAME MIN. 75mm AFFL.
9. ALL TOILET AND AIRLOCK WALLS TO BE 45 STC SOUND RATED.
10. ALL TIMBERS USED ARE TO BE TREATED FOR SUBTERRANEAN TERMITE ATTACK TO A HAZARD LEVEL OF H2 OR BETTER FOR NON-EXPOSED CONDITIONS.

1. ALL SCHEDULES SHOULD BE CHECKED WITH THE REMAINDER OF THE DRAWING SET.
2. SCHEDULED RATES AND AREAS ARE INTENDED FOR ASSISTANCE ONLY. NO RESPONSIBILITY IS TAKEN FOR THE ACCURACY OF QUANTITIES.
3. ANY DISCREPANCIES IN SCHEDULES SHOULD BE IDENTIFIED TO THE AUTHOR NOTED.
4. ALL AREAS ARE GROSS AREAS, UNLESS NOTED OTHERWISE



VERVE
DESIGN GROUP

QBCC LICENCE No. 1236672 PH. (07) 3857 0842
OFFICE 1, LEVEL 1, 488 LUTWYCHE RD, LUTWYCHE 4030 info@vervedesigngroup.com.au

imagine create deliver

- ☐ commercial
- ☐ mixed-use
- ☐ self storage
- ☐ industrial
- ☐ service stations
- ☐ quick service restaurants
- ☐ child care centres
- ☐ large format retail

© 2011 copyright, all rights reserved


This drawing is the © copyright & property of VERVE DESIGN GROUP and must not be used or duplicated without authorisation.

Do not scale this drawing.

Check all dimensions on site prior commencement of works

Project Description	PROPOSED SERVICE STATION	
22 ENTERPRISE CCT., MARYBOROUGH W.		
Scale @A1 As indicated	Date	APRIL 2026
Drawn BC	Approved By	SC

Job Number - Drawing Number	Revision
26024 A102	A

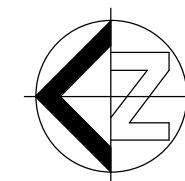


BA ISSUE

THIS DRAWING IS NOT
FOR CONSTRUCTION

LEGEND

2SS	
ARB	ARMCO VEHICLE BARRIER - REFER TO CIVIL ENG. FOR DETAILS
ATM	AUTOMATIC TELLER MACHINE - SUPPLIED & INSTALLED BY LESSEE
BOL-2	STEEL BOLLARD TYPE 2 - REFER DETAIL
BT	BUCKET TRAP - REFER HYD. ENG. DETAILS
CDS	COLDROOM DISPLAY SHELVING
CFD	COLD FOOD DISPLAY - SUPPLIED & INSTALLED BY LESSEE
CH2	LOOSE HIGH STOOL
CM	COFFEE MACHINE - SUPPLIED & INSTALLED BY LESSEE
COL	COLUMN - REFER STRUCT. ENG. DETAILS
CSK	CLEANERS SINK WITH STAINLESS STEEL COVER - REFER HYD. ENG. DETAILS
CTM	CLEANERS TAP MIXER
DB	DISTRIBUTION BOARD - REFER ELEC. ENG. DETAILS
DP	DOWNPIPE - REFER HYD. ENG. DETAILS
DS	DIGITAL SCALE
DTR	DATA RACK - REFER ELEC. ENG. DETAILS
DW	DISHWASHER - SUPPLIED & INSTALLED BY LESSEE
EGR	ELEC. GRIDDLE - SUPPLIED & INSTALLED BY LESSEE
EP	ELECTRICAL PIT - REFER ELEC. ENG. DETAILS
FB	FOLDING BENCH - SUPPLIED & INSTALLED BY LESSEE
FBX	FLOOR BOX - REFER ELEC. ENG. DETAILS
FES	FUEL EMERGENCY STOP BUTTON - REFER FUEL ENG. DETAILS
FRY	FRYERS - SUPPLIED & INSTALLED BY LESSEE
FSB	FUEL SWITCHBOARD - REFER ELEC. ENG. DETAILS
FVP	FUEL/SPEL VENT PIPES - REFER FUEL ENG. DETAILS
FW	FLOOR WASTE - REFER HYD. ENG. DETAILS
HB	HAND BASIN - REFER HYD. ENG. DETAILS
HFD	HOT FOOD DISPLAY - 900 WIDE - COSSIGA
HT	HOSECOCK TAP CONNECTION - REFER HYD. ENG. DETAILS
IC	ICE CREAM FREEZER - SUPPLIED & INSTALLED BY LESSEE
IS	ICE STORAGE - SUPPLIED & INSTALLED BY LESSEE
KR	KERB RAMP TO COMPLY WITH AS1428.1
KY	NEW CONCRETE KERB PAINT FINISH SAFETY YELLOW - REFER CIVIL ENG. DETAILS
LM1	LINEMARKING - WHITE - REFER CIVIL ENG. DETAILS
LPG	LPG CYLINDER STORAGE - SUPPLIED & INSTALLED BY LESSEE
LT	LAUNDRY TUB - SUPPLIED & INSTALLED BY LESSEE
MSB	ELECTRICAL MAIN SWITCHBOARD - REFER ELEC. ENG. DETAILS
MW	MICROWAVE - SUPPLIED & INSTALLED BY LESSEE
NBN	NATIONAL BROADBAND NETWORK CONNECTION - REFER ELEC. ENG. DETAILS
NPW	NIGHT PAY WINDOW - STERLING
ODR	STAINLESS STEEL OVERHEAD DRYING RACK
PO	PIE OVEN WARMER - SUPPLIED & INSTALLED BY LESSEE
POS	POINT OF SALE - SUPPLIED & INSTALLED BY LESSEE
SAF	DIGITAL SAFE
SES-3	STRATCO EZI-SLAT ALUMINIUM SCREENING - 75mm SLATS - 25mm GAP. COLOUR MONUMENT
SGR	SANDWICH GRILL
SH	SHELVING
SSB	STAINLESS STEEL BENCH - SUPPLIED & INSTALLED BY LESSEE
SSB-2	STAINLESS STEEL BENCH WITH SINGLE BOWL SINK
ST	REFRIGERATED SALAD PREP TABLE - SUPPLIED & INSTALLED BY LESSEE
SZ	SLURPEE ZONE - REFER JOINERY DRAWINGS FOR DETAIL - TO BE SUPPLIED & INSTALLED BY LESSEE CONTRACTOR
TAP	HOB MOUNTED SPRAY RINSE TAP ASSEMBLY - SUPPLIED & INSTALLED BY LESSEE
TBL-1	LOOSE TABLE - SUPPLIED & INSTALLED BY LESSEE
TD	TUNDISH - REFER HYD. ENG. DETAILS
TR	18 LOCALISED DOOR THRESHOLD RAMP TO COMPLY WITH AS1428.1
VP	VENT PIPE - REFER HYD. ENG. DETAILS
WS	CONCRETE WHEEL STOP. PAINT FINISH SAFETY YELLOW
WSH/DRY	STACKED WASHER/DRYER - SUPPLIED & INSTALLED BY LESSEE

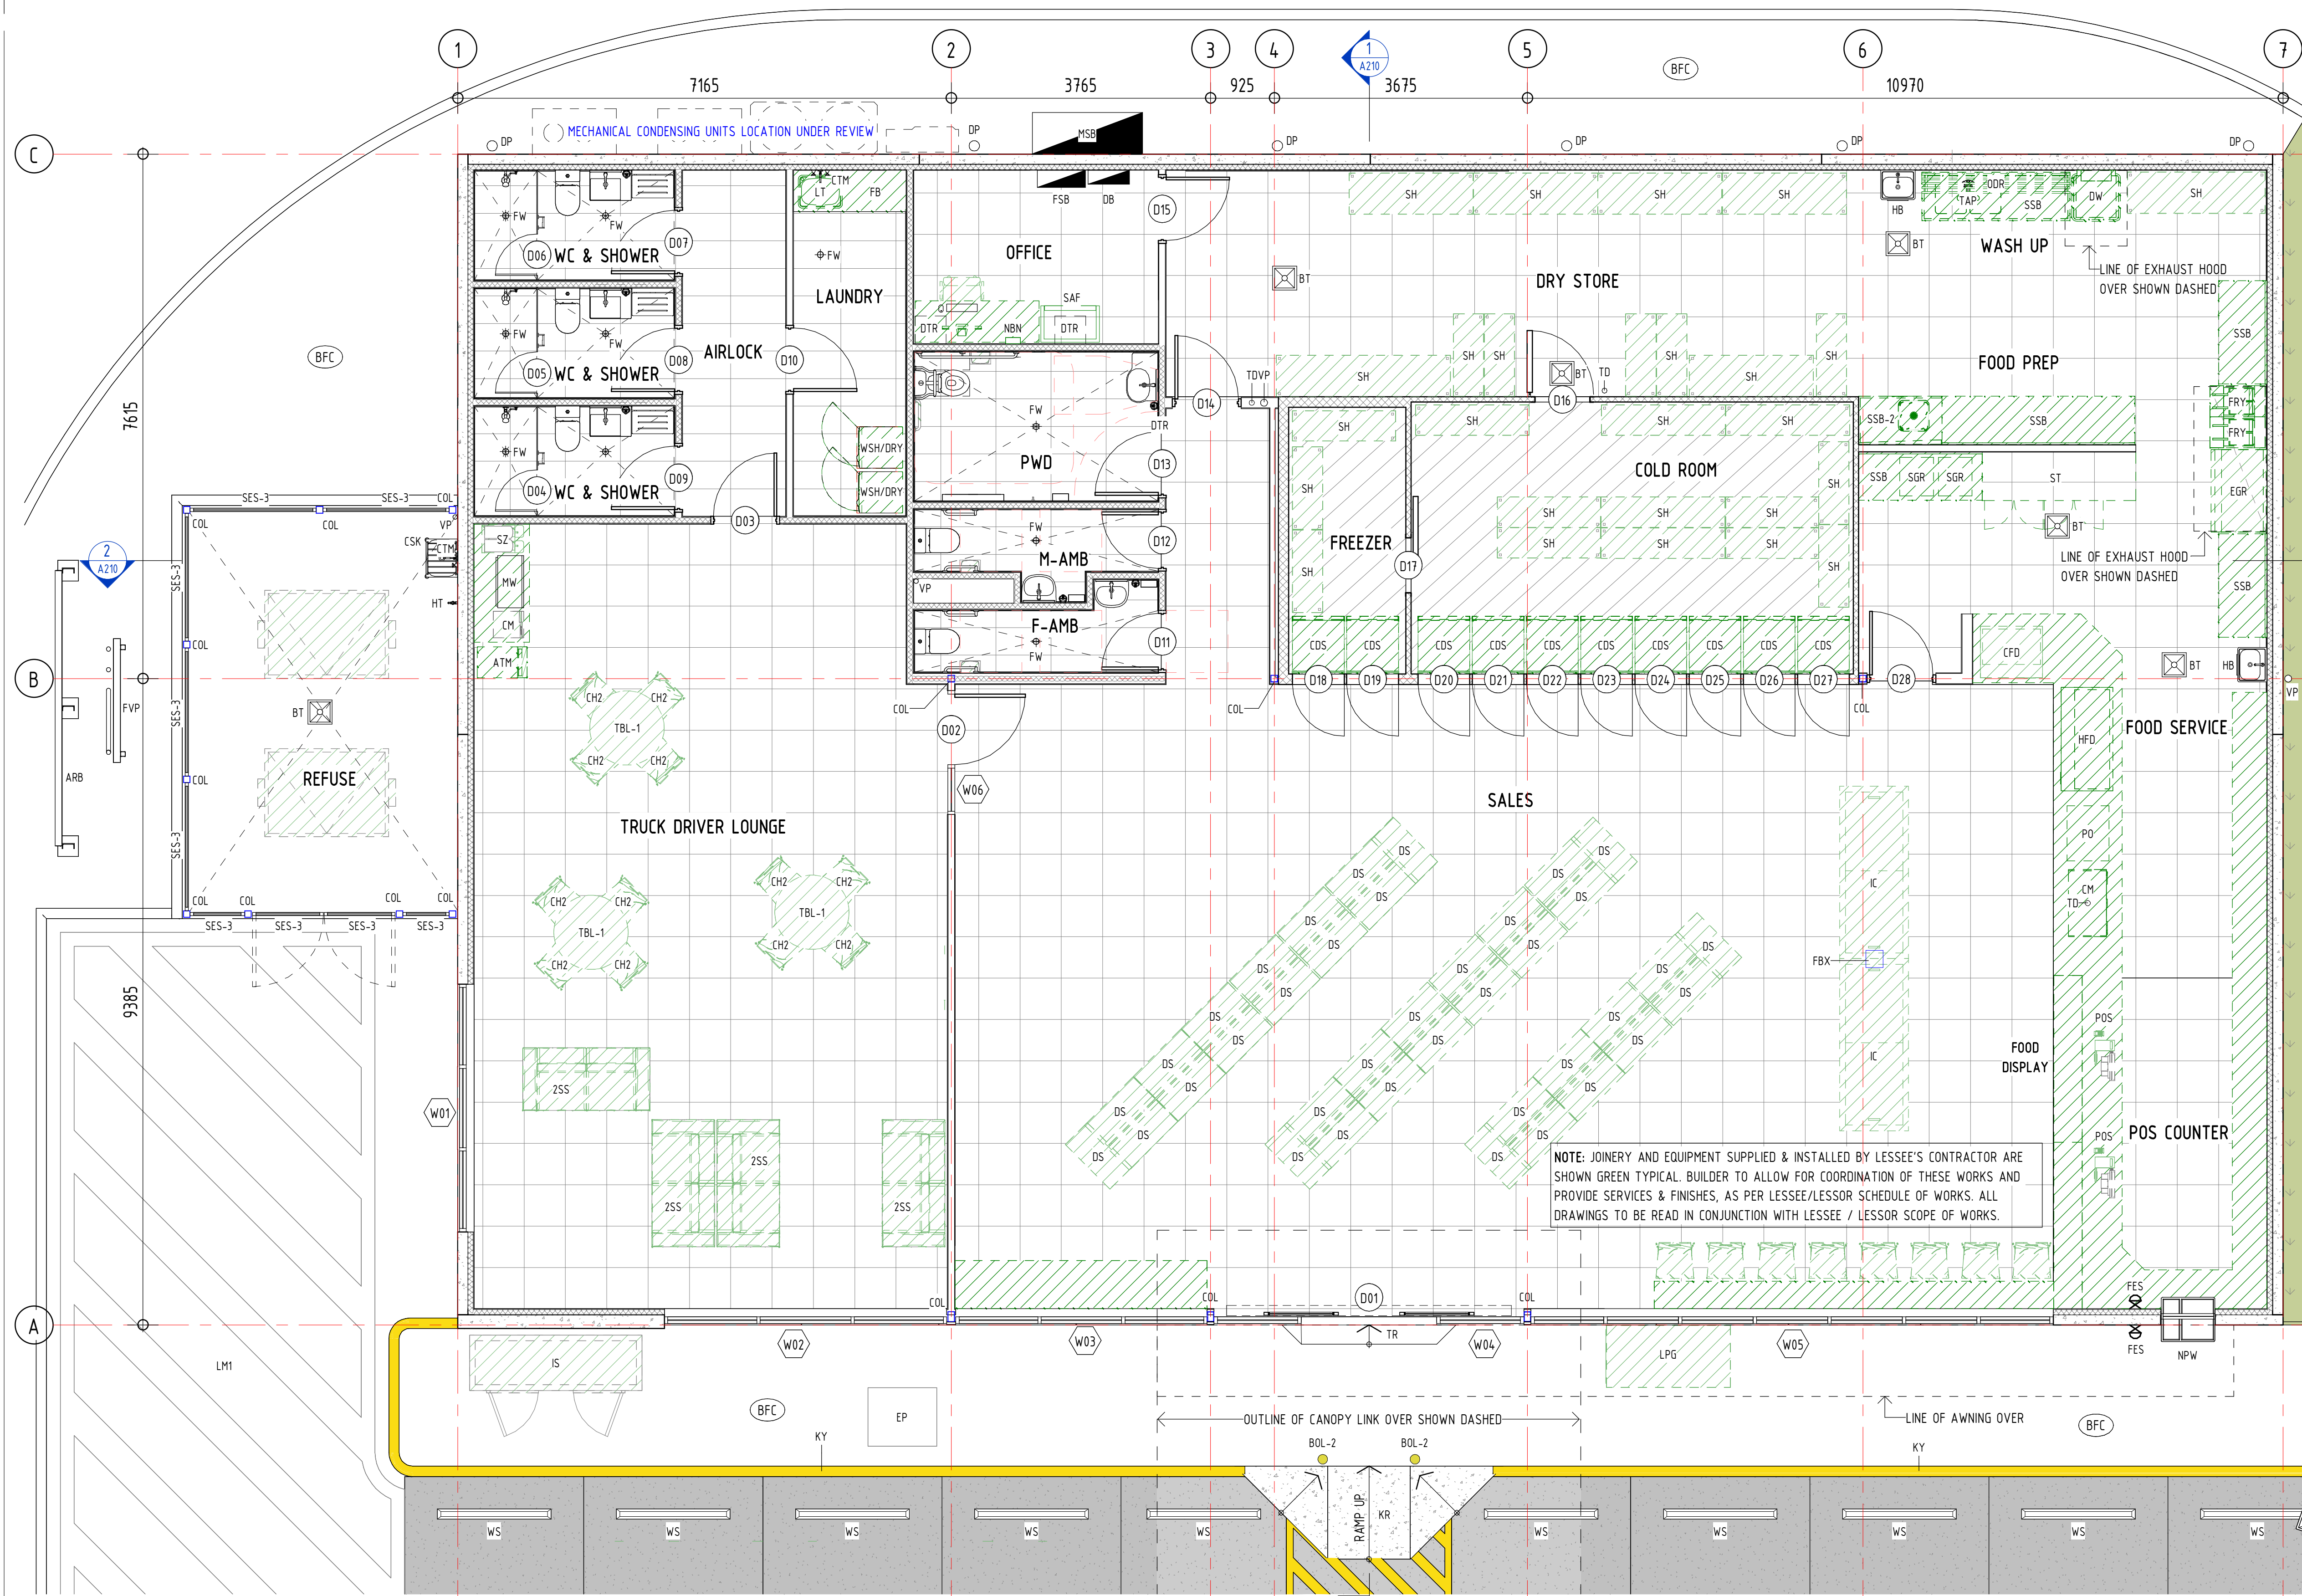

1 PROP. FLOOR PLAN
1:50

ARCHITECTURAL NOTES

- ALL EXIT DOORS, AND DOORS IN THE PATH OF TRAVEL TO EXITS ARE TO COMPLY WITH THE RELEVANT AUST. STANDARDS AND THE REQUIREMENTS OF THE NCC.
- ALL DOORWAYS TO HAVE A MINIMUM UNOBSTRUCTED HEIGHT OF 2.0m (UNLESS OTHERWISE NOTED).
- EXIT SIGNS AND EMERGENCY LIGHTS TO COMPLY WITH AS 2293. EXIT SIGNS TO BE MOUNTED AS DETAILED IN THE ELECTRICAL DRAWINGS OR AS OTHERWISE APPROVED BY THE RELEVANT BUILDING SURVEYOR.
- PORTABLE FIRE EXTINGUISHERS TO COMPLY WITH AS 2444.
- ARTIFICIAL LIGHTING TO COMPLY WITH AS 1680.
- MECHANICAL VENTILATION SYSTEM TO COMPLY WITH AS 1668.2 AND AS 3666.
- ALL WET AREAS TO COMPLY WITH NCC PART F17 & ALL RELEVANT PARTS OF AS 3740.
- ALL WET AREAS TO HAVE BOTTOM PLATE FULLY WRAPPED WITH DAMP PROOF MEMBRANE. CONTINUE UP WALL FRAME MIN. 75mm AFFL.
- ALL TOILET AND AIRLOCK WALLS TO BE 45 STC SOUND RATED.
- ALL TIMBERS USED ARE TO BE TREATED FOR SUBTERRANEAN TERMITE ATTACK TO A HAZARD LEVEL OF H2 OR BETTER FOR NON-EXPOSED CONDITIONS.

GENERAL NOTES

- THESE DRAWINGS SHALL BE READ IN CONJUNCTION WITH ALL OTHER CONSULTANTS DRAWINGS AND SPECIFICATIONS.
- DO NOT SCALE DRAWINGS - FIGURED DIMENSIONS ARE TO TAKE PRECEDENCE AT ALL TIMES.
- ALL DIMENSIONS TO BE CONFIRMED ON SITE AND/OR VERIFIED PRIOR TO CONSTRUCTION OR FABRICATION.
- ALL MATERIALS AND WORKMANSHIP SHALL BE IN ACCORDANCE WITH CURRENT AND RELEVANT SAA CODES, NCC OF AUSTRALIA, THE BUILDING ACT, AND LOCAL AUTHORITIES BY-LAWS.
- ALL EXTERNALLY GLAZED WINDOWS AND DOORS TO BE DESIGNED AND CERTIFIED BY THE MANUFACTURER INCLUDING FIXINGS, AND SHALL COMPLY WITH AS1288 & AS1170.2.
- ALL STAIRS, RAMPS, HANDRAILS AND BALUSTRADES ARE TO COMPLY WITH NCC OF AUSTRALIA, SECTION D & AS1428.1.
- THE CONTRACTOR SHALL BE RESPONSIBLE FOR THE STRUCTURE DURING ERECTION AND PROVIDE ADEQUATE PROPPING AND SUPPORT
- ALL INTERNAL NON-LOADBEARING WALLS, CEILINGS AND OTHER RELEVANT STRUCTURAL COMPONENTS SHALL BE DESIGNED & INSTALLED TO COMPLY WITH SECTION 2 OF AS1170.4 AS REQUIRED.

VERVE SCHEDULES DISCLAIMER:

- ALL SCHEDULES SHOULD BE CHECKED WITH THE REMAINDER OF THE DRAWING SET.
- SCHEDULED RATES AND AREAS ARE INTENDED FOR ASSISTANCE ONLY. NO RESPONSIBILITY IS TAKEN FOR THE ACCURACY OF QUANTITIES.
- ANY DISCREPANCIES IN SCHEDULES SHOULD BE IDENTIFIED TO THE AUTHOR NOTED.
- ALL AREAS ARE GROSS AREAS, UNLESS NOTED OTHERWISE

CONSULTING ENGINEER




- | | |
|---------------------------------------|--|
| ☐ commercial | ☐ service stations |
| ☐ mixed-use | ☐ quick service restaurants |
| ☐ self storage | ☐ child care centres |
| ☐ industrial | ☐ large format retail |

© 2011 copyright, all rights reserved.
This drawing is the © copyright & property of VERVE DESIGN GROUP and must not be used or duplicated without authorisation.
Do not scale this drawing.
Check all dimensions on site prior commencement of works

Revision and approvals				
Rev	Date	Drn	Description	Appr
P1	12.02.2026	PC	PRELIMINARY ISSUE	SS
P2	24.02.2026	PC	REVISED PRELIMINARY ISSUE	SS
P3	09.03.2026	PC	REVISED PRELIMINARY ISSUE	SS
P4	01.05.2026	PC	REVISED PRELIMINARY ISSUE	SS
A	19.06.2026	PC	BA ISSUE	SS

Project Description	
PROPOSED SERVICE STATION	
22 ENTERPRISE CCT., MARYBOROUGH W.	
Scale @A1 1:50	Date FEBRUARY 2026
Drawn PC	Approved By SS

Drawing Title	
PROP. FLOOR PLAN	
Job Number - Drawing Number 26024 A110	Revision A

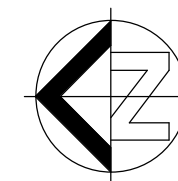

BA ISSUE
THIS DRAWING IS NOT FOR CONSTRUCTION

LEGEND	
CBF-2	COLORBOND FLASHING - COLOUR SURFMIST
COL	COLUMN - REFER STRUCT. ENG. DETAILS
DP	DOWNPIPE - REFER HYD. ENG. DETAILS
LTD-S	LYSAGHT TRIMDEK 0.48BMT COLORBOND SURFMIST
PC-3	PARAPET CAPPING. COLOUR: COLORBOND MONUMENT
PF	PAN FLASHING - COLOUR TO MATCH ROOF
RAL	PROPRIETARY ROOF ACCESS LADDER TO CONTRACTOR SPECIFICATION TO COMPLY WITH AS1657:2018
RAP	SURFACE MOUNT ROOF ACCESS POINT LADDER SUPPORT BRACKET INSTALLED TO MAN. SPEC.
RC	ROOF COWL - REFER MECH. ENG. DETAILS
SGN-5	ILLUMINATED BLADE RETAILER SIGNAGE SUPPLIED & INSTALLED BY LESSEE CONTRACTOR. BUILDER TO PROVIDE POWER SERVICE
VP	VENT PIPE - REFER HYD. ENG. DETAILS

NOTE:
THIS DRAWING TO BE READ IN CONJUNCTION WITH ROOF STORMWATER DRAWINGS PREPARED BY HYDRAULIC ENGINEER

RL NOTE:
RL's SHOWN ARE IN METRES AND REFER TO DATUM LEVEL 00.00


PROPRIETARY ROOF ACCESS SYSTEM
WHERE REQUIRED INSTALL A PROPRIETARY ROOF ACCESS LANYARD SYSTEM TO ASSIST IN THE SAFE ACCESS AND MAINTENANCE OF THE WHOLE OF THE ROOFED AREAS OF THE BUILDING AT ROOF LEVEL.
THE SYSTEM IS TO COMPLY TO AS/NZS 1891.1/1891.2
SUPPLIER/INSTALLER TO PROVIDE PERMANENT LADDER BRACKET, SAFETY GATE, ROOF WALKWAY & APPROPRIATE ROOF MOUNTED HANDRAILS AS REQUIRED.

1. PROPRIETARY ROOF ACCESS SYSTEM INDICATED ON PLAN IS DIAGRAMMATIC ONLY. SUPPLIER/INSTALLER TO DESIGN, INSTALL & CERTIFY SYSTEM.
2. SUPPLIER/INSTALLER TO PROVIDE APPROPRIATE ROOF ACCESS SYSTEM AND SAFETY WARNING SIGNS (AS PER AS 1657). SUPPLIER/INSTALLER TO CONFIRM COMPLIANCE OF ROOF SAFETY SYSTEM WITH RELEVANT STANDARDS PRIOR TO INSTALLATION.

MECHANICAL NOTE :
MECHANICAL EQUIPMENT AND PENETRATION LOCATIONS ARE DIAGRAMMATIC ONLY. REFER MECHANICAL DRAWINGS FOR LOCATIONS AND CLEARANCE REQUIREMENTS.

ROOFING NOTES

1. ROOF SHEETING TO BE **LYSAGHT TRIMDEK 0.48 BMT & LYSAGHT KLIP-LOK 700 HS 0.48 BMT**. AS NOTED ON PLAN.
2. ALL FLASHINGS, CAPPINGS & GUTTERS TO BE COLORBOND FINISH
3. REFER TO MECHANICAL & HYDRAULICS DRAWINGS FOR ROOF PENETRATIONS & EQUIPMENT LOCATIONS.
4. MINIMUM FALL TO GUTTERS TO BE 1:100.
5. ALL EXPOSED DUCTWORK TO BE PAINTED WHITE U.N.O
6. FOLDED METAL CAP OVER JUNCTION OF BOX GUTTERS AT HIGH POINT.
7. CONTINUOUS 1.2mm BMT METAL OVER-FLASHING FROM RIDGE OR CHANGE IN ROOF PITCH TO ROOF PENETRATION.
8. SUPPLY AND INSTALL REMOVABLE LEAF GUARD OVER DOWNPIPES AS REQUIRED.
9. SUPPLY AND INSTALL REMOVABLE GRATES OVER RAIN WATER HEADS AND SUMPS AS REQUIRED.
10. TURN UP SHEET ENDS UNDER FLASHINGS & DOWN INTO GUTTERS.
11. PROVIDE PROFILED FILLERS TO ENDS OF SHEETING, (BETWEEN SHEET & PURLIN AND SHEET & FLASHING).
12. SCRIBE ALL FLASHINGS AND CAPPINGS ACCORDINGLY TO PROFILES. UPSTANDS TO BE MIN. 100mm(H). OVER FLASHINGS TO BE MIN. 200mm(W) AND COVER 2 ROOF PROFILES. VERTICAL LAPS TO BE MIN 100mm. HORIZONTAL LAPS TO BE MIN 150mm.
13. INSTALL SOAKERS ON HIGH SIDE OF ALL ROOF PENETRATIONS UNDER ROOF SHEETING AND APRON FLASHINGS TO OTHER THREE SIDES.
14. ALL EXTERNAL STEELWORK TO BE HOT DIPPED GALVANISED UNLESS OTHERWISE NOTED.
15. ALL SERVICE LINES AND POST PENETRATIONS THROUGH ROOF TO HAVE DEKTITE FLASHINGS.
16. OVERFLASHINGS AND SOAKER FLASHINGS ARE TO BE SAW CUT AND SEALED IN TO BLOCK WALLS WHERE APPLICABLE.

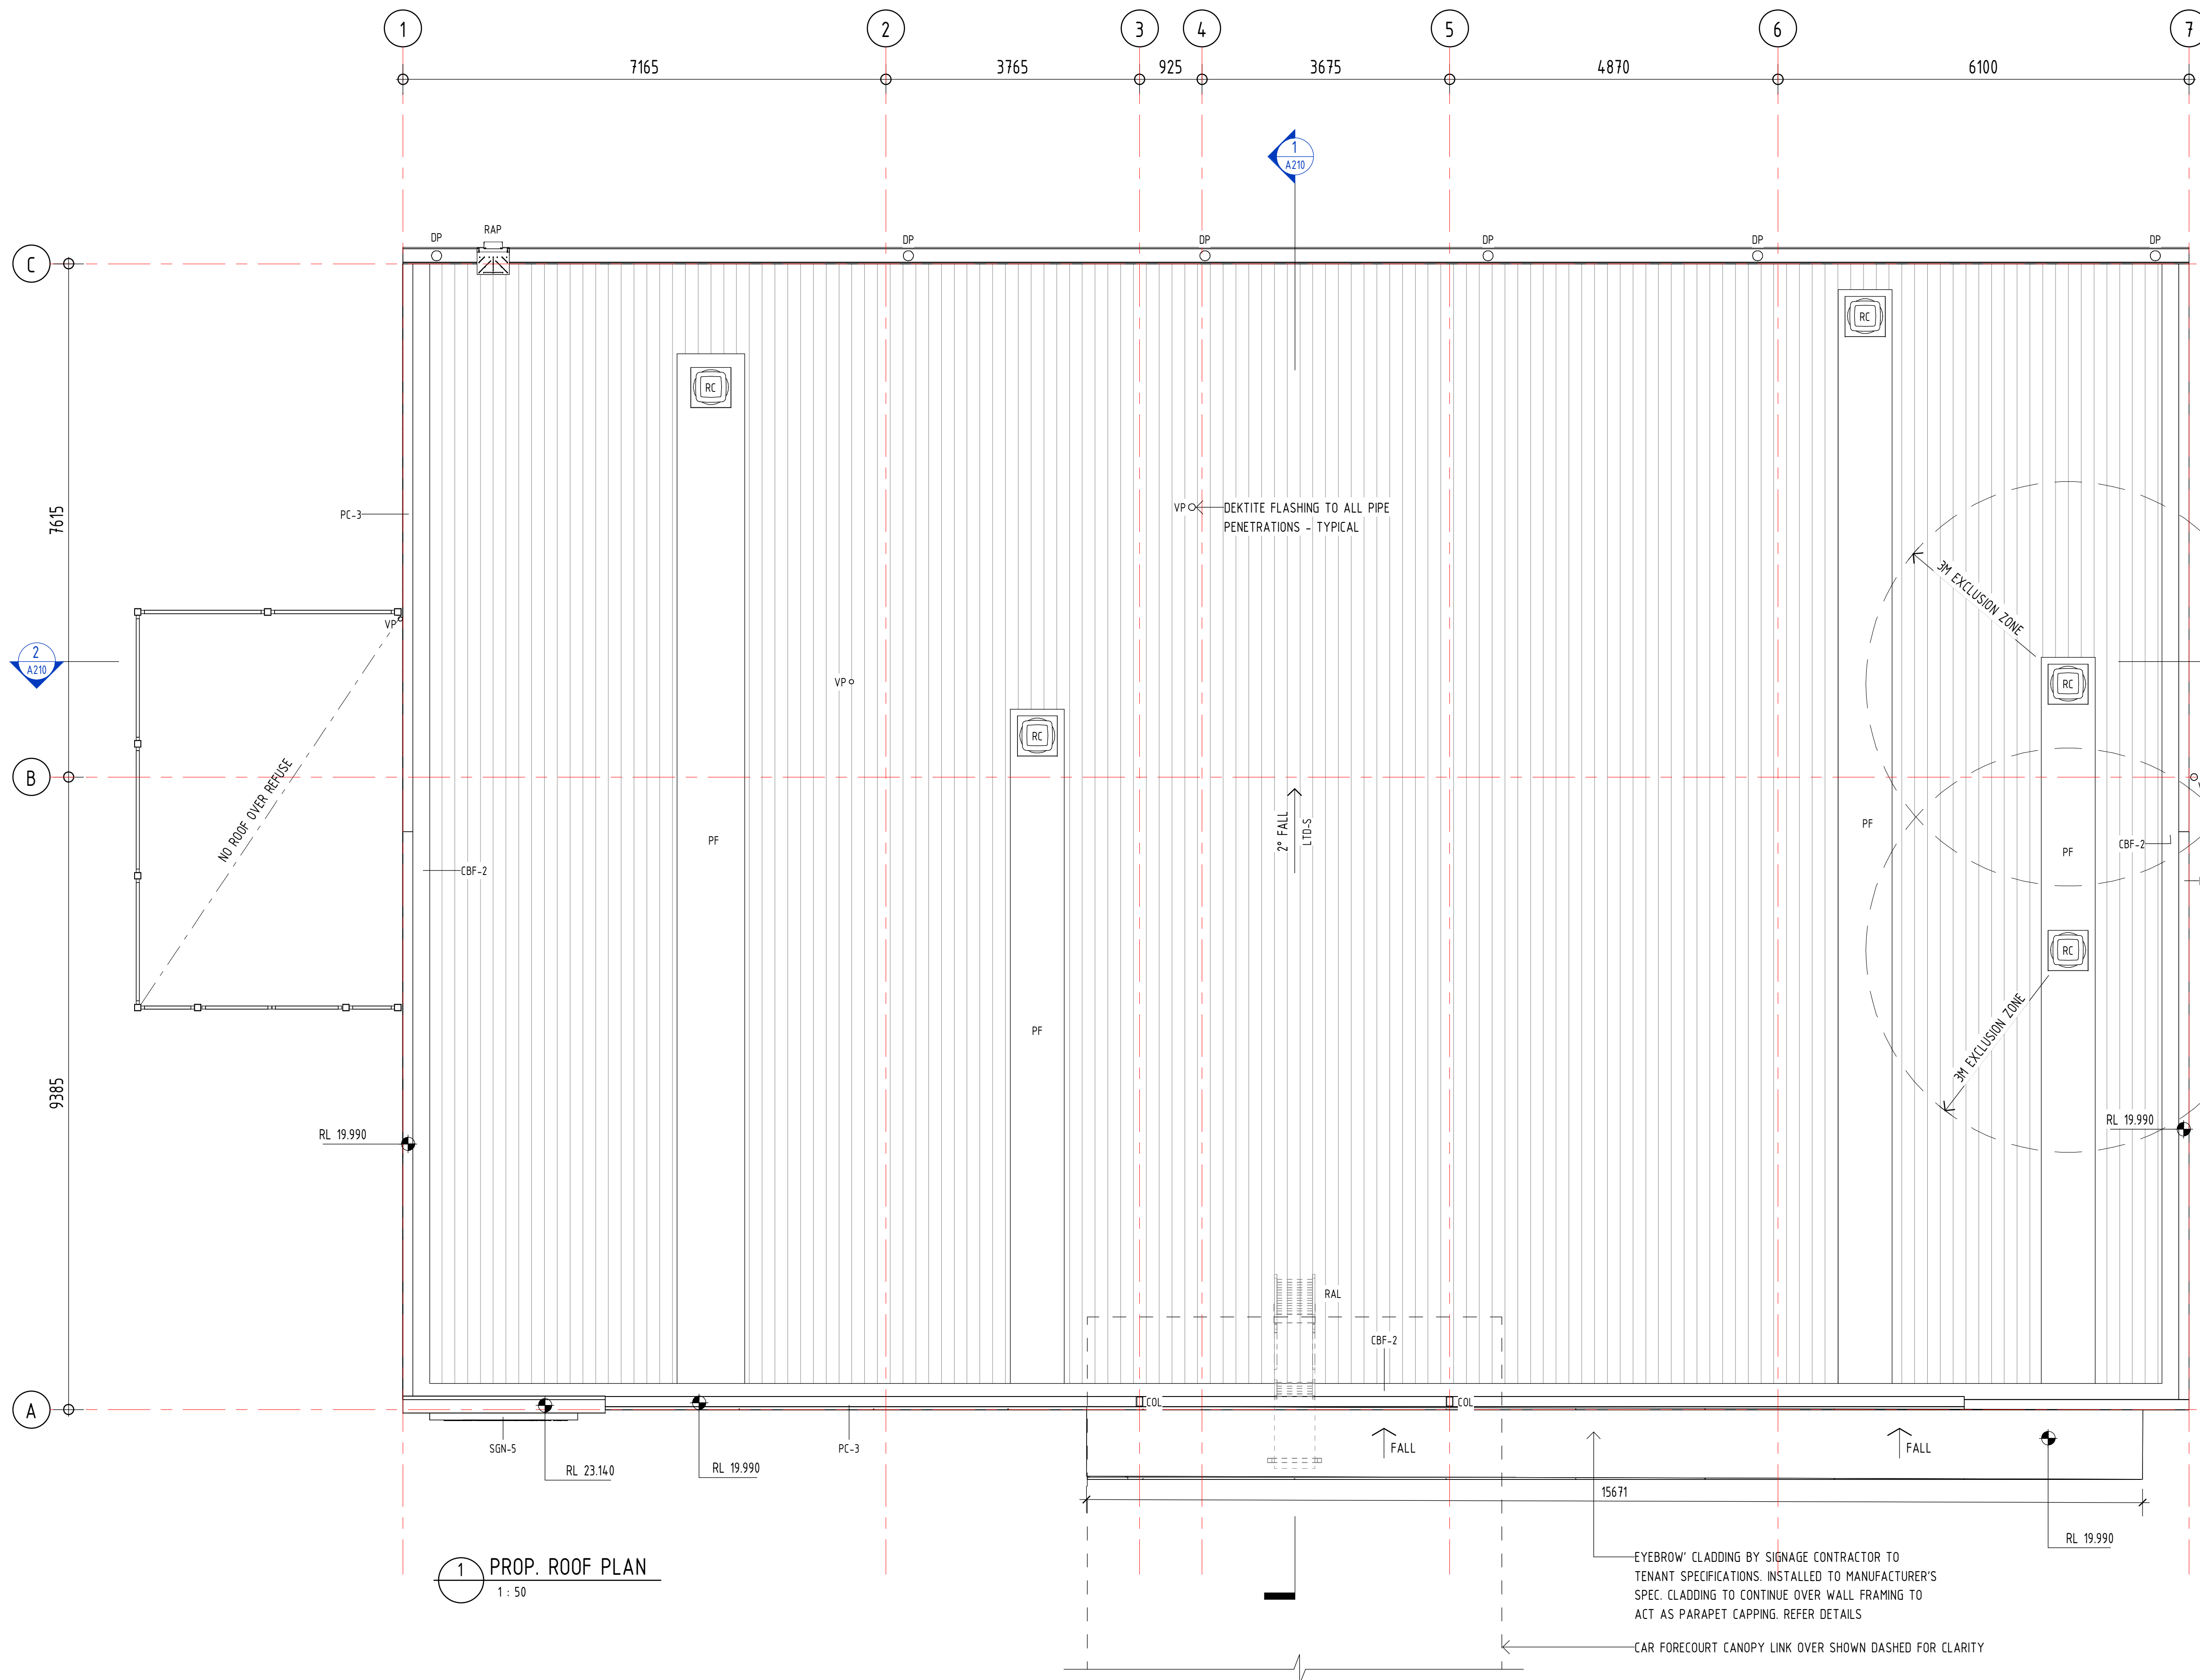

VERVE SCHEDULES DISCLAIMER:

1. ALL SCHEDULES SHOULD BE CHECKED WITH THE REMAINDER OF THE DRAWING SET.
2. SCHEDULED RATES AND AREAS ARE INTENDED FOR ASSISTANCE ONLY. NO RESPONSIBILITY IS TAKEN FOR THE ACCURACY OF QUANTITIES.
3. ANY DISCREPANCIES IN SCHEDULES SHOULD BE IDENTIFIED TO THE AUTHOR NOTED.
4. ALL AREAS ARE GROSS AREAS, UNLESS NOTED OTHERWISE

CONSULTING ENGINEER




☐ commercial ☐ service stations
☐ mixed-use ☐ quick service restaurants
☐ self storage ☐ child care centres
☐ industrial ☐ large format retail

© 2011 copyright, all rights reserved.
This drawing is the © copyright & property of VERVE DESIGN GROUP and must not be used or duplicated without authorisation.
Do not scale this drawing.
Check all dimensions on site prior commencement of works

Revision and approvals				
Rev	Date	Drn	Description	Appr
P1	12.02.2026	PC	PRELIMINARY ISSUE	SS
P2	01.05.2026	PC	REVISED PRELIMINARY ISSUE	SS
A	19.06.2026	PC	BA ISSUE	SS

Project Description	
PROPOSED SERVICE STATION	
22 ENTERPRISE CCT., MARYBOROUGH W.	
Scale @A1 1: 50	Date FEBRUARY 2026
Drawn PC	Approved By SS


Drawing Title	
PROP. ROOF PLAN	
Job Number - Drawing Number 26024 A115	Revision A

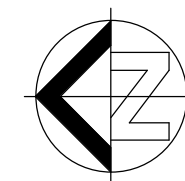

BA ISSUE

THIS DRAWING IS NOT
FOR CONSTRUCTION

LEGEND	
B-1	SURFACE MOUNTED COLD ROOM BATTEN LIGHT - REFER ELEC. ENG. FOR DETAILS
D-1	RECESSED LED DOWNLIGHT - REFER ELEC. ENG. FOR DETAILS
DP	DOWNPIPE - REFER HYD. ENG. DETAILS
EES	EMERGENCY EXIT SIGN - REFER ELEC. ENG. DETAILS
EG	EAVES GUTTER - REFER HYD. ENG. DETAILS
EML	EMERGENCY LIGHT - REFER ELEC. ENG. DETAILS
EX	EXHAUST EGGRATE GRILLE - REFER MECH. ENG. DETAILS
EXH	MECHANICAL EXHAUST HOOD - REFER MECH. ENG. DETAILS
MS	MOTION SENSOR - REFER ELEC. ENG. DETAILS
NPW	NIGHT PAY WINDOW - STERLING
RA	RETURN AIR REGISTER - REFER MECH. ENG. DETAILS
RG	RELIEF GRILLE - REFER MECH. ENG. DETAILS
SA	SUPPLY AIR REGISTER - REFER MECH. ENG. DETAILS
T-1	TRCESSED T-BAR TROFFER - REFER ELEC. ENG. FOR DETAILS
T-2	
VP	VENT PIPE - REFER HYD. ENG. DETAILS

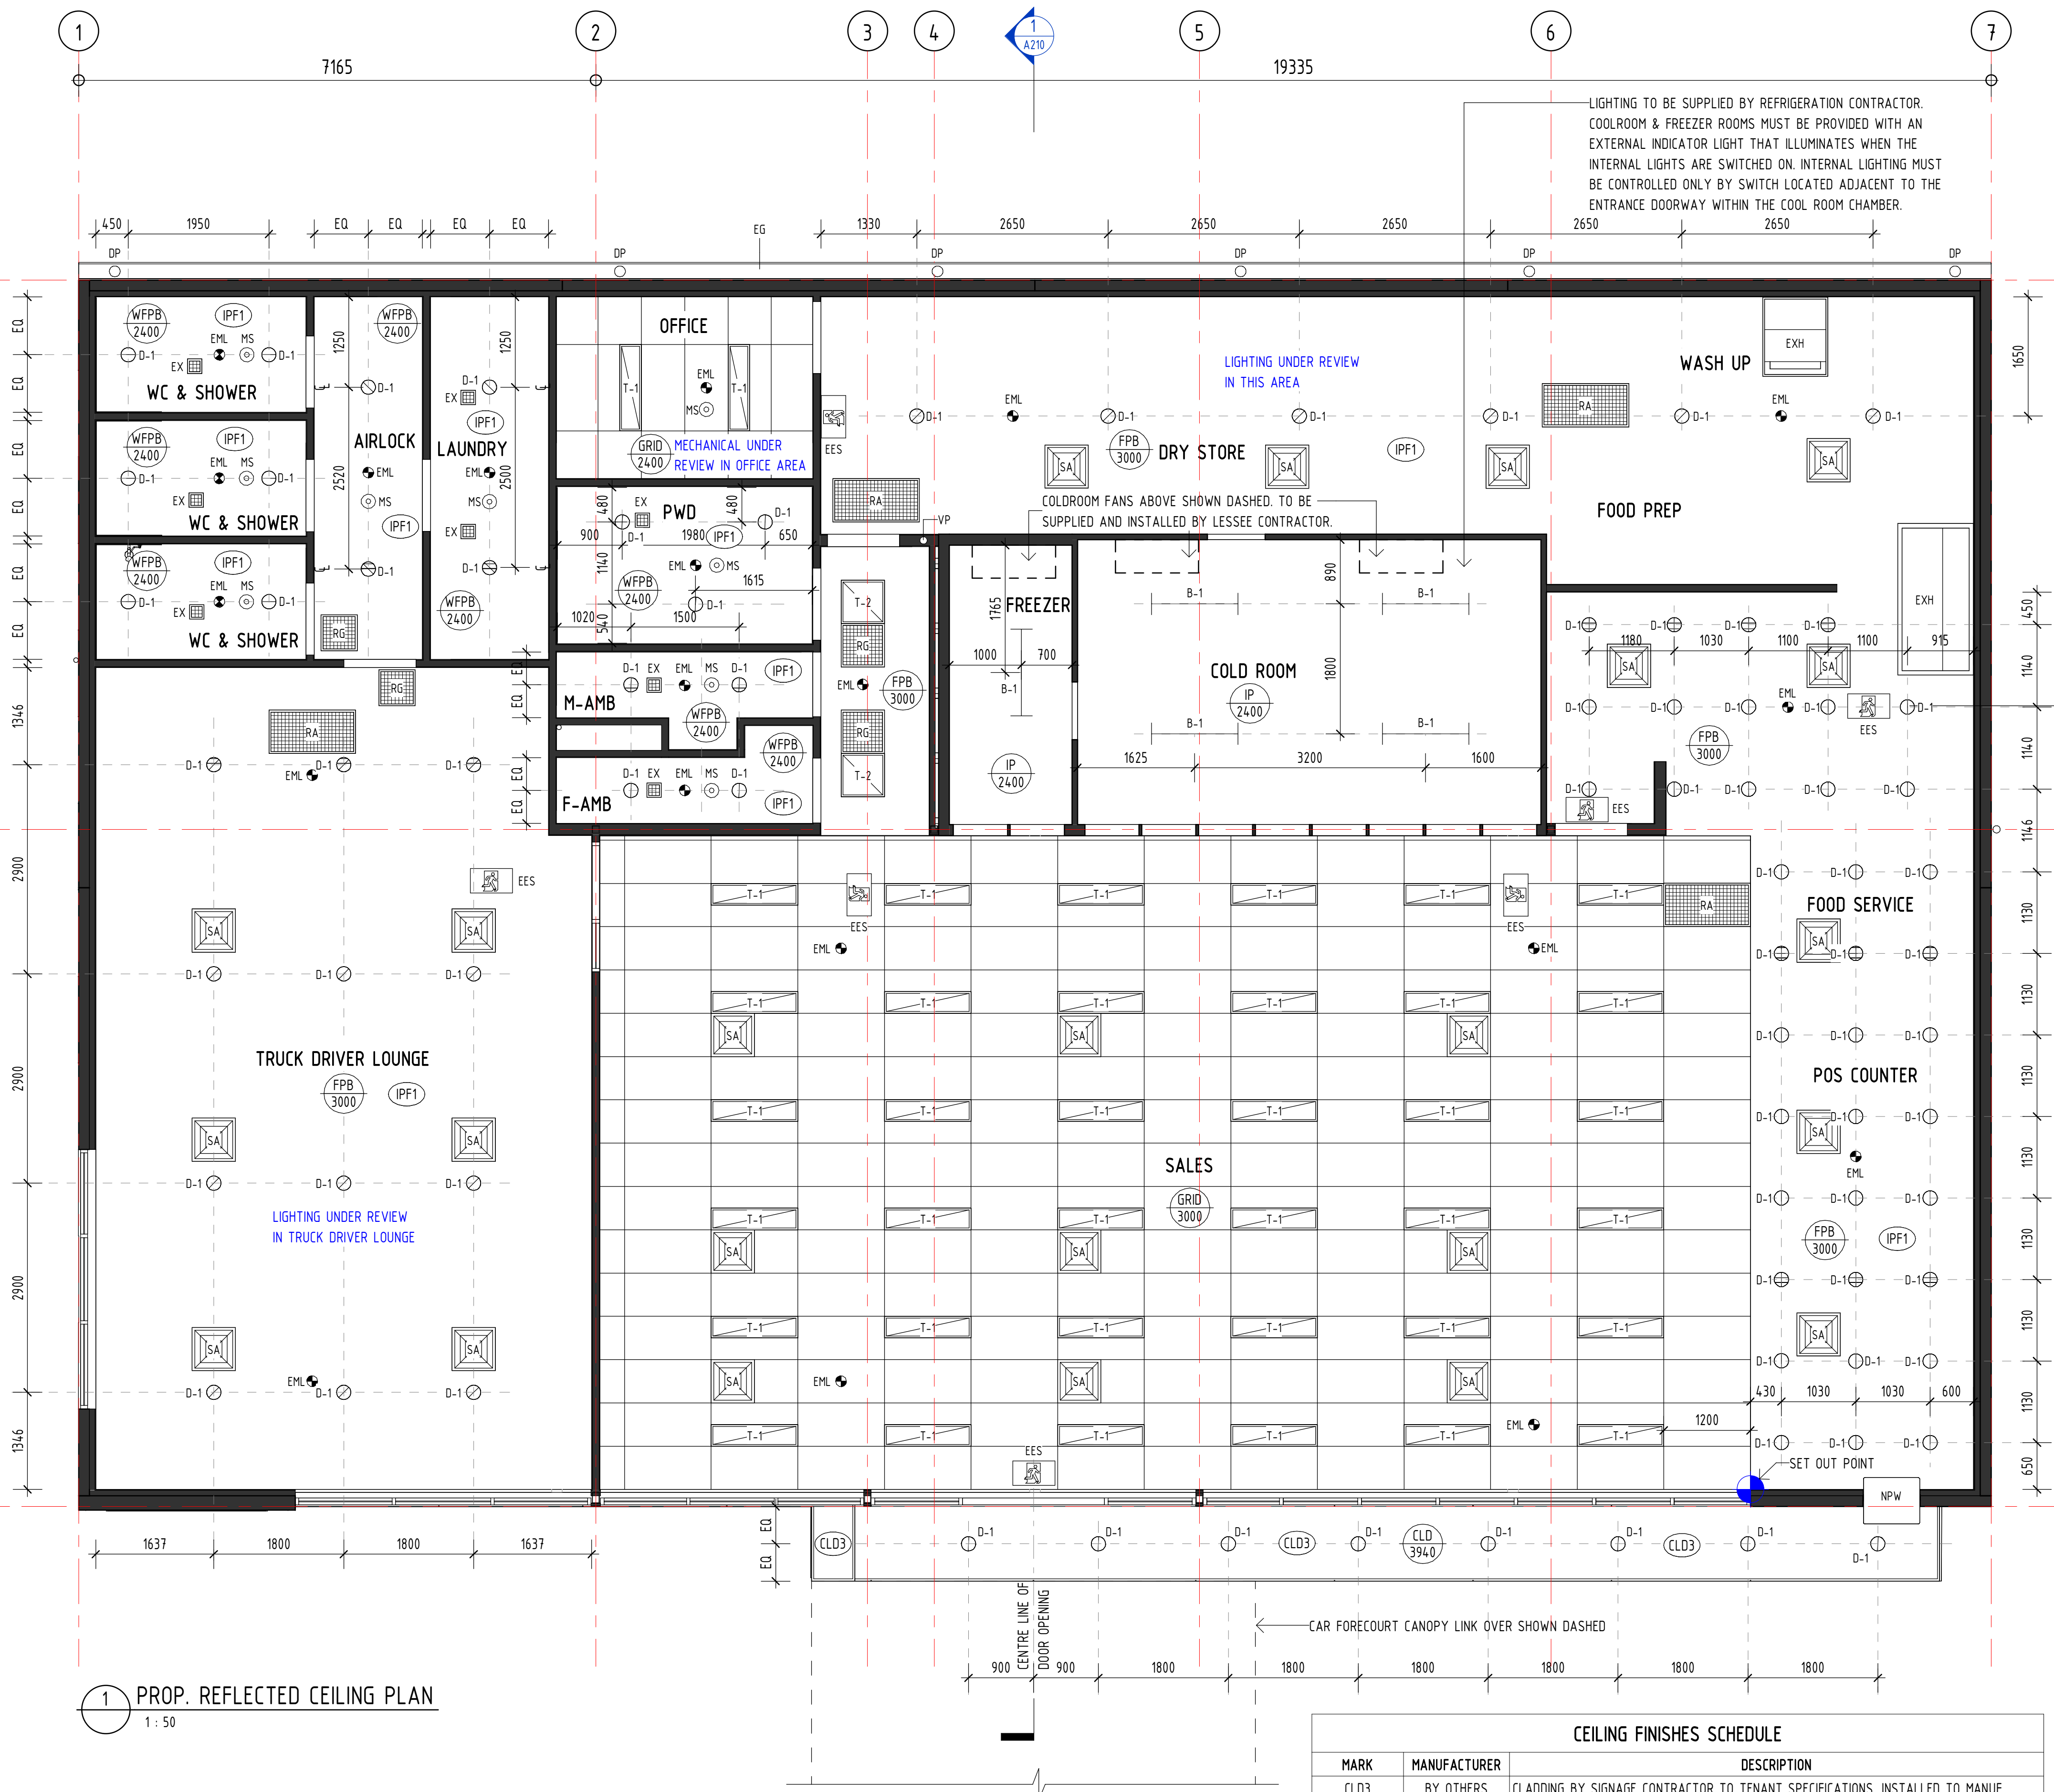

CEILING INSULATION REFER TO SECTION J REPORT FOR
DETAILS

GENERAL NOTES:

- DO NOT SCALE OFF THIS DRAWING.
- THE CONTRACTOR SHALL CARRY OUT A TRIAL SET-OUT OF ALL CEILING AND SOFFIT TYPES AND VERIFY WITH THE SUPERINTENDENT PRIOR TO CONSTRUCTION PROCEEDING.
- GENERALLY SET-OUT ROOMS FROM CENTRE LINE BETWEEN WALLS, WHERE NO SET-OUT SHOWN ASSUME CENTRAL SET-OUT.
- "equal" RELATES ONLY TO OPPOSING DIMENSION IN THAT DIMENSION LINE.
- CHECK ALL DIMENSIONS ON SITE WITHIN ROOMS PRIOR INSTALLATION OF FITTINGS. NOTIFY SUPERINTENDENT OF ANY DISCREPANCIES PRIOR PROCEEDING.
- CEILING HEIGHTS SHOWN ARE TAKEN FROM THE TOP OF THE CONC. FLOOR SLAB.
- FOR MECHANICAL AND ELECTRICAL EQUIPMENT TYPES AND MODELS, REFER TO ENGINEERS DRAWINGS.
- SET-OUT OF ALL ELECTRICAL AND MECHANICAL FIXTURES AND FITTINGS TO BE CONFIRMED ON SITE WITH THE SUPERINTENDENT PRIOR TO FRAMING, CUTTING ETC. OF THE CEILING LINING.
- ALL ELEMENTS IDENTIFIED IN AS1170.4 SECTION 8 ARE TO BE DESIGNED, SUPPLIED & INSTALLED BY THE BUILDER/ CONTRACTOR TO ENSURE COMPLIANCE WITH THE REQUIREMENTS OF AS1170.4.
- SEISMIC RESTRAINT SYSTEMS FOR SERVICES SHALL BE PROVIDED AS REQUIRED PER SECTION 8.1.4(b) OF AS1170.4.

LEGEND - REFLECTED CEILING PLAN

eg
WPB CEILING MATERIAL
2700 CEILING HEIGHT ABOVE CONC. SLAB LEVEL

MATERIAL:

IP INSULATED COLDROOM PANEL 100mm THICK
FPB FLUSHSET PLASTERBOARD
GRID VINYL FACED PLASTER TILE 600x1200
WFPB WET AREA FLUSHSET PLASTERBOARD
STP STRAMIT PREMIER 300 COLORBOND
CLADDING SURFMIST
CLD 'EYEBROW' CLADDING BY SIGNAGE CONTRACTOR TO TENANT SPECIFICATIONS. INSTALL TO MANUFACTURERS SPECIFICATIONS

CEILING FINISHES SCHEDULE				
MARK	MANUFACTURER	DESCRIPTION		
CLD3	BY OTHERS	CLADDING BY SIGNAGE CONTRACTOR TO TENANT SPECIFICATIONS. INSTALLED TO MANUF. SPEC. COLOUR: KEETON 'MARINE BLUE'		
IPF1	CONTRACTOR	13mm FLUSH-SET PLASTERBOARD CEILING LININGS WITH SQUARE SET EDGES TO WALLS		

VERVE SCHEDULES DISCLAIMER:

- ALL SCHEDULES SHOULD BE CHECKED WITH THE REMAINDER OF THE DRAWING SET.
- SCHEDULED RATES AND AREAS ARE INTENDED FOR ASSISTANCE ONLY. NO RESPONSIBILITY IS TAKEN FOR THE ACCURACY OF QUANTITIES.
- ANY DISCREPANCIES IN SCHEDULES SHOULD BE IDENTIFIED TO THE AUTHOR NOTED.
- ALL AREAS ARE GROSS AREAS, UNLESS NOTED OTHERWISE

CONSULTING ENGINEER




- ☐ commercial
- ☐ mixed-use
- ☐ self storage
- ☐ industrial
- ☐ service stations
- ☐ quick service restaurants
- ☐ child care centres
- ☐ large format retail

© 2011 copyright, all rights reserved.
This drawing is the © copyright & property of VERVE DESIGN GROUP and must not be used or duplicated without authorisation.
Do not scale this drawing.
Check all dimensions on site prior commencement of works

Revision and approvals				
Rev	Date	Drn	Description	Appr
P1	12.02.2026	PC	PRELIMINARY ISSUE	SS
P2	09.03.2026	PC	REVISED PRELIMINARY ISSUE	SS
P3	01.05.2026	PC	REVISED PRELIMINARY ISSUE	SS
A	19.06.2026	PC	BA ISSUE	SS

Project Description	
PROPOSED SERVICE STATION	
22 ENTERPRISE CCT., MARYBOROUGH W.	
Scale @A1 1 : 50	Date FEBRUARY 2026
Drawn PC	Approved By SS

Drawing Title	
PROP. REFLECTED CEILING PLAN	
Job Number - Drawing Number 26024	Revision A

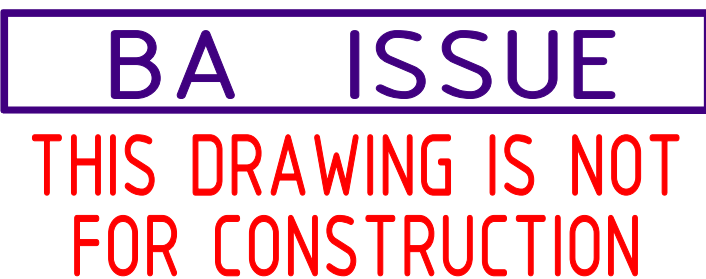


LEGEND

REFER SITE PLAN & CIVIL DRAWINGS FOR LEVELS
OUTSIDE BUILDING ENVELOPE

BFC	BROOM FINISH NATURAL GREY CONCRETE
STF	STEEL TROWEL FINISH NATURAL GREY CONCRETE
BLACK	BLACK CONCRETE HAND STIPPLE FINISH (NON-SLIP)
	CLOUR: CCS BLACK OXIDE 8% DOSAGE RATE
	SEALANT: NUTECH - PETROL RESISTANT
	PAVECOAT - PR210 BLACK COLOURED WITH
	NUTECH ANTI-SLIP ADDITIVE APPLIED AS PER
	MANUFACTURER'S INSTRUCTIONS.

Drawing Title
PROP. SLAB SETOUT PLAN

Job Number - Drawing Number	Revision
26024 A130	A

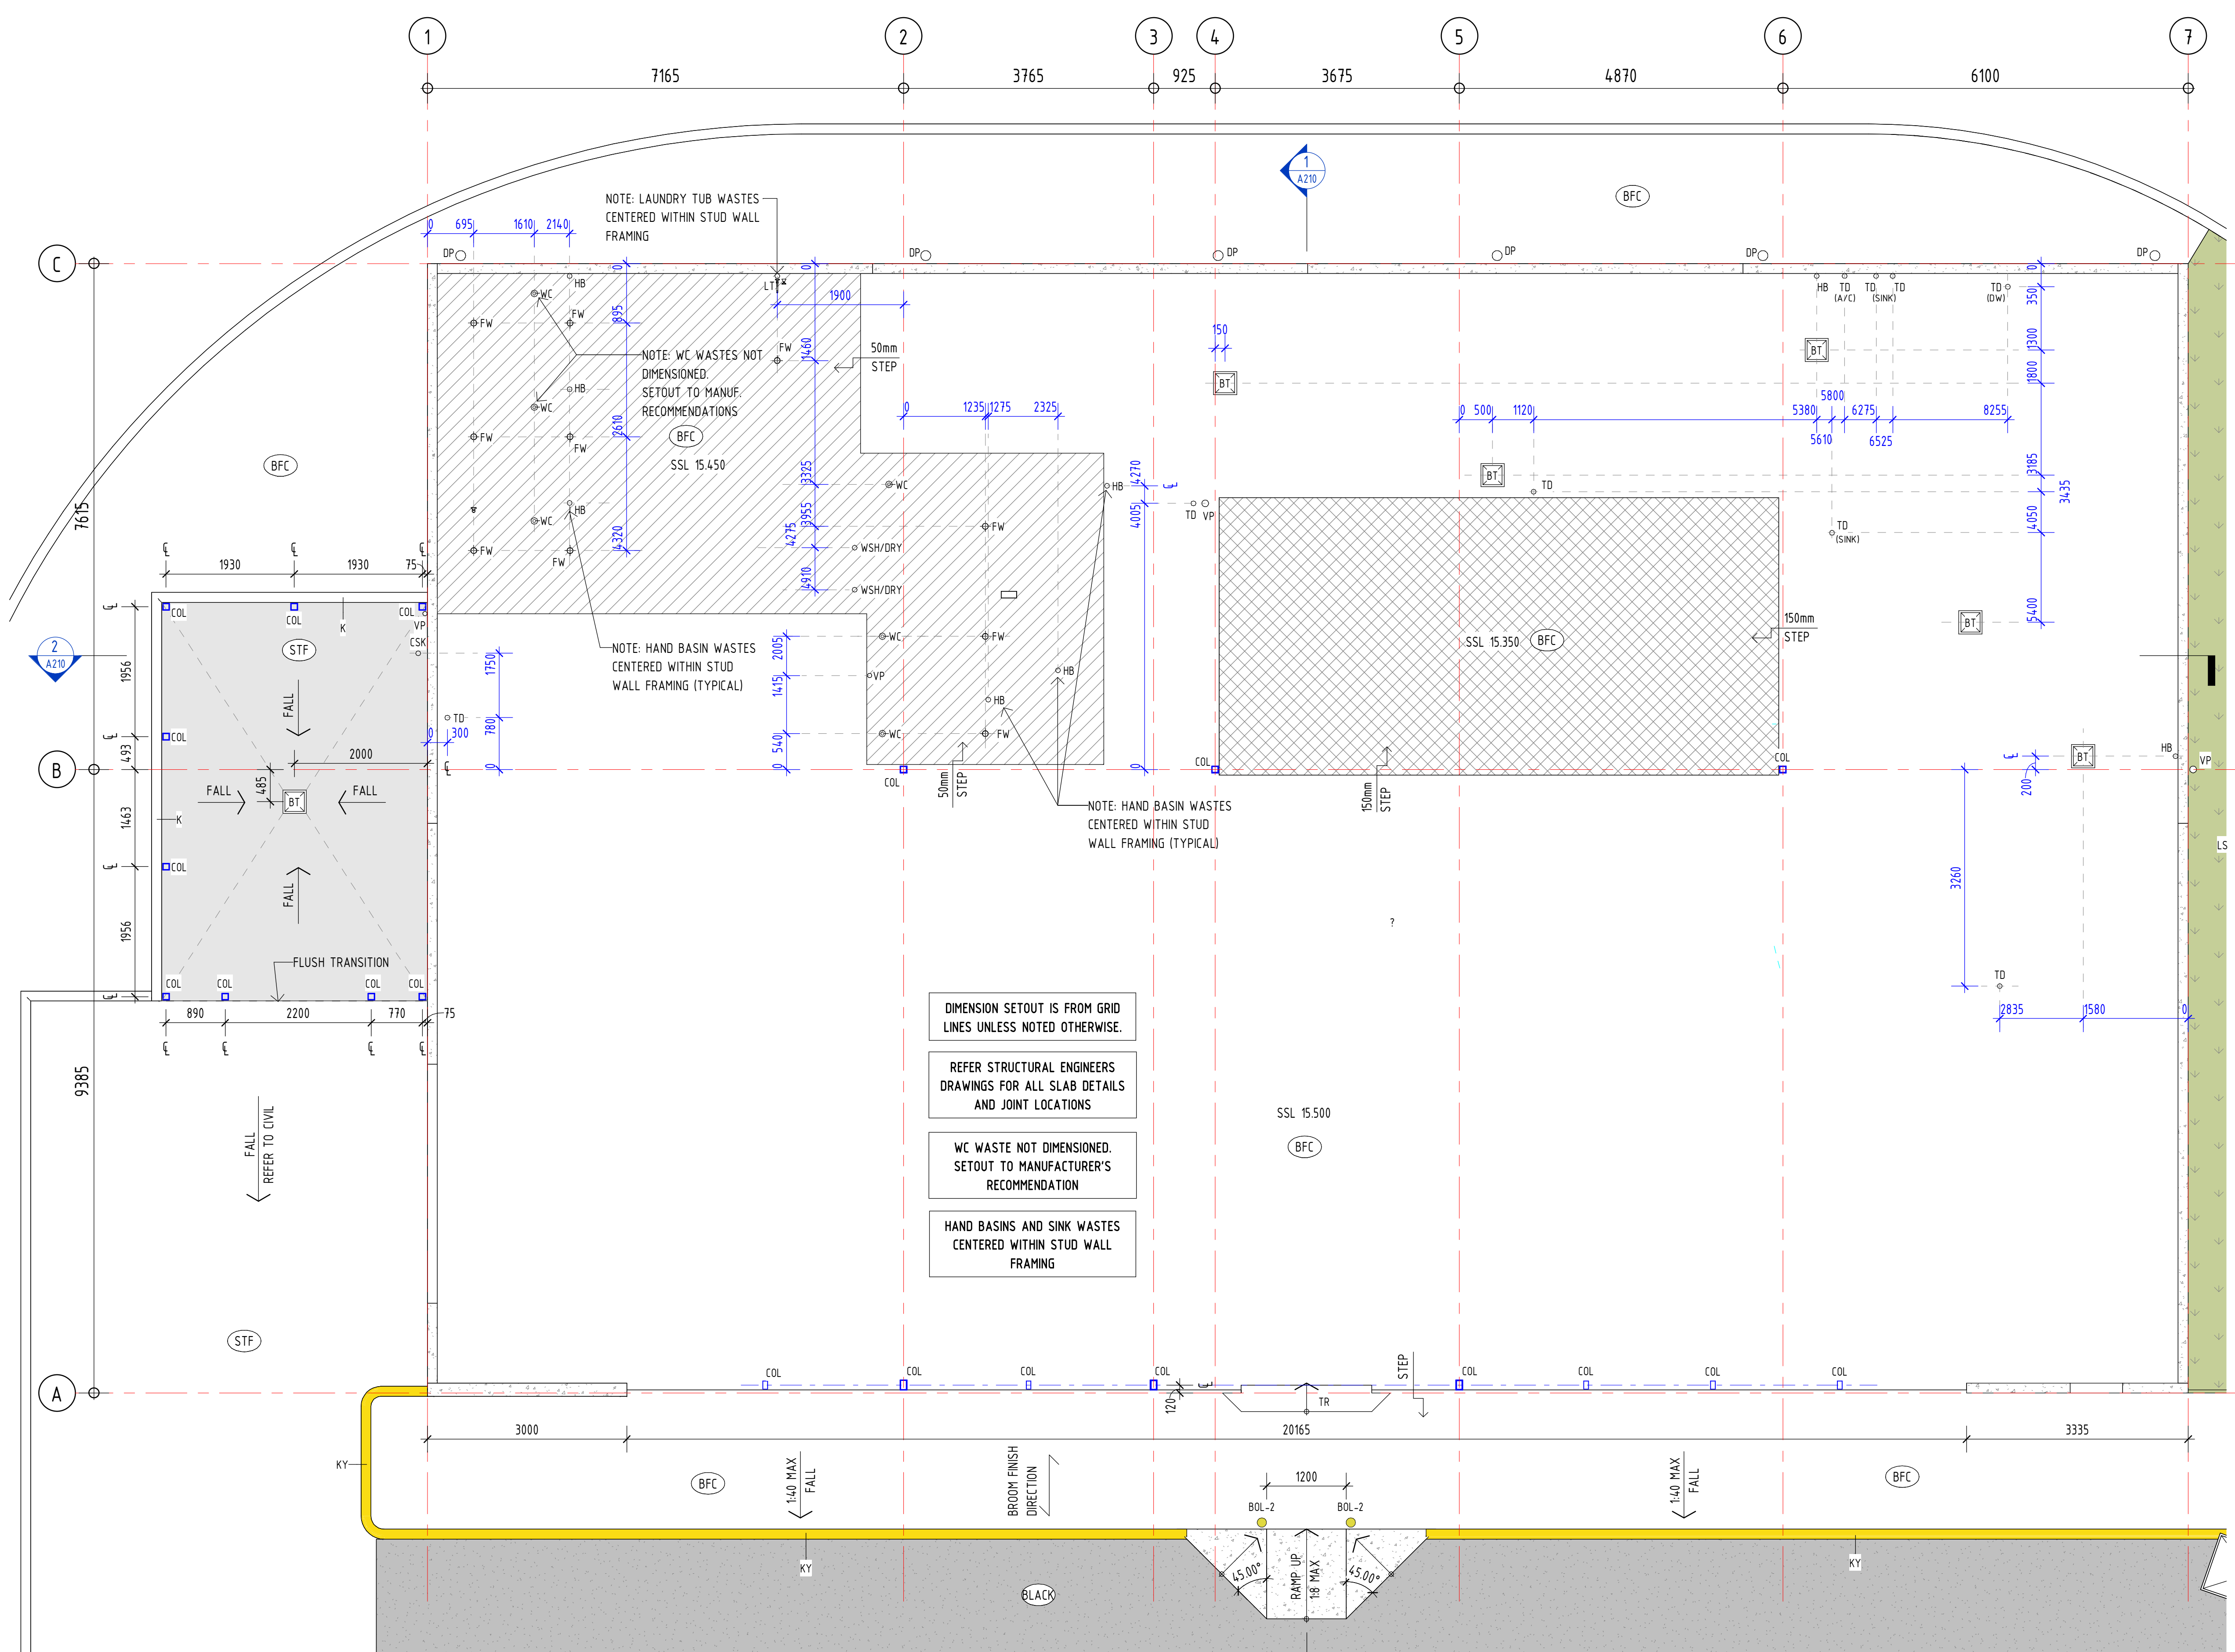

VERVE SCHEDULES DISCLAIMER:

1. ALL SCHEDULES SHOULD BE CHECKED WITH THE REMAINDER OF THE DRAWING SET.
2. SCHEDULED RATES AND AREAS ARE INTENDED FOR ASSISTANCE ONLY. NO RESPONSIBILITY IS TAKEN FOR THE ACCURACY OF QUANTITIES.
3. ANY DISCREPANCIES IN SCHEDULES SHOULD BE IDENTIFIED TO THE AUTHOR NOTED.
4. ALL AREAS ARE GROSS AREAS, UNLESS NOTED OTHERWISE

CONSULTING ENGINEER



- ☐ commercial
- ☐ mixed-use
- ☐ self storage
- ☐ industrial
- ☐ service stations
- ☐ quick service restaurants
- ☐ child care centres
- ☐ large format retail

© 2011 copyright, all rights reserved

This drawing is the © copyright & property of VERVE DESIGN GROUP and must not be used or duplicated without authorisation.

Do not scale this drawing.

Check all dimensions on site prior commencement of works

Revision and approvals				
Rev	Date	Drn	Description	App
P1	01.05.2026	PC	REVISED PRELIMINARY ISSUE	SS
A	19.06.2026	PC	BA ISSUE	SS


Project Description	PROPOSED SERVICE STATION
---------------------	--------------------------

22 ENTERPRISE CCT., MARYBOROUGH W.

Scale @ A1 1: 50	Date APRIL 2026
Drawn PC	Approved By SS

Drawing Title

PROP. SLAB SETOUT PLAN

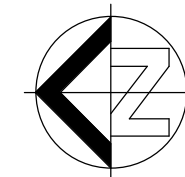


BA ISSUE

THIS DRAWING IS NOT
FOR CONSTRUCTION

LEGEND

BT	BUCKET TRAP - REFER HYD. ENG. DETAILS
COL	COLUMN - REFER STRUCT. ENG. DETAILS
DP	DOWNPIPE - REFER HYD. ENG. DETAILS
FT	ALUMINIUM FLOOR TRIM
FW	FLOOR WASTE - REFER HYD. ENG. DETAILS
TD	TUNDISH - REFER HYD. ENG. DETAILS
TR	1:8 LOCALISED DOOR THRESHOLD RAMP TO COMPLY WITH AS1428.1
VP	VENT PIPE - REFER HYD. ENG. DETAILS

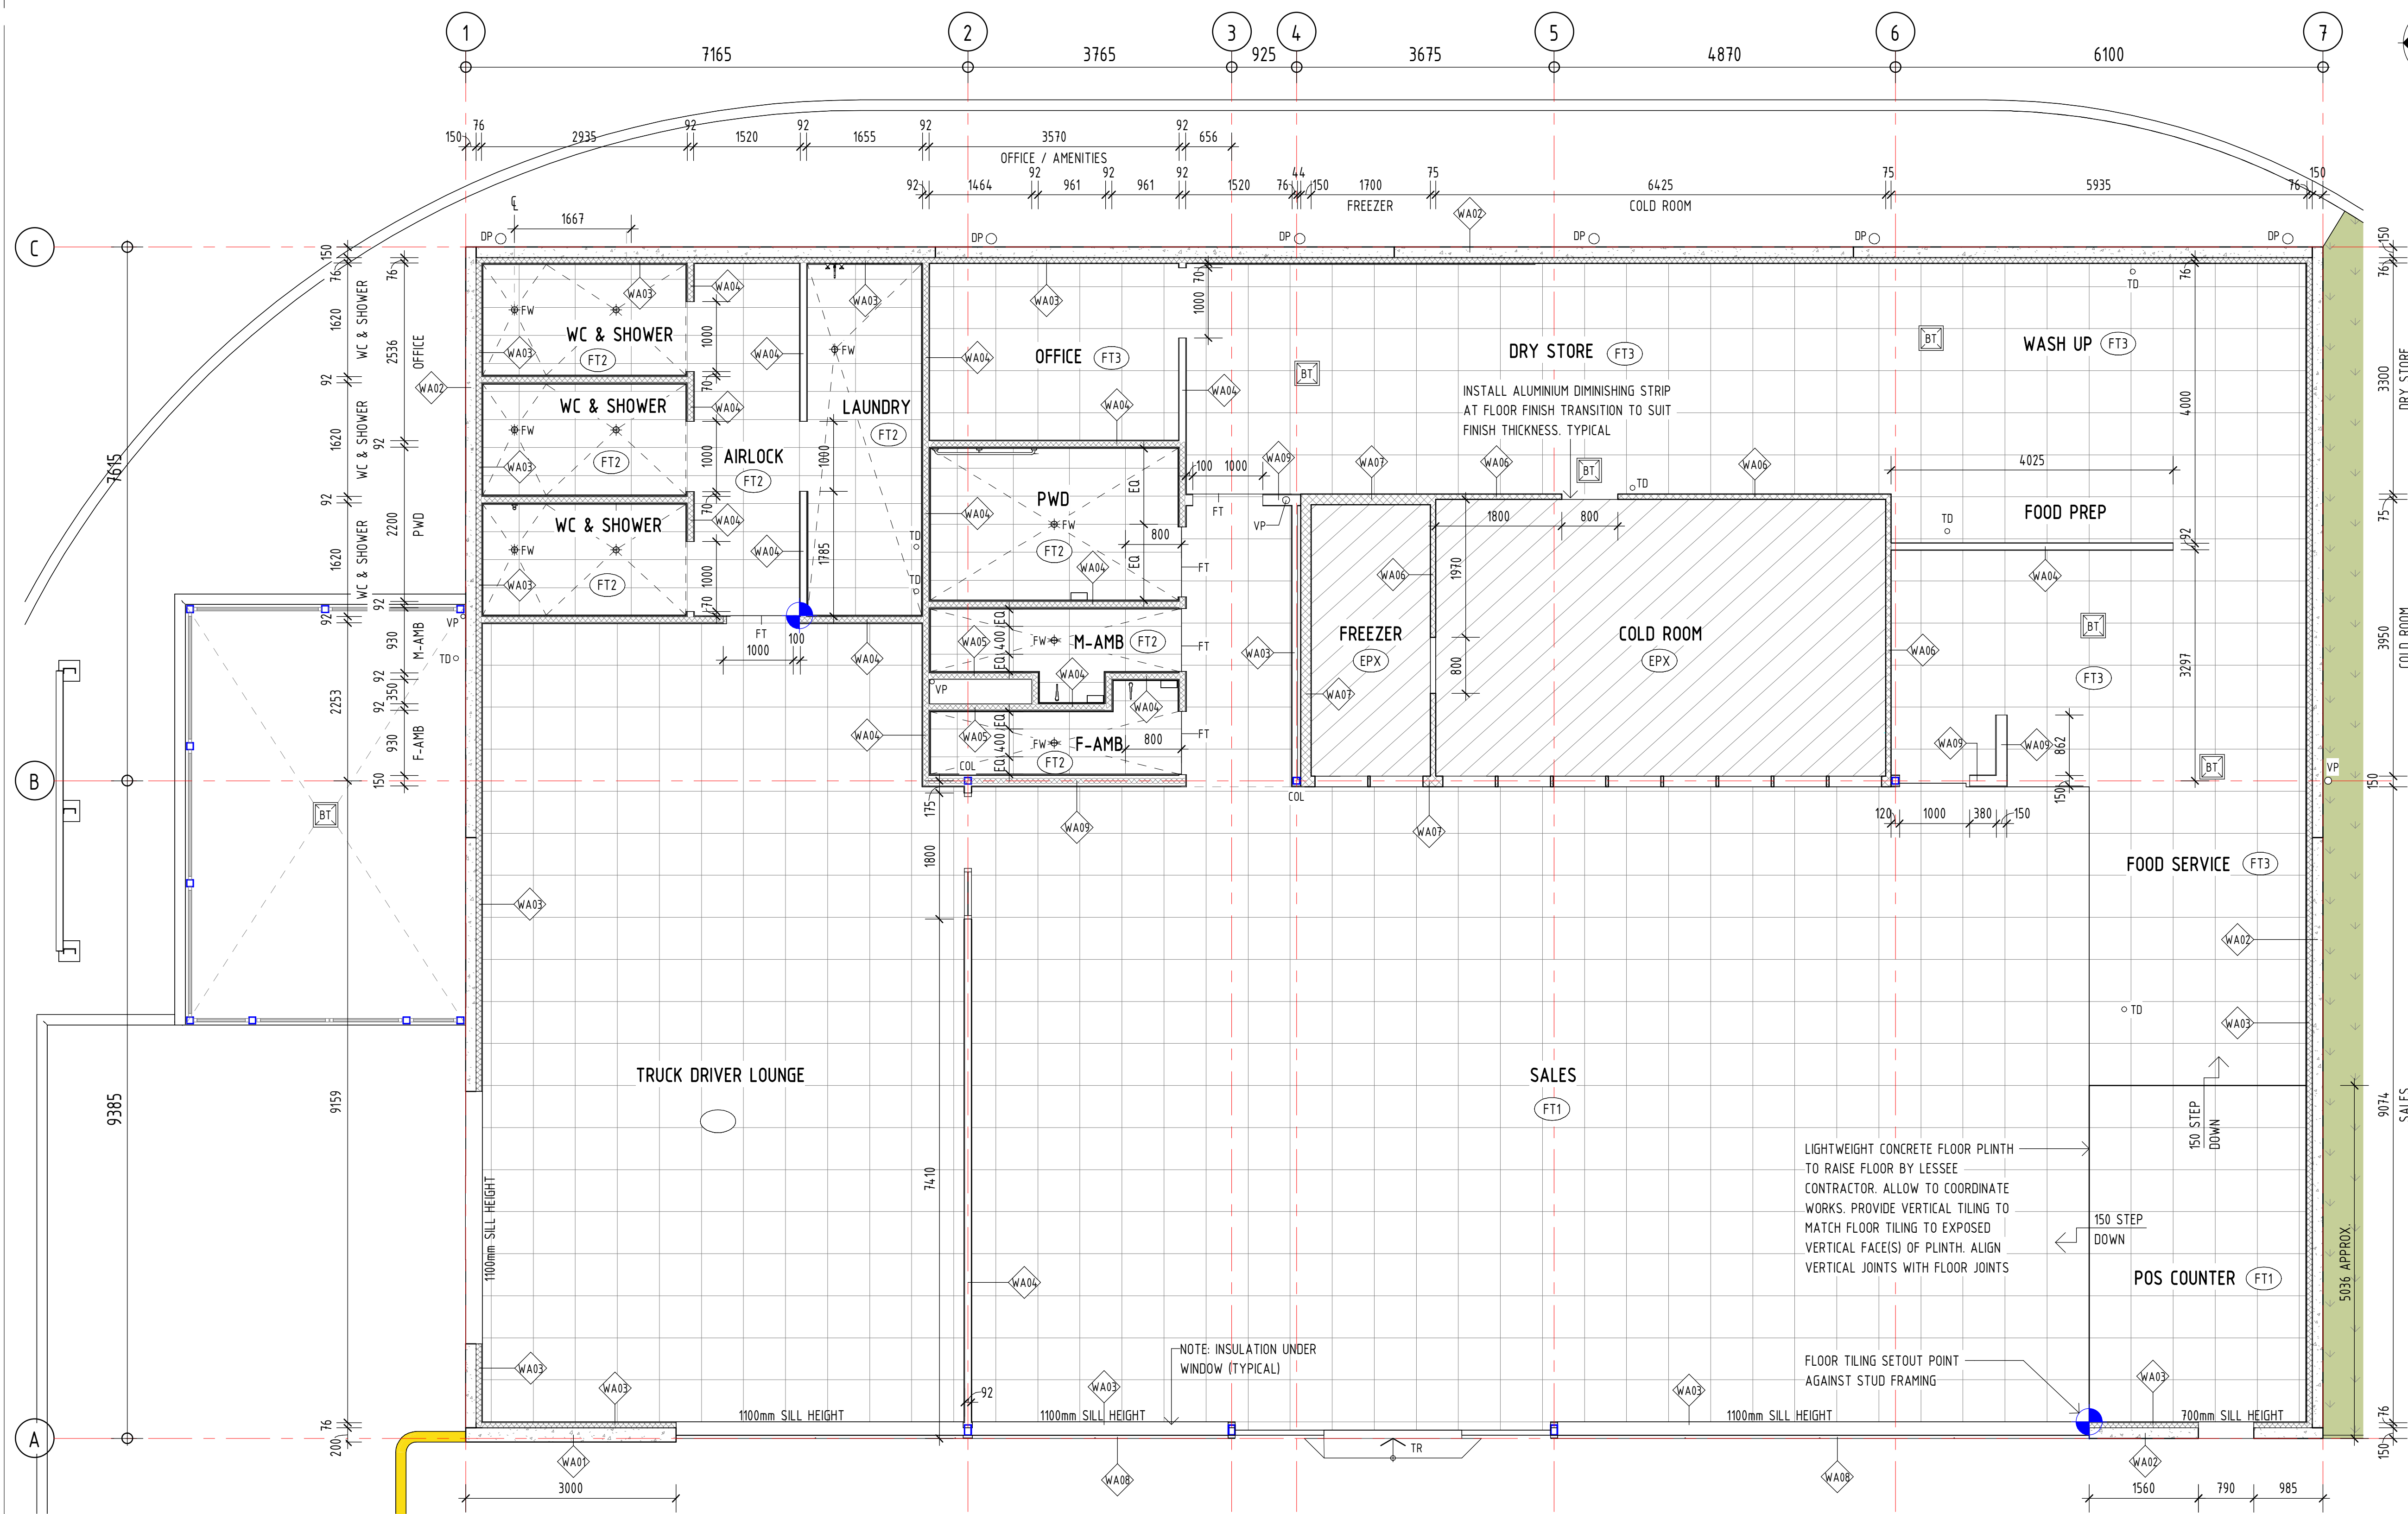

NOTE: ALL ELEMENTS IDENTIFIED IN AS1170.4 SECTION 8 ARE TO BE DESIGNED, SUPPLIED & INSTALLED BY THE BUILDER/ CONTRACTOR TO ENSURE COMPLIANCE WITH THE REQUIREMENTS OF AS1170.4 INCLUDING SEISMIC RESTRAINT SYSTEMS FOR SERVICES AS REQUIRED PER SECTION 8.1.4(b) OF AS1170.4

INTERNAL FINISHES SCHEDULE

MARK	MANUFACTURER	DESCRIPTION	COMMENTS
EPX	ALLNEX	NUTHANE SB POLYURETHANE: MID GREY	MIN. R12 SLIP RATING. 100mm HIGH COVING TO WALL
FT1	AMBER TILES LIVERPOOL	FLOOR TILE - 600x600 "DURA GREY"	100mm ALUMINIUM SKIRTING - ARMOURSPRAY BLACK SATIN: 9109024S. R11 SLIP RATING. GROUT: GREY.
FT2	AMBER TILES LIVERPOOL	FLOOR TILE - 800x400 "STOCKTON WHITE". PRODUCT CODE: AAC84ACD0DR.	R10 SLIP RATING. GROUT: GREY.
FT3	AMBER TILES LIVERPOOL	FLOOR TILE - 600x600 "DURA GREY"	MIN. R12 SLIP RATING. GROUT: GREY EPOXY. 100mm ALUMINIUM SKIRTING - ARMOURSPRAY BLACK SATIN: 9109024S
IPF2	TAUBMANS	INTERIOR PAINT FINISH - 'CRISP WHITE' LOW SHEEN.	APPLIED TO INTERNAL WALLS.
IPF3	TAUBMANS	SEMI-GLOSS PAINT FINISH: SEALORD T15 25.5	INTERNAL DOORS
L1	LAMINEX	CLOUR: GUNMETAL FINISH: NATURAL	TOILET PARTITION - PREFABRICATED 19mm MOISTURE RESISTANT LAMINATED BOARD EDGES SHALL BE TREATED WITH HEAVY DUTY PVC EDGE STRIPS
WT1	AMBER TILES LIVERPOOL	WALL TILE - 800x400 "STOCKTON WHITE". PRODUCT CODE: AAC84ACD0DR.	GROUT: GREY.
WT2	COLORTILE	WALL TILE - 280x70 "DARK NIGHT SUNSET MATT" - WHITE GROUT.	GROUT: ARDEX EG15 WHITE. 5mm JOINTS

WALL TYPE SCHEDULE

MARK	DESCRIPTION	COMMENTS
WA01	200mm PRE-CAST CONCRETE WALL PANELS	REFER STRUCTURAL ENGINEERS DRAWINGS. REFER WEATHERPROOFING REPORT.
WA02	150mm PRE-CAST CONCRETE WALL PANELS	REFER STRUCTURAL ENGINEERS DRAWINGS. REFER WEATHERPROOFING REPORT.
WA03	76mm METAL STUD WALL FRAMING WITH 1 LAYER 10mm PLASTERBOARD TO ONE SIDE	9mm VILLABOARD TO WET AREAS & 9mm FC TO STORE ROOM. MIN R2.0 24 kg/m ³ BATT INSULATION TO COMPLY WITH SECTION J
WA04	92mm METAL STUD WALL FRAMING WITH 1 LAYER OF 10mm PLASTERBOARD TO BOTH SIDES	9mm VILLABOARD TO WET AREAS & 9mm FC TO STORE ROOM. MIN R1.4 24kg/m ³ BATT INSULATION.
WA05	92mm METAL STUD WALL FRAMING WITH 1 LAYER 13mm PLASTERBOARD TO ONE SIDE	BY MANUFACTURER.
WA06	75mm INSULATED COLDROOM PANEL	BY MANUFACTURER.
WA07	150mm INSULATED COLDROOM PANEL	BY MANUFACTURER.
WA08	150 METAL STUD WALL FRAMING WITH 35mm TOP HAT SECTION WITH 9mm FIBRE CEMENT SHEETING	
WA09	150mm METAL STUD WALL FRAMING WITH 1 LAYER OF 10mm PLASTERBOARD TO BOTH SIDES	9mm VILLABOARD TO WET AREAS & 9mm FC TO STORE ROOM. MIN R1.4 24kg/m ³ BATT INSULATION.

- VERVE SCHEDULES DISCLAIMER:**
- ALL SCHEDULES SHOULD BE CHECKED WITH THE REMAINDER OF THE DRAWING SET.
 - SCHEDULED RATES AND AREAS ARE INTENDED FOR ASSISTANCE ONLY. NO RESPONSIBILITY IS TAKEN FOR THE ACCURACY OF QUANTITIES.
 - ANY DISCREPANCIES IN SCHEDULES SHOULD BE IDENTIFIED TO THE AUTHOR NOTED.
 - ALL AREAS ARE GROSS AREAS, UNLESS NOTED OTHERWISE

CONSULTING ENGINEER



- ☐ commercial
- ☐ mixed-use
- ☐ self storage
- ☐ industrial
- ☐ service stations
- ☐ quick service restaurants
- ☐ child care centres
- ☐ large format retail

© 2011 copyright, all rights reserved.

This drawing is the © copyright & property of VERVE DESIGN GROUP and must not be used or duplicated without authorisation.


Do not scale this drawing.

Check all dimensions on site prior commencement of works

Revision and approvals				
Rev	Date	Drn	Description	Appr
P1	01.05.2026	PC	REVISED PRELIMINARY ISSUE	SS
A	19.06.2026	PC	BA ISSUE	SS

Project Description	
PROPOSED SERVICE STATION	
22 ENTERPRISE CCT., MARYBOROUGH W.	
Scale @A1 1: 50	Date APRIL 2026
Drawn PC	Approved By SS


Drawing Title	
PROP. FLOOR FINISHES & PORTIONS PLAN	
Job Number - Drawing Number 26024	Revision A

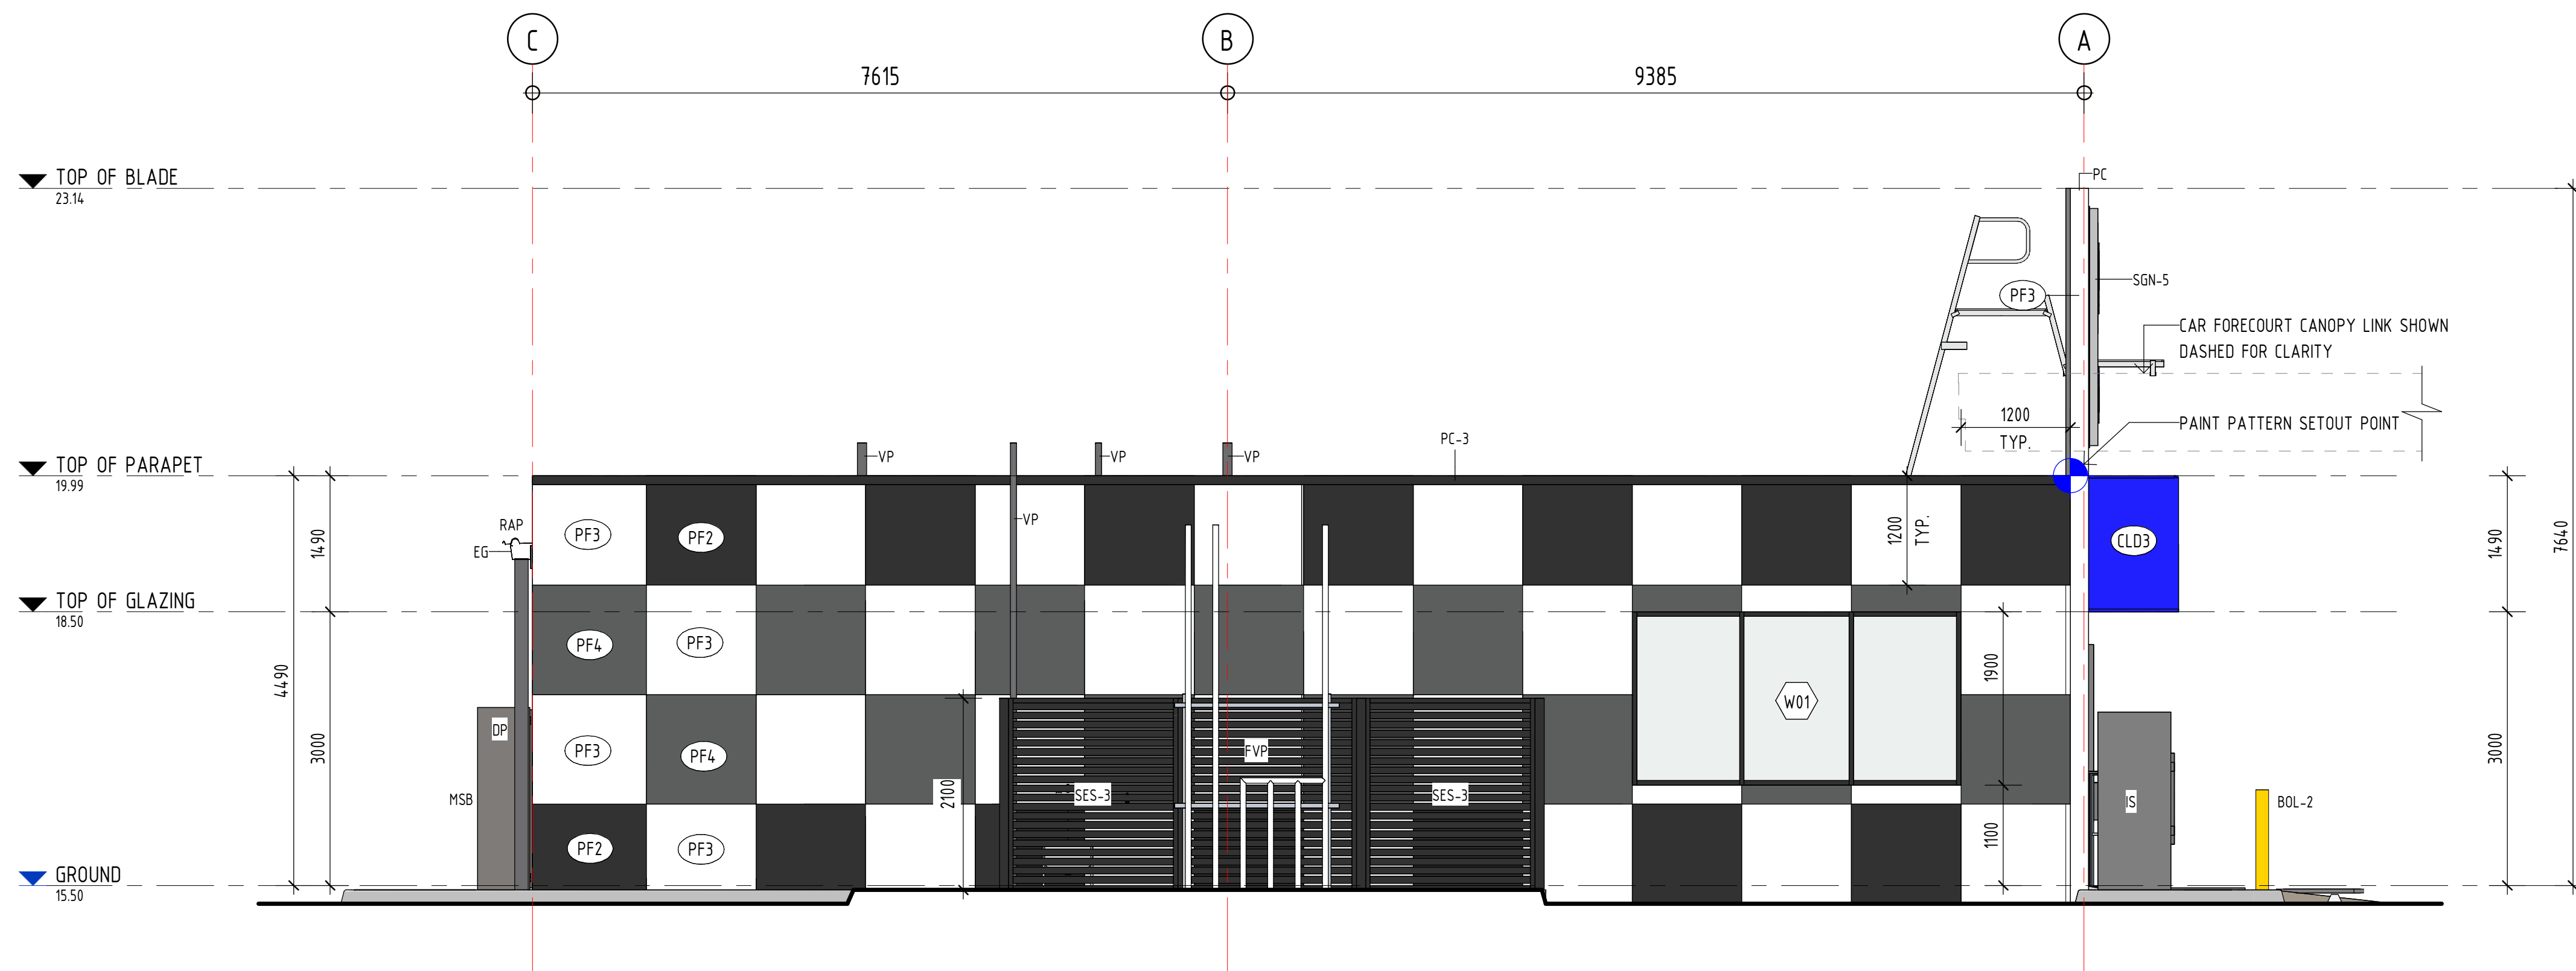

1 BUILDING ELEVATION NORTH
1 : 50

LEGEND	
ARB	ARMCO VEHICLE BARRIER - REFER TO CIVIL ENG. FOR DETAILS
BOL-2	STEEL BOLLARD TYPE 2 - REFER DETAIL
COL	COLUMN - REFER STRUCT. ENG. DETAILS
DP	DOWNPIPE - REFER HYD. ENG. DETAILS
EG	EAVES GUTTER - REFER HYD. ENG. DETAILS
FES	FUEL EMERGENCY STOP BUTTON - REFER FUEL ENG. DETAILS
FVP	FUEL/SPEL VENT PIPES - REFER FUEL ENG. DETAILS
IS	ICE STORAGE - SUPPLIED & INSTALLED BY LESSEE
LPG	LPG CYLINDER STORAGE - SUPPLIED & INSTALLED BY LESSEE
MSB	ELECTRICAL MAIN SWITCHBOARD - REFER ELEC. ENG. DETAILS
NPW	NIGHT PAY WINDOW - STERLING
PC	PARAPET CAPPING. REFER ELEVATIONS FOR COLOUR
PC-3	PARAPET CAPPING. COLOUR: COLORBOND MONUMENT
RAP	SURFACE MOUNT ROOF ACCESS POINT LADDER SUPPORT BRACKET INSTALLED TO MAN. SPEC.
SES-3	STRATCO EZI-SLAT ALUMINIUM SCREENING - 75mm SLATS - 25mm GAP. COLOUR MONUMENT
SGN-3	ILLUMINATED SHOPFRONT RETAILER SIGNAGE SUPPLIED & INSTALLED BY LESSEE CONTRACTOR. BUILDER TO PROVIDE POWER SERVICE
SGN-4	ILLUMINATED SHOPFRONT LOCATION SIGNAGE SUPPLIED & INSTALLED BY LESSEE CONTRACTOR. BUILDER TO PROVIDE POWER SERVICE
SGN-5	ILLUMINATED BLADE RETAILER SIGNAGE SUPPLIED & INSTALLED BY LESSEE CONTRACTOR. BUILDER TO PROVIDE POWER SERVICE
VP	VENT PIPE - REFER HYD. ENG. DETAILS

EXTERNAL FINISHES SCHEDULE			
MARK	MANUFACTURER	DESCRIPTION	COMMENTS
CLD1	BY OTHERS	ALUCOBOND PLUS ON 35mm TOP HATS BY SIGNAGE CONTRACTOR TO TENANT SPECIFICATIONS. COLOUR: 'WHITE 16'	
CLD2	JAMES HARDIE	9mm EXPRESSED JOINT FC CLADDING ON 35mm PROPRIETARY BATTEN SYSTEM	PAINT FINISH: PF4
CLD3	BY OTHERS	CLADDING BY SIGNAGE CONTRACTOR TO TENANT SPECIFICATIONS. INSTALLED TO MANUF. SPEC. COLOUR: KEETON 'MARINE BLUE'	
PF1	DULUX	PAINT FINISH. COLOUR "WOODLAND GREY" C23	
PF2	DULUX	PAINT FINISH. COLOUR "COLORBOND MONUMENT" C29	
PF3	DULUX	PAINT FINISH. COLOUR: 'WHITE ON WHITE' SW	EXTERIOR
PF4	DULUX	PAINT FINISH. COLOUR "COLORBOND BASALT" C30	
VN2	BY OTHERS	VINYL. COLOUR: 'MOBIL BLUE' BY SIGNAGE CONTRACTOR TO TENANT SPECIFICATIONS. INSTALLED TO MANUF. SPEC.	

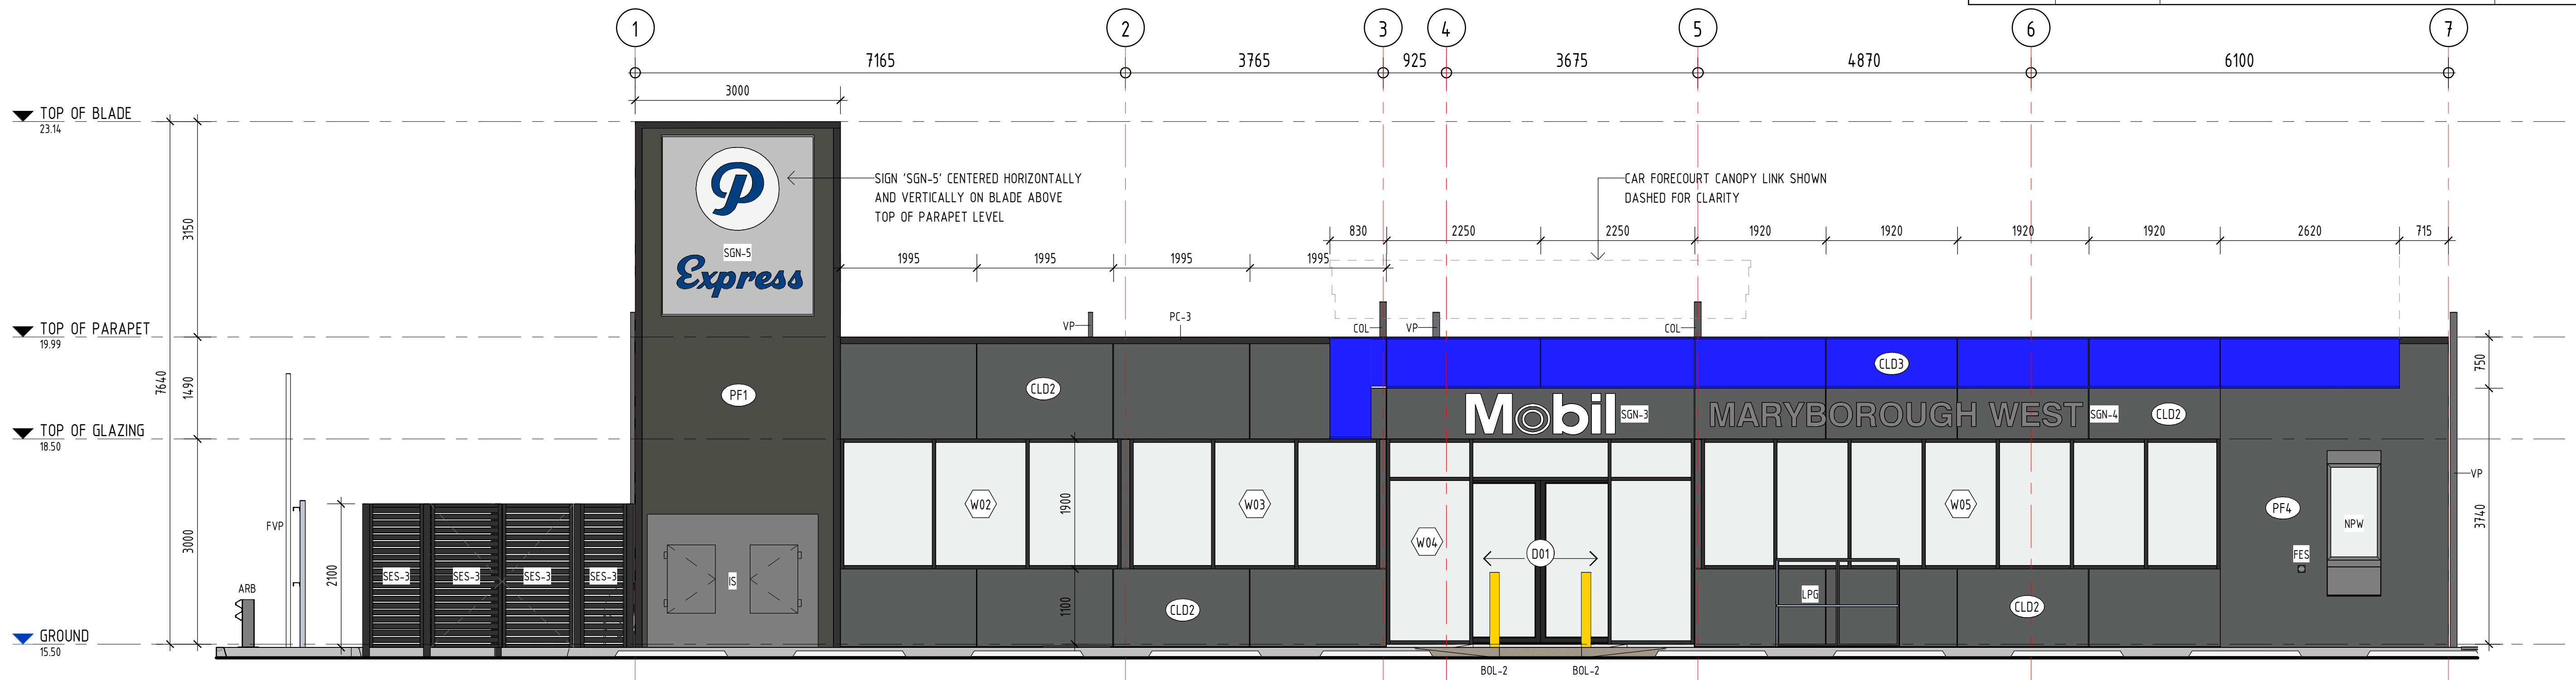

2 BUILDING ELEVATION WEST
1 : 50

VERVE SCHEDULES DISCLAIMER:

- ALL SCHEDULES SHOULD BE CHECKED WITH THE REMAINDER OF THE DRAWING SET.
- SCHEDULED RATES AND AREAS ARE INTENDED FOR ASSISTANCE ONLY. NO RESPONSIBILITY IS TAKEN FOR THE ACCURACY OF QUANTITIES.
- ANY DISCREPANCIES IN SCHEDULES SHOULD BE IDENTIFIED TO THE AUTHOR NOTED.
- ALL AREAS ARE GROSS AREAS, UNLESS NOTED OTHERWISE

CONSULTING ENGINEER



- commercial
- mixed-use
- self storage
- industrial
- service stations
- quick service restaurants
- child care centres
- large format retail

© 2011 copyright, all rights reserved.
This drawing is the © copyright & property of VERVE DESIGN GROUP and must not be used or duplicated without authorisation.
Do not scale this drawing.
Check all dimensions on site prior commencement of works

Revision and approvals				
Rev	Date	Drn	Description	Appr
P1	12.02.2026	PC	PRELIMINARY ISSUE	SS
P2	09.03.2026	PC	REVISED PRELIMINARY ISSUE	SS
P3	01.05.2026	PC	REVISED PRELIMINARY ISSUE	SS
A	19.06.2026	PC	BA ISSUE	SS

Project Description	
PROPOSED SERVICE STATION	
22 ENTERPRISE CCT., MARYBOROUGH W.	
Scale @A1 1 : 50	Date FEBRUARY 2026
Drawn PC	Approved By SS


Drawing Title	
PROP. BUILDING ELEVATIONS	
Job Number - Drawing Number	Revision
26024 A200	A

THIS DRAWING IS NOT
FOR CONSTRUCTION


EXTERNAL FINISHES SCHEDULE			
MARK	MANUFACTURER	DESCRIPTION	COMMENTS
CLD1	BY OTHERS	ALUCOBOND PLUS ON 35mm TOP HATS BY SIGNAGE CONTRACTOR TO TENANT SPECIFICATIONS. COLOUR: 'WHITE 16'	
CLD2	JAMES HARDIE	9mm EXPRESSED JOINT FC CLADDING ON 35mm PROPRIETARY BATTEN SYSTEM	PAINT FINISH: PF4
CLD3	BY OTHERS	CLADDING BY SIGNAGE CONTRACTOR TO TENANT SPECIFICATIONS. INSTALLED TO MANUF. SPEC. COLOUR: KEETON 'MARINE BLUE'	
PF1	DULUX	PAINT FINISH. COLOUR "WOODLAND GREY" C23	
PF2	DULUX	PAINT FINISH. COLOUR "COLORBOND MONUMENT" C29	
PF3	DULUX	PAINT FINISH. COLOUR: 'WHITE ON WHITE' 5W	EXTERIOR
PF4	DULUX	PAINT FINISH. COLOUR "COLORBOND BASALT" C30	
VN2	BY OTHERS	VINYL. COLOUR: 'MOBIL BLUE' BY SIGNAGE CONTRACTOR TO TENANT SPECIFICATIONS. INSTALLED TO MANUF. SPEC.	



Drawing Title		
PROP. BUILDING ELEVATIONS		
Job Number - Drawing Number		Revision
26024	A201	A

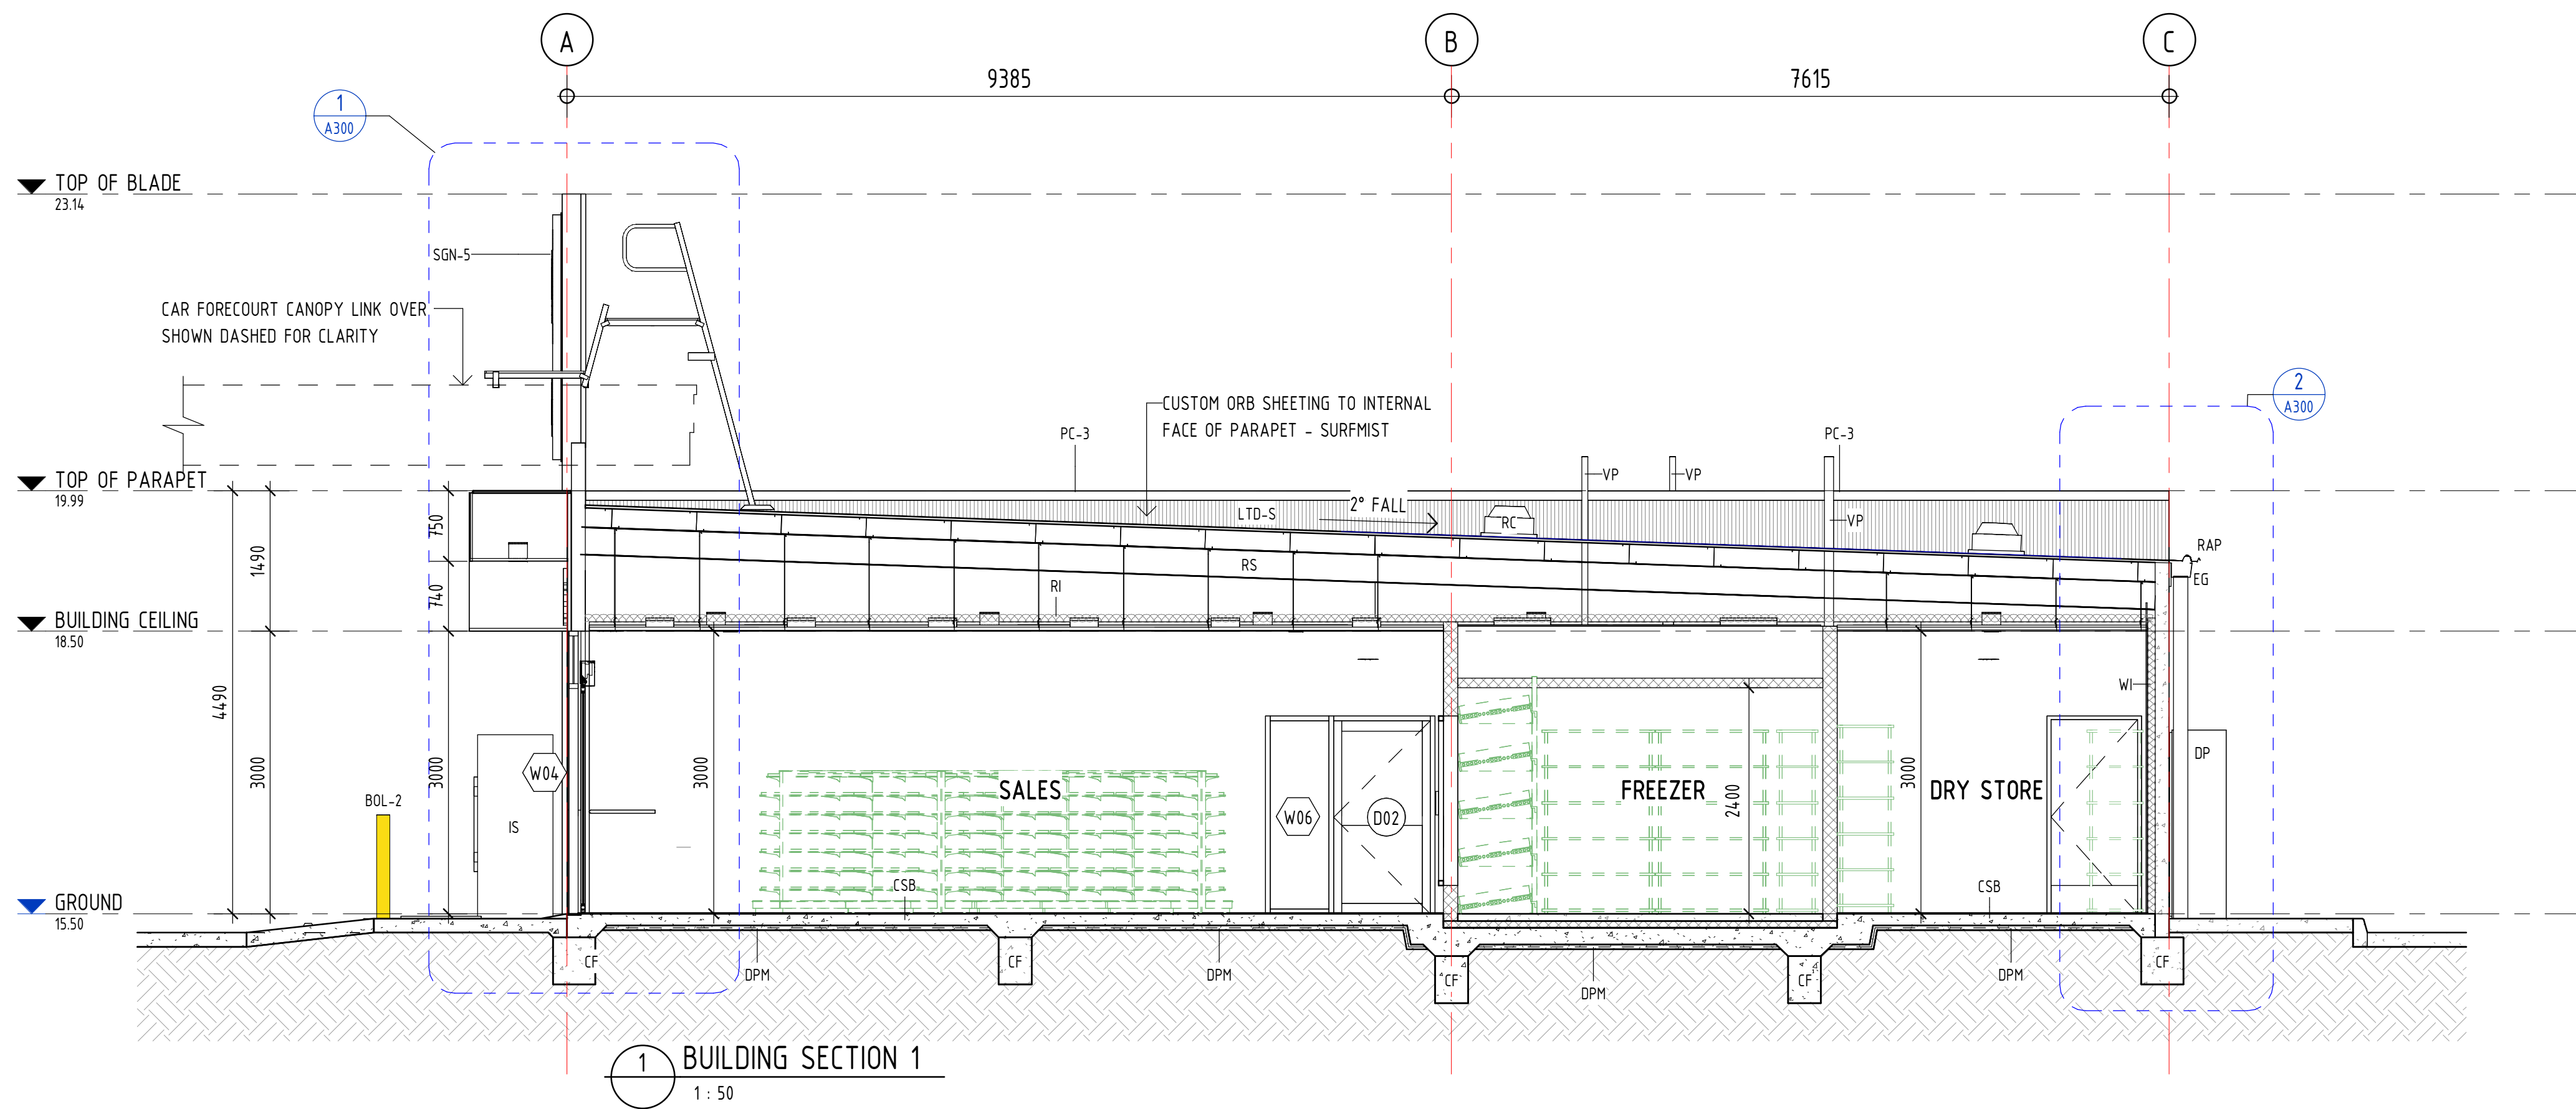

LEGEND	
BOL-2	STEEL BOLLARD TYPE 2 - REFER DETAIL
CBF-2	COLORBOND FLASHING - COLOUR SURFMIST
CF	CONCRETE FOOTING - REFER STRUCT. ENG. DETAILS
CSB	CONCRETE SLAB - REFER STRUCT. ENG. DETAILS
CSK	CLEANERS SINK WITH STAINLESS STEEL COVER - REFER HYD. ENG. DETAILS
CTM	CLEANERS TAP MIXER
DP	DOWNPIPE - REFER HYD. ENG. DETAILS
DPM	DAMP PROOF MEMBRANE
EG	EAVES GUTTER - REFER HYD. ENG. DETAILS
HT	HOSECOCK TAP CONNECTION - REFER HYD. ENG. DETAILS
IS	ICE STORAGE - SUPPLIED & INSTALLED BY LESSEE
LTD-S	LYSAGHT TRIMDEK 0.48BMT COLORBOND SURFMIST
PC	PARAPET CAPPING. REFER ELEVATIONS FOR COLOUR
PC-3	PARAPET CAPPING. COLOUR: COLORBOND MONUMENT
RAP	SURFACE MOUNT ROOF ACCESS POINT LADDER SUPPORT BRACKET INSTALLED TO MAN. SPEC.
RC	ROOF COWL - REFER MECH. ENG. DETAILS
RI	ROOF INSULATION - TO COMPLY WITH ENERGY EFFICIENCY REPORT
RS	ROOF STRUCTURE - REFER STRUCT. ENG. DETAILS
SES-3	STRATCO EZI-SLAT ALUMINIUM SCREENING - 75mm SLATS - 25mm GAP. COLOUR MONUMENT
SGN-5	ILLUMINATED BLADE RETAILER SIGNAGE SUPPLIED & INSTALLED BY LESSEE CONTRACTOR. BUILDER TO PROVIDE POWER SERVICE
VP	VENT PIPE - REFER HYD. ENG. DETAILS
WI	WALL INSULATION - TO COMPLY WITH ENERGY EFFICIENCY REPORT

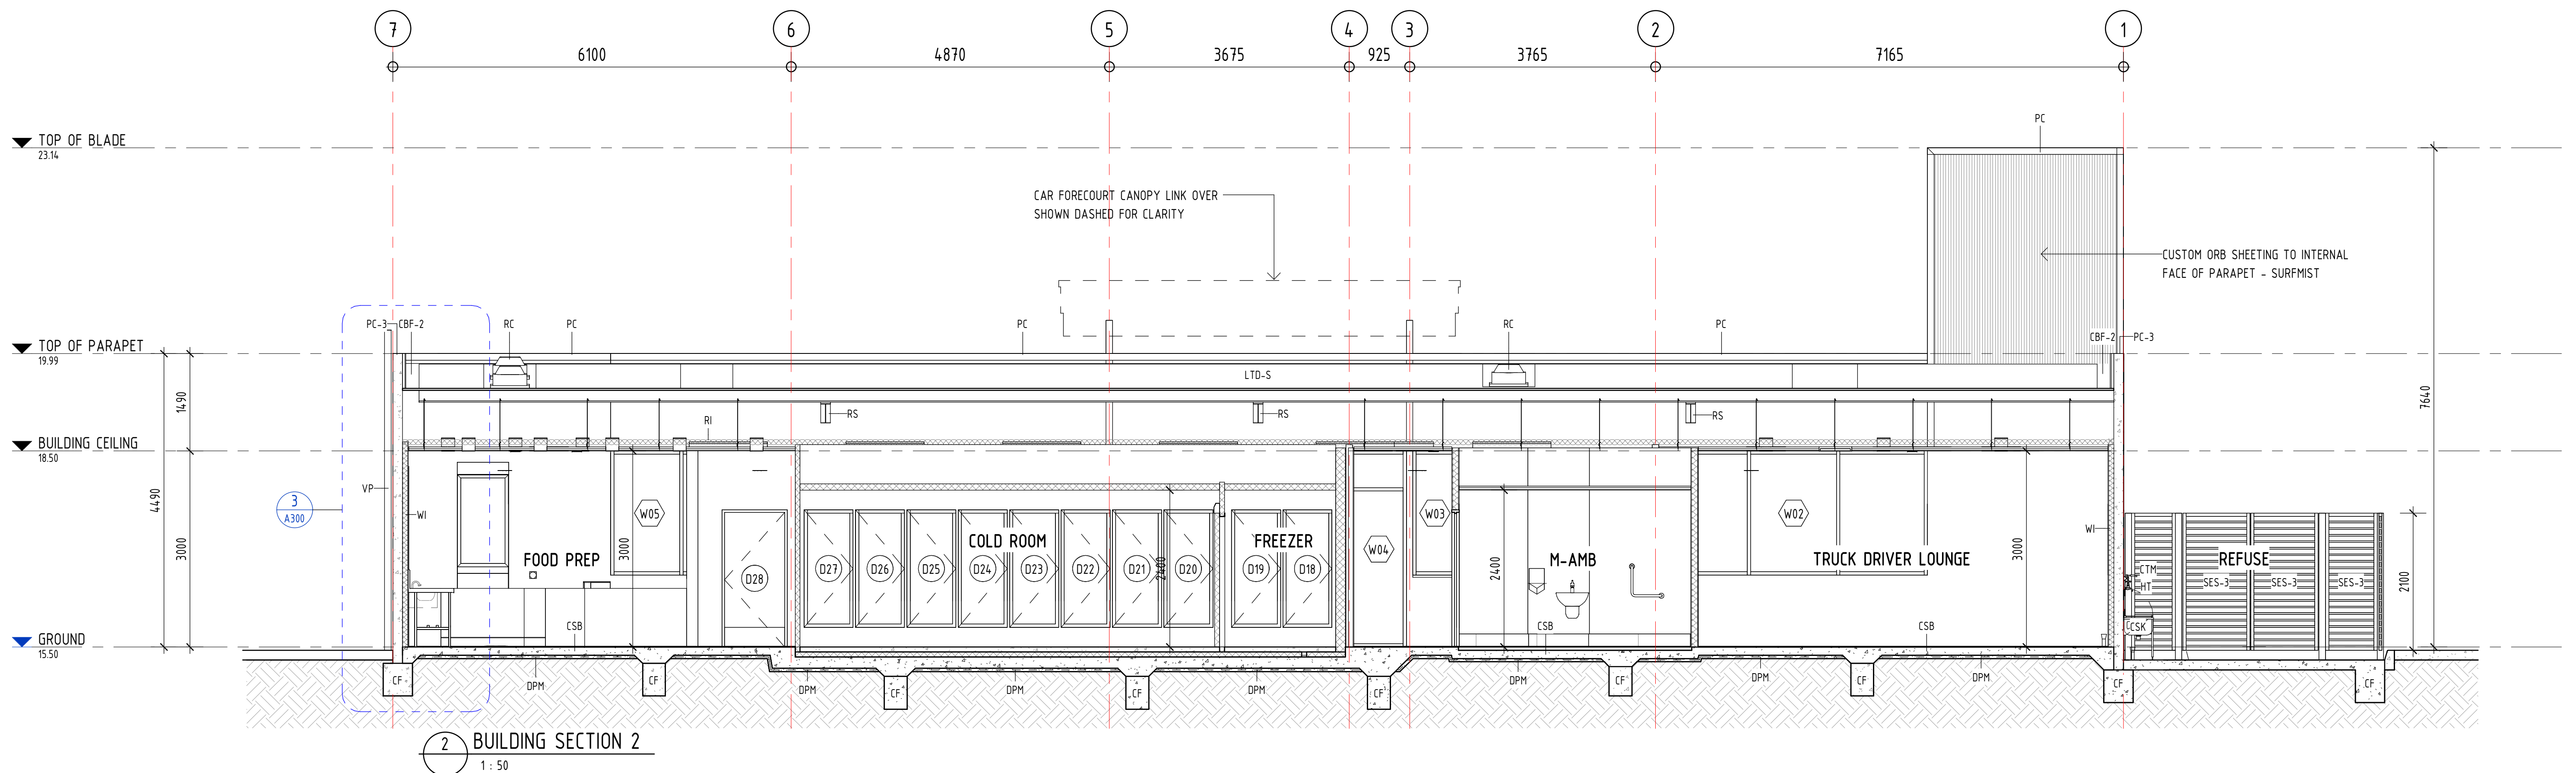

VERVE SCHEDULES DISCLAIMER:

1. ALL SCHEDULES SHOULD BE CHECKED WITH THE REMAINDER OF THE DRAWING SET.

2. SCHEDULED RATES AND AREAS ARE INTENDED FOR ASSISTANCE ONLY. NO RESPONSIBILITY IS TAKEN FOR THE ACCURACY OF QUANTITIES.

3. ANY DISCREPANCIES IN SCHEDULES SHOULD BE IDENTIFIED TO THE AUTHOR NOTED.

4. ALL AREAS ARE GROSS AREAS, UNLESS NOTED OTHERWISE

CONSULTING ENGINEER




- ☐ commercial ☐ service stations ☐ mixed-use ☐ quick service restaurants ☐ self storage ☐ child care centres ☐ industrial ☐ large format retail

© 2011 copyright, all rights reserved.
This drawing is the © copyright & property of VERVE DESIGN GROUP and must not be used or duplicated without authorisation.
Do not scale this drawing.
Check all dimensions on site prior commencement of works

Revision and approvals				
Rev	Date	Drn	Description	Appr
P1	12.02.2026	PC	PRELIMINARY ISSUE	SS
P2	09.03.2026	PC	REVISED PRELIMINARY ISSUE	SS
P3	01.05.2026	PC	REVISED PRELIMINARY ISSUE	SS
A	19.06.2026	PC	BA ISSUE	SS

Project Description	
PROPOSED SERVICE STATION	
22 ENTERPRISE CCT., MARYBOROUGH W.	
Scale @A1 1: 50	Date FEBRUARY 2026
Drawn PC	Approved By SS

Drawing Title	
PROP. BUILDING SECTIONS	
Job Number - Drawing Number 26024 A210	Revision A

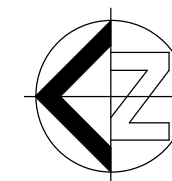

BA ISSUE

THIS DRAWING IS NOT
FOR CONSTRUCTION

GENERAL NOTES

1. THESE DRAWINGS SHALL BE READ IN CONJUNCTION WITH ALL OTHER CONSULTANTS DRAWINGS AND SPECIFICATIONS.
2. DO NOT SCALE DRAWINGS - FIGURED DIMENSIONS ARE TO TAKE PRECEDENCE AT ALL TIMES.
3. ALL DIMENSIONS TO BE CONFIRMED ON SITE AND/OR VERIFIED PRIOR TO CONSTRUCTION OR FABRICATION.
4. ALL MATERIALS AND WORKMANSHIP SHALL BE IN ACCORDANCE WITH CURRENT AND RELEVANT SAA CODES, NCC OF AUSTRALIA, THE BUILDING ACT, AND LOCAL AUTHORITIES BY-LAWS.
5. ALL EXTERNALLY GLAZED WINDOWS AND DOORS TO BE DESIGNED AND CERTIFIED BY THE MANUFACTURER INCLUDING FIXINGS, AND SHALL COMPLY WITH AS1288 & AS1170.2.
6. ALL STAIRS, RAMP, HANDRAILS AND BALUSTRADES ARE TO COMPLY WITH NCC OF AUSTRALIA, SECTION D & AS1428.1.
7. THE CONTRACTOR SHALL BE RESPONSIBLE FOR THE STRUCTURE DURING ERECTION AND PROVIDE ADEQUATE PROPPING AND SUPPORT.
8. ALL INTERNAL NON-LOADBEARING WALLS, CEILINGS AND OTHER RELEVANT STRUCTURAL COMPONENTS SHALL BE DESIGNED & INSTALLED TO COMPLY WITH SECTION 2 OF AS1170.4 AS REQUIRED.


LEGEND

- BFC BROOM FINISH NATURAL GREY CONCRETE
STF STEEL TROWEL FINISH NATURAL GREY CONCRETE
BLACK BLACK CONCRETE HAND STIPPLE FINISH (NON-SLIP)
COLOUR: CCS BLACK OXIDE 8% DOSAGE RATE
SEALANT: NUTECH - PETROL RESISTANT
PAVECOAT - PR210 BLACK COLOURED WITH
NUTECH ANTI-SLIP ADDITIVE APPLIED AS PER
MANUFACTURER'S INSTRUCTIONS.


PAVEMENT & FLOOR FINISHES TO ACHIEVE SLIP RESISTANCE IN COMPLIANCE WITH PART D1 OF THE NCC & TABLE 3A + TABLE 3B WITHIN STANDARDS AUSTRALIA HANDBOOK 198:2014 (SA HB 198:2014).

LEGEND

ADB	AD BLUE DISPENSER - REFER FUEL ENG. DETAILS
AHR	AIR HOSE REEL
BOL-1	STEEL BOLLARD TYPE 1 - REFER DETAIL
BOL-3	STEEL BOLLARD TYPE 3 - REFER DETAIL
CC1	CANOPY COLUMN - REFER STRUCT. ENG. DETAILS
DP	DOWNPIPE - REFER HYD. ENG. DETAILS
FE	FIRE EXTINGUISHER - SUPPLIED & INSTALLED BY LESSEE
FFB	FUEL FILL BOX - REFER FUEL ENG. DETAILS
HT	HOSECOCK TAP CONNECTION - REFER HYD. ENG. DETAILS
NAD	NEW AD BLUE FUEL DISPENSER - REFER FUEL ENG. DETAILS
NFD	NEW FUEL DISPENSER - REFER FUEL ENG. DETAILS
PAS	PUBLIC ADDRESS SYSTEM SPEAKER - REFER ELEC. ENG. DETAILS
PTD-2	FORECOURT PAPER TOWEL DISPENSER SUPPLIED & INSTALLED BY LESSEE
SFFB	SECOND FUEL FILL BOX - REFER FUEL ENG. DETAILS
SGN-6	ILLUMINATED 'WAVE LIGHT' SIGNAGE SUPPLIED & INSTALLED BY LESSEE CONTRACTOR. BUILDER TO PROVIDE POWER SERVICE
SGN-7	NON-ILLUMINATED SIGNAGE SUPPLIED & INSTALLED BY LESSEE CONTRACTOR
SGN-8	NON-ILLUMINATED SIGNAGE SUPPLIED & INSTALLED BY LESSEE CONTRACTOR
SWG	STORMWATER GULLY - REFER CIVIL ENG. DETAILS

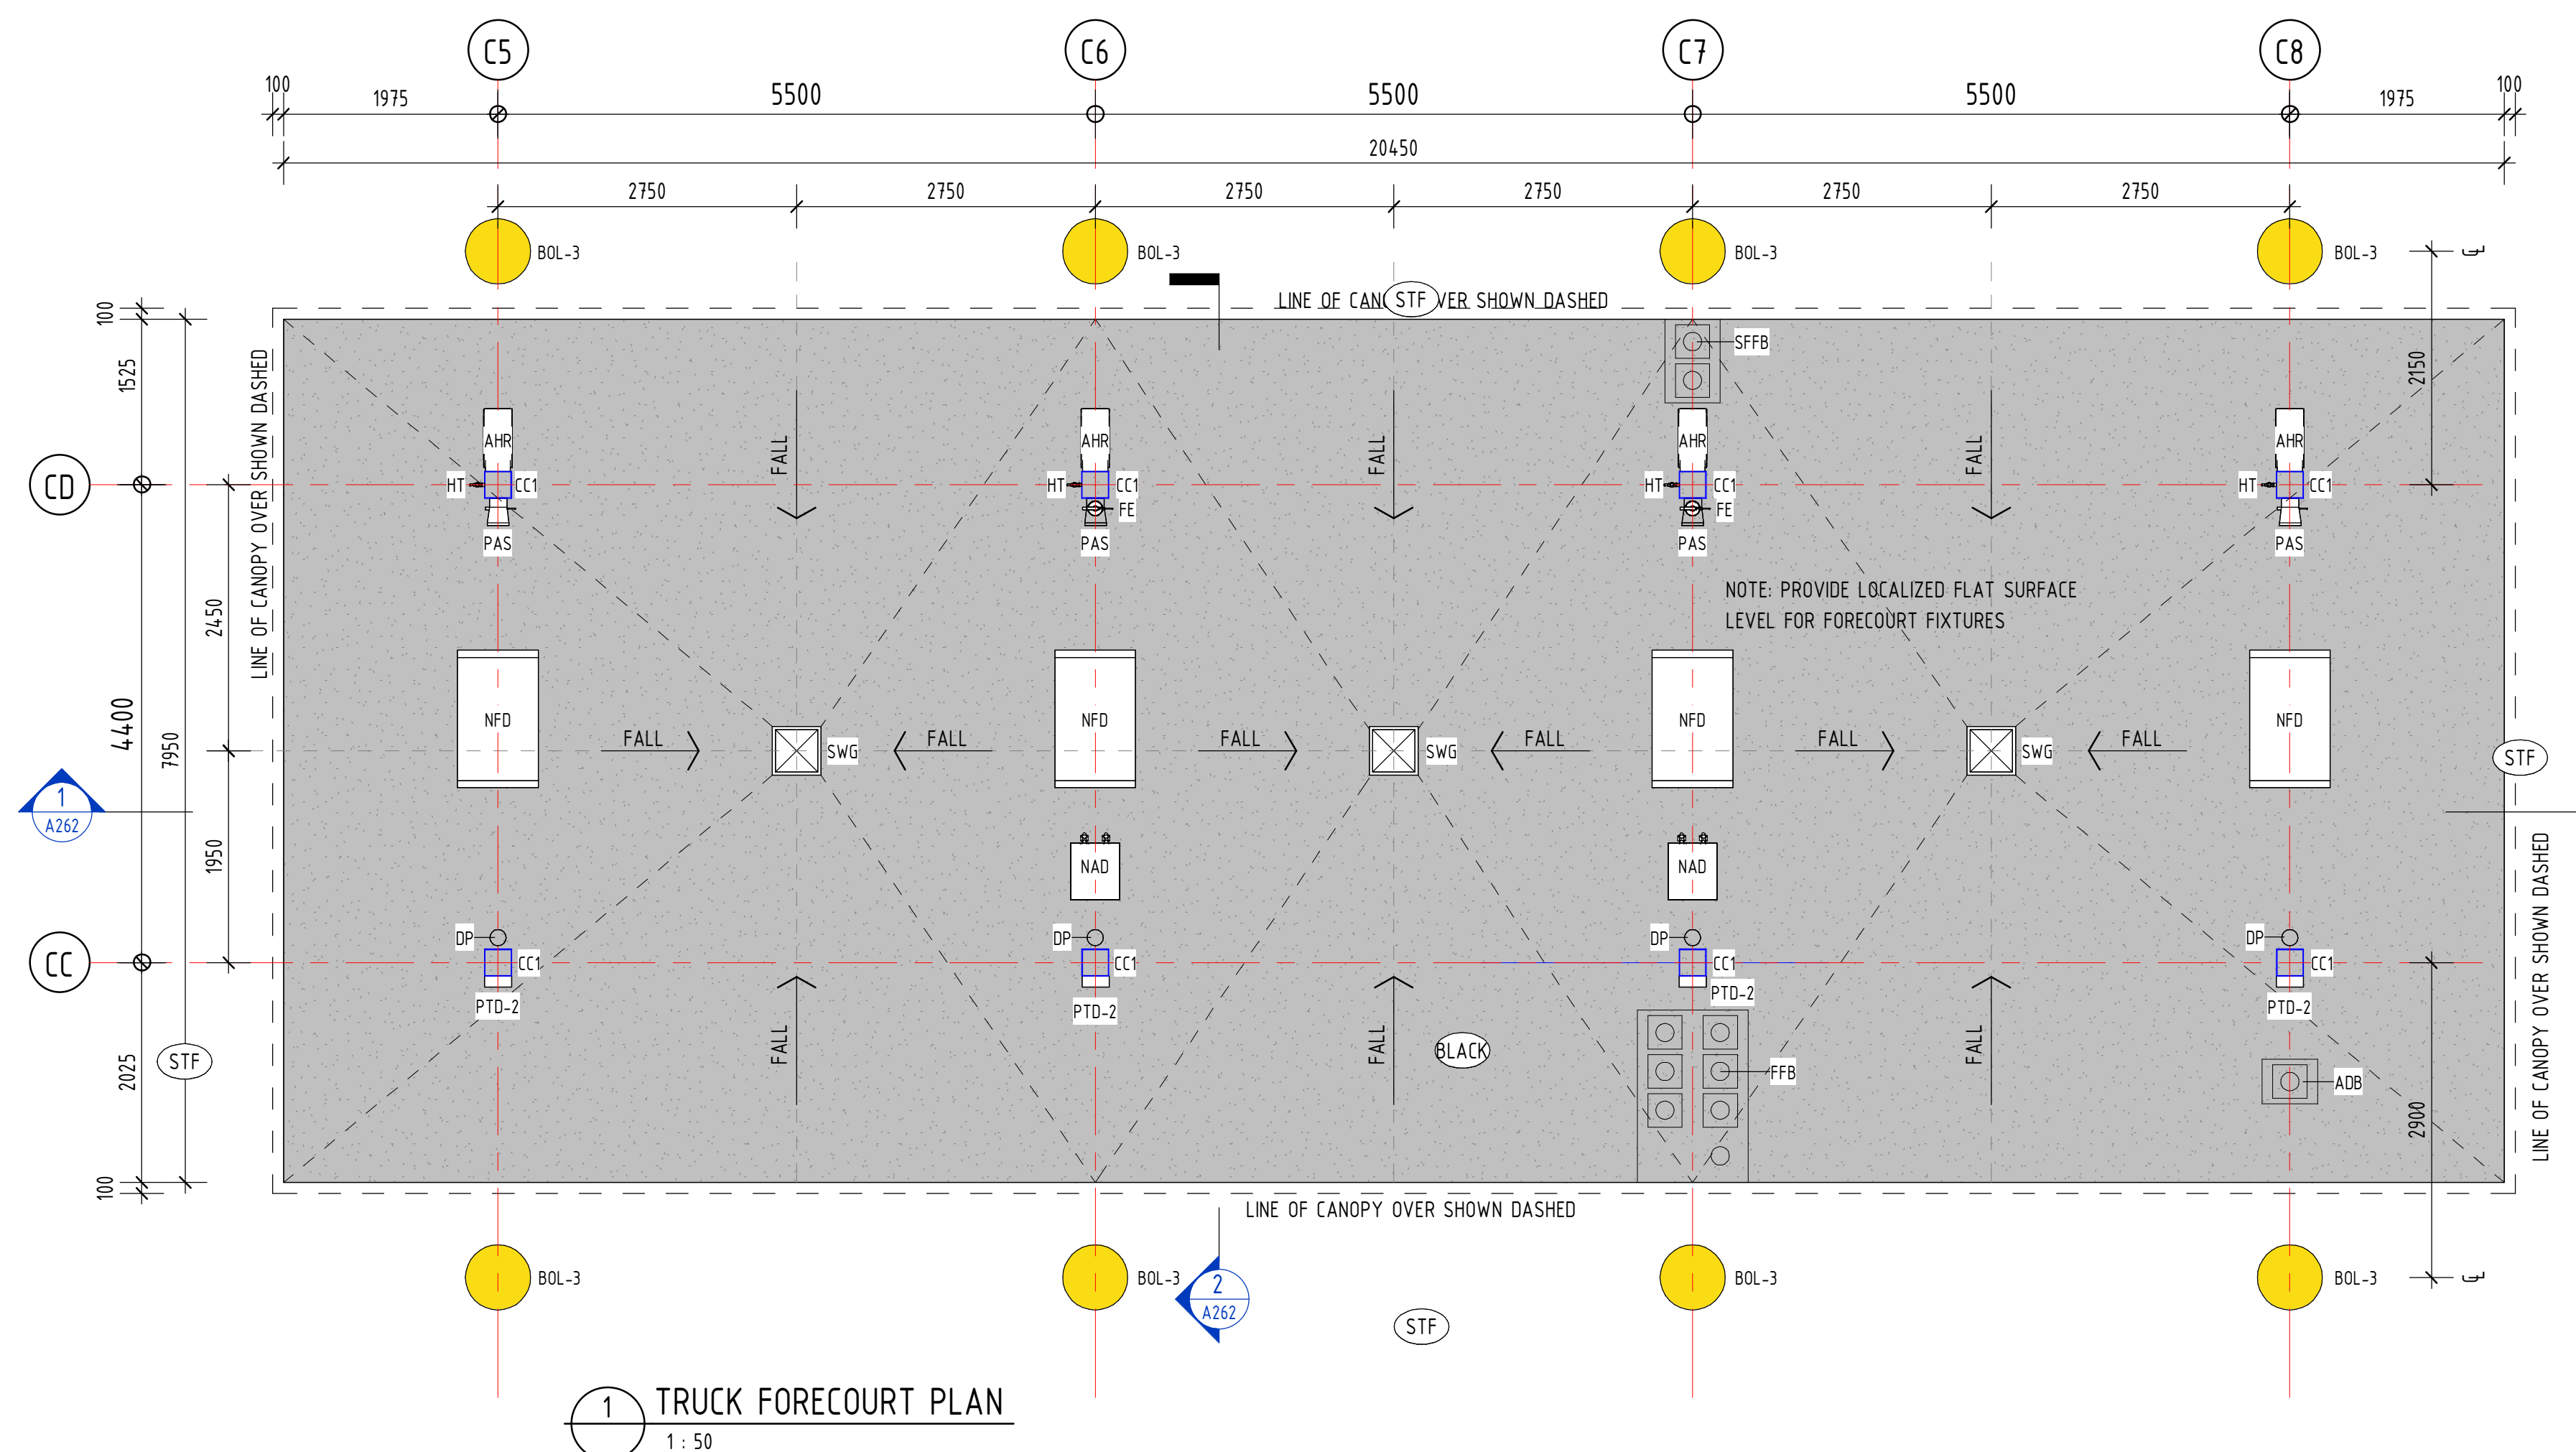

1 TRUCK FORECOURT PLAN
1 : 50

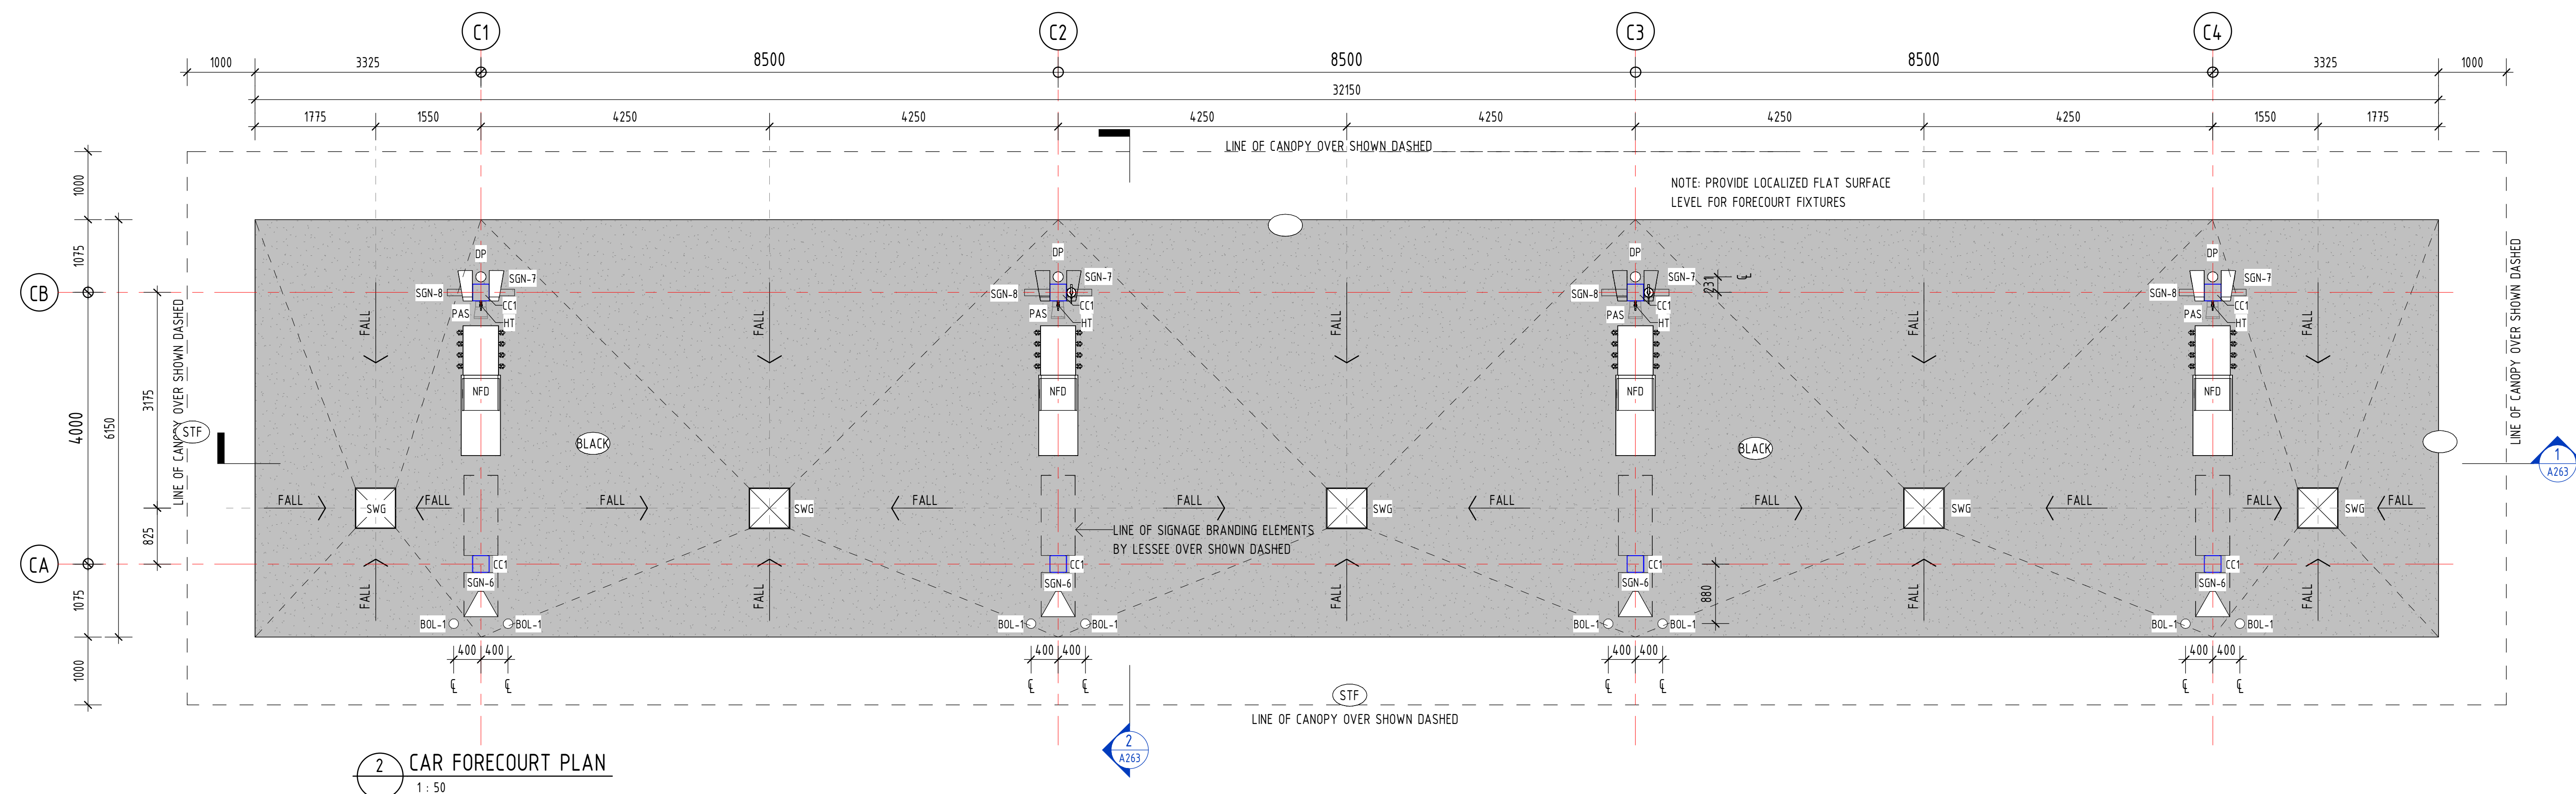

2 CAR FORECOURT PLAN
1 : 50

VERVE SCHEDULES DISCLAIMER:

1. ALL SCHEDULES SHOULD BE CHECKED WITH THE REMAINDER OF THE DRAWING SET.
2. SCHEDULED RATES AND AREAS ARE INTENDED FOR ASSISTANCE ONLY. NO RESPONSIBILITY IS TAKEN FOR THE ACCURACY OF QUANTITIES.
3. ANY DISCREPANCIES IN SCHEDULES SHOULD BE IDENTIFIED TO THE AUTHOR NOTED.
4. ALL AREAS ARE GROSS AREAS, UNLESS NOTED OTHERWISE

CONSULTING ENGINEER




- ☐ commercial ☐ service stations ☐ mixed-use ☐ quick service restaurants ☐ self storage ☐ child care centres ☐ industrial ☐ large format retail

© 2011 copyright, all rights reserved.
This drawing is the © copyright & property of VERVE Design Group and must not be used or duplicated without authorisation.
Do not scale this drawing.
Check all dimensions on site prior commencement of works

Revision and approvals				
Rev	Date	Drn	Description	Appr
P1	12.02.2026	PC	PRELIMINARY ISSUE	SS
P2	01.05.2026	PC	REVISED PRELIMINARY ISSUE	SS
A	19.06.2026	PC	BA ISSUE	SS

Project Description	
PROPOSED SERVICE STATION	
22 ENTERPRISE CCT., MARYBOROUGH W.	
Scale @A1 1 : 50	Date FEBRUARY 2026
Drawn PC	Approved By SS

Drawing Title	
PROP. CAR & TRUCK FORECOURT CANOPY PLANS	
Job Number - Drawing Number 26024 A250	Revision A

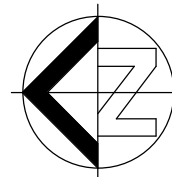

BA ISSUE
THIS DRAWING IS NOT FOR CONSTRUCTION

LEGEND	
BG	BOX GUTTER - REFER HYD. ENG. DETAILS
CC1	CANOPY COLUMN - REFER STRUCT. ENG. DETAILS
CL	CANOPY LIGHT - REFER ELEC. ENG. DETAILS
DP	DOWNPIPE - REFER HYD. ENG. DETAILS
LKL-Z	LYSAGHT KLIP-LOK HI STRENGTH 0.48BMT ZINCALUME
OF	OVERFLOW - REFER HYD. ENG. DETAILS
PAS	PUBLIC ADDRESS SYSTEM SPEAKER - REFER ELEC. ENG. DETAILS
PC	PARAPET CAPPING. REFER ELEVATIONS FOR COLOUR
RAP	SURFACE MOUNT ROOF ACCESS POINT LADDER SUPPORT BRACKET INSTALLED TO MAN. SPEC.
S	SUMP - REFER HYD. ENG. DETAILS
ZF	ZINCALUME FLASHING

NOTE:
THIS DRAWING TO BE READ IN CONJUNCTION WITH ROOF STORMWATER DRAWINGS PREPARED BY HYDRAULIC ENGINEER

RL NOTE:
RL's SHOWN ARE IN METRES AND REFER TO DATUM LEVEL 00.00

PROPRIETARY ROOF ACCESS SYSTEM

WHERE REQUIRED INSTALL A PROPRIETARY ROOF ACCESS LANYARD SYSTEM TO ASSIST IN THE SAFE ACCESS AND MAINTENANCE OF THE WHOLE OF THE ROOFED AREAS OF THE BUILDING AT ROOF LEVEL.
THE SYSTEM IS TO COMPLY TO AS/NZS 1891.1/1891.2
SUPPLIER/INSTALLER TO PROVIDE PERMANENT LADDER BRACKET, SAFETY GATE, ROOF WALKWAY & APPROPRIATE ROOF MOUNTED HANDRAILS AS REQUIRED.

1. PROPRIETARY ROOF ACCESS SYSTEM INDICATED ON PLAN IS DIAGRAMMATIC ONLY. SUPPLIER/INSTALLER TO DESIGN, INSTALL & CERTIFY SYSTEM.
2. SUPPLIER/INSTALLER TO PROVIDE APPROPRIATE ROOF ACCESS SYSTEM AND SAFETY WARNING SIGNS (AS PER AS 1657). SUPPLIER/INSTALLER TO CONFIRM COMPLIANCE OF ROOF SAFETY SYSTEM WITH RELEVANT STANDARDS PRIOR TO INSTALLATION.

MECHANICAL NOTE :

MECHANICAL EQUIPMENT AND PENETRATION LOCATIONS ARE DIAGRAMMATIC ONLY. REFER MECHANICAL DRAWINGS FOR LOCATIONS AND CLEARANCE REQUIREMENTS.

ROOFING NOTES

1. ROOF SHEETING TO BE **LYSAGHT TRIMDEK 0.48 BMT & LYSAGHT KLIP-LOK 700 HS 0.48 BMT**, AS NOTED ON PLAN.
2. ALL FLASHINGS, CAPPINGS & GUTTERS TO BE COLORBOND FINISH
3. REFER TO MECHANICAL & HYDRAULICS DRAWINGS FOR ROOF PENETRATIONS & EQUIPMENT LOCATIONS.
4. MINIMUM FALL TO GUTTERS TO BE 1:100.
5. ALL EXPOSED DUCTWORK TO BE PAINTED WHITE UNO
6. FOLDED METAL CAP OVER JUNCTION OF BOX GUTTERS AT HIGH POINT.
7. CONTINUOUS 12mm BMT METAL OVER-FLASHING FROM RIDGE OR CHANGE IN ROOF PITCH TO ROOF PENETRATION.
8. SUPPLY AND INSTALL REMOVABLE LEAF GUARD OVER DOWNPIPES AS REQUIRED.
9. SUPPLY AND INSTALL REMOVABLE GRATES OVER RAIN WATER HEADS AND SUMPS AS REQUIRED.
10. TURN UP SHEET ENDS UNDER FLASHINGS & DOWN INTO GUTTERS.
11. PROVIDE PROFILED FILLERS TO ENDS OF SHEETING, (BETWEEN SHEET & PURLIN AND SHEET & FLASHING).
12. SCRIBE ALL FLASHINGS AND CAPPINGS ACCORDINGLY TO PROFILES. UPSTANDS TO BE MIN. 100mm(H). OVER FLASHINGS TO BE MIN. 200mm(W) AND COVER 2 ROOF PROFILES. VERTICAL LAPS TO BE MIN 100mm. HORIZONTAL LAPS TO BE MIN 150mm.
13. INSTALL SOAKERS ON HIGH SIDE OF ALL ROOF PENETRATIONS UNDER ROOF SHEETING AND APRON FLASHINGS TO OTHER THREE SIDES.
14. ALL EXTERNAL STEELWORK TO BE HOT DIPPED GALVANISED UNLESS OTHERWISE NOTED.
15. ALL SERVICE LINES AND POST PENETRATIONS THROUGH ROOF TO HAVE DEKTITE FLASHINGS.
16. OVERFLASHINGS AND SOAKER FLASHINGS ARE TO BE SAW CUT AND SEALED IN TO BLOCK WALLS WHERE APPLICABLE.

GENERAL NOTES:



1. DO NOT SCALE OFF THIS DRAWING.
2. THE CONTRACTOR SHALL CARRY OUT A TRIAL SET-OUT OF ALL CEILING AND SOFFIT TYPES AND VERIFY WITH THE SUPERINTENDENT PRIOR TO CONSTRUCTION PROCEEDING.
3. GENERALLY SET-OUT ROOMS FROM CENTRE LINE BETWEEN WALLS, WHERE NO SET-OUT SHOWN ASSUME CENTRAL SET-OUT.
4. "equal" RELATES ONLY TO OPPOSING DIMENSION IN THAT DIMENSION LINE.
5. CHECK ALL DIMENSIONS ON SITE WITHIN ROOMS PRIOR INSTALLATION OF FITTINGS. NOTIFY SUPERINTENDENT OF ANY DISCREPANCIES PRIOR PROCEEDING.
6. CEILING HEIGHTS SHOWN ARE TAKEN FROM THE TOP OF THE CONC. FLOOR SLAB.
7. FOR MECHANICAL AND ELECTRICAL EQUIPMENT TYPES AND MODELS, REFER TO ENGINEERS DRAWINGS.
8. SET-OUT OF ALL ELECTRICAL AND MECHANICAL FIXTURES AND FITTINGS TO BE CONFIRMED ON SITE WITH THE SUPERINTENDENT PRIOR TO FRAMING, CUTTING ETC. OF THE CEILING LINING.
9. ALL ELEMENTS IDENTIFIED IN AS1170.4 SECTION 8 ARE TO BE DESIGNED, SUPPLIED & INSTALLED BY THE BUILDER/ CONTRACTOR TO ENSURE COMPLIANCE WITH THE REQUIREMENTS OF AS1170.4
10. SEISMIC RESTRAINT SYSTEMS FOR SERVICES SHALL BE PROVIDED AS REQUIRED PER SECTION 8.14(b) OF AS1170.4

LEGEND - REFLECTED CEILING PLAN

eg:
WPB CEILING MATERIAL
2700 CEILING HEIGHT ABOVE CONC. SLAB LEVEL

MATERIAL:

IP INSULATED COLDROOM PANEL 100mm THICK
FPB FLUSHSET PLASTERBOARD
GRID VINYL FACED PLASTER TILE 600x1200
WFPB WET AREA FLUSHSET PLASTERBOARD
STP STRAMIT PREMIER 300 COLORBOND
CLADDING SURFMIST
CLD 'EYEBROW' CLADDING BY SIGNAGE CONTRACTOR TO TENANT SPECIFICATIONS. INSTALL TO MANUFACTURERS SPECIFICATIONS

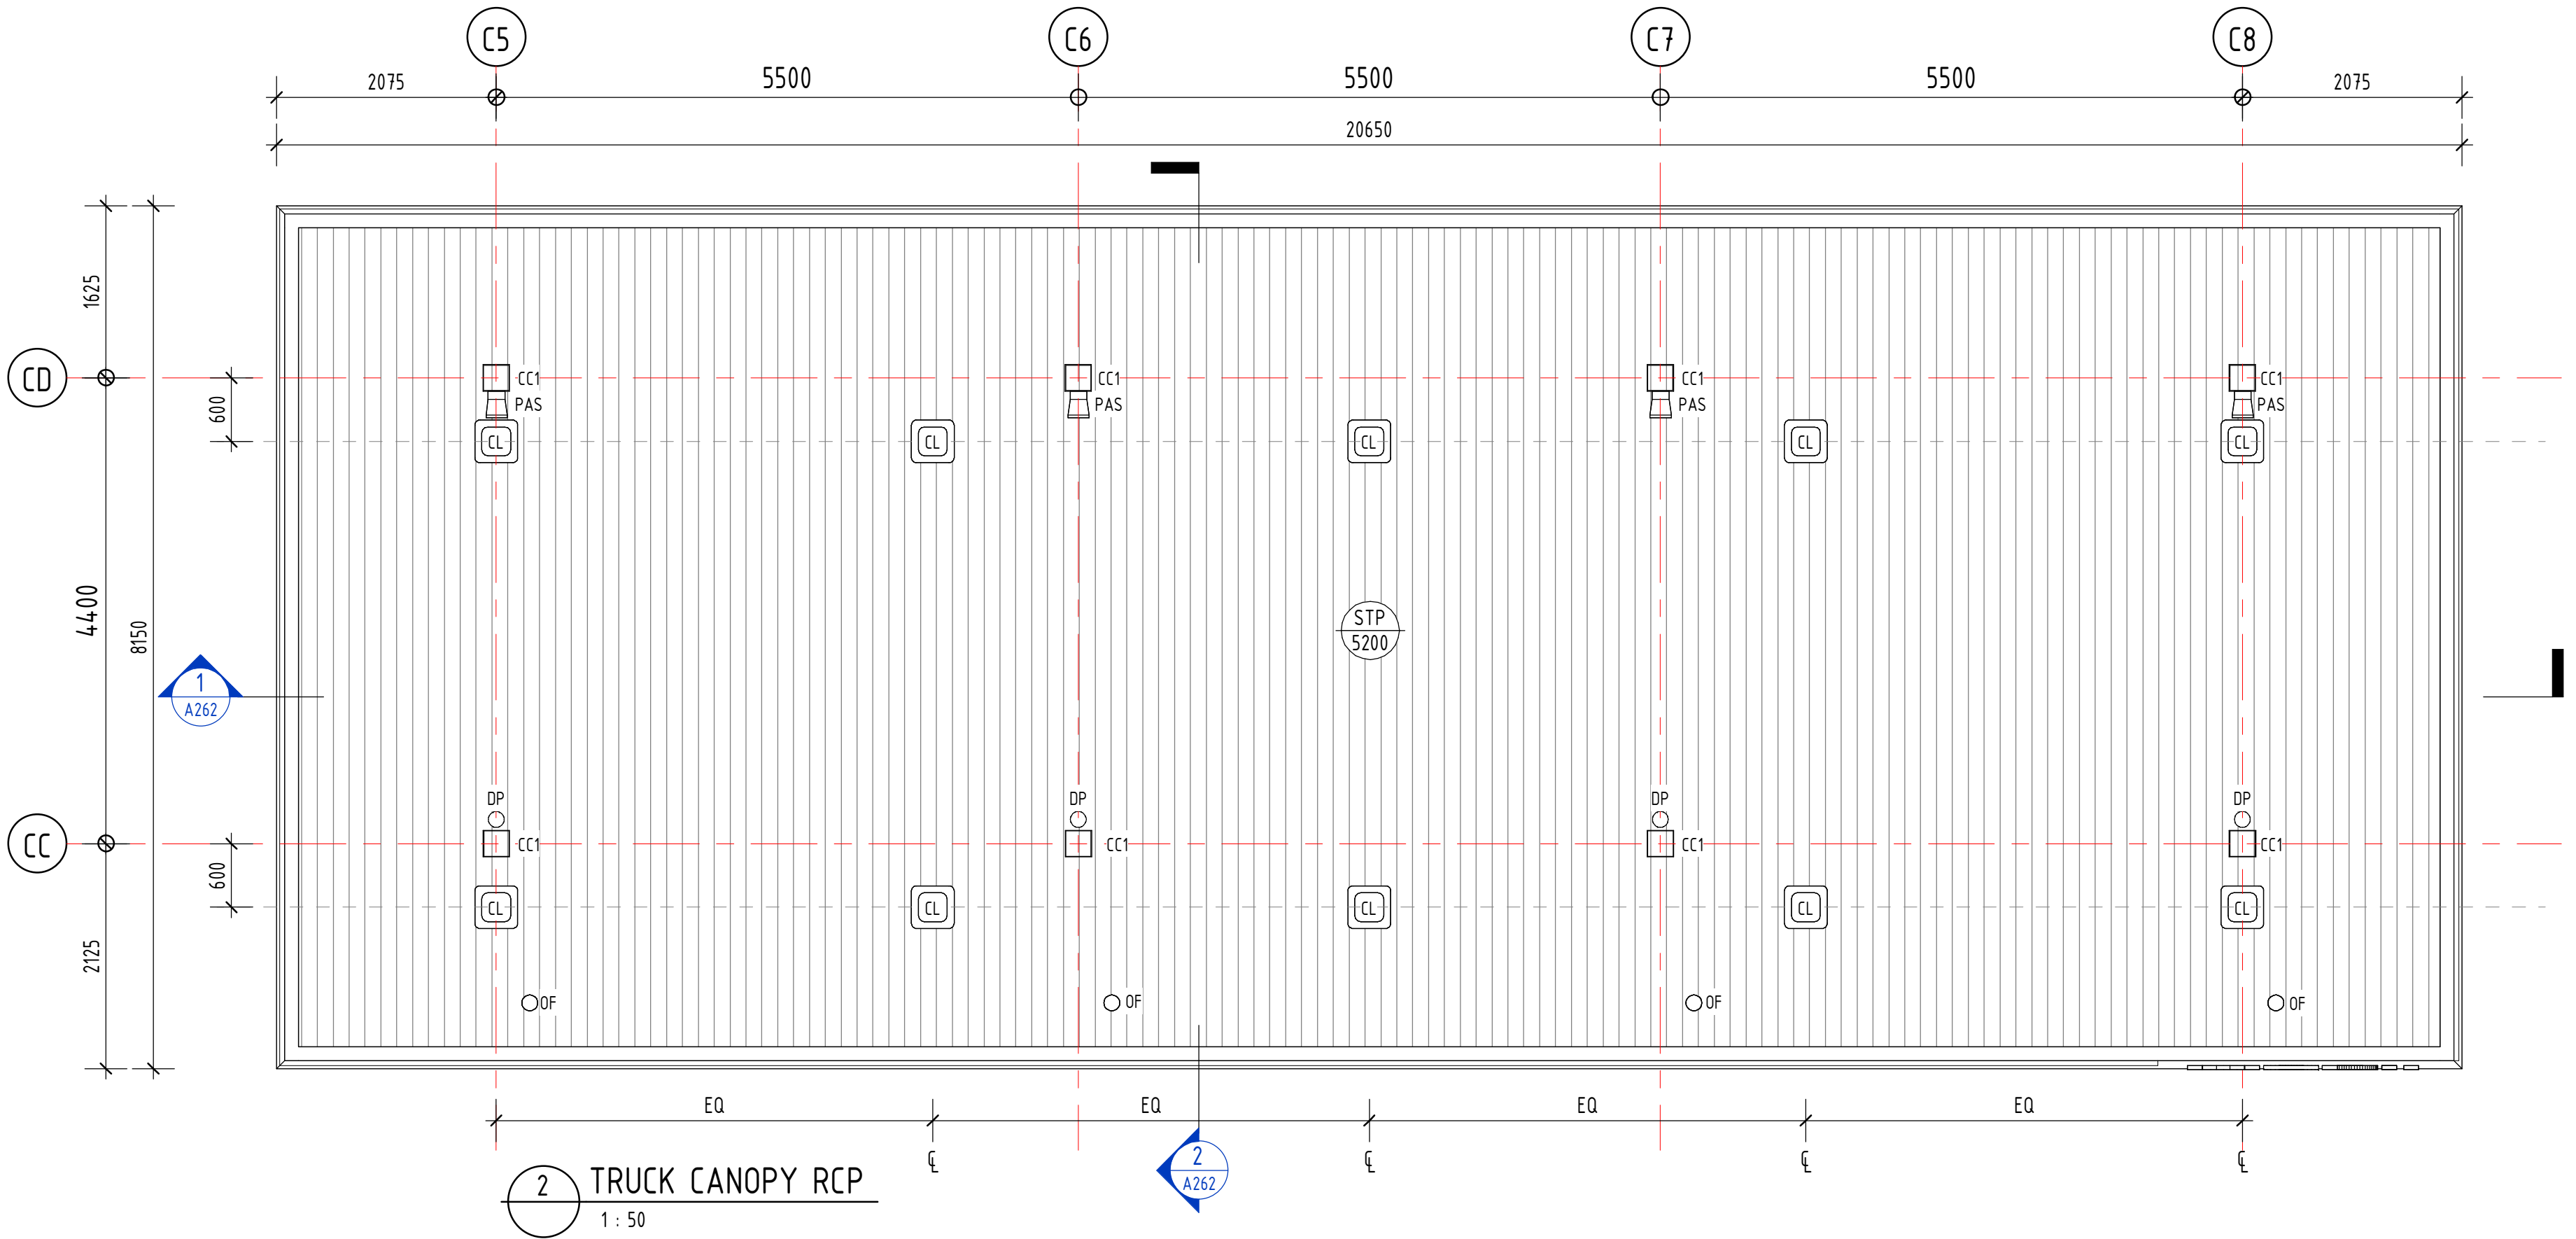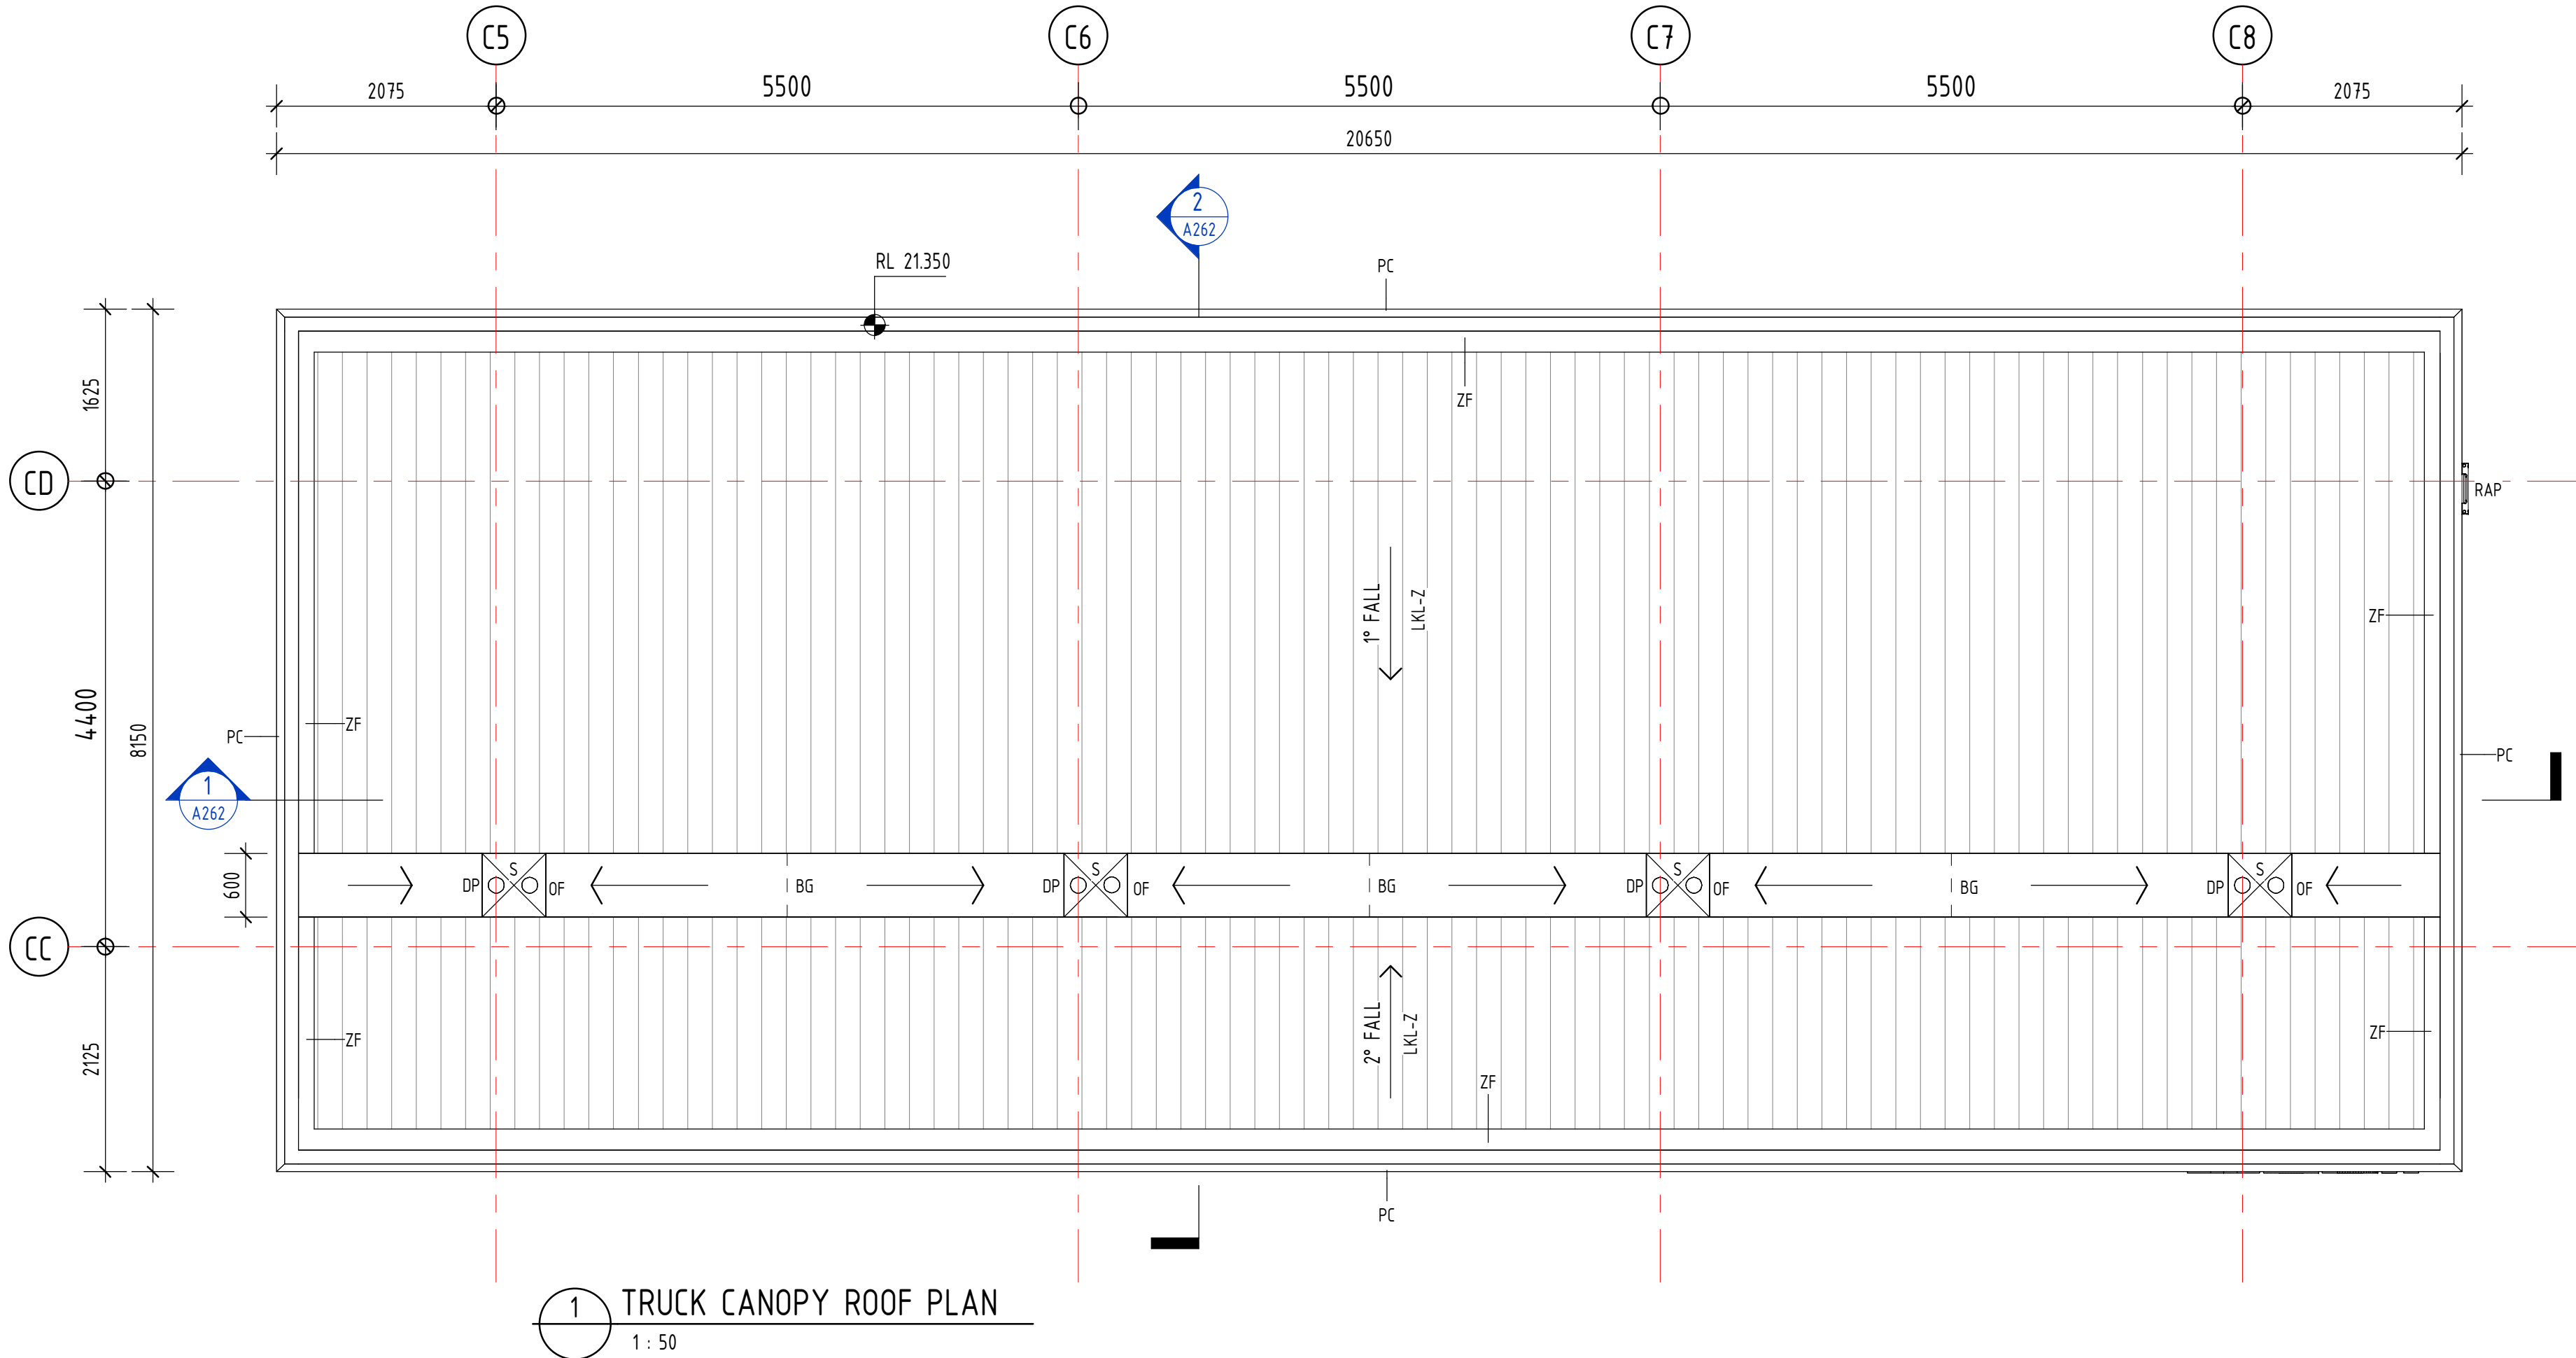

VERVE SCHEDULES DISCLAIMER:
1. ALL SCHEDULES SHOULD BE CHECKED WITH THE REMAINDER OF THE DRAWING SET.
2. SCHEDULED RATES AND AREAS ARE INTENDED FOR ASSISTANCE ONLY. NO RESPONSIBILITY IS TAKEN FOR THE ACCURACY OF QUANTITIES.
3. ANY DISCREPANCIES IN SCHEDULES SHOULD BE IDENTIFIED TO THE AUTHOR NOTED.
4. ALL AREAS ARE GROSS AREAS, UNLESS NOTED OTHERWISE

CONSULTING ENGINEER



- ☐ commercial
- ☐ mixed-use
- ☐ self storage
- ☐ industrial
- ☐ service stations
- ☐ quick service restaurants
- ☐ child care centres
- ☐ large format retail

© 2011 copyright, all rights reserved.

This drawing is the © copyright & property of VERVE DESIGN GROUP and must not be used or duplicated without authorisation.

Do not scale this drawing.

Check all dimensions on site prior commencement of works

Revision and approvals			
Rev	Date	Drn	Description
P1	12.02.2026	PC	PRELIMINARY ISSUE
P2	01.05.2026	PC	REVISED PRELIMINARY ISSUE
A	19.06.2026	PC	BA ISSUE


Project Description	
PROPOSED SERVICE STATION	
22 ENTERPRISE CCT., MARYBOROUGH W.	
Scale @A1 1 : 50	Date FEBRUARY 2026
Drawn PC	Approved By SS

Drawing Title	
PROP. TRUCK FORECOURT CANOPY ROOF & RCP	
Job Number - Drawing Number 26024 A251	Revision A



	LEGEND
BG	BOX GUTTER - REFER HYD. ENG. DETAILS
DP	DOWNPIPE - REFER HYD. ENG. DETAILS
DPS	DOWNPIPE WITH SPREADER - REFER HYD. ENG. DETAILS
LKL-Z	LYSAGHT KLIP-LOK HI STRENGTH 0.48BMT ZINCALUME
OF	OVERFLOW - REFER HYD. ENG. DETAILS
PC	PARAPET CAPPING, REFER ELEVATIONS FOR COLOUR
RAL	PROPRIETARY ROOF ACCESS LADDER TO CONTRACTOR SPECIFICATION TO COMPLY WITH AS1657:2018
S	SUMP - REFER HYD. ENG. DETAILS
ZF	ZINCALUME FLASHING

Drawing Title PROP. CAR FORECOURT CANOPY ROOF		
Job Number - Drawing Number 26024 A252		Revision A

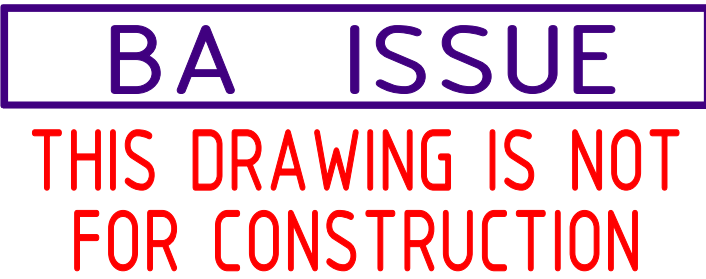

1. DO NOT SCALE OFF THIS DRAWING.
2. THE CONTRACTOR SHALL CARRY OUT A TRIAL SET-OUT OF ALL CEILING AND SOFFIT TYPES AND VERIFY WITH THE SUPERINTENDENT PRIOR TO CONSTRUCTION PROCEEDING.
3. GENERALLY SET-OUT ROOMS FROM CENTRE LINE BETWEEN WALLS, WHERE NO SET-OUT SHOWN ASSUME CENTRAL SET-OUT.
4. "equal" RELATES ONLY TO OPPOSING DIMENSION IN THAT DIMENSION LINE.
5. CHECK ALL DIMENSIONS ON SITE WITHIN ROOMS PRIOR INSTALLATION OF FITTINGS. NOTIFY SUPERINTENDENT IF ANY DISCREPANCIES PRIOR PROCEEDING;
6. CEILING HEIGHTS SHOWN ARE TAKEN FROM THE TOP OF THE CONC. FLOOR SLAB.
7. FOR MECHANICAL AND ELECTRICAL EQUIPMENT TYPES AND MODELS, REFER TO ENGINEERS DRAWINGS.
8. SET-OUT OF ALL ELECTRICAL AND MECHANICAL FIXTURES AND FITTINGS TO BE CONFIRMED ON SITE WITH THE SUPERINTENDENT PRIOR TO FRAMING, CUTTING ETC. OF THE CEILING LINING.
9. ALL ELEMENTS IDENTIFIED IN AS1170.4 SECTION 8 ARE TO BE DESIGNED, SUPPLIED & INSTALLED BY THE BUILDER/ CONTRACTOR TO ENSURE COMPLIANCE WITH THE REQUIREMENTS OF AS1170.4
10. SEISMIC RESTRAINT SYSTEMS FOR SERVICES SHALL BE PROVIDED AS REQUIRED PER SECTION 8.14(b) OF AS1170.4

eg:
WPB CEILING MATERIAL
2700 CEILING HEIGHT ABOVE CONC. SLAB LEVEL

IP	INSULATED COLDROOM PANEL 100mm THICK
FPB	FLUSHSET PLASTERBOARD
GRID	VINYL FACED PLASTER TILE 600x1200
WFPB	WET AREA FLUSHSET PLASTERBOARD
STP	STRAMIT PREMIER 300 COLORBOND CLADDING SURFMIST
CLD	'EYEBROW' CLADDING BY SIGNAGE CONTRACTOR TO TENANT SPECIFICATIONS. INSTALL TO MANUFACTURERS SPECIFICATIONS

LEGEND	
CC1	CANOPY COLUMN - REFER STRUCT. ENG. DETAILS
CL	CANOPY LIGHT - REFER ELEC. ENG. DETAILS
DP	DOWNPipe - REFER HYD. ENG. DETAILS
DPS	DOWNPipe WITH SPREADER - REFER HYD. ENG. DETAILS
OF	OVERFLOW - REFER HYD. ENG. DETAILS
PAS	PUBLIC ADDRESS SYSTEM SPEAKER - REFER ELEC. ENG. DETAILS
STP	STRAMIT PREMIER 300 SOFFIT CLADDING. COLOUR COLORBOND SURFMIST

BA ISSUE
THIS DRAWING IS NOT FOR CONSTRUCTION

GENERAL NOTES:

- DO NOT SCALE OFF THIS DRAWING.
- THE CONTRACTOR SHALL CARRY OUT A TRIAL SET-OUT OF ALL CEILING AND SOFFIT TYPES AND VERIFY WITH THE SUPERINTENDENT PRIOR TO CONSTRUCTION PROCEEDING.
- GENERALLY SET-OUT ROOMS FROM CENTRE LINE BETWEEN WALLS, WHERE NO SET-OUT SHOWN ASSUME CENTRAL SET-OUT.
- "equal" RELATES ONLY TO OPPOSING DIMENSION IN THAT DIMENSION LINE.
- CHECK ALL DIMENSIONS ON SITE WITHIN ROOMS PRIOR INSTALLATION OF FITTINGS. NOTIFY SUPERINTENDENT OF ANY DISCREPANCIES PRIOR PROCEEDING.
- CEILING HEIGHTS SHOWN ARE TAKEN FROM THE TOP OF THE CONC. FLOOR SLAB.
- FOR MECHANICAL AND ELECTRICAL EQUIPMENT TYPES AND MODELS, REFER TO ENGINEERS DRAWINGS.
- SET-OUT OF ALL ELECTRICAL AND MECHANICAL FIXTURES AND FITTINGS TO BE CONFIRMED ON SITE WITH THE SUPERINTENDENT PRIOR TO FRAMING, CUTTING ETC. OF THE CEILING LINING.
- ALL ELEMENTS IDENTIFIED IN AS1170.4 SECTION 8 ARE TO BE DESIGNED, SUPPLIED & INSTALLED BY THE BUILDER/ CONTRACTOR TO ENSURE COMPLIANCE WITH THE REQUIREMENTS OF AS1170.4
- SEISMIC RESTRAINT SYSTEMS FOR SERVICES SHALL BE PROVIDED AS REQUIRED PER SECTION 8.14(b) OF AS1170.4


LEGEND - REFLECTED CEILING PLAN
eg:
WPB CEILING MATERIAL
2700 CEILING HEIGHT ABOVE CONC. SLAB LEVEL

MATERIAL:
IP INSULATED COLDROOM PANEL 100mm THICK
FPB FLUSHSET PLASTERBOARD
GRID VINYL FACED PLASTER TILE 600x1200
WFPB WET AREA FLUSHSET PLASTERBOARD
STP STRAMIT PREMIER 300 COLORBOND CLADDING SURFMIST
CLD 'EYEBROW' CLADDING BY SIGNAGE CONTRACTOR TO TENANT SPECIFICATIONS. INSTALL TO MANUFACTURERS SPECIFICATIONS

LEGEND

CC1	CANOPY COLUMN - REFER STRUCT. ENG. DETAILS
CL	CANOPY LIGHT - REFER ELEC. ENG. DETAILS
DP	DOWNPIPE - REFER HYD. ENG. DETAILS
DPS	DOWNPIPE WITH SPREADER - REFER HYD. ENG. DETAILS
OF	OVERFLOW - REFER HYD. ENG. DETAILS
PAS	PUBLIC ADDRESS SYSTEM SPEAKER - REFER ELEC. ENG. DETAILS
STP	STRAMIT PREMIER 300 SOFFIT CLADDING. COLOUR COLORBOND SURFMIST

1. ALL SCHEDULES SHOULD BE CHECKED WITH THE REMAINDER OF THE DRAWING SET.
2. SCHEDULED RATES AND AREAS ARE INTENDED FOR ASSISTANCE ONLY. NO RESPONSIBILITY IS TAKEN FOR THE ACCURACY OF QUANTITIES.
3. ANY DISCREPANCIES IN SCHEDULES SHOULD BE IDENTIFIED TO THE AUTHOR NOTED.
4. ALL AREAS ARE GROSS AREAS, UNLESS NOTED OTHERWISE

 

VERVE
DESIGN GROUP

OBCC LICENCE NO. 1236672 PH. (07) 3857 0942
OFFICE 1, LEVEL 1, 488 LUTWICHE RD, LUTWICHE 4030 info@vervedesigngroup.com.au

imagine ☐ **create** ☐ **deliver**

- ☐ commercial
- ☐ mixed-use
- ☐ self storage
- ☐ industrial
- ☐ service stations
- ☐ quick service restaurants
- ☐ child care centres
- ☐ large format retail

© 2011 copyright, all rights reserved

This drawing is the © copyright & property of VERVE DESIGN GROUP and must not be used or duplicated without authorisation.

Do not scale this drawing.


Check all dimensions on site prior commencement of works

Revision and approvals				
Rev	Date	Drn	Description	Appr
P1	12.02.2026	PC	PRELIMINARY ISSUE	SS
P2	01.05.2026	PC	REVISED PRELIMINARY ISSUE	SS
A	19.06.2026	PC	BA ISSUE	SS

Project Description	
PROPOSED SERVICE STATION	
22 ENTERPRISE CCT., MARYBOROUGH W.	
Scale @A1 1:50	Date FEBRUARY 2026
Drawn PC	Approved By SS

Drawing Title
PROP. CAR FORECOURT
CANOPY RCP

Job Number - Drawing Number	Revision
26024 A253	A

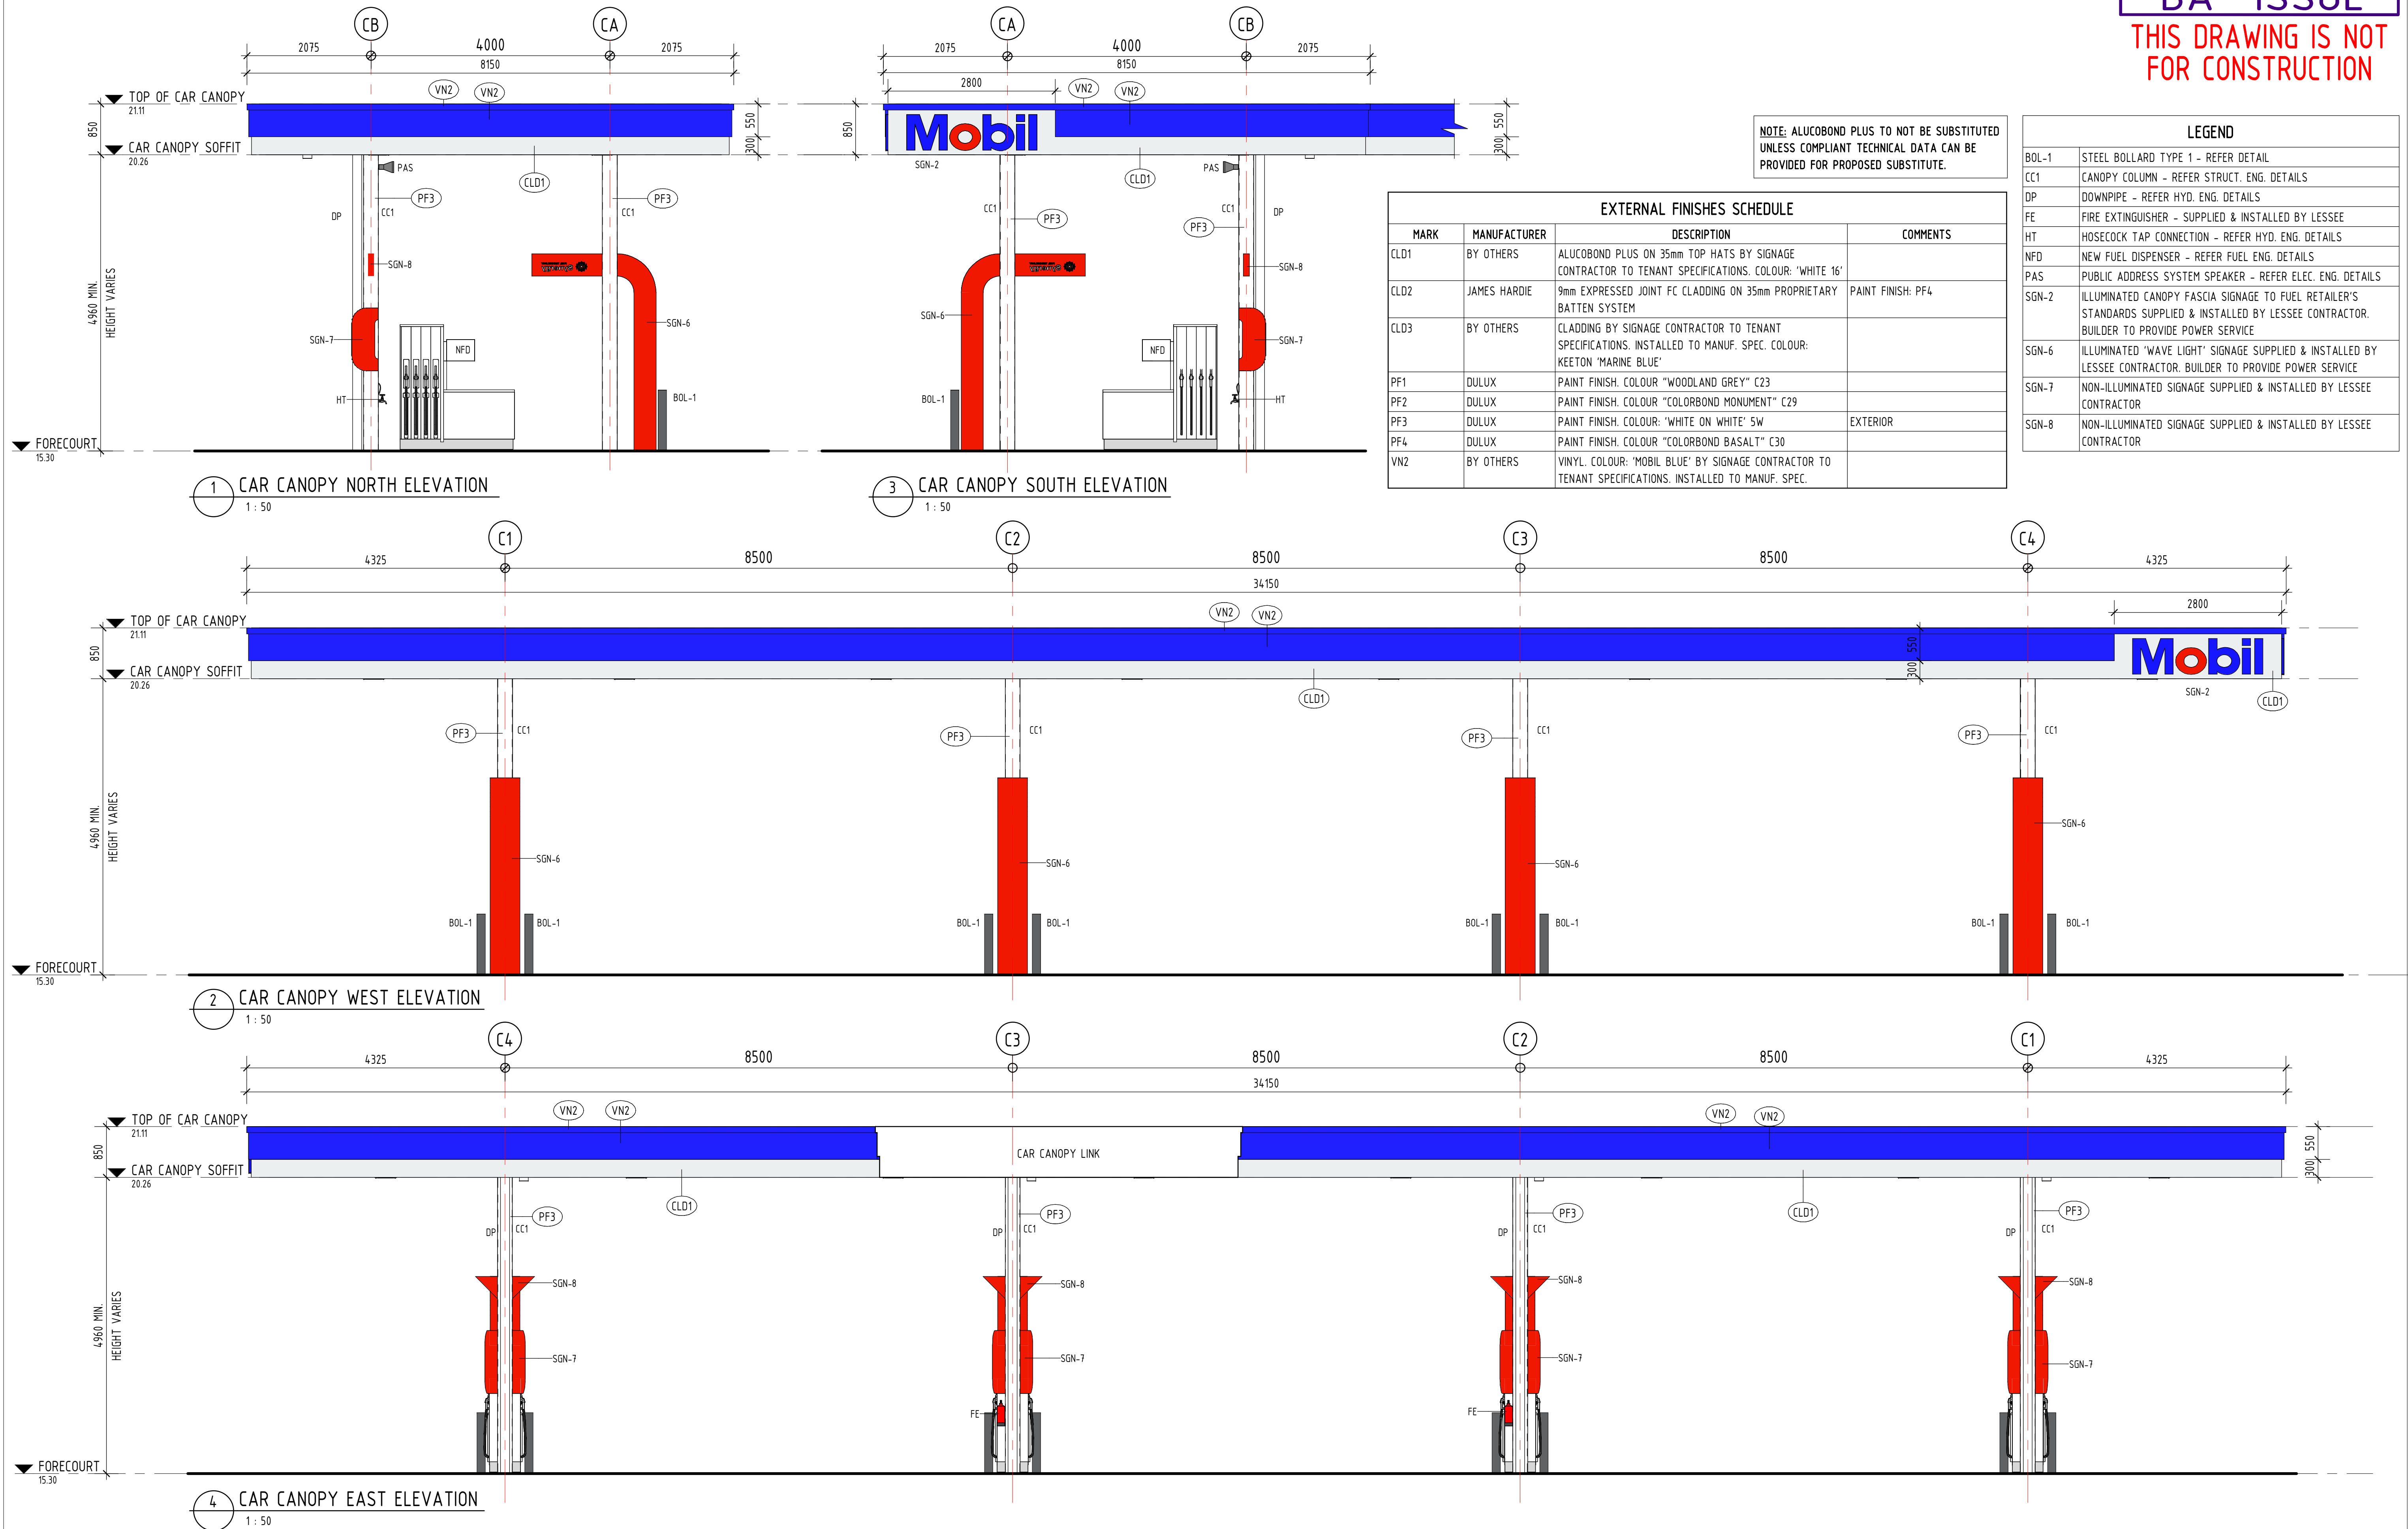


BA ISSUE

THIS DRAWING IS NOT FOR CONSTRUCTION

NOTE: ALUCOBOND PLUS TO NOT BE SUBSTITUTED UNLESS COMPLIANT TECHNICAL DATA CAN BE PROVIDED FOR PROPOSED SUBSTITUTE.


LEGEND	
AHR	AIR HOSE REEL
BOL-3	STEEL BOLLARD TYPE 3 - REFER DETAIL
CC1	CANOPY COLUMN - REFER STRUCT. ENG. DETAILS
DP	DOWNPIPE - REFER HYD. ENG. DETAILS
FE	FIRE EXTINGUISHER - SUPPLIED & INSTALLED BY LESSEE
HT	HOSECOCK TAP CONNECTION - REFER HYD. ENG. DETAILS
NAD	NEW AD BLUE FUEL DISPENSER - REFER FUEL ENG. DETAILS
NFD	NEW FUEL DISPENSER - REFER FUEL ENG. DETAILS
PAS	PUBLIC ADDRESS SYSTEM SPEAKER - REFER ELEC. ENG. DETAILS
PTD-2	FORECOURT PAPER TOWEL DISPENSER SUPPLIED & INSTALLED BY LESSEE
RAP	SURFACE MOUNT ROOF ACCESS POINT LADDER SUPPORT BRACKET INSTALLED TO MAN. SPEC.
SGN-2	ILLUMINATED CANOPY FASCIA SIGNAGE TO FUEL RETAILER'S STANDARDS SUPPLIED & INSTALLED BY LESSEE CONTRACTOR. BUILDER TO PROVIDE POWER SERVICE

EXTERNAL FINISHES SCHEDULE			
MARK	MANUFACTURER	DESCRIPTION	COMMENTS
CLD1	BY OTHERS	ALUCOBOND PLUS ON 35mm TOP HATS BY SIGNAGE CONTRACTOR TO TENANT SPECIFICATIONS. COLOUR: 'WHITE 16'	
CLD2	JAMES HARDIE	9mm EXPRESSED JOINT FC CLADDING ON 35mm PROPRIETARY BATTEN SYSTEM	PAINT FINISH: PF4
CLD3	BY OTHERS	CLADDING BY SIGNAGE CONTRACTOR TO TENANT SPECIFICATIONS. INSTALLED TO MANUF. SPEC. COLOUR: KEETON 'MARINE BLUE'	
PF1	DULUX	PAINT FINISH. COLOUR "WOODLAND GREY" C23	
PF2	DULUX	PAINT FINISH. COLOUR "COLORBOND MONUMENT" C29	
PF3	DULUX	PAINT FINISH. COLOUR: 'WHITE ON WHITE' 5W	EXTERIOR
PF4	DULUX	PAINT FINISH. COLOUR "COLORBOND BASALT" C30	
VN2	BY OTHERS	VINYL. COLOUR: 'MOBIL BLUE' BY SIGNAGE CONTRACTOR TO TENANT SPECIFICATIONS. INSTALLED TO MANUF. SPEC.	

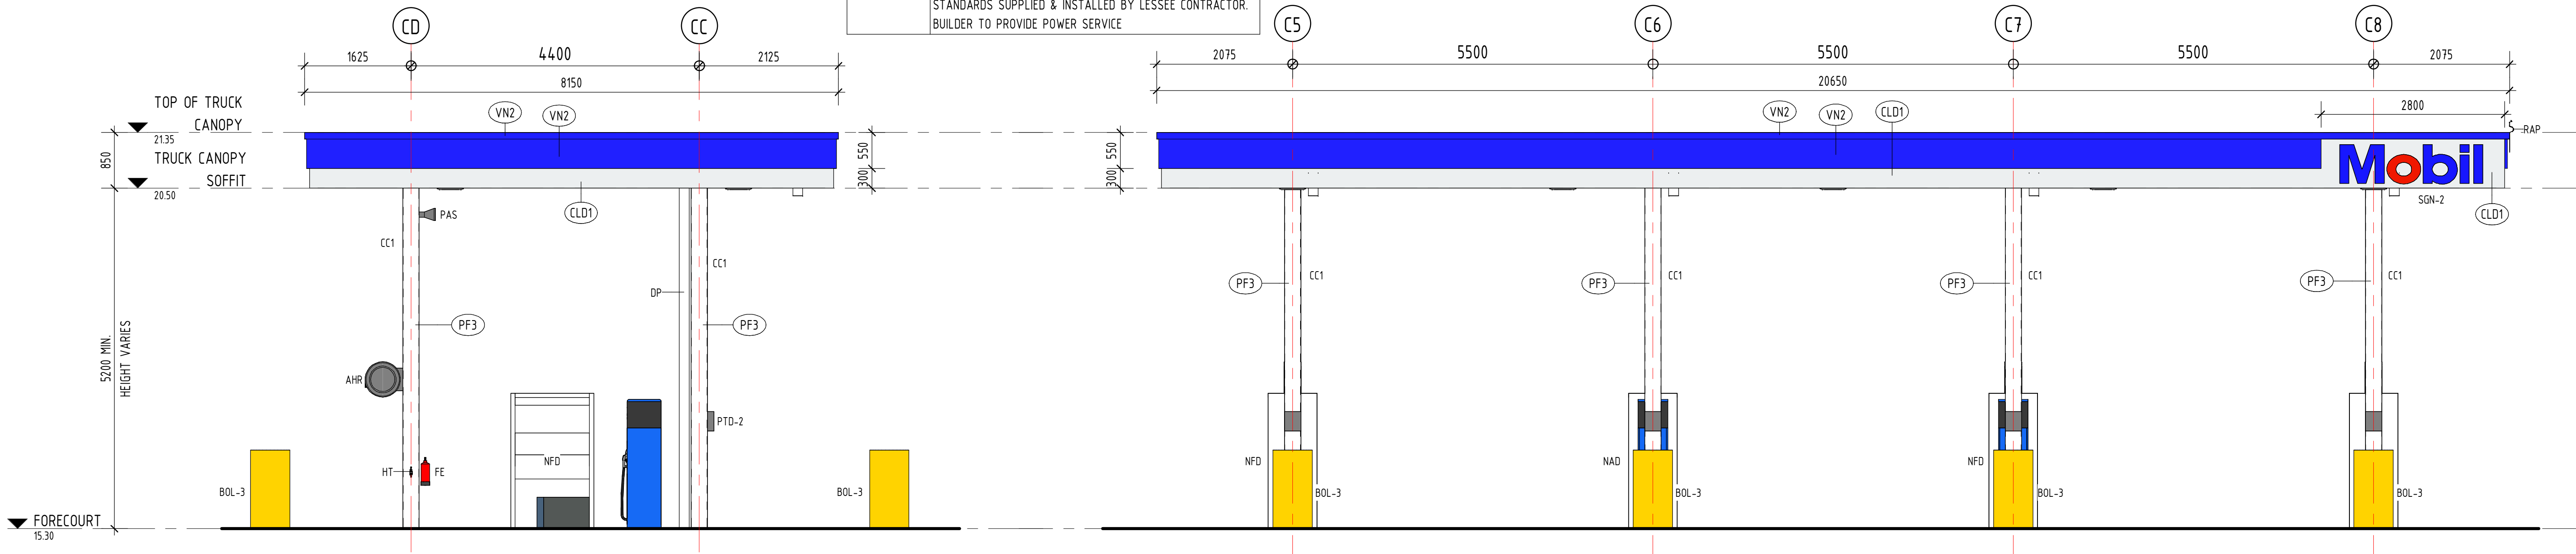


1 TRUCK CANOPY NORTH ELEVATION
1 : 50

2 TRUCK CANOPY WEST ELEVATION
1 : 50

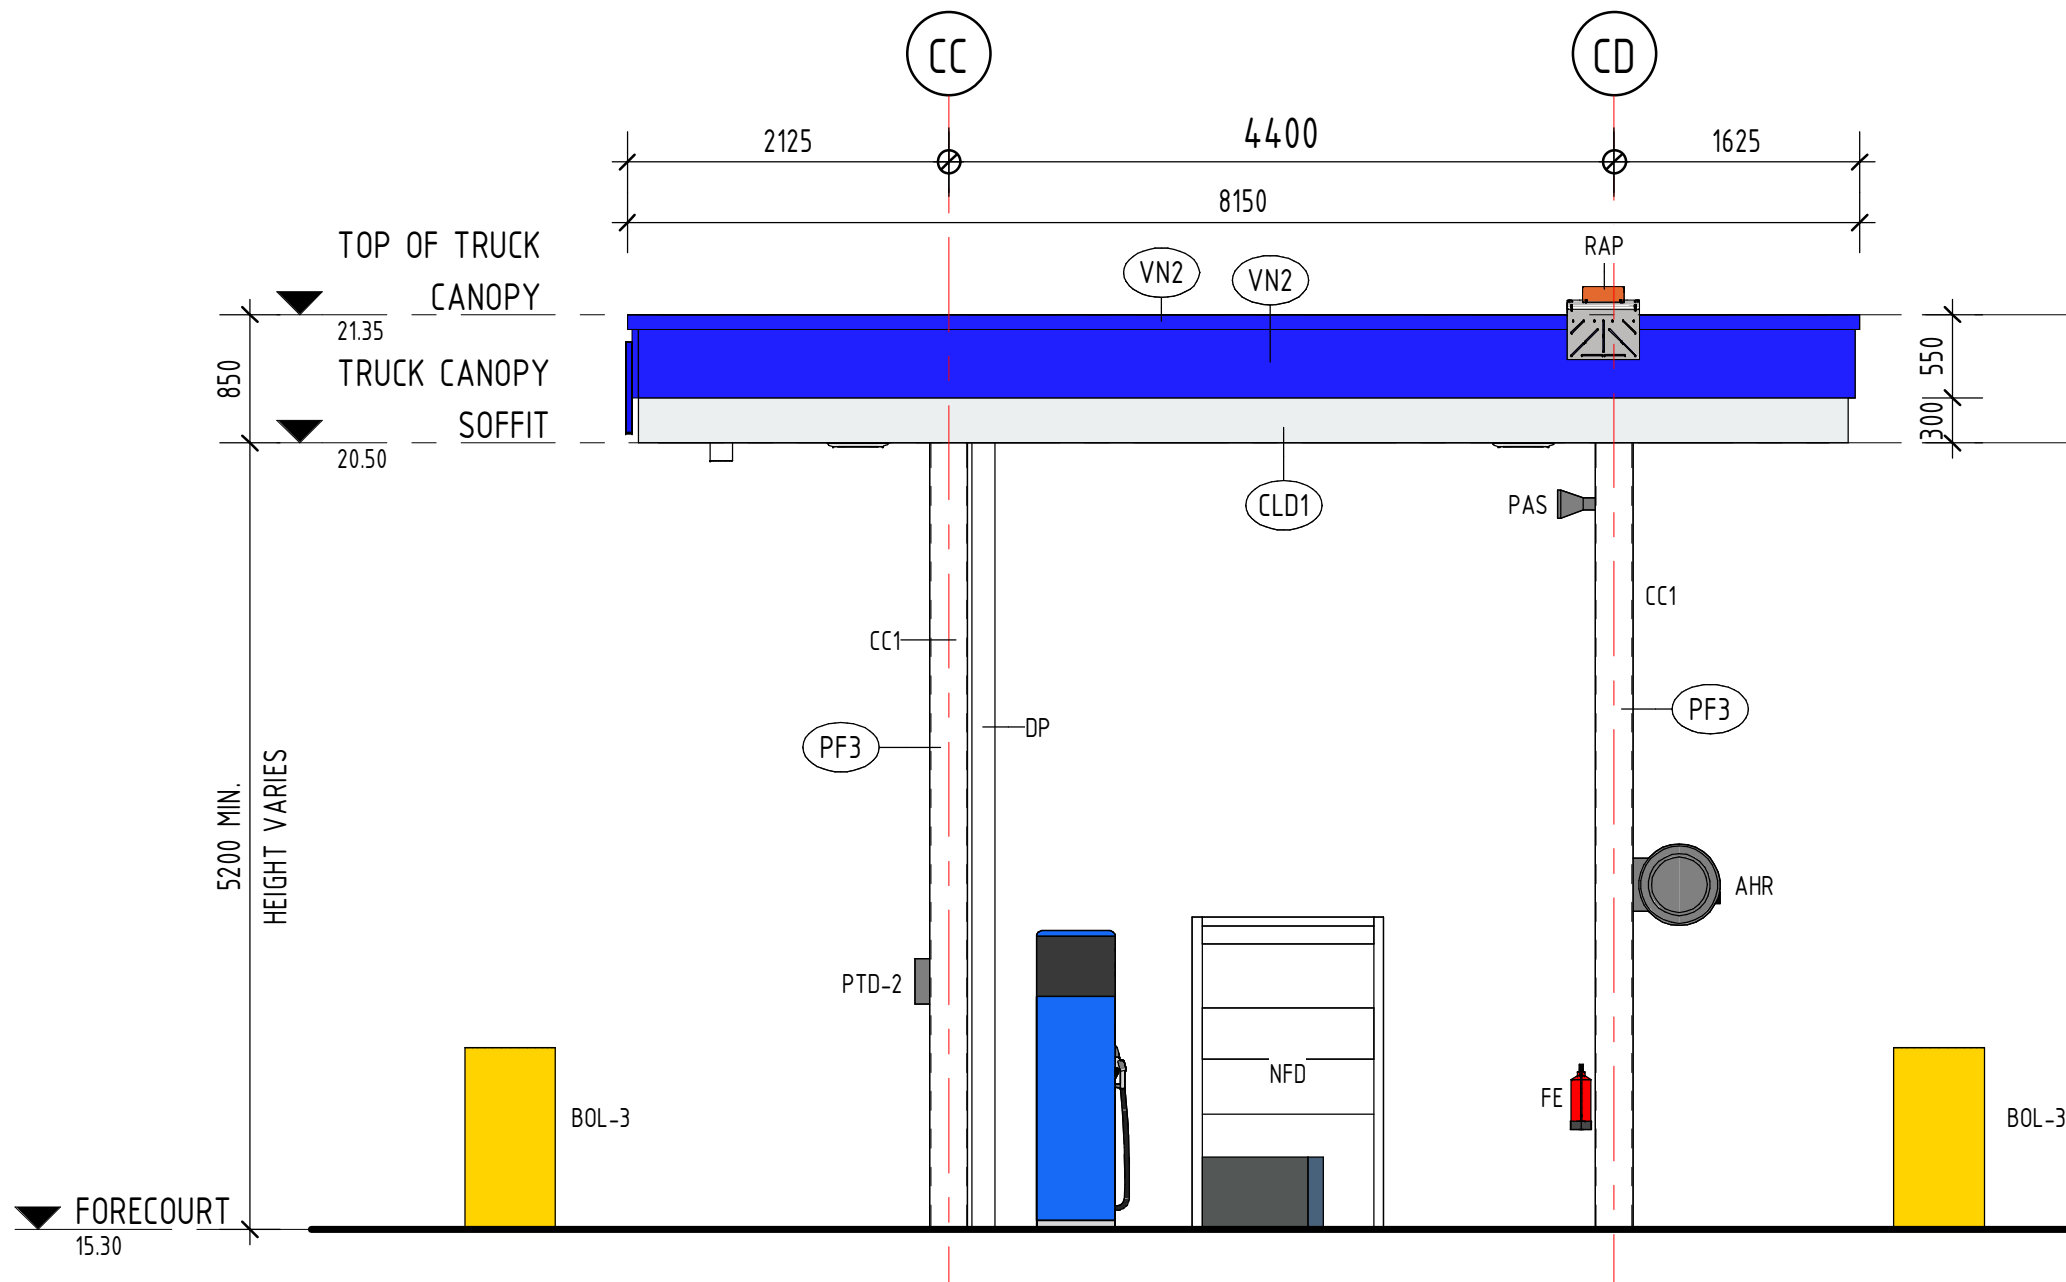

3 TRUCK CANOPY SOUTH ELEVATION
1 : 50

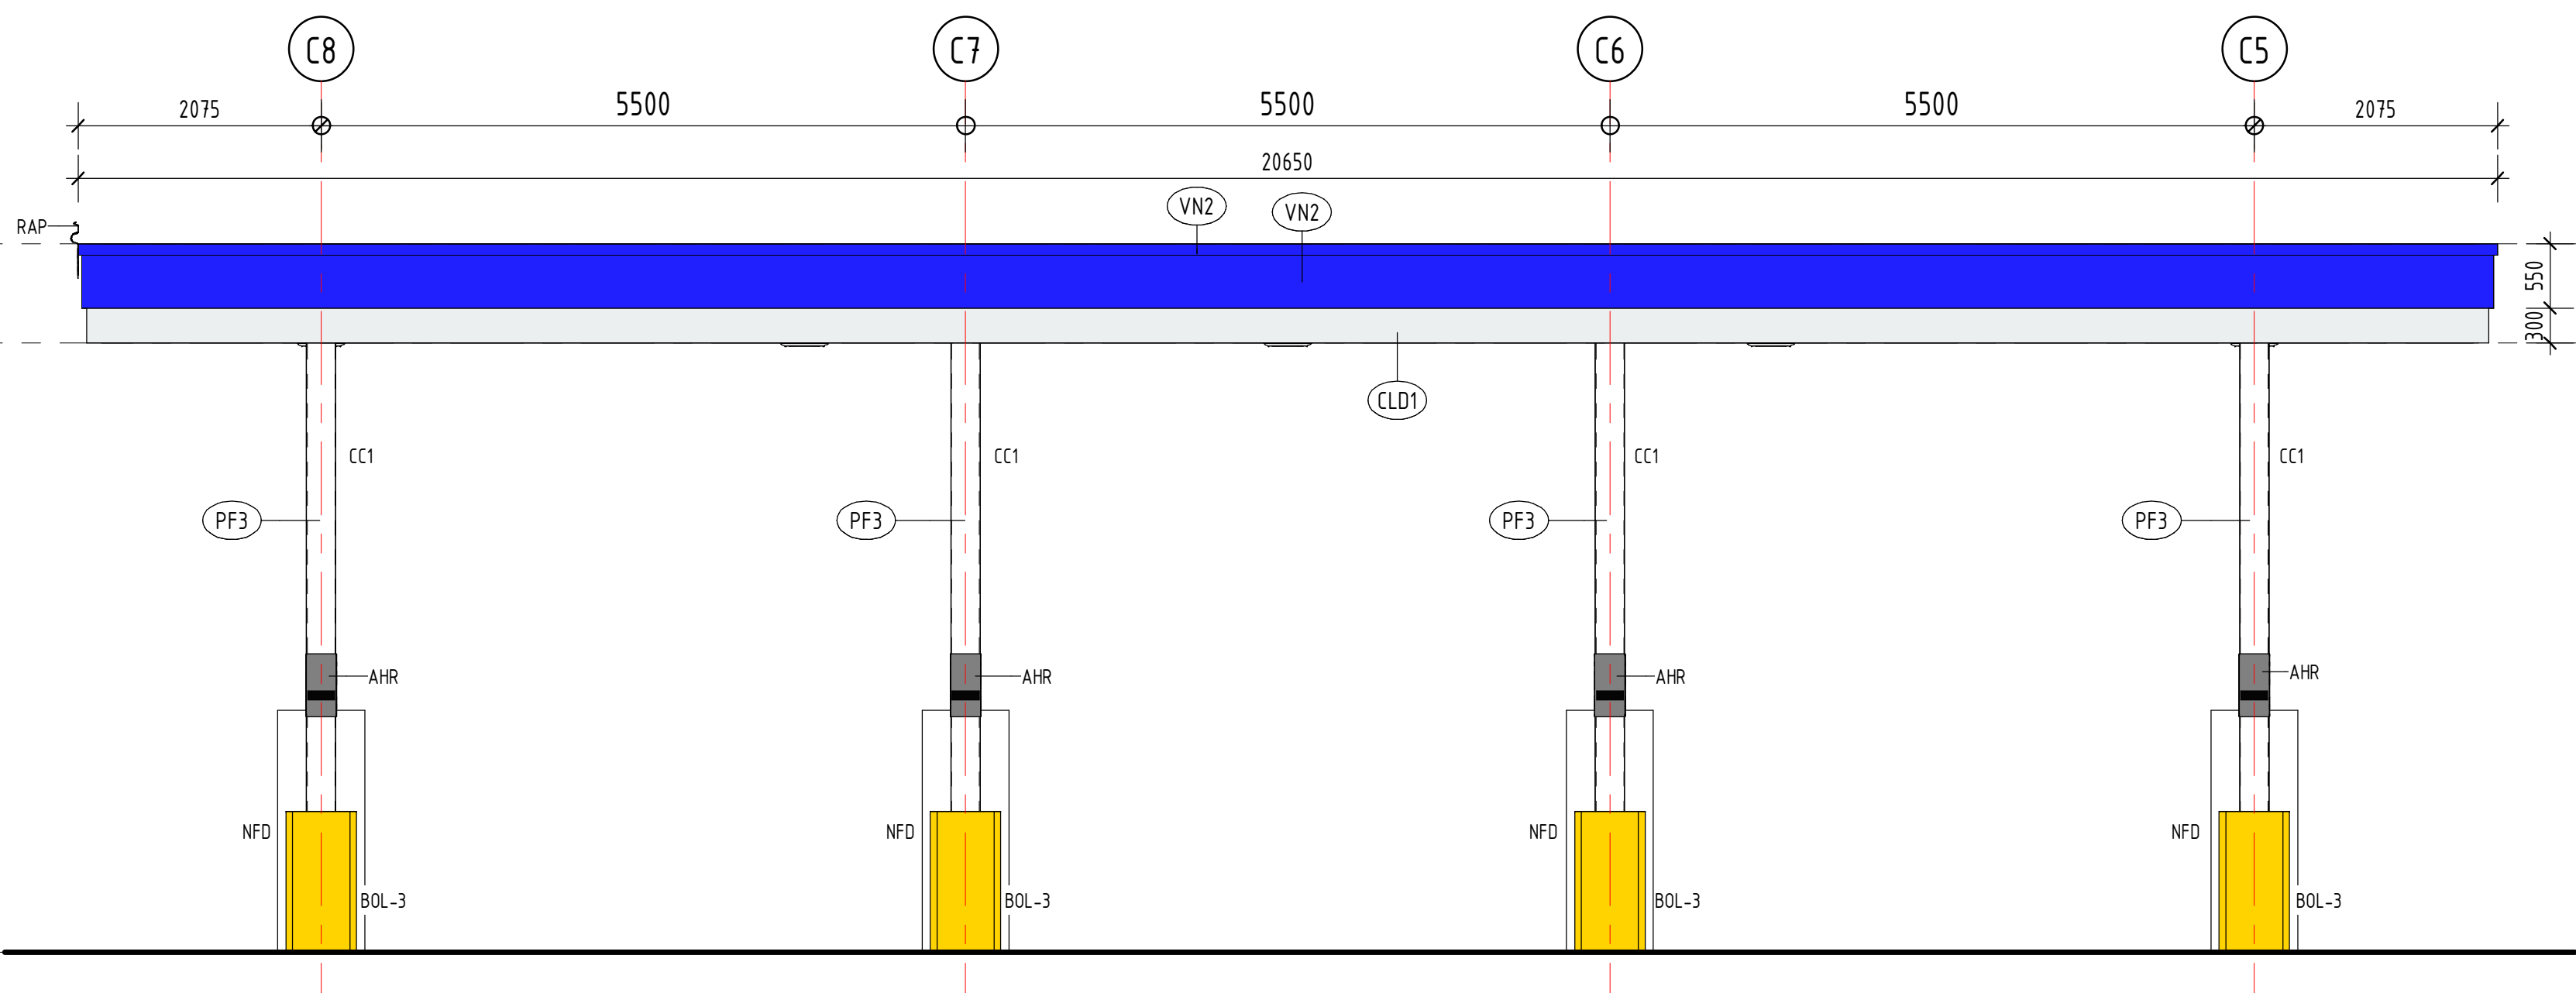

4 TRUCK CANOPY EAST ELEVATION
1 : 50

VERVE SCHEDULES DISCLAIMER:

1. ALL SCHEDULES SHOULD BE CHECKED WITH THE REMAINDER OF THE DRAWING SET.

2. SCHEDULED RATES AND AREAS ARE INTENDED FOR ASSISTANCE ONLY. NO RESPONSIBILITY IS TAKEN FOR THE ACCURACY OF QUANTITIES.

3. ANY DISCREPANCIES IN SCHEDULES SHOULD BE IDENTIFIED TO THE AUTHOR NOTED.

4. ALL AREAS ARE GROSS AREAS, UNLESS NOTED OTHERWISE

CONSULTING ENGINEER



- ☐ commercial
- ☐ mixed-use
- ☐ self storage
- ☐ industrial
- ☐ service stations
- ☐ quick service restaurants
- ☐ child care centres
- ☐ large format retail

© 2011 copyright, all rights reserved.

This drawing is the © copyright & property of VERVE DESIGN GROUP and must not be used or duplicated without authorisation.


Do not scale this drawing.

Check all dimensions on site prior commencement of works

Revision and approvals				
Rev	Date	Drn	Description	Appr
P1	12.02.2026	PC	PRELIMINARY ISSUE	SS
P2	01.05.2026	PC	REVISED PRELIMINARY ISSUE	SS
A	19.06.2026	PC	BA ISSUE	SS


Project Description	
PROPOSED SERVICE STATION	
22 ENTERPRISE CCT., MARYBOROUGH W.	
Scale @A1 1 : 50	Date FEBRUARY 2026
Drawn PC	Approved By SS

Drawing Title	
PROP. TRUCK FORECOURT CANOPY ELEVATIONS	
Job Number - Drawing Number 26024 A261	Revision A

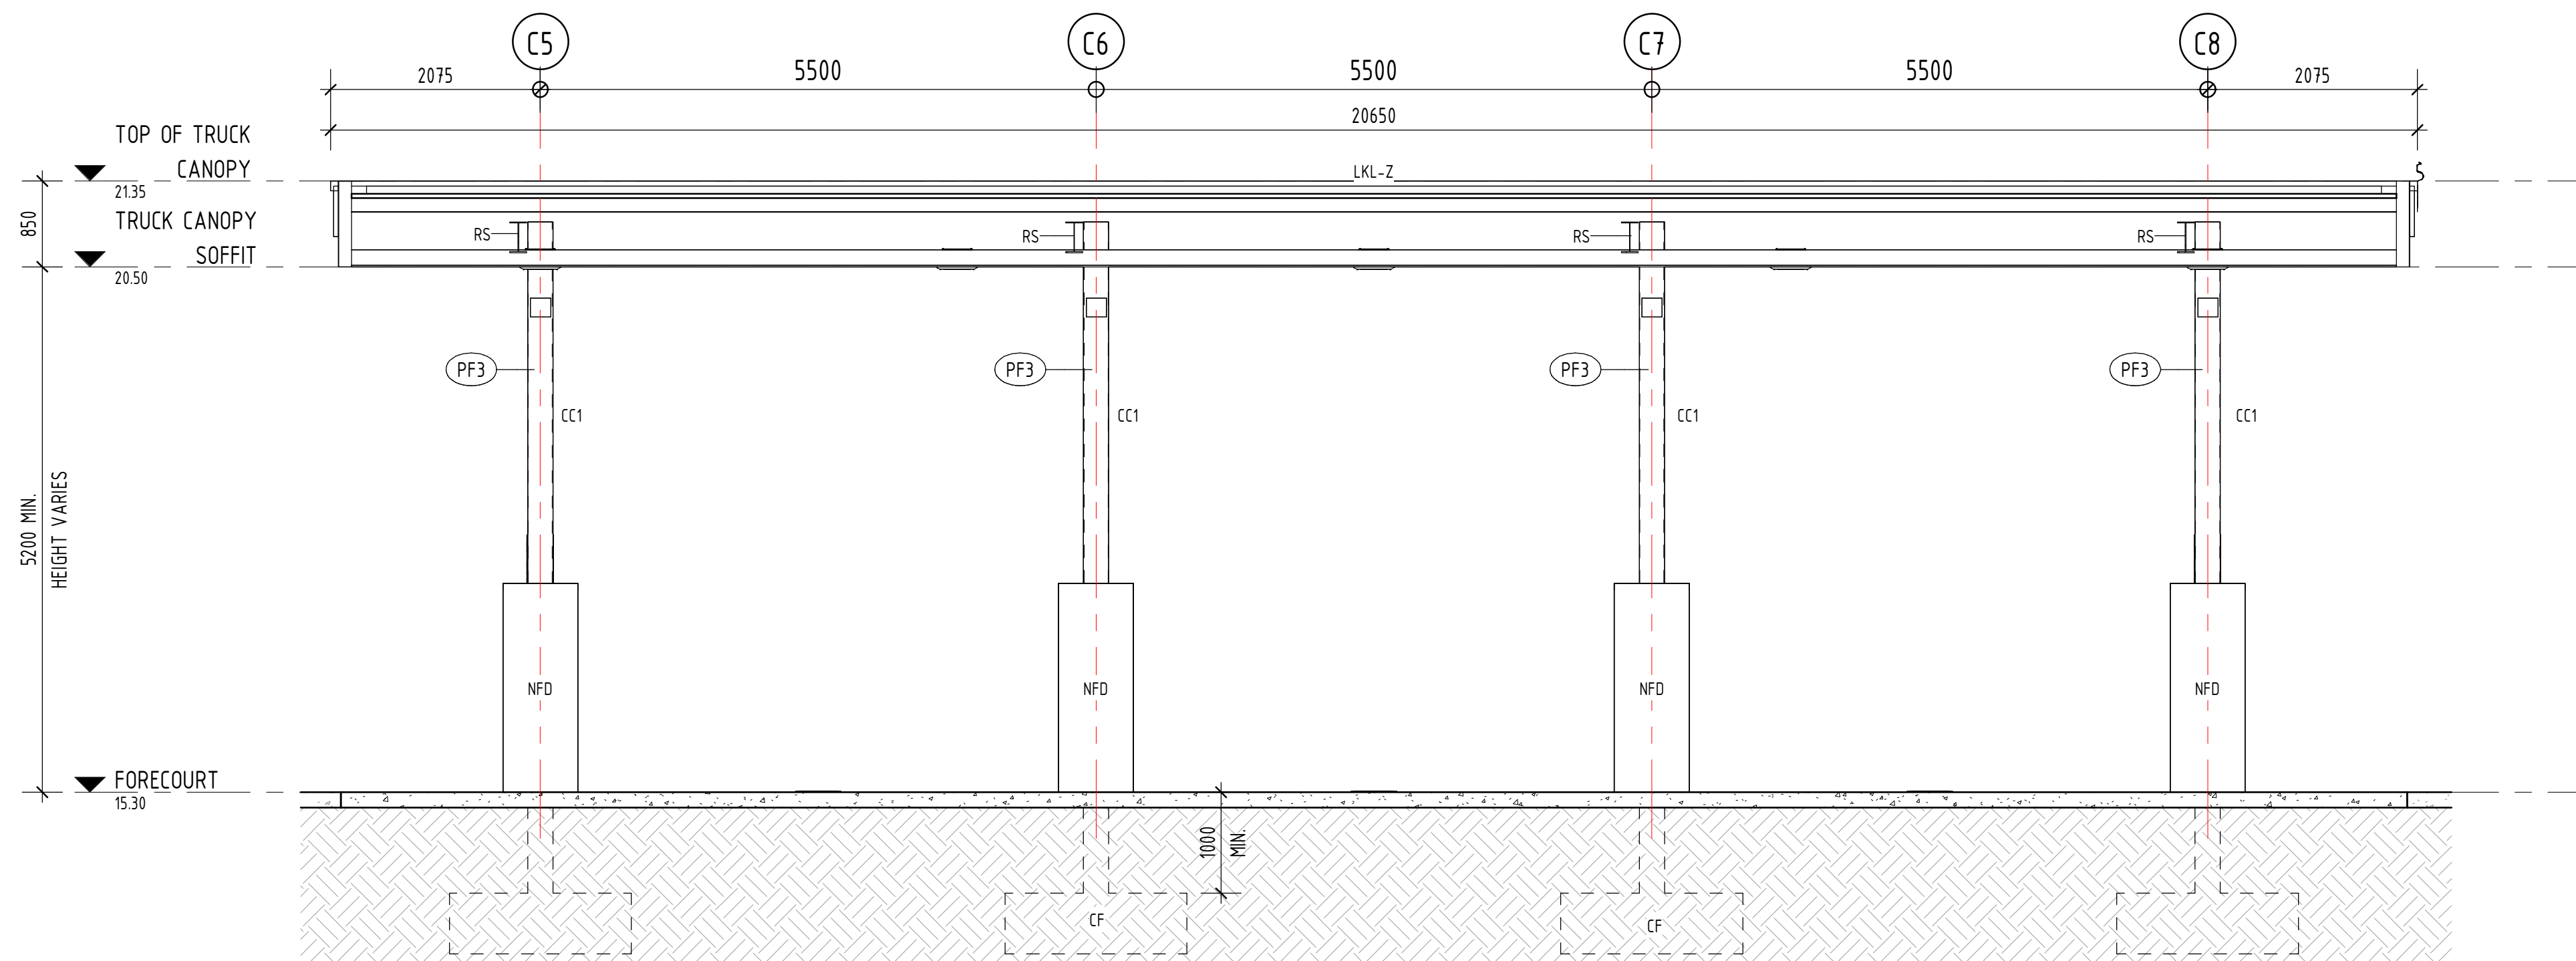

1 TRUCK CANOPY SECTION 1

1 : 50

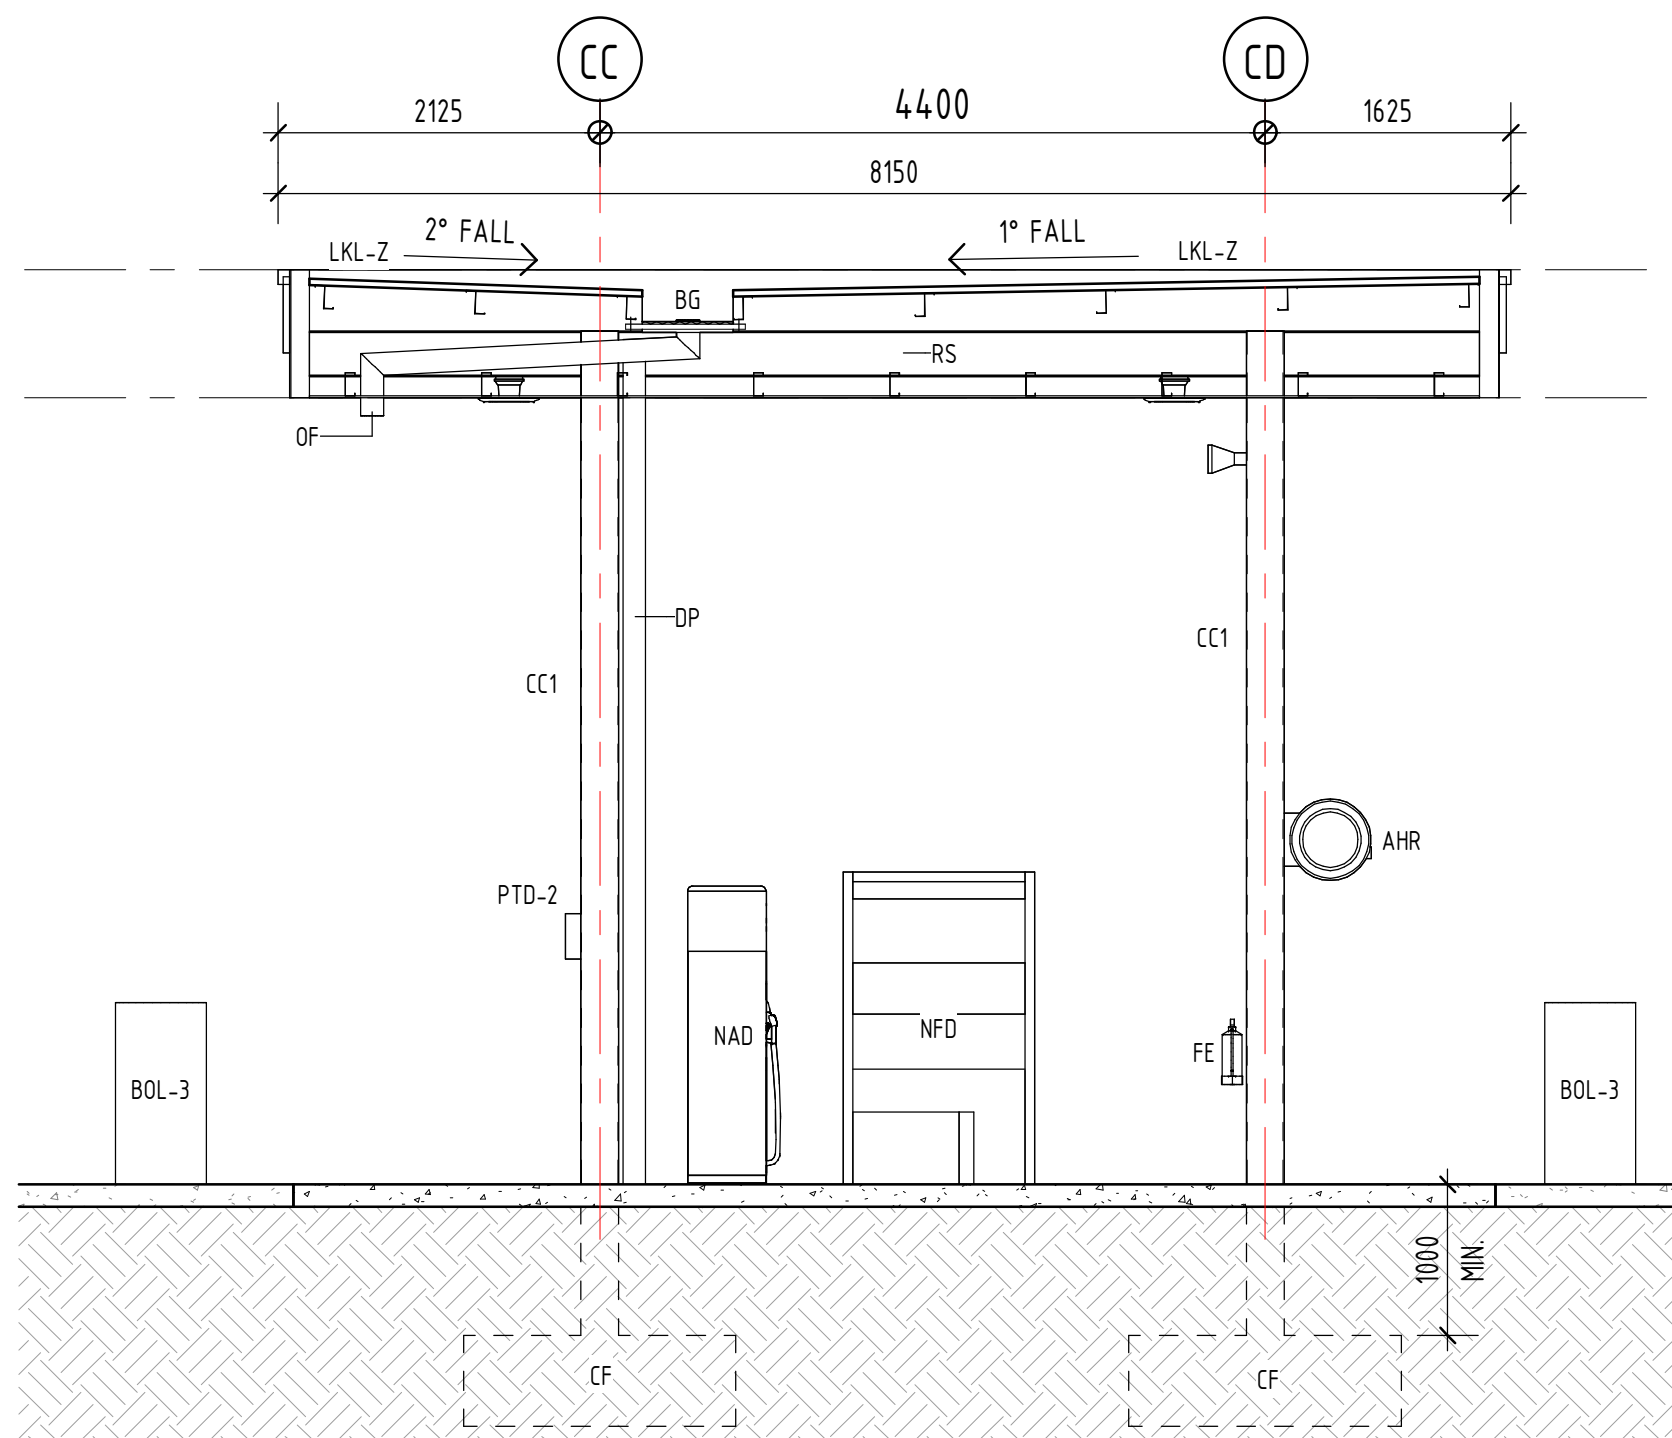

2 TRUCK CANOPY SECTION 2

1 : 50

NOTE: ALUCOBOND PLUS TO NOT BE SUBSTITUTED UNLESS COMPLIANT TECHNICAL DATA CAN BE PROVIDED FOR PROPOSED SUBSTITUTE.

EXTERNAL FINISHES SCHEDULE			
MARK	MANUFACTURER	DESCRIPTION	COMMENTS
CLD1	BY OTHERS	ALUCOBOND PLUS ON 35mm TOP HATS BY SIGNAGE CONTRACTOR TO TENANT SPECIFICATIONS. COLOUR: 'WHITE 16'	
CLD2	JAMES HARDIE	9mm EXPRESSED JOINT FC CLADDING ON 35mm PROPRIETARY BATTEN SYSTEM	PAINT FINISH: PF4
CLD3	BY OTHERS	CLADDING BY SIGNAGE CONTRACTOR TO TENANT SPECIFICATIONS. INSTALLED TO MANUF. SPEC. COLOUR: KEETON 'MARINE BLUE'	
PF1	DULUX	PAINT FINISH. COLOUR 'WOODLAND GREY' C23	
PF2	DULUX	PAINT FINISH. COLOUR 'COLORBOND MONUMENT' C29	
PF3	DULUX	PAINT FINISH. COLOUR: 'WHITE ON WHITE' 5W	EXTERIOR
PF4	DULUX	PAINT FINISH. COLOUR 'COLORBOND BASALT' C30	
VN2	BY OTHERS	VINYL. COLOUR: 'MOBIL BLUE' BY SIGNAGE CONTRACTOR TO TENANT SPECIFICATIONS. INSTALLED TO MANUF. SPEC.	

LEGEND	
AHR	AIR HOSE REEL
BG	BOX GUTTER - REFER HYD. ENG. DETAILS
BOL-3	STEEL BOLLARD TYPE 3 - REFER DETAIL
CC1	CANOPY COLUMN - REFER STRUCT. ENG. DETAILS
CF	CONCRETE FOOTING - REFER STRUCT. ENG. DETAILS
DP	DOWNPIPE - REFER HYD. ENG. DETAILS
FE	FIRE EXTINGUISHER - SUPPLIED & INSTALLED BY LESSEE
LKL-Z	LYSAGHT KLIP-LOK HI STRENGTH 0.48BMT ZINCALUME
NAD	NEW AD BLUE FUEL DISPENSER - REFER FUEL ENG. DETAILS
NFD	NEW FUEL DISPENSER - REFER FUEL ENG. DETAILS
OF	OVERFLOW - REFER HYD. ENG. DETAILS
PTD-2	FORECOURT PAPER TOWEL DISPENSER SUPPLIED & INSTALLED BY LESSEE
RS	ROOF STRUCTURE - REFER STRUCT. ENG. DETAILS

VERVE SCHEDULES DISCLAIMER:

1. ALL SCHEDULES SHOULD BE CHECKED WITH THE REMAINDER OF THE DRAWING SET.

2. SCHEDULED RATES AND AREAS ARE INTENDED FOR ASSISTANCE ONLY. NO RESPONSIBILITY IS TAKEN FOR THE ACCURACY OF QUANTITIES.

3. ANY DISCREPANCIES IN SCHEDULES SHOULD BE IDENTIFIED TO THE AUTHOR NOTED.

4. ALL AREAS ARE GROSS AREAS, UNLESS NOTED OTHERWISE

CONSULTING ENGINEER



☐ commercial ☐ service stations ☐ mixed-use ☐ quick service restaurants ☐ self storage ☐ child care centres ☐ industrial ☐ large format retail

© 2011 copyright, all rights reserved.
This drawing is the © copyright & property of VERVE DESIGN GROUP and must not be used or duplicated without authorisation.
Do not scale this drawing.
Check all dimensions on site prior commencement of works

Revision and approvals				
Rev	Date	Drn	Description	Appr
P1	12.02.2026	PC	PRELIMINARY ISSUE	SS
P2	01.05.2026	PC	REVISED PRELIMINARY ISSUE	SS
A	19.06.2026	PC	BA ISSUE	SS

Project Description
PROPOSED SERVICE STATION
22 ENTERPRISE CCT., MARYBOROUGH W.


Scale @A1
1 : 50
Drawn
PC

Date
FEBRUARY 2026
Approved By
SS


Drawing Title
PROP. FORECOURT TRUCK CANOPY SECTIONS

Job Number - Drawing Number
26024 A262

Revision
A

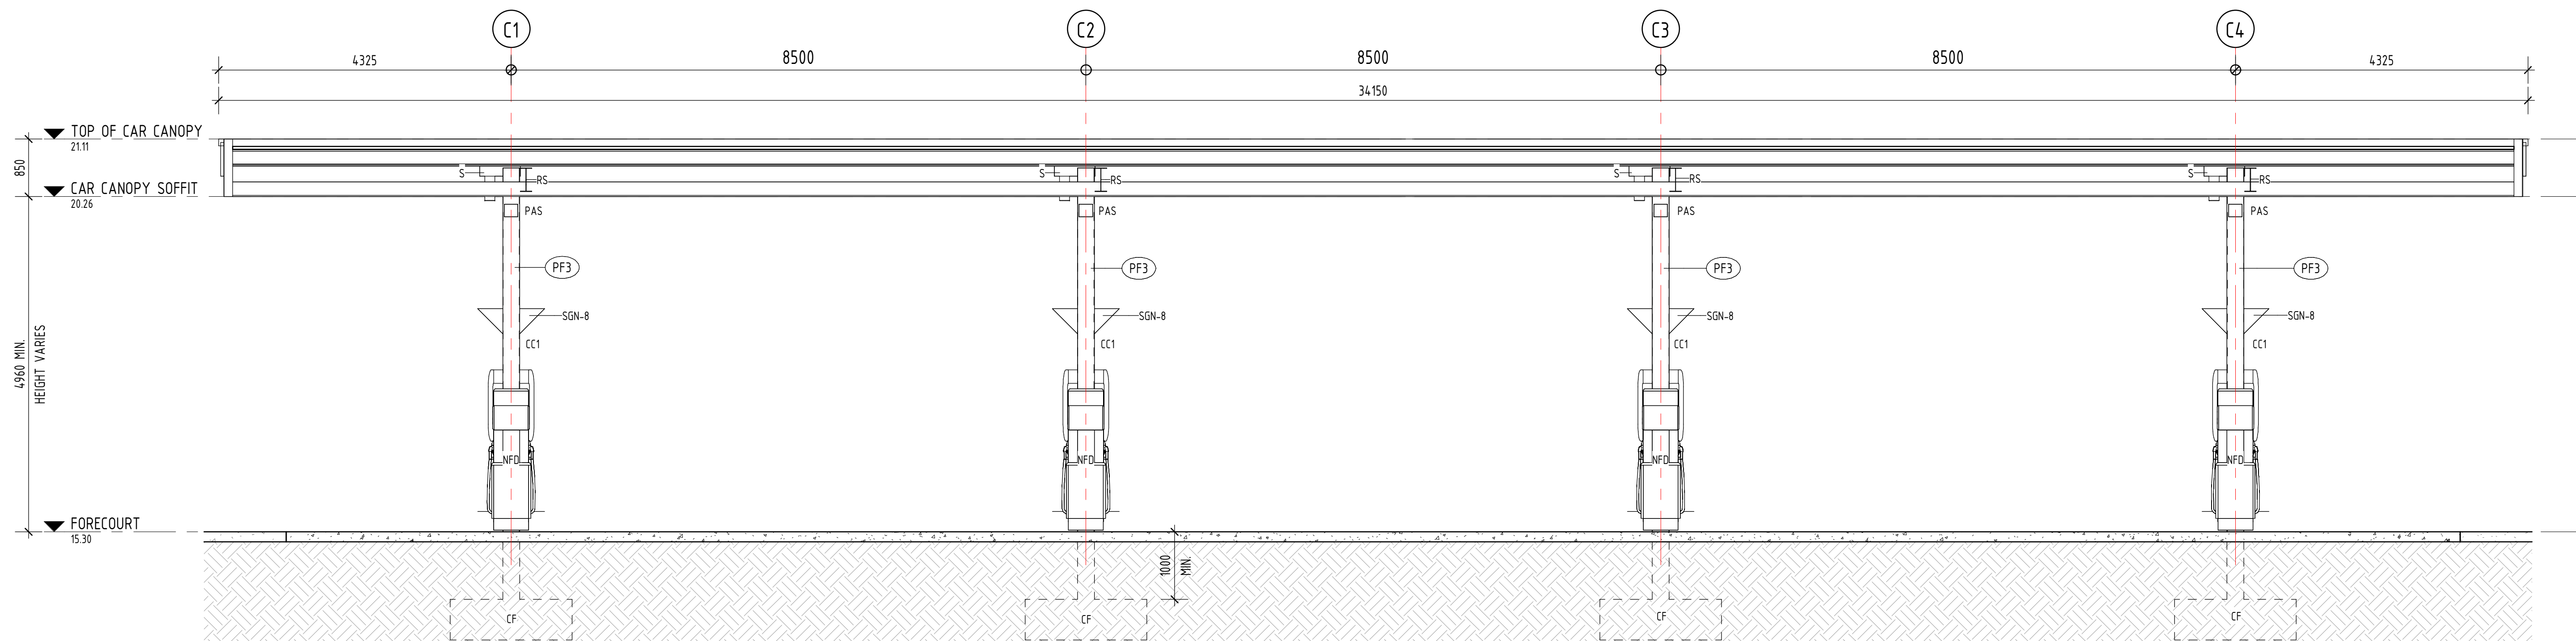

1 CAR CANOPY SECTION 1
1 : 50

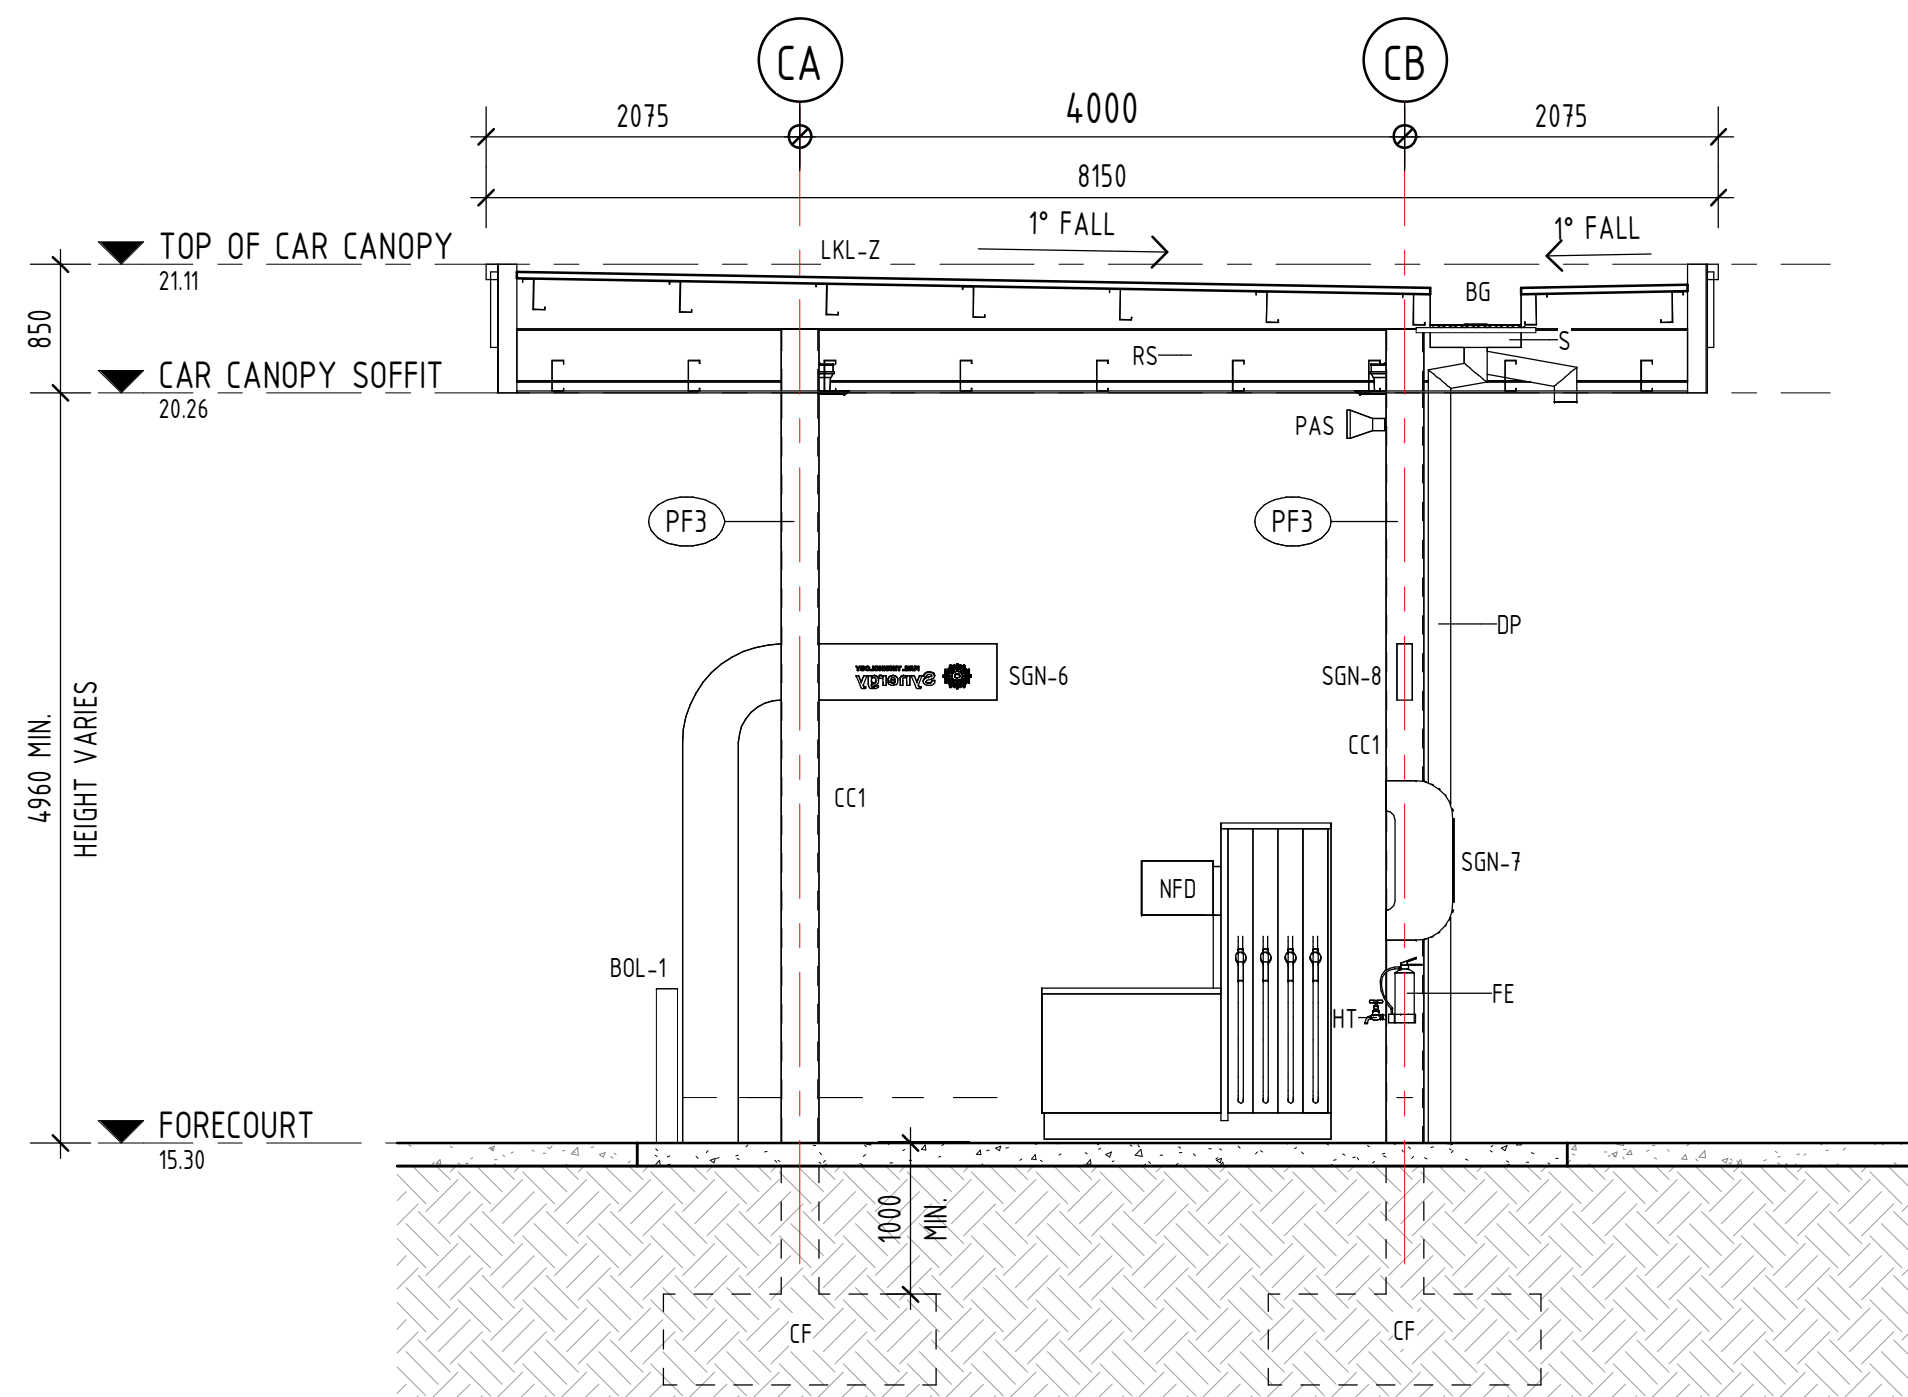

2 CAR CANOPY SECTION 2
1 : 50

NOTE: ALUCOBOND PLUS TO NOT BE SUBSTITUTED
UNLESS COMPLIANT TECHNICAL DATA CAN BE
PROVIDED FOR PROPOSED SUBSTITUTE.

EXTERNAL FINISHES SCHEDULE			
MARK	MANUFACTURER	DESCRIPTION	COMMENTS
CLD1	BY OTHERS	ALUCOBOND PLUS ON 35mm TOP HATS BY SIGNAGE CONTRACTOR TO TENANT SPECIFICATIONS. COLOUR: 'WHITE 16'	
CLD2	JAMES HARDIE	9mm EXPRESSED JOINT FC CLADDING ON 35mm PROPRIETARY BATTEN SYSTEM	PAINT FINISH: PF4
CLD3	BY OTHERS	CLADDING BY SIGNAGE CONTRACTOR TO TENANT SPECIFICATIONS. INSTALLED TO MANUF. SPEC. COLOUR: KEETON 'MARINE BLUE'	
PF1	DULUX	PAINT FINISH. COLOUR "WOODLAND GREY" C23	
PF2	DULUX	PAINT FINISH. COLOUR "COLORBOND MONUMENT" C29	
PF3	DULUX	PAINT FINISH. COLOUR: 'WHITE ON WHITE' 5W	EXTERIOR
PF4	DULUX	PAINT FINISH. COLOUR "COLORBOND BASALT" C30	
VN2	BY OTHERS	VINYL. COLOUR: 'MOBIL BLUE' BY SIGNAGE CONTRACTOR TO TENANT SPECIFICATIONS. INSTALLED TO MANUF. SPEC.	

LEGEND	
BG	BOX GUTTER - REFER HYD. ENG. DETAILS
BOL-1	STEEL BOLLARD TYPE 1 - REFER DETAIL
CC1	CANOPY COLUMN - REFER STRUCT. ENG. DETAILS
CF	CONCRETE FOOTING - REFER STRUCT. ENG. DETAILS
DP	DOWNPIPE - REFER HYD. ENG. DETAILS
FE	FIRE EXTINGUISHER - SUPPLIED & INSTALLED BY LESSEE
HT	HOSECOCK TAP CONNECTION - REFER HYD. ENG. DETAILS
LKL-Z	LYSAGHT KLIP-LOK HI STRENGTH 0.48BMT ZINCALUME
NFD	NEW FUEL DISPENSER - REFER FUEL ENG. DETAILS
PAS	PUBLIC ADDRESS SYSTEM SPEAKER - REFER ELEC. ENG. DETAILS
RS	ROOF STRUCTURE - REFER STRUCT. ENG. DETAILS
S	SUMP - REFER HYD. ENG. DETAILS
SGN-6	ILLUMINATED 'WAVE LIGHT' SIGNAGE SUPPLIED & INSTALLED BY LESSEE CONTRACTOR. BUILDER TO PROVIDE POWER SERVICE
SGN-7	NON-ILLUMINATED SIGNAGE SUPPLIED & INSTALLED BY LESSEE CONTRACTOR
SGN-8	NON-ILLUMINATED SIGNAGE SUPPLIED & INSTALLED BY LESSEE CONTRACTOR

VERVE SCHEDULES DISCLAIMER:

- ALL SCHEDULES SHOULD BE CHECKED WITH THE REMAINDER OF THE DRAWING SET.
- SCHEDULED RATES AND AREAS ARE INTENDED FOR ASSISTANCE ONLY. NO RESPONSIBILITY IS TAKEN FOR THE ACCURACY OF QUANTITIES.
- ANY DISCREPANCIES IN SCHEDULES SHOULD BE IDENTIFIED TO THE AUTHOR NOTED.
- ALL AREAS ARE GROSS AREAS, UNLESS NOTED OTHERWISE

CONSULTING ENGINEER




- ☐ commercial
- ☐ mixed-use
- ☐ self storage
- ☐ industrial
- ☐ service stations
- ☐ quick service restaurants
- ☐ child care centres
- ☐ large format retail


© 2011 copyright, all rights reserved.
This drawing is the copyright & property of VERVE DESIGN GROUP and must not be used or duplicated without authorisation.
Do not scale this drawing.
Check all dimensions on site prior commencement of works

Revision and approvals				
Rev	Date	Drn	Description	Appr
P1	01.05.2026	PC	REVISED PRELIMINARY ISSUE	SS
A	19.06.2026	PC	BA ISSUE	SS


Project Description		Scale		Date		Job Number - Drawing Number		Revision
PROPOSED SERVICE STATION		Scale @A1 1 : 50		FEBRUARY 2026		26024 A263		A
22 ENTERPRISE CCT., MARYBOROUGH W.		Drawn PC		Approved By SS				

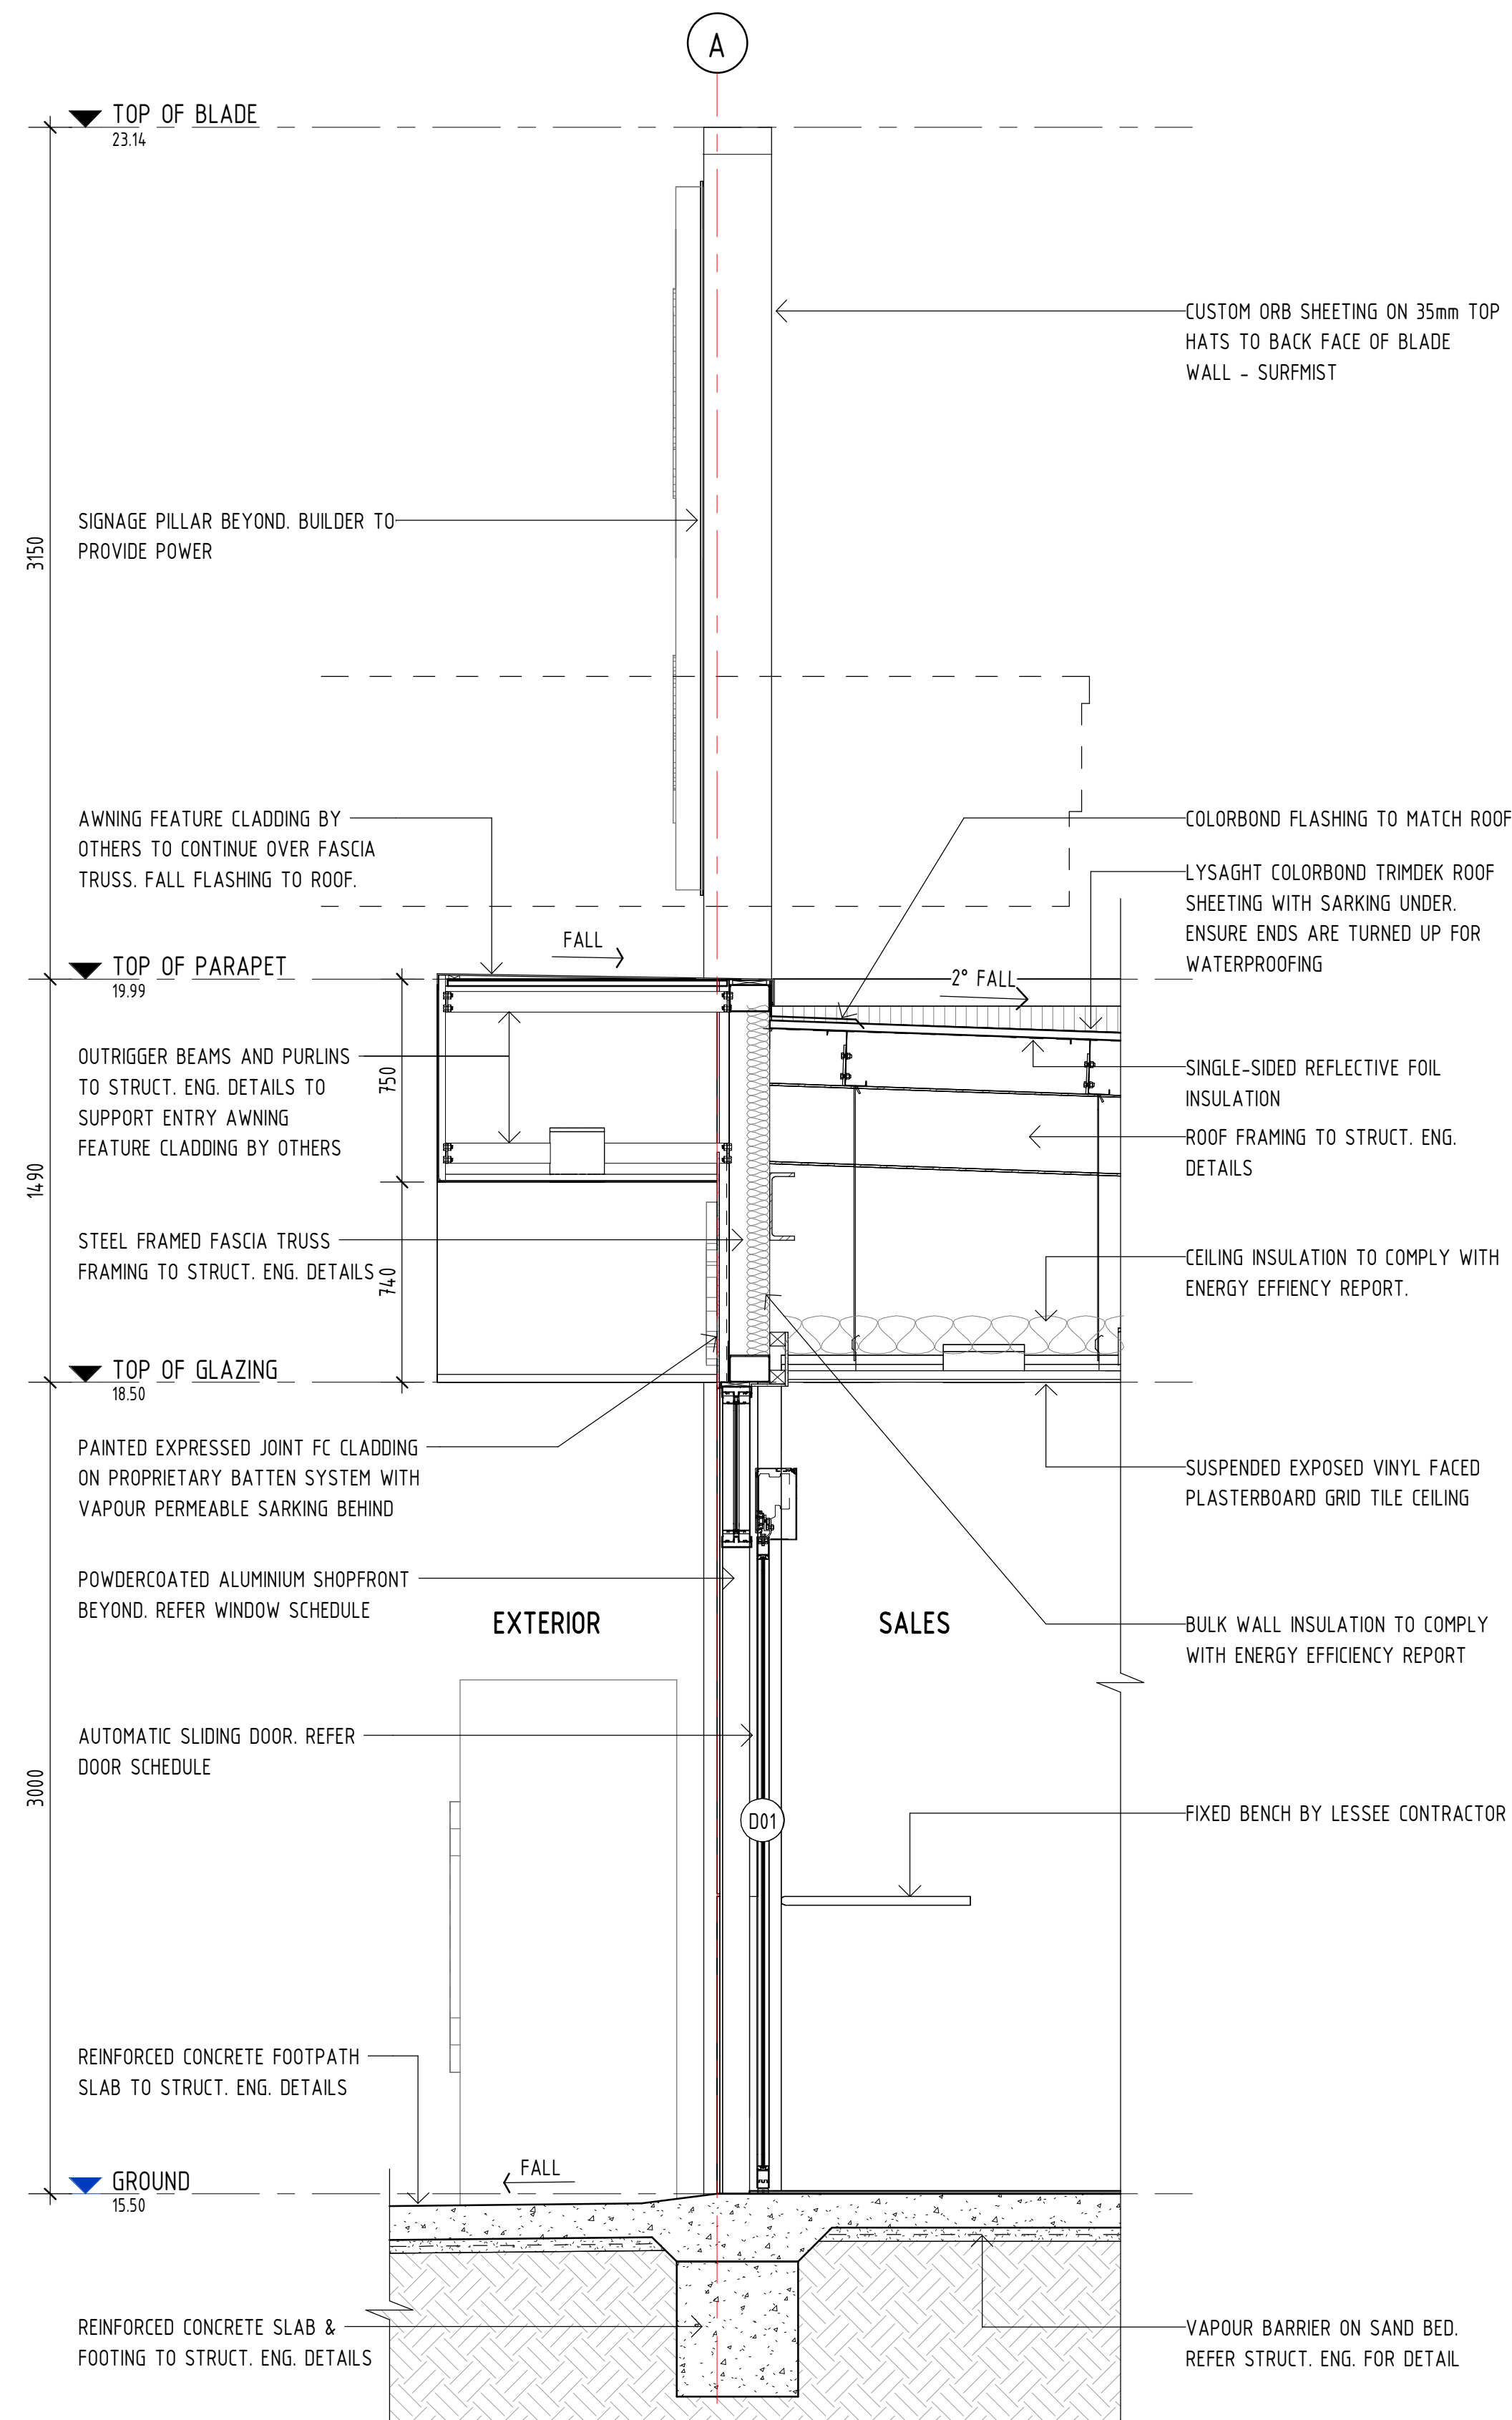

1 WALL SECTION 1
A210 1:20

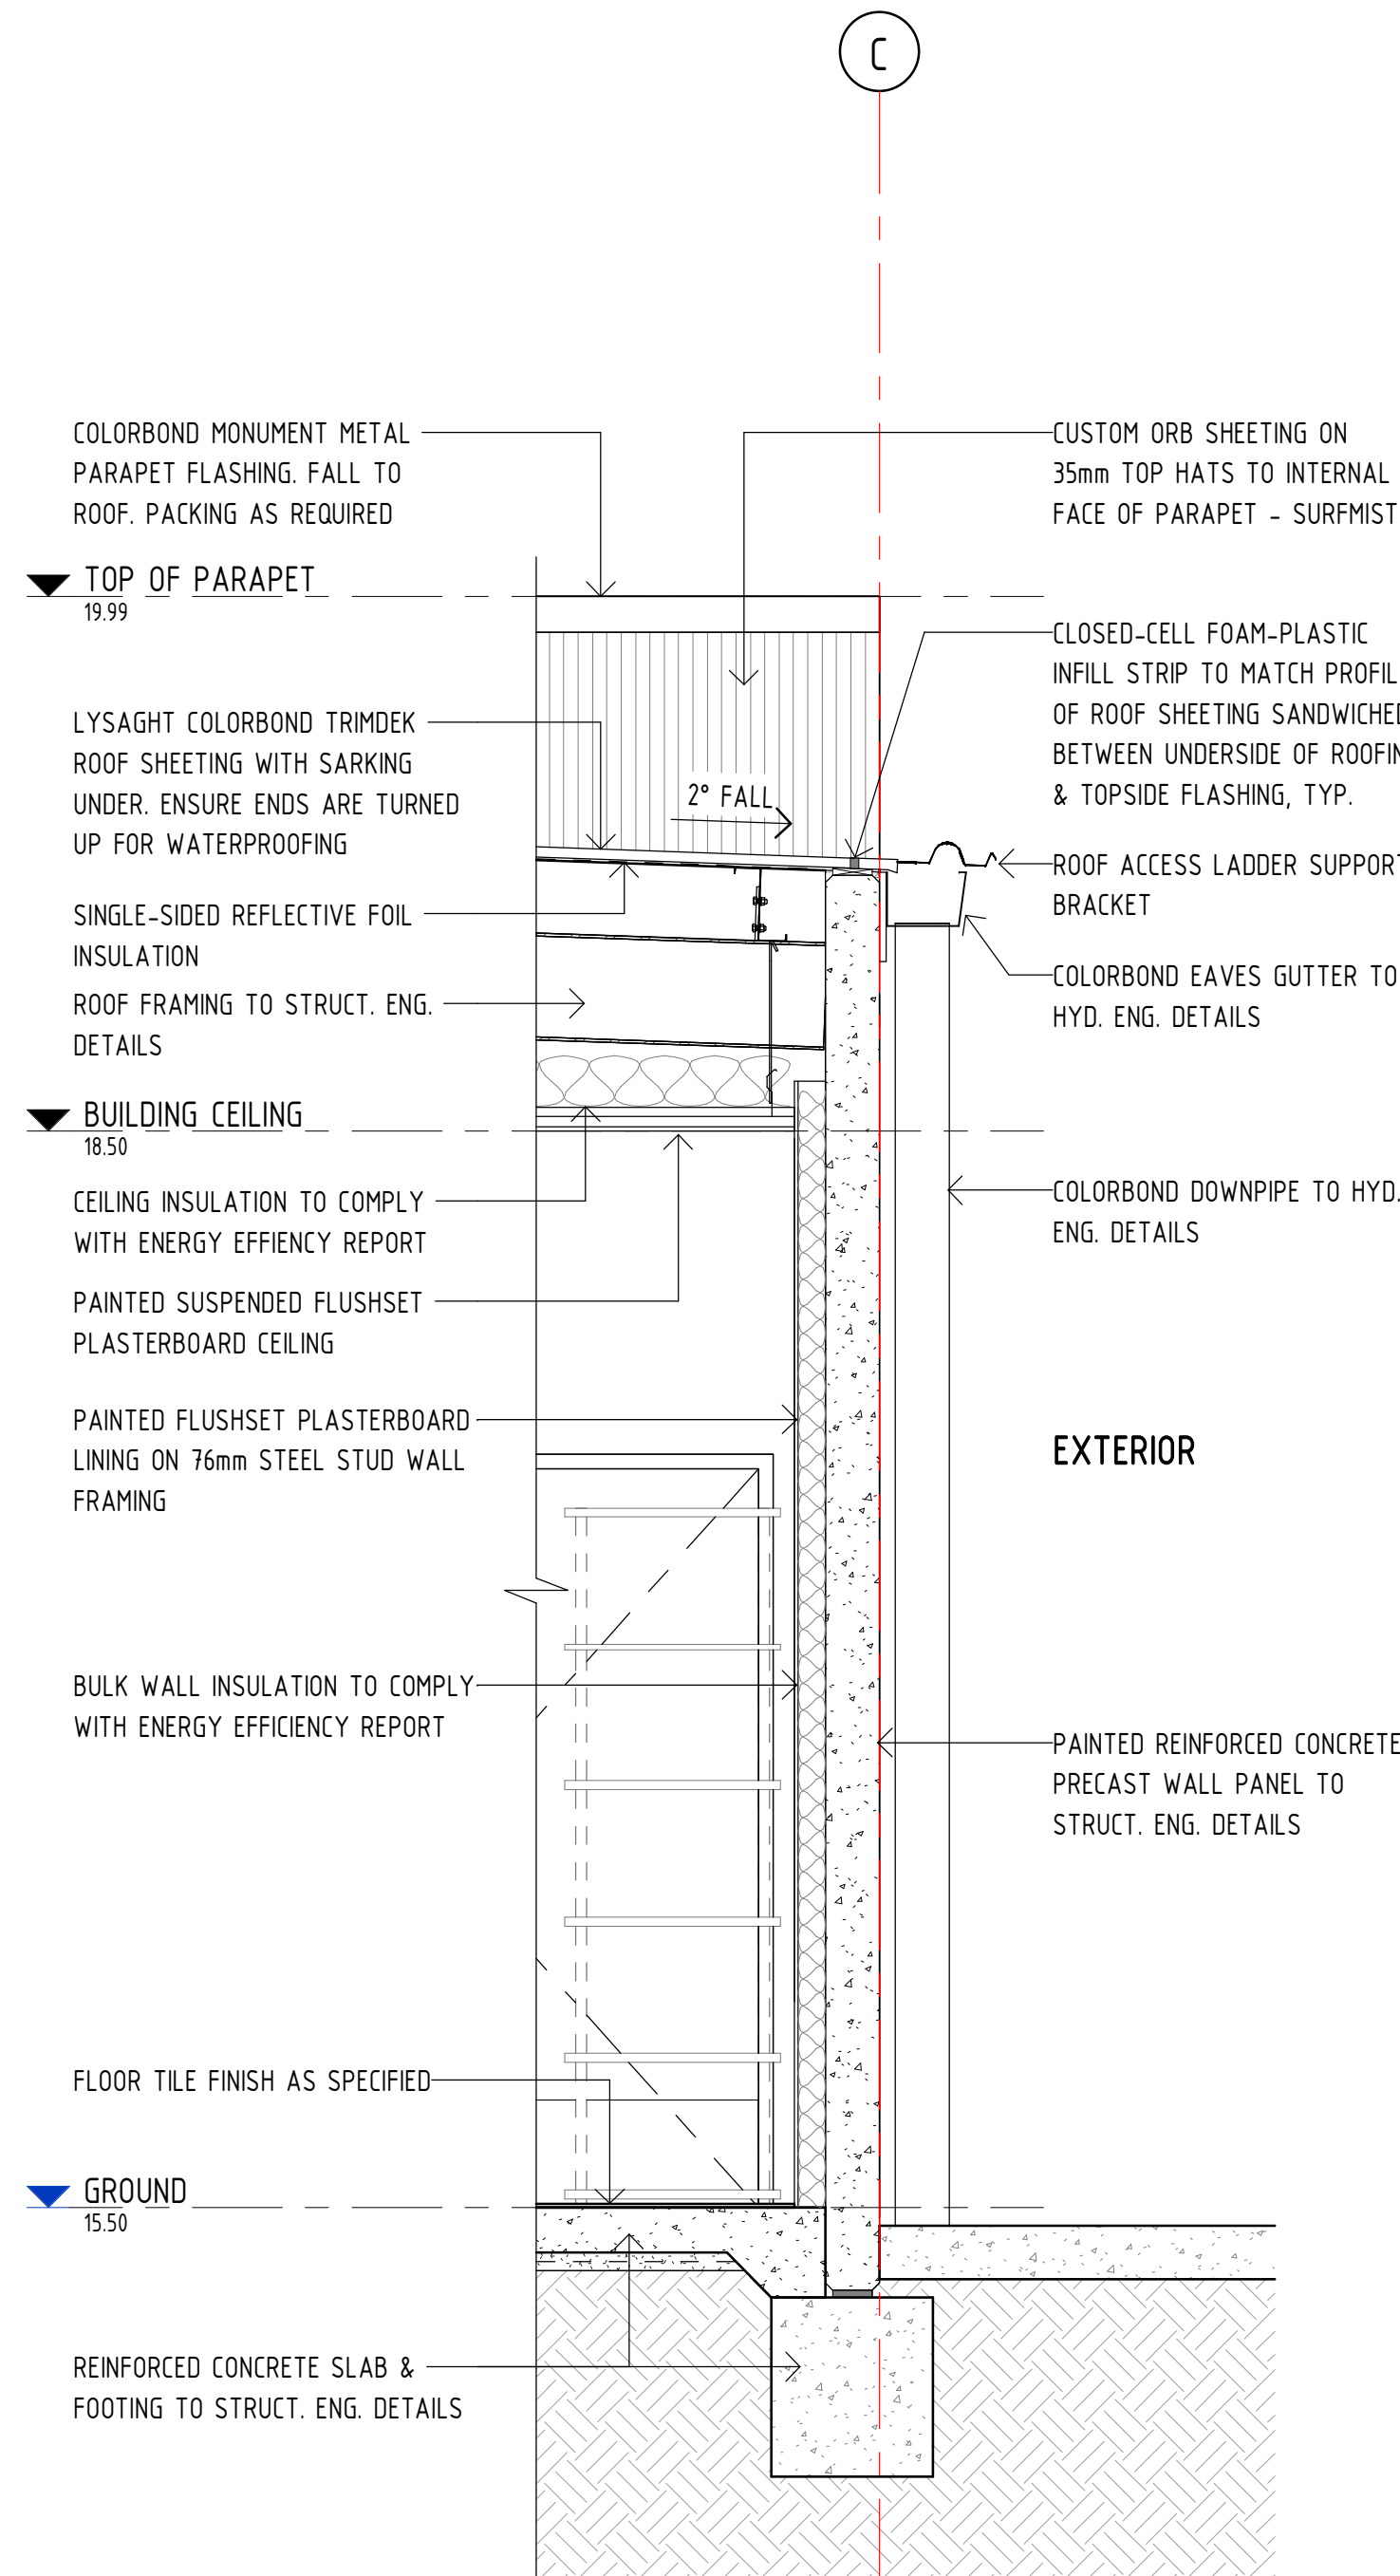

2 WALL SECTION 2
A210 1:20

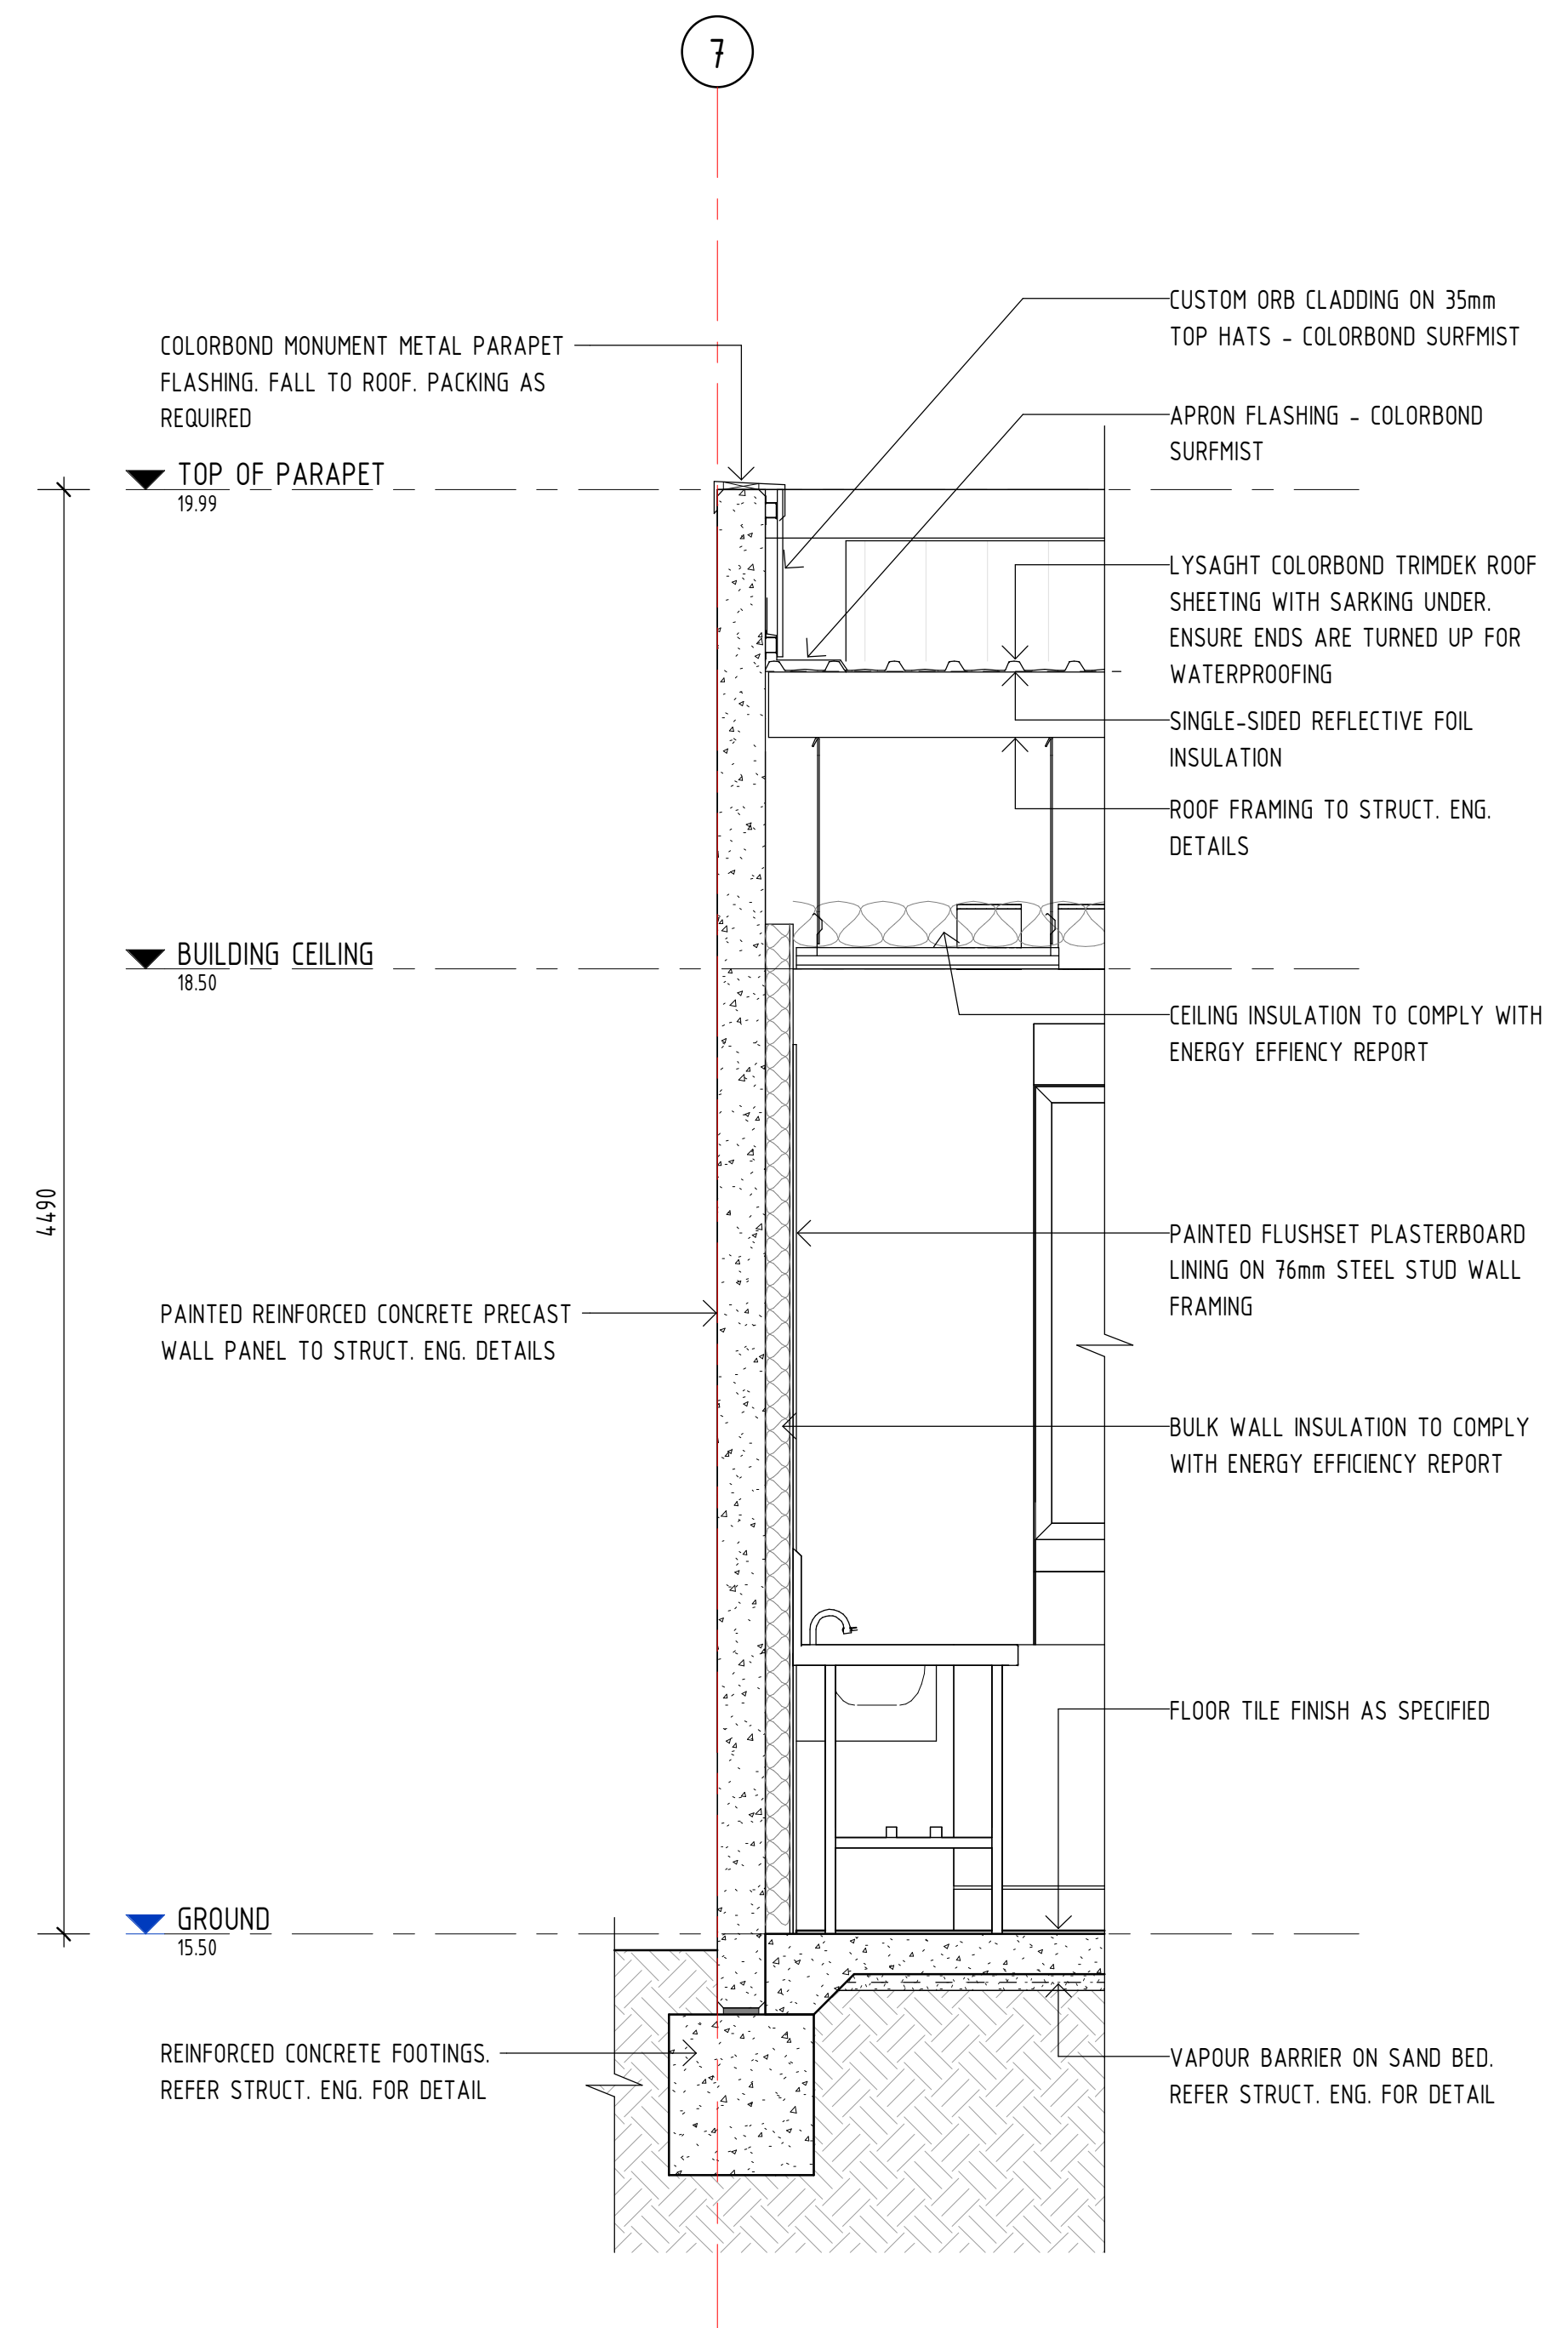

3 WALL SECTION 3
A210 1:20

VERVE SCHEDULES DISCLAIMER:

- ALL SCHEDULES SHOULD BE CHECKED WITH THE REMAINDER OF THE DRAWING SET.
- SCHEDULED RATES AND AREAS ARE INTENDED FOR ASSISTANCE ONLY. NO RESPONSIBILITY IS TAKEN FOR THE ACCURACY OF QUANTITIES.
- ANY DISCREPANCIES IN SCHEDULES SHOULD BE IDENTIFIED TO THE AUTHOR NOTED.
- ALL AREAS ARE GROSS AREAS, UNLESS NOTED OTHERWISE

CONSULTING ENGINEER



☐ commercial ☐ service stations
☐ mixed-use ☐ quick service restaurants
☐ self storage ☐ child care centres
☐ industrial ☐ large format retail


© 2011 copyright, all rights reserved.
This drawing is the © copyright & property of VERVE DESIGN GROUP and must not be used or duplicated without authorisation.
Do not scale this drawing.
Check all dimensions on site prior commencement of works

Revision and approvals					Description	Appr
Rev	Date	Drn	PC	BA ISSUE		
A	19.06.2026	PC				SS

Project Description		Drawing Title	
PROPOSED SERVICE STATION		WALL SECTIONS	
22 ENTERPRISE CCT., MARYBOROUGH W.			
Scale @A1 1:20	Date JUNE 2026	Job Number - Drawing Number 26024 A300	Revision A
Drawn PC	Approved By SS		

THIS DRAWING IS NOT
FOR CONSTRUCTION

BSN-1	ACCESSIBLE HAND BASIN AS1428.1 COMPLIANT - SUPPLIED & INSTALLED BY LESSEE
BT	BUCKET TRAP - REFER HYD. ENG. DETAILS
CH	CLOTHES HOOK
FW	FLOOR WASTE - REFER HYD. ENG. DETAILS
MI	MIRROR
PWD-BM	AS 1428.1 COMPLIANT BASIN MIXER
SD	SOAP DISPENSER - SUPPLIED & INSTALLED BY LESSEE
SHM	SHOWER RAIL WITH MIXER
SHM-1	AS 1428.1 COMPLIANT SHOWER MIXER
SHS-1	FOLDING SHOWER SEAT - METLAM ML993
TRH	TOILET ROLL HOLDER
WC-1	AMBULANT TOILET SUITE AS1428.1 COMPLIANT

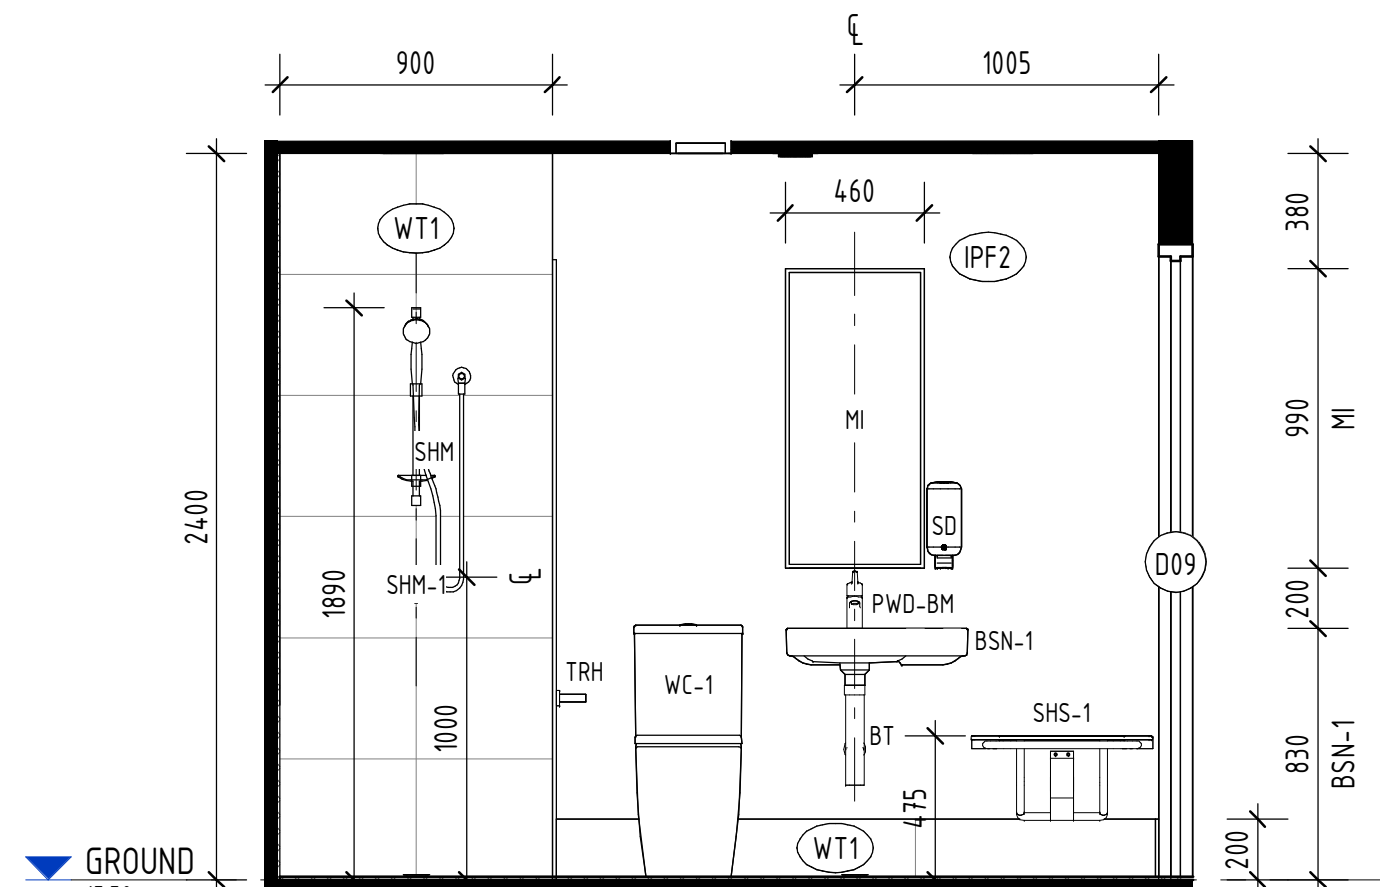

Technical drawing of a room layout showing dimensions and equipment locations:

- Dimensions:**
 - Total width: 900
 - Total height: 2400
 - Distance from top wall to bottom wall: 2050
 - Distance from left wall to right wall: 1350
 - Distance from bottom wall to floor level: 200
- Equipment Locations:**
 - D09 (Circular symbol) located near the top-left corner.
 - CH (Cylindrical symbol) located near the top-left corner.
 - IPFZ (Oval symbol) located in the upper central area.
 - WT1 (Oval symbol) located in the lower right area.
 - WT1 (Oval symbol) located in the lower right area.
- Legend:**
 - GROUND (Symbol)
 - ISO (Symbol)

[illegible]

5 WC & SHOWER - ELEVATION 4 (TYPICAL)
1 : 25

INTERNAL FINISHES SCHEDULE			
MARK	MANUFACTURER	DESCRIPTION	COMMENTS
EPX	ALLNEX	NUTHANE SB POLYURETHANE: MID GREY	MIN. R12 SLIP RATING. 100mm HIGH COVING TO WALL
FT1	AMBER TILES LIVERPOOL	FLOOR TILE - 600x600 "DURA GREY"	100mm ALUMINIUM SKIRTING - ARMOURSPRAY BLACK SATIN: 9109024S. R11 SLIP RATING. GROUT: GREY.
FT2	AMBER TILES LIVERPOOL	FLOOR TILE - 800x400 'STOCKTON WHITE'. PRODUCT CODE: AAC84ACD0DR.	R10 SLIP RATING. GROUT: GREY.
FT3	AMBER TILES LIVERPOOL	FLOOR TILE - 600x600 "DURA GREY"	MIN. R12 SLIP RATING. GROUT: GREY EPOXY. 100mm ALUMINIUM SKIRTING - ARMOURSPRAY BLACK SATIN: 9109024S
IPF2	TAUBMANS	INTERIOR PAINT FINISH - 'CRISP WHITE' LOW SHEEN.	APPLIED TO INTERNAL WALLS.
IPF3	TAUBMANS	SEMI-GLOSS PAINT FINISH: SEALORD T15 25.5	INTERNAL DOORS
L1	LAMINEX	COLOUR: GUNMETAL FINISH: NATURAL	TOILET PARTITION - PREFABRICATED 19mm MOISTURE RESISTANT LAMINATED BOARD EDGES SHALL BE TREATED WITH HEAVY DUTY PVC EDGE STRIPS
WT1	AMBER TILES LIVERPOOL	WALL TILE - 800x400 'STOCKTON WHITE'. PRODUCT CODE: AAC84ACD0DR.	GROUT: GREY.
WT2	COLORTILE	WALL TILE - 280x70 "DARK NIGHT SUNSET MATT" - WHITE GROUT.	GROUT: ARDEX EG15 WHITE. 5mm JOINTS

MARK	DESCRIPTION	MANUFACTURER	MODEL	SUPPLIER	INSTALLER
BSN-1	HAND BASIN	CAROMA	CAROMA URBANE II RIGHT HAND SHELF WALL BASIN, 1 TAP HOLE (878710W)	BUILDER	BUILDER
CH	COAT HOOK	REECE PLUMBING	SONIA TECNO SINGLE HOOK LARGE-CHROME, CODE:283557	BUILDER	BUILDER
CTM	CLEANERS TAP MIXER	CAROMA	ELEGANCE II LAUNDRY SET. PRODUCT CODE: V631799CA	BUILDER	BUILDER
MI	MIRROR	JD MACDONALD	MIRROR WITH STAINLESS STEEL INTER-LOK ANGLE FRAME. PRODUCT CODE: 10-0600-V1839	BUILDER	BUILDER
PWD-BM	PWD SINK MIXER	CAROMA	SKANDIC CARE BASIN MIXER (HOT & COLD), PRODUCT CODE: 90995C5A.	BUILDER	BUILDER
SD	SOAP DISPENSER	TORK	LIQUID AND SPRAY SOAP DISPENSER - WHITE, PRODUCT CODE: 560000	BUILDER	BUILDER
SHM	SHOWER RAIL WITH MIXER	CAROMA	TASMAN II RAIL SHOWER 992545C3A	BUILDER	BUILDER
SHM-1	SHOWER MIXER	CAROMA	AQUA SHOWER MIXER. COLOUR: CHROME. CODE: 90988C	BUILDER	BUILDER
SHS-1	FOLDING SHOWER SEAT	METLAM	ACCESSIBLE FOLDING SHOWER SEAT - COMPACT LAMINATE ML994_CL (OR EQUAL APPROVED)	BUILDER	BUILDER
TRH	TOILET ROLL HOLDER	METLAM	SINGLE SURFACE MOUNTED 10-7305	BUILDER	BUILDER
WC-1	AMBULANT TOILET SUITE	CAROMA	URBANE II CF WFCC BE 4S SUITE + OLIDA SC SEAT CODE: 746350W	BUILDER	BUILDER

1. ALL SCHEDULES SHOULD BE CHECKED WITH THE REMAINDER OF THE DRAWING SET.
2. SCHEDULED RATES AND AREAS ARE INTENDED FOR ASSISTANCE ONLY. NO RESPONSIBILITY IS TAKEN FOR THE ACCURACY OF QUANTITIES.
3. ANY DISCREPANCIES IN SCHEDULES SHOULD BE IDENTIFIED TO THE AUTHOR NOTED.
4. ALL AREAS ARE GROSS AREAS, UNLESS NOTED OTHERWISE

 **VERVE**
DESIGN GROUP

QBCC LICENCE No. 1236672 PH. (07) 3857 0942
OFFICE 1, LEVEL 1, 488 LUTWICHE RD, LUTWICHE 4030 info@vervedesigngroup.com.au

imagine ☐ **create** ☐ **deliver**

- ☐ commercial
- ☐ mixed-use
- ☐ self storage
- ☐ industrial
- ☐ service stations
- ☐ quick service restaurants
- ☐ child care centres
- ☐ large format retail

© 2011 copyright, all rights reserved


This drawing is the © copyright & property of VERVE DESIGN GROUP and must not be used or duplicated without authorisation.

Do not scale this drawing.


Check all dimensions on site prior commencement of works

Project Description	
PROPOSED SERVICE STATION	
22 ENTERPRISE CCT., MARYBOROUGH W.	
Scale @A1 1 : 25	Date APRIL 2026
Drawn PC	Approved By SS


Job Number - Drawing Number	Revision
26024 A500	A

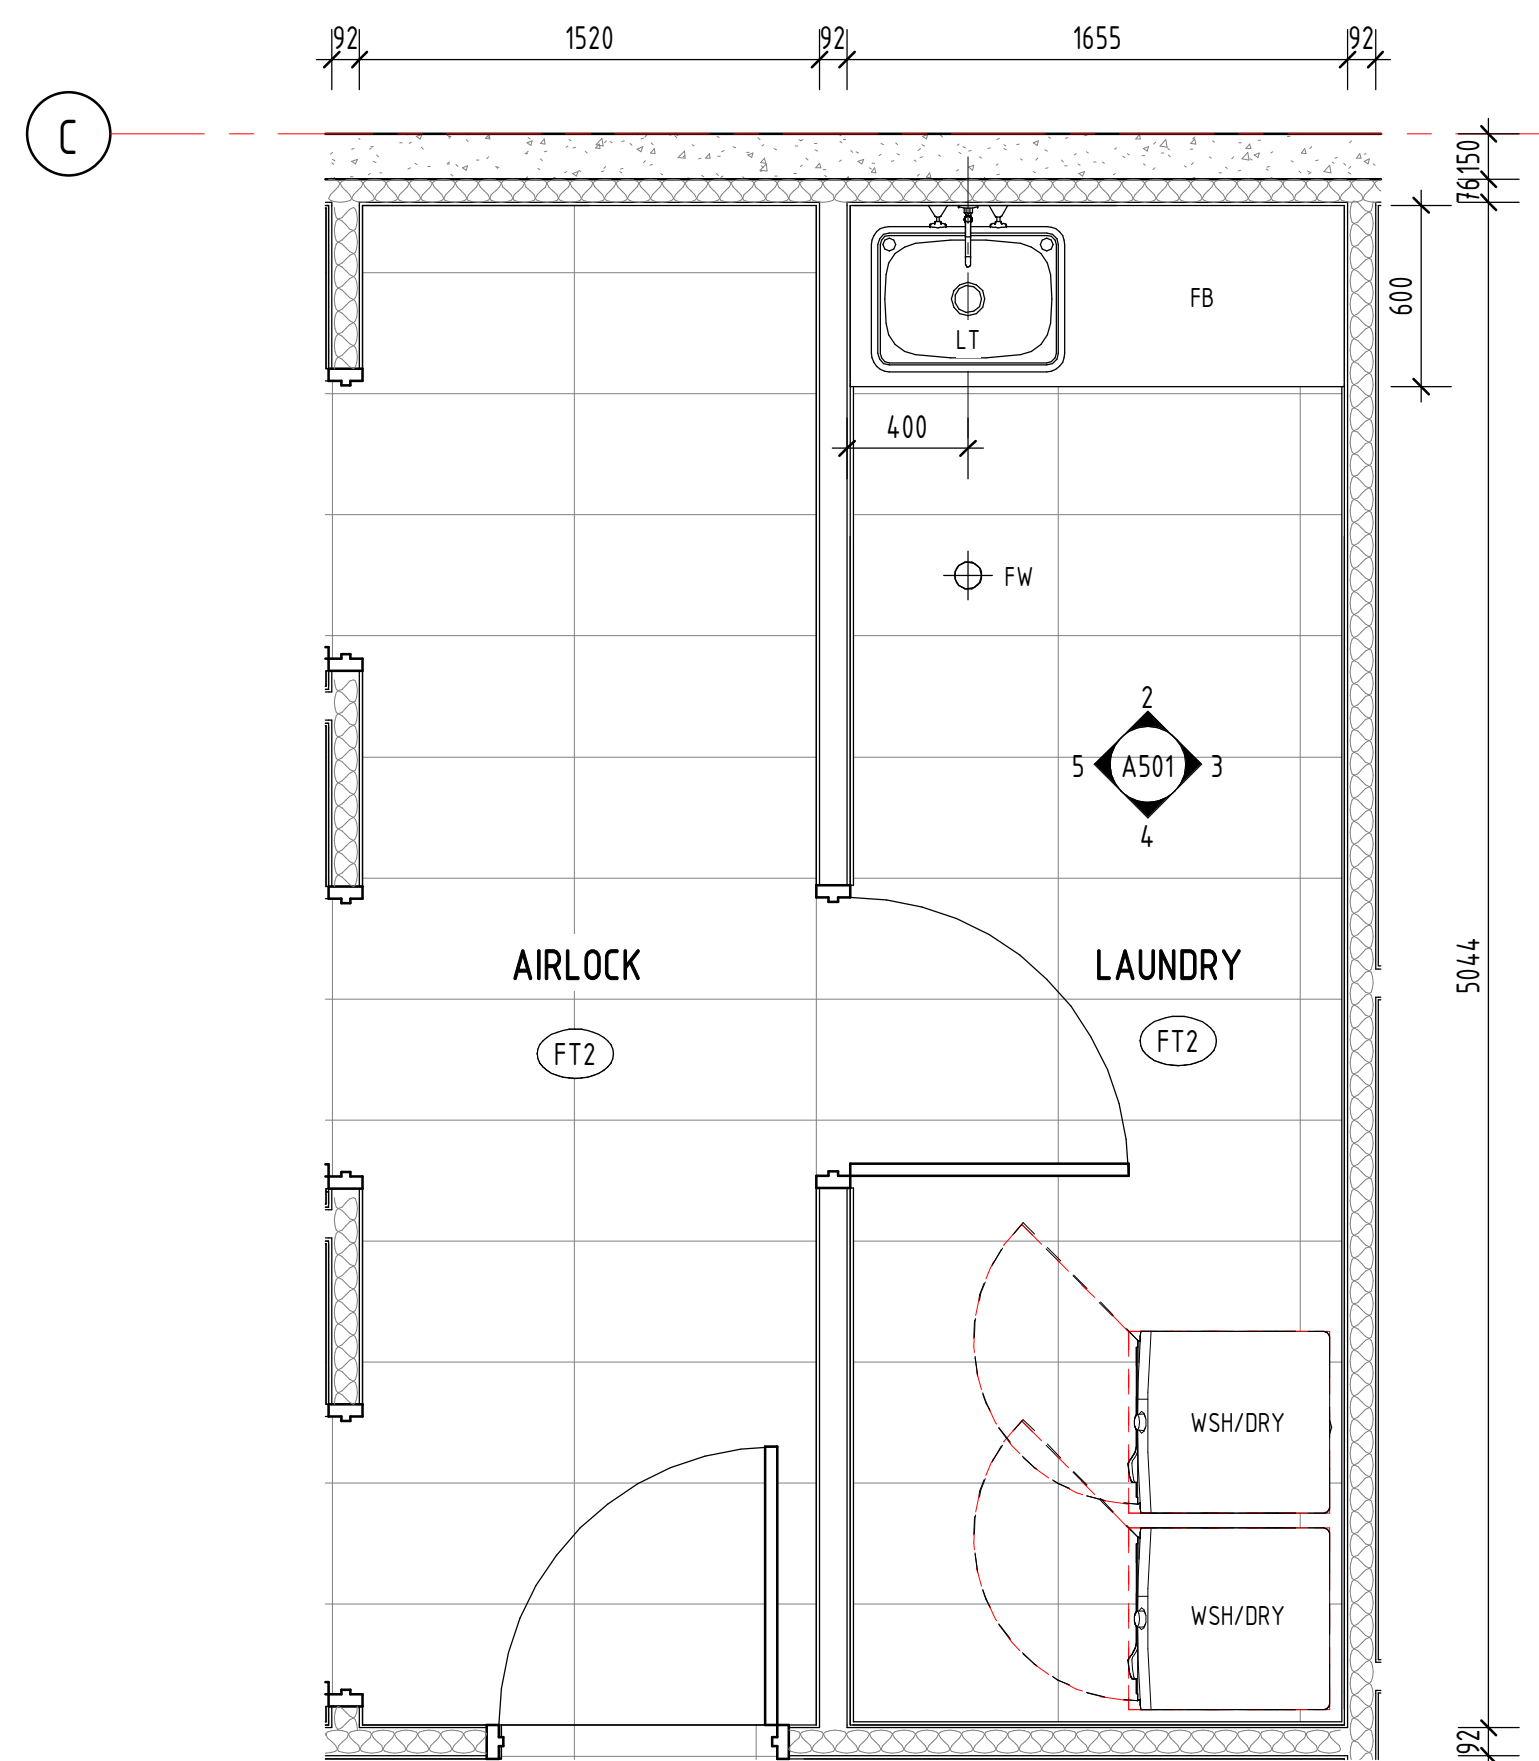


1 PROP. LAUNDRY PLAN
1 : 25

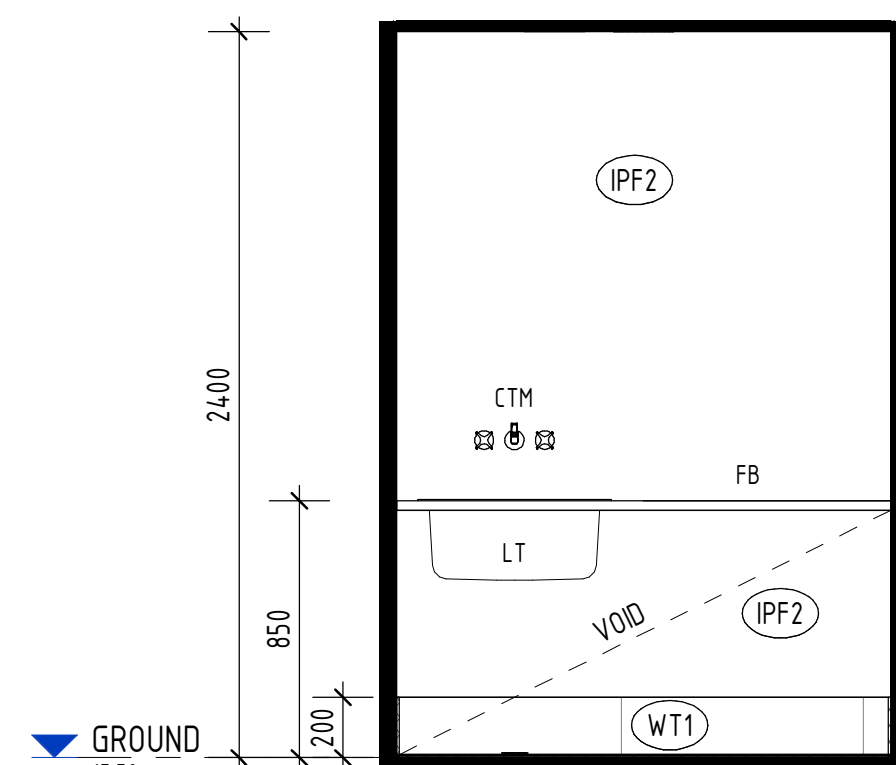


2 LAUNDRY - ELEVATION 1
1 : 25

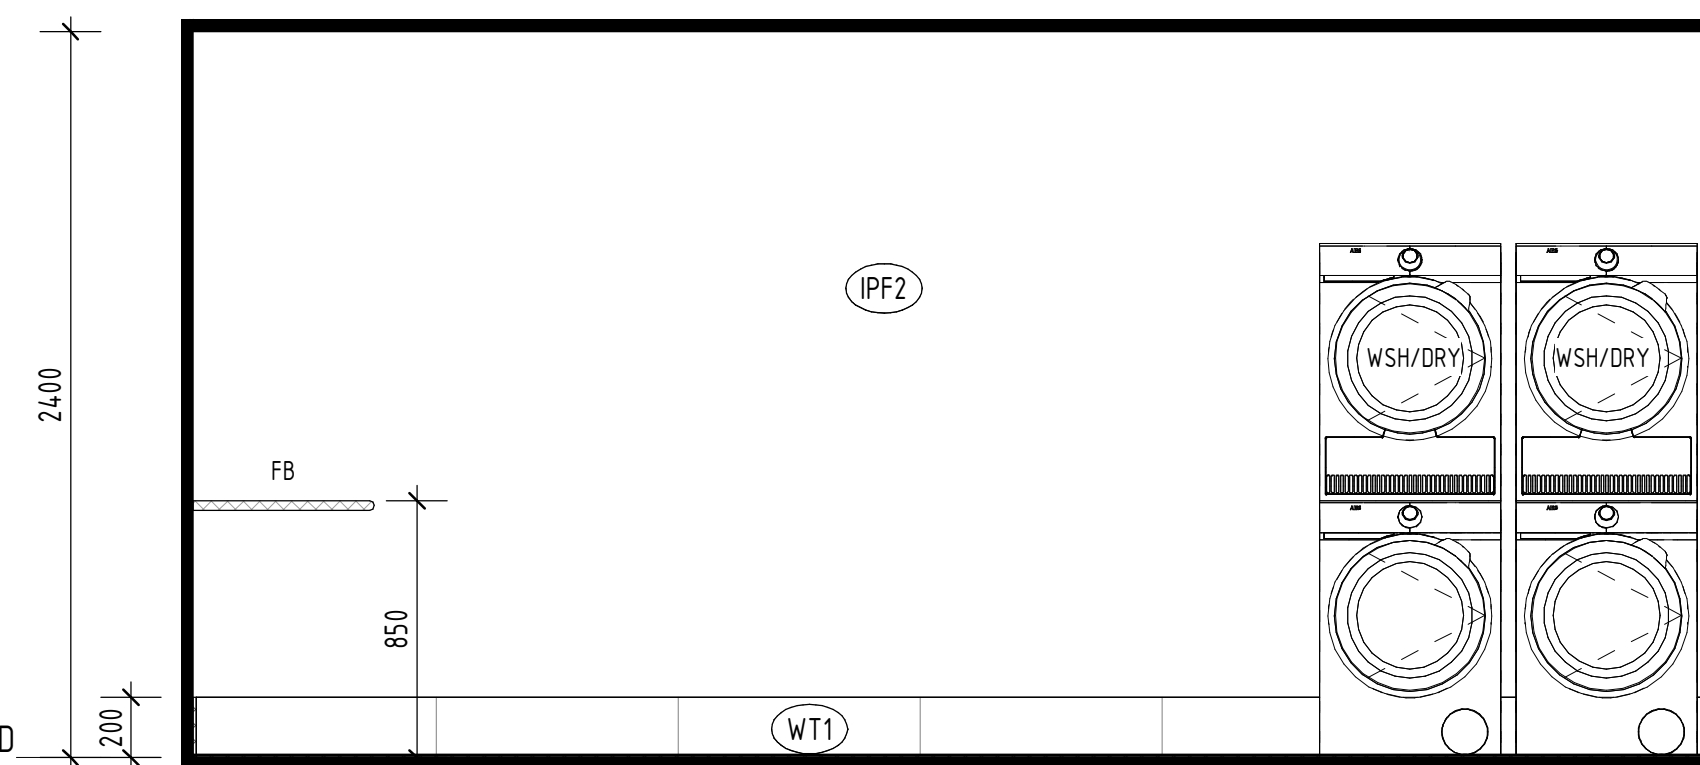

3 LAUNDRY - ELEVATION 2
1 : 25

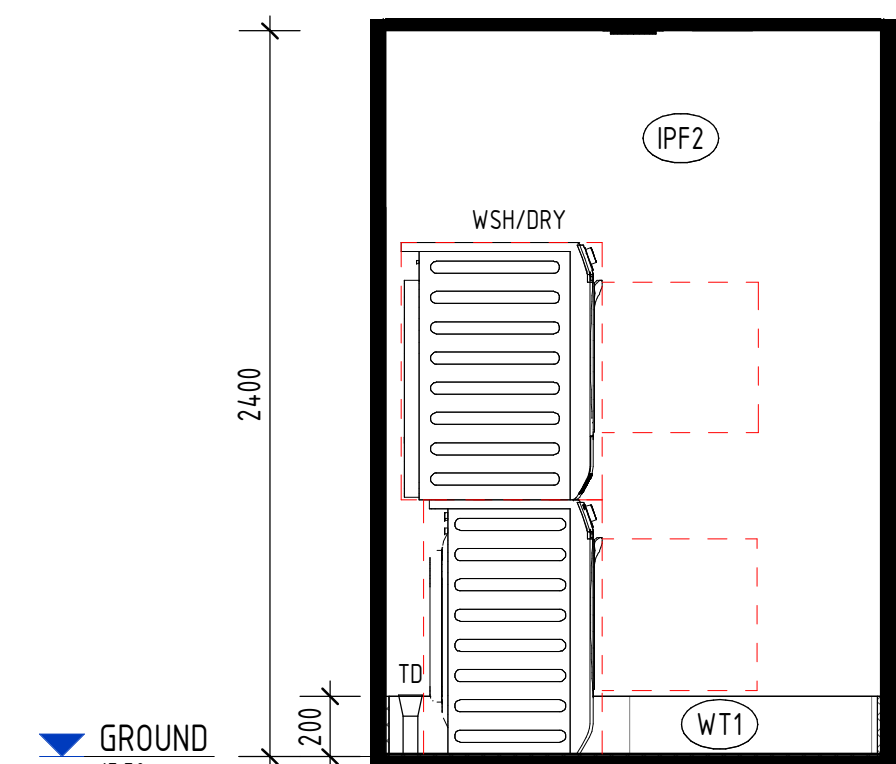

4 LAUNDRY - ELEVATION 3
1 : 25

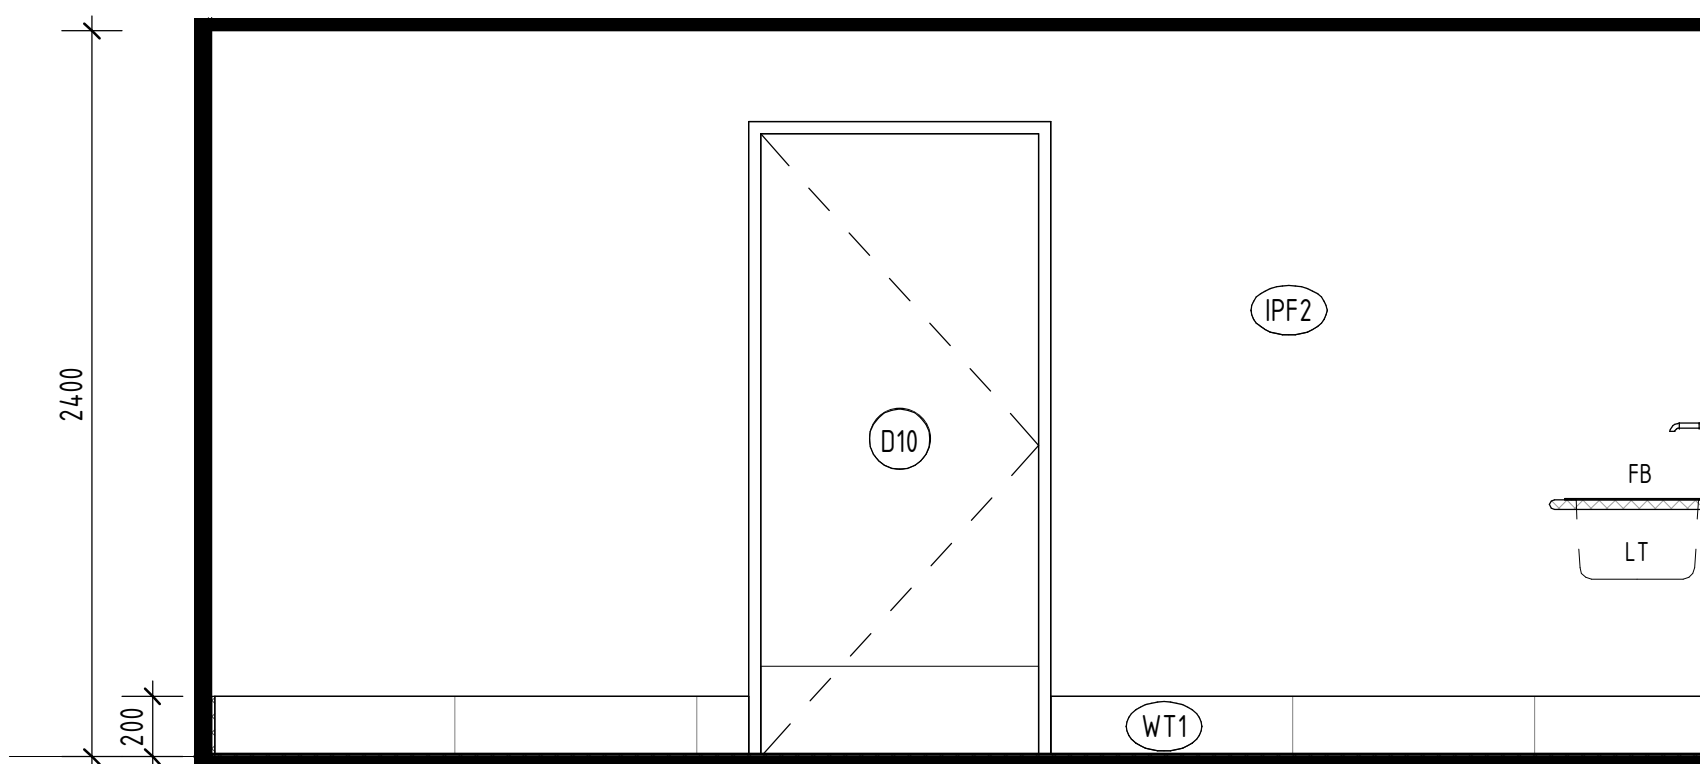

5 LAUNDRY - ELEVATION 4
1 : 25

LEGEND	
CTM	CLEANERS TAP MIXER
FB	FOLDING BENCH - SUPPLIED & INSTALLED BY LESSEE
FW	FLOOR WASTE - REFER HYD. ENG. DETAILS
LT	LAUNDRY TUB - SUPPLIED & INSTALLED BY LESSEE
TD	TUNDISH - REFER HYD. ENG. DETAILS
WSH/DRY	STACKED WASHER/DRYER - SUPPLIED & INSTALLED BY LESSEE

NOTE: ALL ITEMS TO BE INSTALLED IN ACCORDANCE WITH AS1428.1

INTERNAL FINISHES SCHEDULE			
MARK	MANUFACTURER	DESCRIPTION	COMMENTS
EPX	ALLNEX	NUTHANE SB POLYURETHANE: MID GREY	MIN. R12 SLIP RATING. 100mm HIGH COVING TO WALL
FT1	AMBER TILES LIVERPOOL	FLOOR TILE - 600x600 "DURA GREY"	100mm ALUMINIUM SKIRTING -ARMOURSPRAY BLACK SATIN: 9109024S. R11 SLIP RATING. GROUT: GREY.
FT2	AMBER TILES LIVERPOOL	FLOOR TILE - 800x400 "STOCKTON WHITE". PRODUCT CODE: AAC84ACD0DR.	R10 SLIP RATING. GROUT: GREY.
FT3	AMBER TILES LIVERPOOL	FLOOR TILE - 600x600 "DURA GREY"	MIN. R12 SLIP RATING. GROUT: GREY EPOXY. 100mm ALUMINIUM SKIRTING -ARMOURSPRAY BLACK SATIN: 9109024S
IPF2	TAUBMANS	INTERIOR PAINT FINISH - 'CRISP WHITE' LOW SHEEN.	APPLIED TO INTERNAL WALLS.
IPF3	TAUBMANS	SEMI-GLOSS PAINT FINISH: SEALORD T15 25.5	INTERNAL DOORS
L1	LAMINEX	COLOUR: GUNMETAL	TOILET PARTITION - PREFABRICATED 19mm MOISTURE RESISTANT LAMINATED BOARD EDGES SHALL BE TREATED WITH HEAVY DUTY PVC EDGE STRIPS
WT1	AMBER TILES LIVERPOOL	WALL TILE - 800x400 "STOCKTON WHITE". PRODUCT CODE: AAC84ACD0DR.	GROUT: GREY.
WT2	COLORITILE	WALL TILE - 280x70 "DARK NIGHT SUNSET MATT" - WHITE GROUT.	GROUT: ARDEX EG15 WHITE. 5mm JOINTS

EQUIPMENT & FIXTURE SCHEDULE - PWD					
MARK	DESCRIPTION	MANUFACTURER	MODEL	SUPPLIER	INSTALLER
BSN-1	HAND BASIN	CAROMA	CAROMA URBANE II RIGHT HAND SHELF WALL BASIN, 1 TAP HOLE (878710W)	BUILDER	BUILDER
CH	COAT HOOK	REECE PLUMBING	SONIA TECNO SINGLE HOOK LARGE-CHROME, CODE:283557	BUILDER	BUILDER
CTM	CLEANERS TAP MIXER	CAROMA	ELEGANCE II LAUNDRY SET. PRODUCT CODE: V631179C4A	BUILDER	BUILDER
MI	MIRROR	JD MACDONALD	MIRROR WITH STAINLESS STEEL INTER-LOK ANGLE FRAME. PRODUCT CODE: 10-0600-V1839	BUILDER	BUILDER
PWD-BM	PWD SINK MIXER	CAROMA	SKANDIC CARE BASIN MIXER (HOT & COLD), PRODUCT CODE: 90995CSA.	BUILDER	BUILDER
SD	SOAP DISPENSER	TORK	LIQUID AND SPRAY SOAP DISPENSER - WHITE, PRODUCT CODE: 560000	BUILDER	BUILDER
SHM	SHOWER RAIL WITH MIXER	CAROMA	TASMAN II RAIL SHOWER 992545C3A	BUILDER	BUILDER
SHM-1	SHOWER MIXER	CAROMA	ACQUA SHOWER MIXER. COLOUR: CHROME. CODE: 90988C	BUILDER	BUILDER
SHS-1	FOLDING SHOWER SEAT	METLAM	ACCESSIBLE FOLDING SHOWER SEAT - COMPACT LAMINATE ML994_CL (OR EQUAL APPROVED)	BUILDER	BUILDER
TRH	TOILET ROLL HOLDER	METLAM	SINGLE SURFACE MOUNTED 10-7305	BUILDER	BUILDER
WC-1	AMBULANT TOILET SUITE	CAROMA	URBANE II CF WFCC BE 4S SUITE + OLIDA SC SEAT CODE: 746350W	BUILDER	BUILDER

VERVE SCHEDULES DISCLAIMER:

1. ALL SCHEDULES SHOULD BE CHECKED WITH THE REMAINDER OF THE DRAWING SET.

2. SCHEDULED RATES AND AREAS ARE INTENDED FOR ASSISTANCE ONLY. NO RESPONSIBILITY IS TAKEN FOR THE ACCURACY OF QUANTITIES.

3. ANY DISCREPANCIES IN SCHEDULES SHOULD BE IDENTIFIED TO THE AUTHOR NOTED.

4. ALL AREAS ARE GROSS AREAS, UNLESS NOTED OTHERWISE

CONSULTING ENGINEER



- ☐ commercial ☐ service stations ☐ mixed-use ☐ quick service restaurants ☐ self storage ☐ child care centres ☐ industrial ☐ large format retail

© 2011 copyright, all rights reserved.

This drawing is the © copyright & property of VERVE DESIGN GROUP and must not be used or duplicated without authorisation.


Do not scale this drawing.

Check all dimensions on site prior commencement of works

Revision and approvals			
Rev	Date	Drn	Description
P1	01.05.2026	PC	REVISED PRELIMINARY ISSUE
A	19.06.2026	PC	BA ISSUE




Project Description	
PROPOSED SERVICE STATION	
22 ENTERPRISE CCT., MARYBOROUGH W.	
Scale @A1 1 : 25	Date APRIL 2026
Drawn PC	Approved By SS

Drawing Title	
INTERNAL ELEVATIONS - AMENITIES	
Job Number - Drawing Number 26024	Revision A


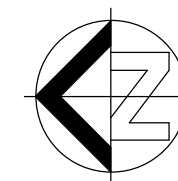


BA ISSUE

THIS DRAWING IS NOT
FOR CONSTRUCTION

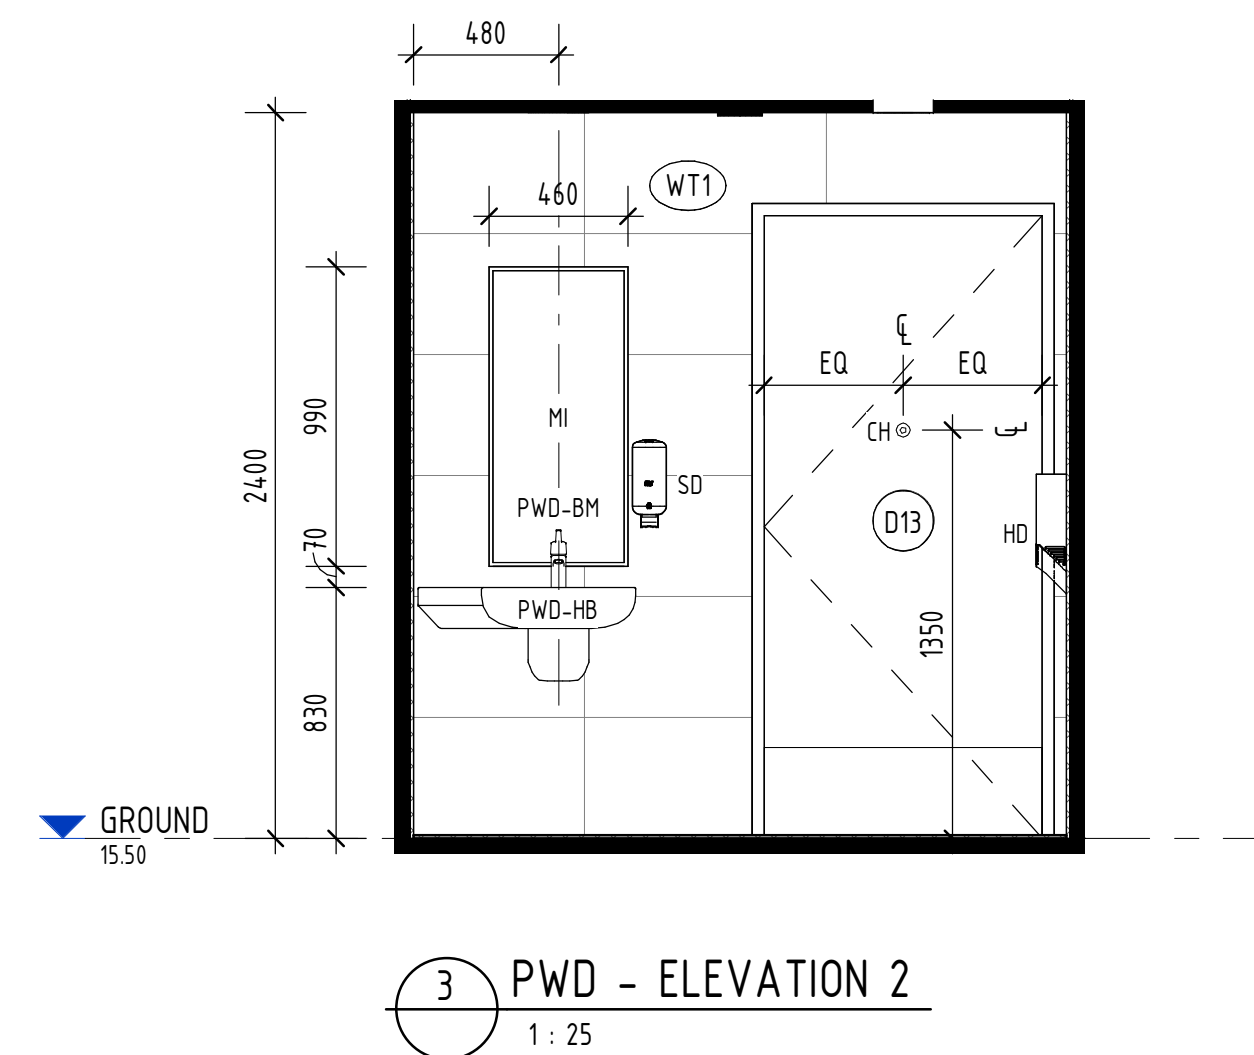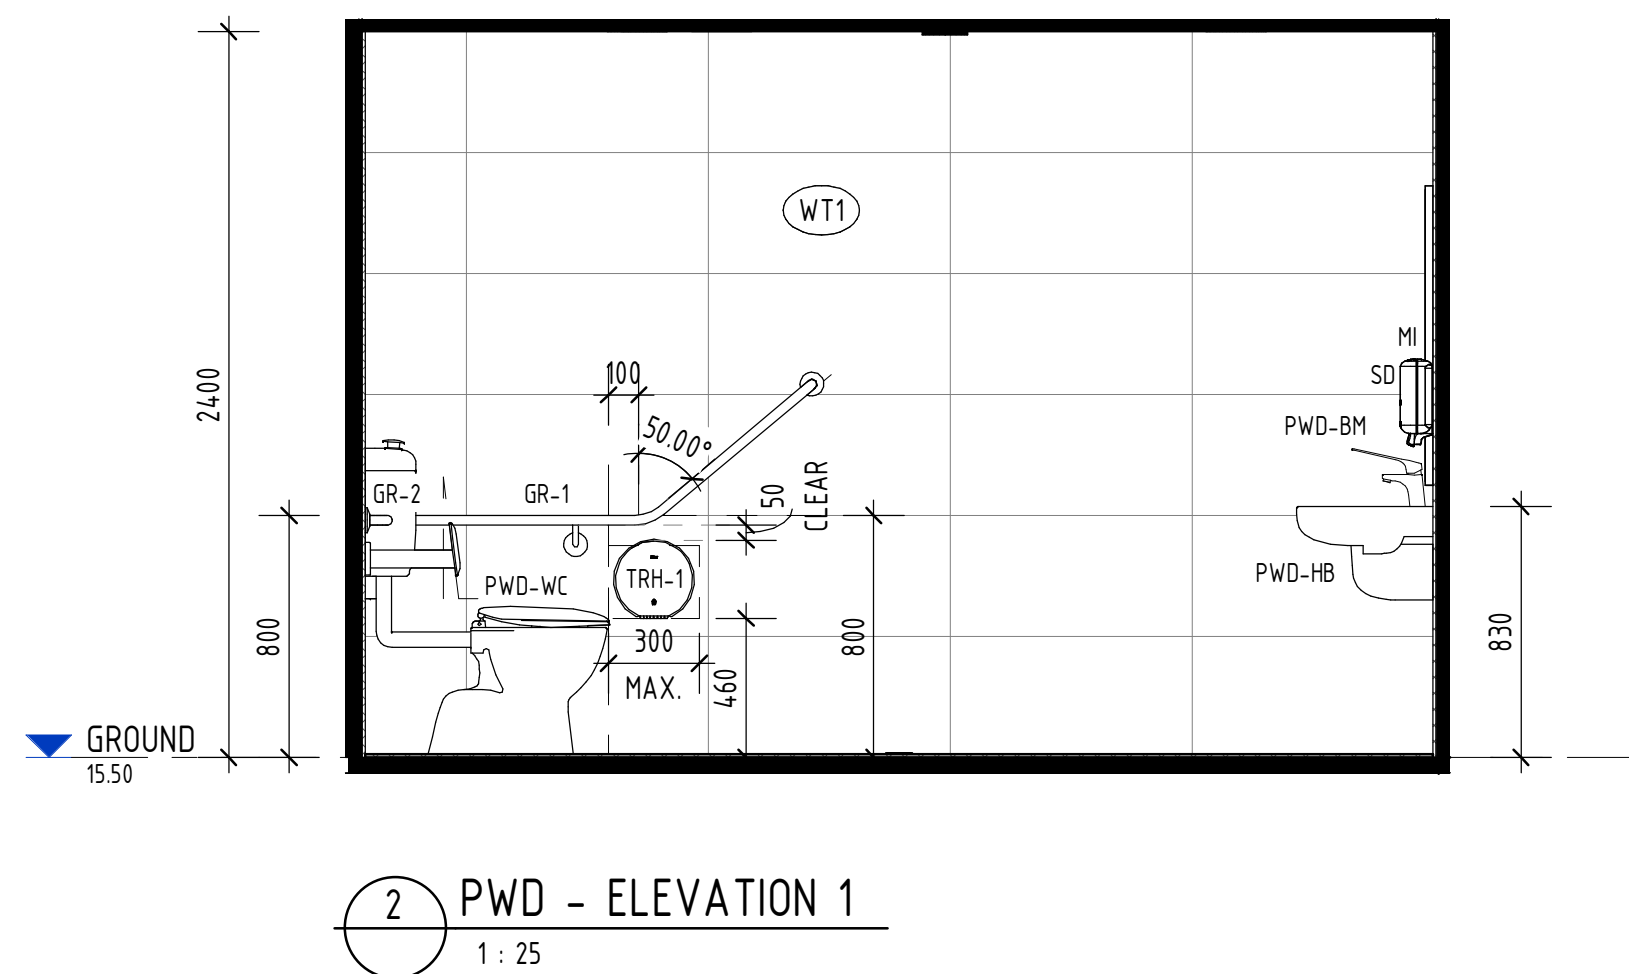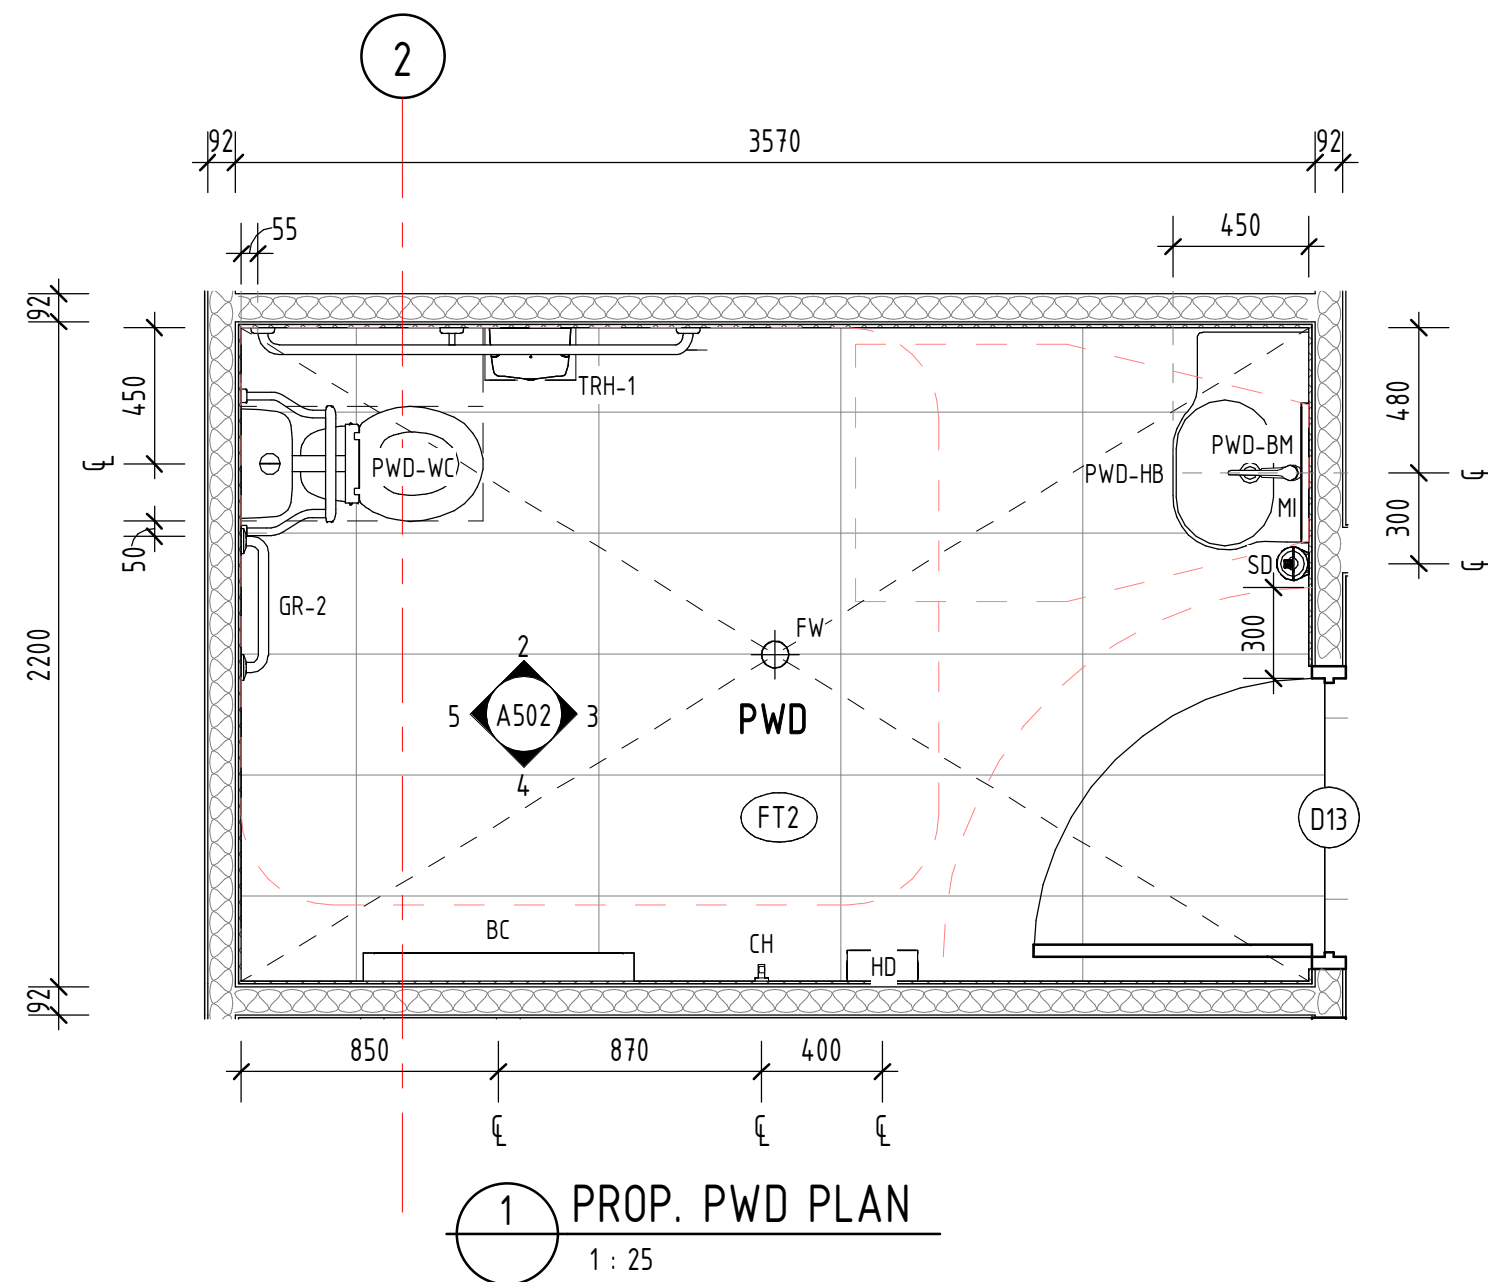

LEGEND	
BC	BABY CHANGE TABLE
CH	CLOTHES HOOK
FW	FLOOR WASTE - REFER HYD. ENG. DETAILS
GR-1	GRAB RAIL - AMBULANT - AS1428.1 COMPLIANT
GR-2	GRAB RAIL STRAIGHT AS1428.1 COMPLIANT
HD	HAND DRYER
MI	MIRROR
PWD-BM	AS 1428.1 COMPLIANT BASIN MIXER
PWD-HB	AS 1428.1 COMPLIANT HAND BASIN
PWD-WC	AS 1428.1 COMPLIANT WC
SD	SOAP DISPENSER - SUPPLIED & INSTALLED BY LESSEE
TRH-1	TOILET ROLL HOLDER AS1428.1 COMPLIANT

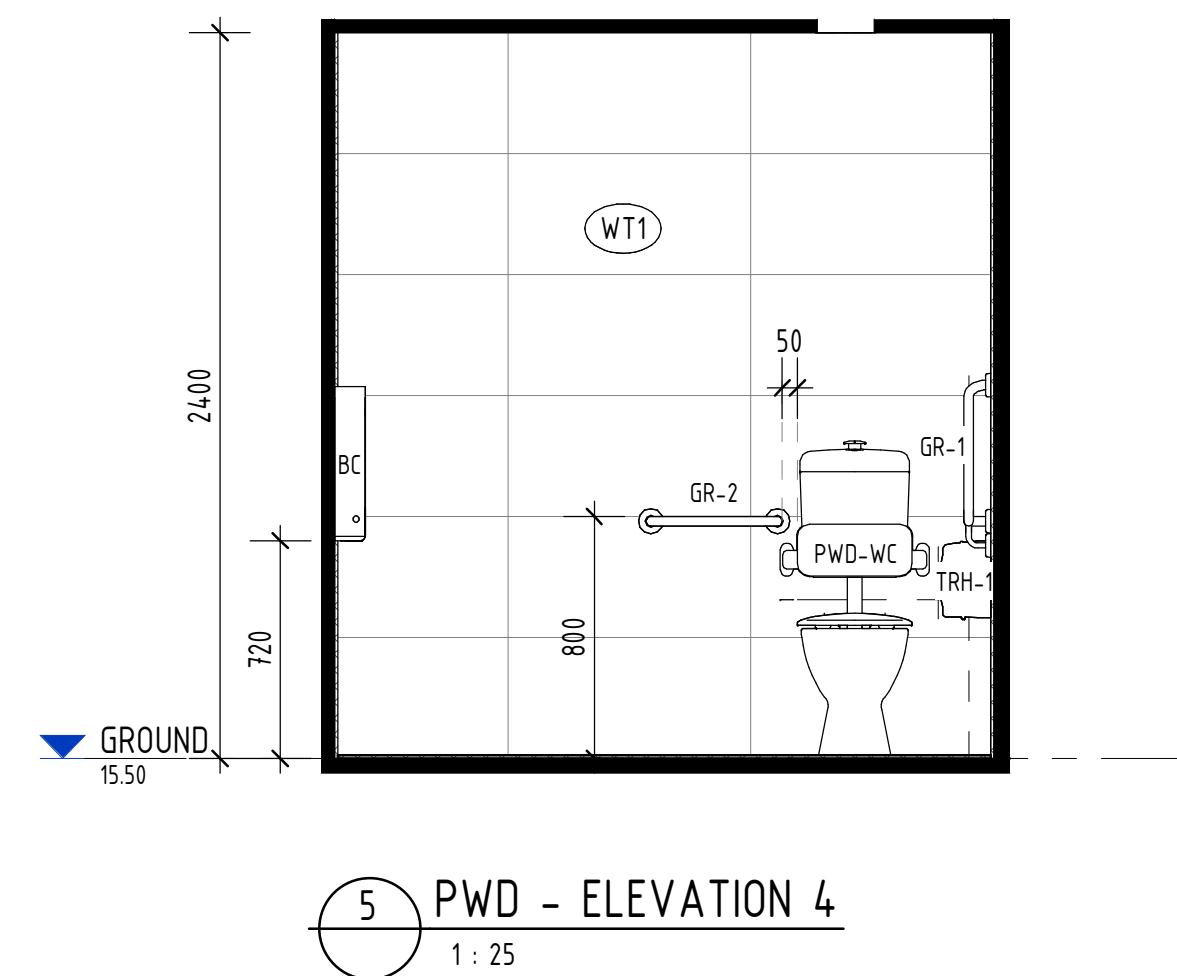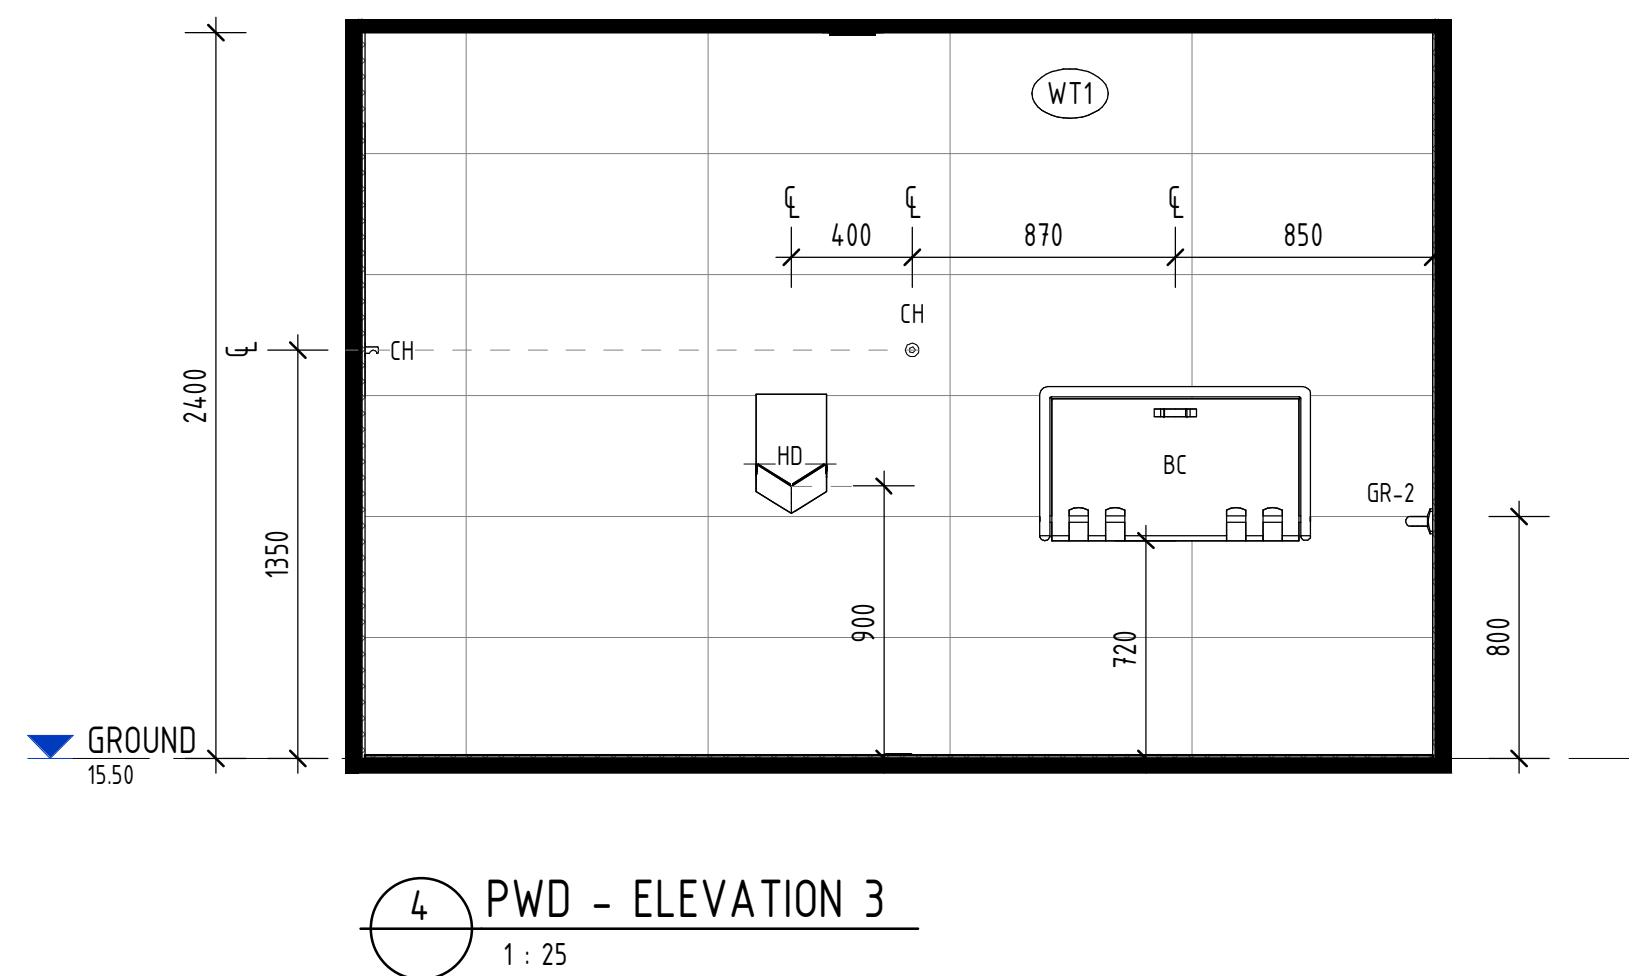

NOTE: ALL ITEMS TO BE INSTALLED IN ACCORDANCE
WITH AS1428.1

INTERNAL FINISHES SCHEDULE			
MARK	MANUFACTURER	DESCRIPTION	COMMENTS
EPX	ALLNEX	NUTHANE SB POLYURETHANE: MID GREY	MIN. R12 SLIP RATING. 100mm HIGH COVING TO WALL
FT1	AMBER TILES LIVERPOOL	FLOOR TILE - 600x600 "DURA GREY"	100mm ALUMINIUM SKIRTING -ARMOURSpray BLACK SATIN: 9109024S. R11 SLIP RATING. GROUT: GREY.
FT2	AMBER TILES LIVERPOOL	FLOOR TILE - 800x400 'STOCKTON WHITE'. PRODUCT CODE: AAC84ACD0DR.	R10 SLIP RATING. GROUT: GREY.
FT3	AMBER TILES LIVERPOOL	FLOOR TILE - 600x600 "DURA GREY"	MIN. R12 SLIP RATING. GROUT: GREY EPOXY. 100mm ALUMINIUM SKIRTING -ARMOURSpray BLACK SATIN: 9109024S
IPF2	TAUBMANS	INTERIOR PAINT FINISH - 'CRISP WHITE' LOW SHEEN.	APPLIED TO INTERNAL WALLS.
IPF3	TAUBMANS	SEMI-GLOSS PAINT FINISH: SEALORD T15 25.5	INTERNAL DOORS
L1	LAMINEX	COLOR: GUNMETAL	TOILET PARTITION - PREFABRICATED 19mm MOISTURE RESISTANT LAMINATED BOARD EDGES SHALL BE TREATED WITH HEAVY DUTY PVC EDGE STRIPS
WT1	AMBER TILES LIVERPOOL	WALL TILE - 800x400 'STOCKTON WHITE'. PRODUCT CODE: AAC84ACD0DR.	GROUT: GREY.
WT2	COLOR TILE	WALL TILE - 280x70 "DARK NIGHT SUNSET MATT" - WHITE GROUT.	GROUT: ARDEX EG15 WHITE. 5mm JOINTS

EQUIPMENT & FIXTURE SCHEDULE - PWD					
MARK	DESCRIPTION	MANUFACTURER	MODEL	SUPPLIER	INSTALLER
BSN-1	HAND BASIN	CAROMA	CAROMA URBANE II RIGHT HAND SHELF WALL BASIN, 1 TAP HOLE (878710W)	BUILDER	BUILDER
CH	COAT HOOK	REECE PLUMBING	SONIA TECNO SINGLE HOOK LARGE-CHROME, CODE:283557	BUILDER	BUILDER
CTM	CLEANERS TAP MIXER	CAROMA	ELEGANCE II LAUNDRY SET. PRODUCT CODE: V631179C4A	BUILDER	BUILDER
MI	MIRROR	JD MACDONALD	MIRROR WITH STAINLESS STEEL INTER-LOK ANGLE FRAME. PRODUCT CODE: 10-0600-V1839	BUILDER	BUILDER
PWD-BM	PWD SINK MIXER	CAROMA	SKANDIC CARE BASIN MIXER (HOT & COLD), PRODUCT CODE: 90995CSA.	BUILDER	BUILDER
SD	SOAP DISPENSER	TORK	LIQUID AND SPRAY SOAP DISPENSER - WHITE, PRODUCT CODE: 560000	BUILDER	BUILDER
SHM	SHOWER RAIL WITH MIXER	CAROMA	TASMAN II RAIL SHOWER 992545C3A	BUILDER	BUILDER
SHM-1	SHOWER MIXER	CAROMA	ACQUA SHOWER MIXER. COLOUR: CHROME. CODE: 90988C	BUILDER	BUILDER
SHS-1	FOLDING SHOWER SEAT	METLAM	ACCESSIBLE FOLDING SHOWER SEAT - COMPACT LAMINATE ML994_CL (OR EQUAL APPROVED)	BUILDER	BUILDER
TRH	TOILET ROLL HOLDER	METLAM	SINGLE SURFACE MOUNTED 10-7305	BUILDER	BUILDER
WC-1	AMBULANT TOILET SUITE	CAROMA	URBANE II CF WFCC BE 4S SUITE + OLIDA SC SEAT CODE: 746350W	BUILDER	BUILDER

VERVE SCHEDULES DISCLAIMER:

- ALL SCHEDULES SHOULD BE CHECKED WITH THE REMAINDER OF THE DRAWING SET.
- SCHEDULED RATES AND AREAS ARE INTENDED FOR ASSISTANCE ONLY. NO RESPONSIBILITY IS TAKEN FOR THE ACCURACY OF QUANTITIES.
- ANY DISCREPANCIES IN SCHEDULES SHOULD BE IDENTIFIED TO THE AUTHOR NOTED.
- ALL AREAS ARE GROSS AREAS, UNLESS NOTED OTHERWISE

CONSULTING ENGINEER




☐ commercial ☐ service stations
☐ mixed-use ☐ quick service restaurants
☐ self storage ☐ child care centres
☐ industrial ☐ large format retail

© 2011 copyright, all rights reserved.
This drawing is the copyright & property of VERVE DESIGN GROUP and must not be used or duplicated without authorisation.
Do not scale this drawing.
Check all dimensions on site prior commencement of works

Revision and approvals				
Rev	Date	Drn	Description	Appr
P1	01.05.2026	PC	REVISED PRELIMINARY ISSUE	SS
A	19.06.2026	PC	BA ISSUE	SS



Project Description
PROPOSED SERVICE STATION
22 ENTERPRISE CCT., MARYBOROUGH W.
Scale @A1
1: 25
Date
APRIL 2026
Approved By
SS

Drawing Title
INTERNAL ELEVATIONS - AMENITIES
Job Number - Drawing Number
26024
Revision
A502
Revision
A

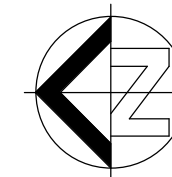


BA ISSUE

THIS DRAWING IS NOT
FOR CONSTRUCTION

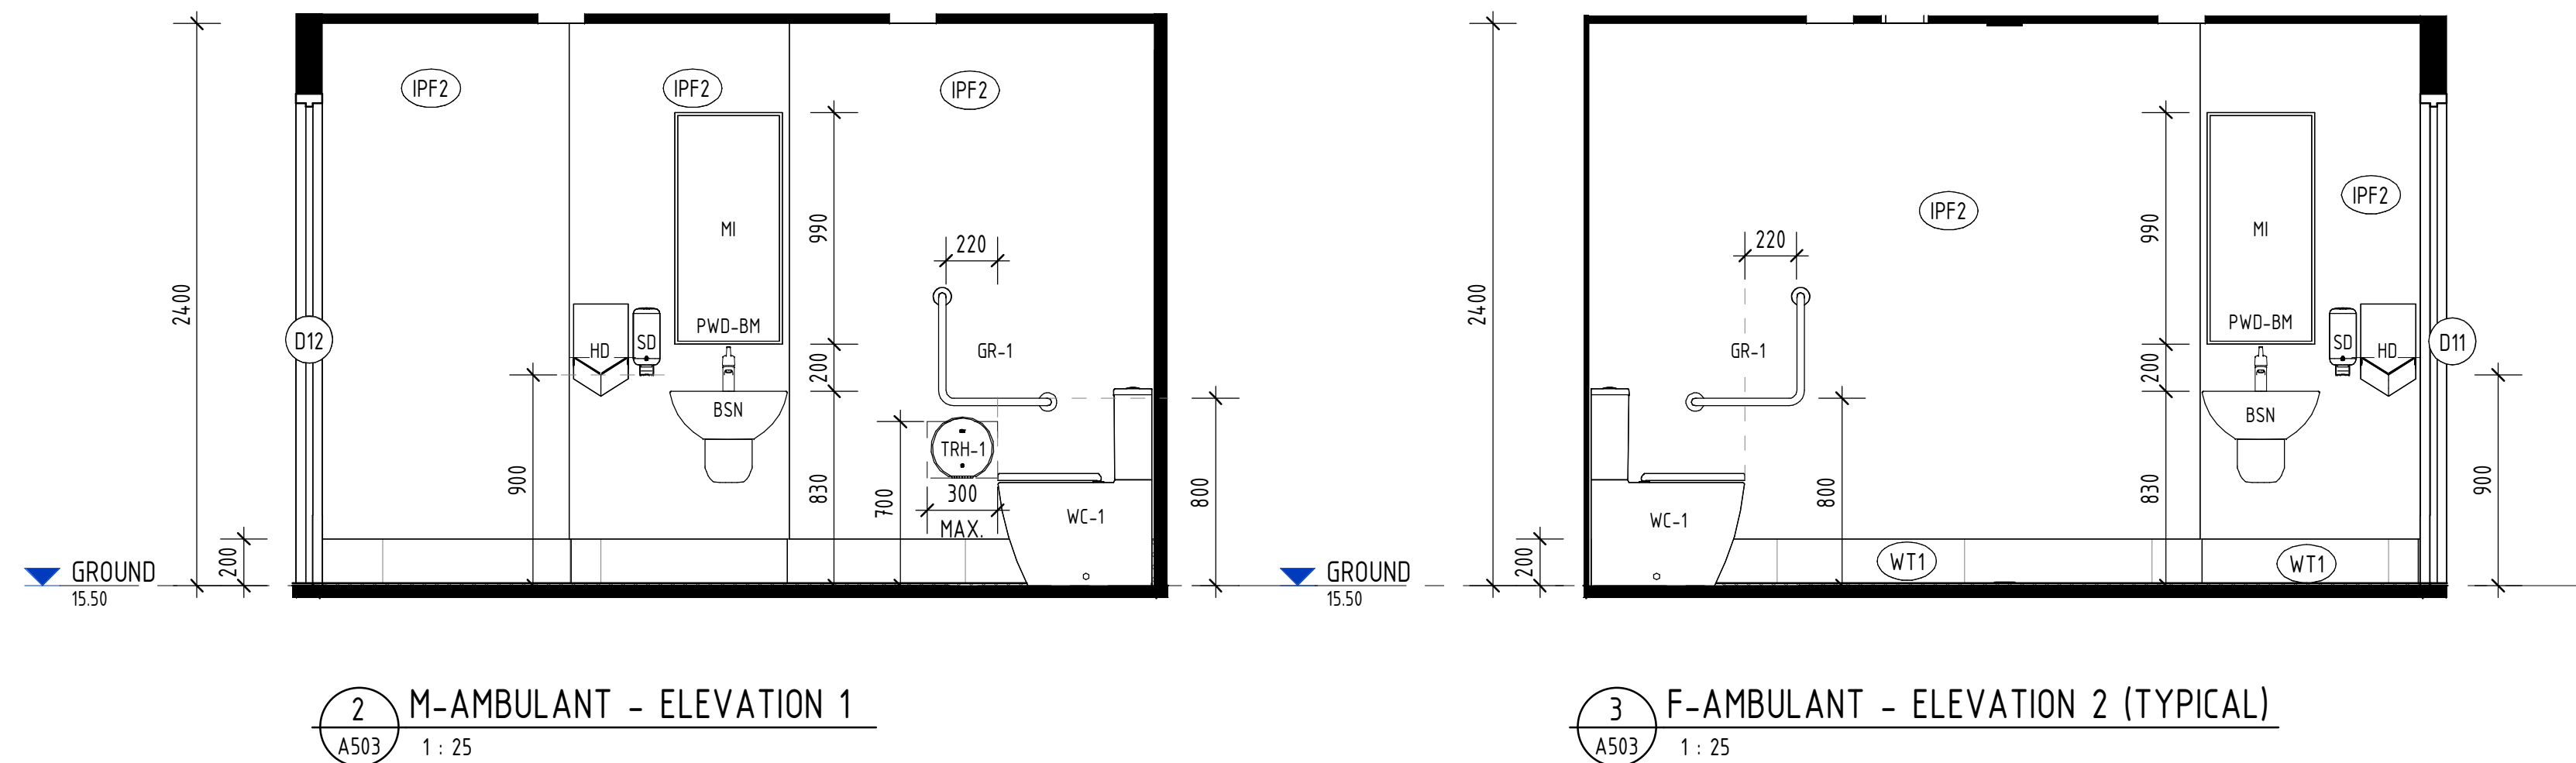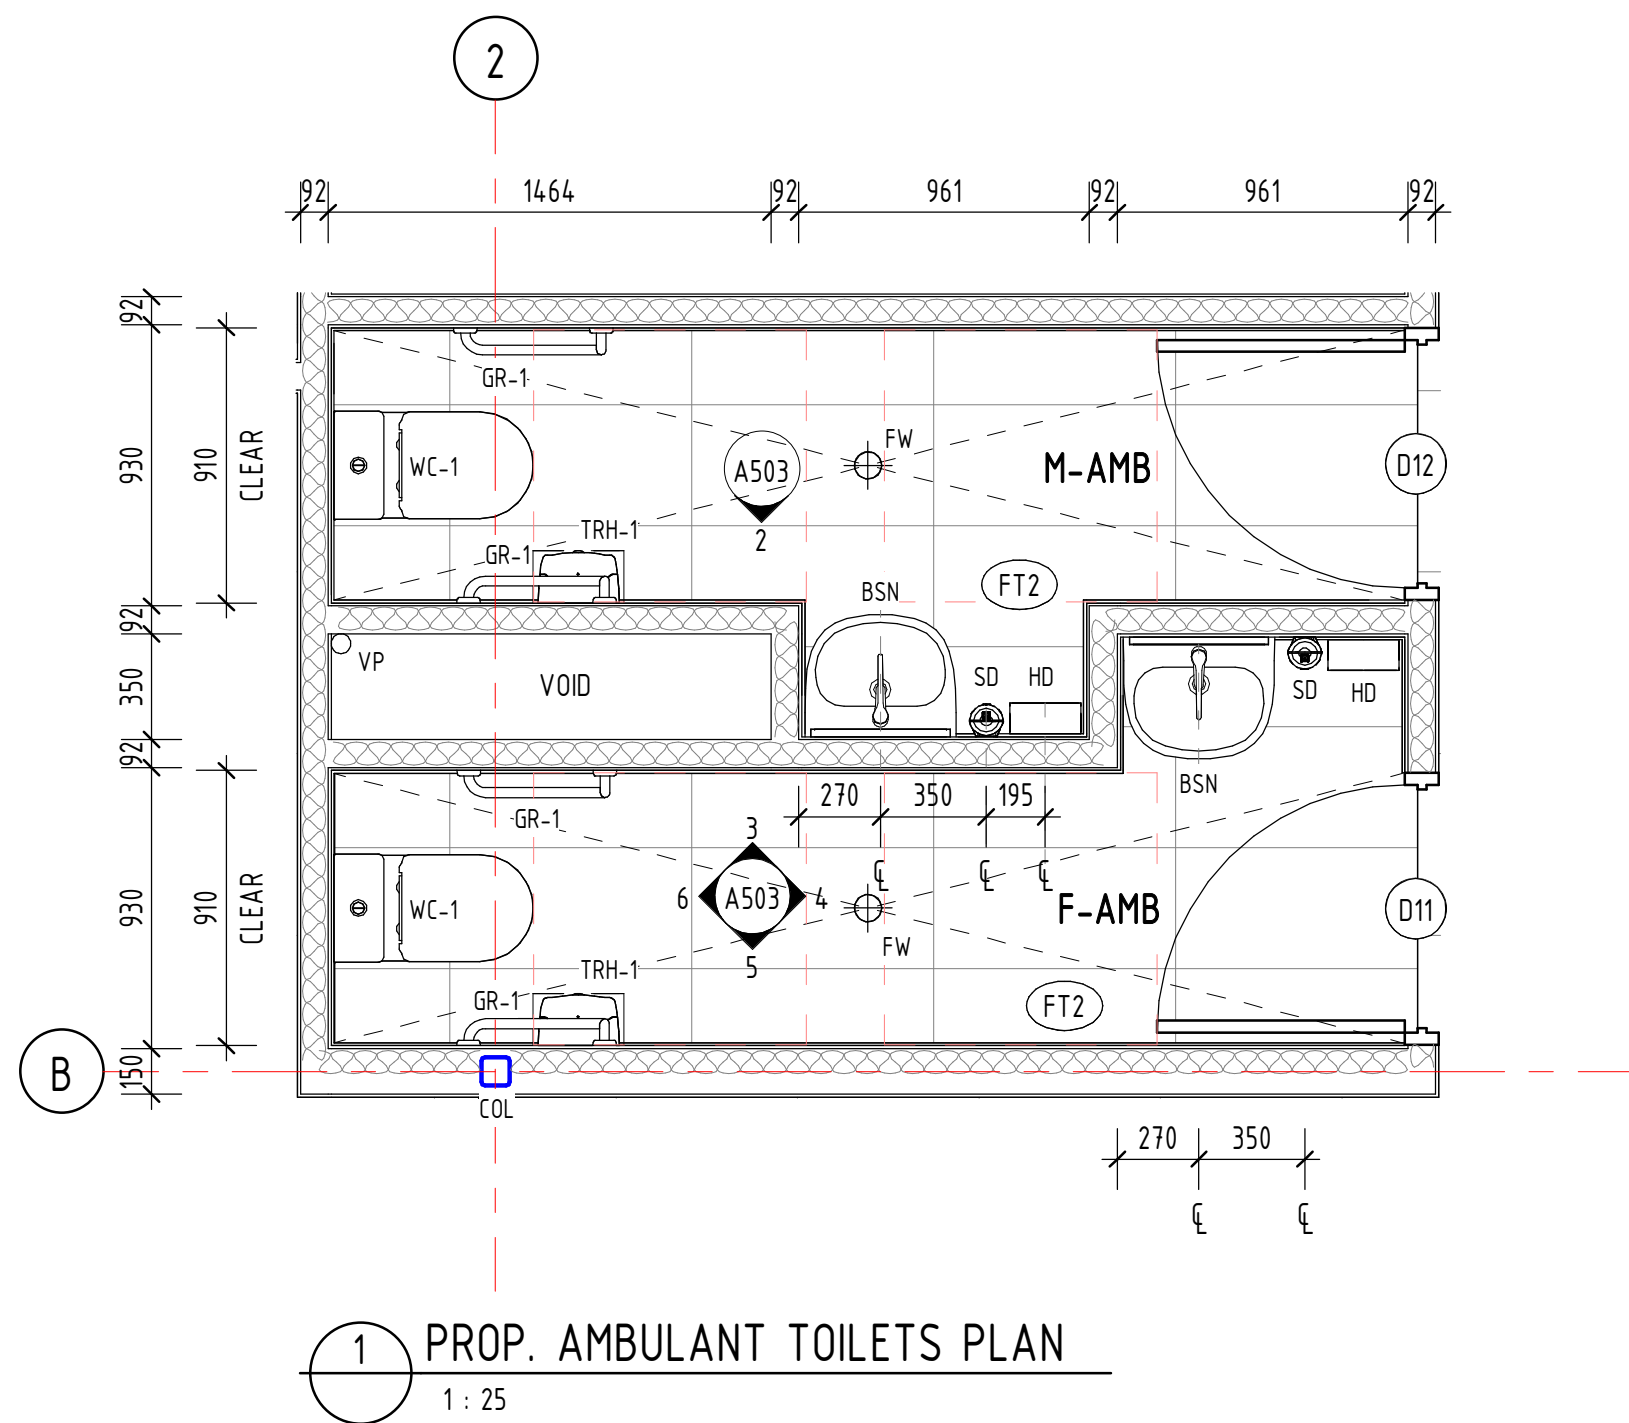

LEGEND	
BSN	HAND BASIN
CH	CLOTHES HOOK
COL	COLUMN - REFER STRUCT. ENG. DETAILS
FW	FLOOR WASTE - REFER HYD. ENG. DETAILS
GR-1	GRAB RAIL - AMBULANT - AS1428.1 COMPLIANT
HD	HAND DRYER
MI	MIRROR
PWD-BM	AS 1428.1 COMPLIANT BASIN MIXER
SD	SOAP DISPENSER - SUPPLIED & INSTALLED BY LESSEE
TRH-1	TOILET ROLL HOLDER AS1428.1 COMPLIANT
VP	VENT PIPE - REFER HYD. ENG. DETAILS
WC-1	AMBULANT TOILET SUITE AS1428.1 COMPLIANT

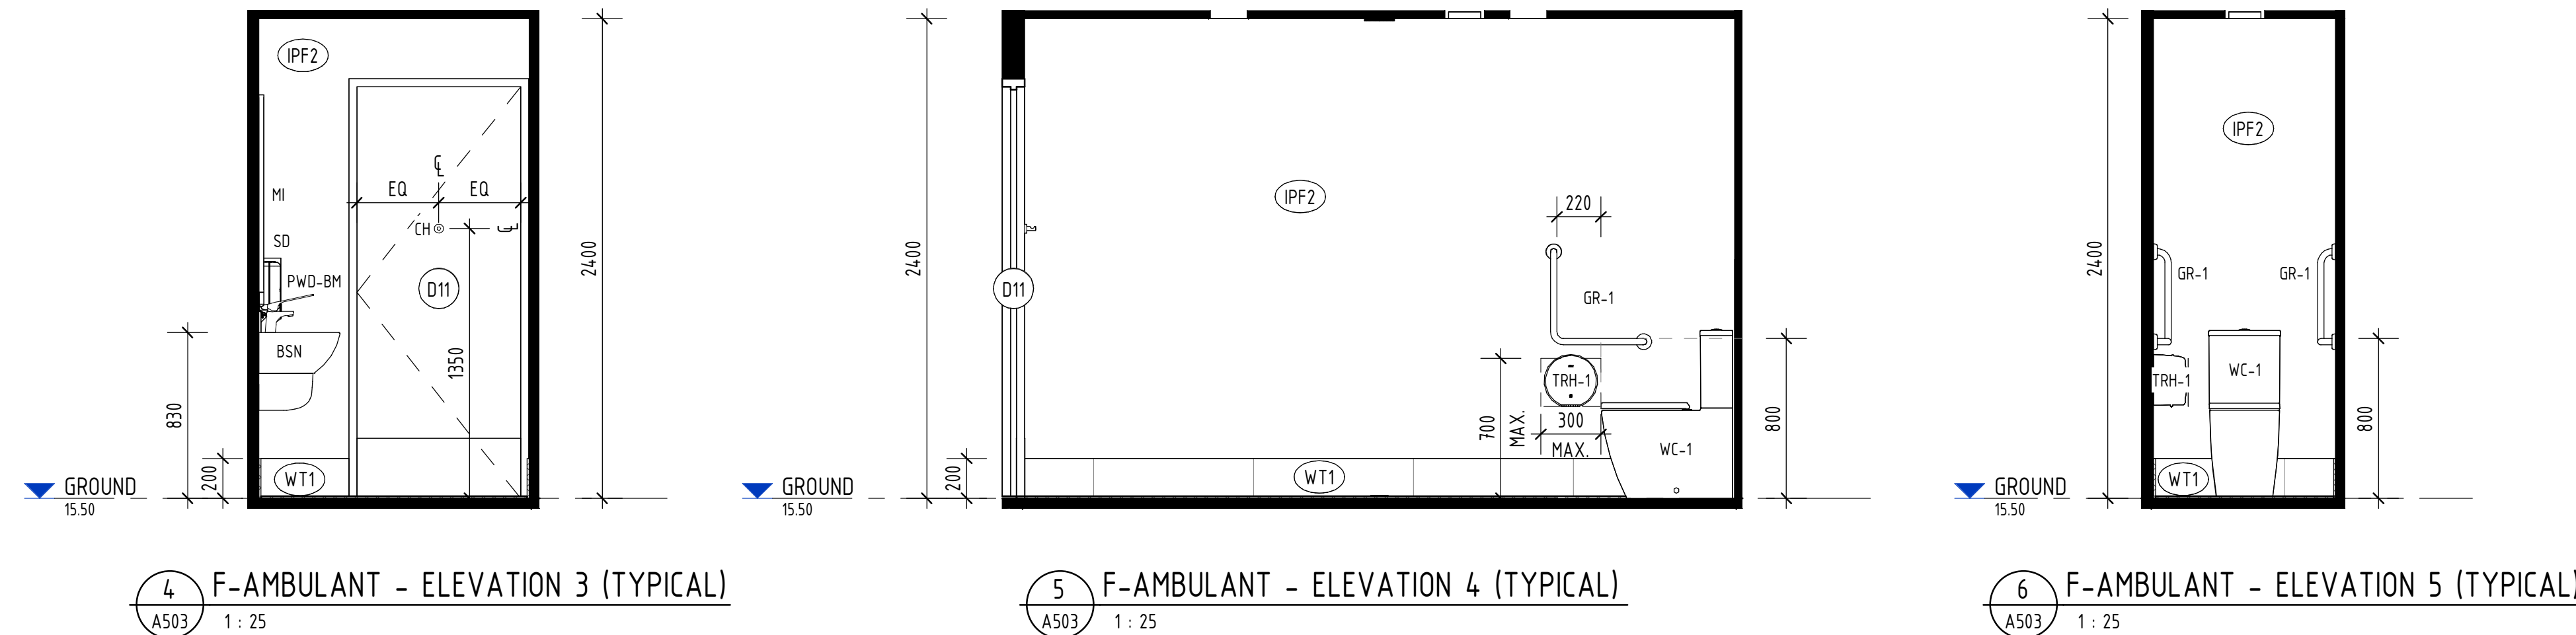

NOTE: ALL ITEMS TO BE INSTALLED IN ACCORDANCE
WITH AS1428.1

INTERNAL FINISHES SCHEDULE			
MARK	MANUFACTURER	DESCRIPTION	COMMENTS
EPX	ALLNEX	NUTHANE SB POLYURETHANE: MID GREY	MIN. R12 SLIP RATING. 100mm HIGH COVING TO WALL
FT1	AMBER TILES LIVERPOOL	FLOOR TILE - 600x600 "DURA GREY"	100mm ALUMINIUM SKIRTING - ARMOURSpray BLACK SATIN: 9109024S. R11 SLIP RATING. GROUT: GREY.
FT2	AMBER TILES LIVERPOOL	FLOOR TILE - 800x400 "STOCKTON WHITE". PRODUCT CODE: AAC84ACD0DR.	R10 SLIP RATING. GROUT: GREY.
FT3	AMBER TILES LIVERPOOL	FLOOR TILE - 600x600 "DURA GREY"	MIN. R12 SLIP RATING. GROUT: GREY EPOXY. 100mm ALUMINIUM SKIRTING - ARMOURSpray BLACK SATIN: 9109024S
IPF2	TAUBMANS	INTERIOR PAINT FINISH - 'CRISP WHITE' LOW SHEEN.	APPLIED TO INTERNAL WALLS.
IPF3	TAUBMANS	SEMI-GLOSS PAINT FINISH: SEALORD T15 25.5	INTERNAL DOORS
L1	LAMINEX	COLOR: GUNMETAL	TOILET PARTITION - PREFABRICATED 19mm MOISTURE RESISTANT LAMINATED BOARD EDGES SHALL BE TREATED WITH HEAVY DUTY PVC EDGE STRIPS
WT1	AMBER TILES LIVERPOOL	WALL TILE - 800x400 "STOCKTON WHITE". PRODUCT CODE: AAC84ACD0DR.	GROUT: GREY.
WT2	COLORTILE	WALL TILE - 280x70 "DARK NIGHT SUNSET MATT" - WHITE GROUT.	GROUT: ARDEX EG15 WHITE. 5mm JOINTS

EQUIPMENT & FIXTURE SCHEDULE - PWD					
MARK	DESCRIPTION	MANUFACTURER	MODEL	SUPPLIER	INSTALLER
BSN-1	HAND BASIN	CAROMA	CAROMA URBANE II RIGHT HAND SHELF WALL BASIN, 1 TAP HOLE (878710W)	BUILDER	BUILDER
CH	COAT HOOK	REECE PLUMBING	SONIA TECNO SINGLE HOOK LARGE-CHROME, CODE:283557	BUILDER	BUILDER
CTM	CLEANERS TAP MIXER	CAROMA	ELEGANCE II LAUNDRY SET. PRODUCT CODE: V631179C4A	BUILDER	BUILDER
MI	MIRROR	JD MACDONALD	MIRROR WITH STAINLESS STEEL INTER-LOK ANGLE FRAME. PRODUCT CODE: 10-0600-V1839	BUILDER	BUILDER
PWD-BM	PWD SINK MIXER	CAROMA	SKANDIC CARE BASIN MIXER (HOT & COLD), PRODUCT CODE: 90995CSA.	BUILDER	BUILDER
SD	SOAP DISPENSER	TORK	LIQUID AND SPRAY SOAP DISPENSER - WHITE, PRODUCT CODE: 560000	BUILDER	BUILDER
SHM	SHOWER RAIL WITH MIXER	CAROMA	TASMAN II RAIL SHOWER 992545C3A	BUILDER	BUILDER
SHM-1	SHOWER MIXER	CAROMA	ACQUA SHOWER MIXER. COLOUR: CHROME. CODE: 90988C	BUILDER	BUILDER
SHS-1	FOLDING SHOWER SEAT	METLAM	ACCESSIBLE FOLDING SHOWER SEAT - COMPACT LAMINATE ML994_CL (OR EQUAL APPROVED)	BUILDER	BUILDER
TRH	TOILET ROLL HOLDER	METLAM	SINGLE SURFACE MOUNTED 10-7305	BUILDER	BUILDER
WC-1	AMBULANT TOILET SUITE	CAROMA	URBANE II CF WFCC BE 4S SUITE + OLIDA SC SEAT CODE: 746350W	BUILDER	BUILDER

VERVE SCHEDULES DISCLAIMER:

- ALL SCHEDULES SHOULD BE CHECKED WITH THE REMAINDER OF THE DRAWING SET.
- SCHEDULED RATES AND AREAS ARE INTENDED FOR ASSISTANCE ONLY. NO RESPONSIBILITY IS TAKEN FOR THE ACCURACY OF QUANTITIES.
- ANY DISCREPANCIES IN SCHEDULES SHOULD BE IDENTIFIED TO THE AUTHOR NOTED.
- ALL AREAS ARE GROSS AREAS, UNLESS NOTED OTHERWISE

CONSULTING ENGINEER



- ☐ commercial
- ☐ mixed-use
- ☐ self storage
- ☐ industrial
- ☐ service stations
- ☐ quick service restaurants
- ☐ child care centres
- ☐ large format retail

© 2011 copyright, all rights reserved.

This drawing is the © copyright & property of VERVE DESIGN GROUP and must not be used or duplicated without authorisation.

Do not scale this drawing.

Check all dimensions on site prior commencement of works

Revision and approvals

Rev	Date	Drn	Description	Appr
P1	01.05.2026	PC	REVISED PRELIMINARY ISSUE	SS
A	19.06.2026	PC	BA ISSUE	SS

Project Description

PROPOSED SERVICE STATION

22 ENTERPRISE CCT., MARYBOROUGH W.

Scale @A1
1: 25

Drawn
PC

Date
APRIL 2026

Approved By
SS

Drawing Title

INTERNAL ELEVATIONS -
AMENITIES

Job Number - Drawing Number
26024

A503

Revision
A

DOOR NOTES

1. TO BE READ IN CONJUNCTION WITH DOOR HARDWARE SCHEDULE PREPARED BY ASSA ABLOY.
2. ALL WORK TO BE COMPLETED IN ACCORDANCE WITH THE SPECIFICATIONS, THE SCOPE OF WORKS, AND THE REQUIREMENTS OF THE LOCAL COUNCIL AND ALL SUPPLY AUTHORITIES
3. ALL WORK TO BE COMPLETED IN ACCORDANCE WITH THE REQUIREMENTS OF THE NATIONAL CONSTRUCTION CODE.
4. ALL DIMENSIONS TO BE CONFIRMED ON SITE BY BUILDER
5. ALL DOOR FURNITURE TO BE 1500mm AFFL TO CENTRE LINE OF HANDLES (U.N.O)
6. AIR GRILLES TO BE SCREW IN TYPE - REFER MECHANICAL DRAWINGS FOR SIZE AND LOCATION
7. REFER TO FLOOR PLAN TO VERIFY DIRECTION OF DOOR SWING
8. SOLID CORE FLUSH PANEL DOORS SHALL COMPLY WITH AS1908. SECTION 4
9. DISABLE ACCESS IS, WHERE REQUIRED, TO COMPLY WITH PART D3 OF THE NCC AND AS1428.1 AND IS TO BE MAINTAINED AT ALL TIMES
10. DOOR SIGNAGE HEIGHTS TO BE LOCATED BETWEEN 1200mm AND 1600mm AFFL, PER AS1428.1
11. ALL EXTERNAL DOORS TO HAVE WEATHER SEALS
12. ALL INTERNAL DOORS TO HAVE A MINIMUM LUMINANCE CONTRAST OF 30% IN ACCORDANCE WITH AS1428.1 U.N.O.
13. ALL DOOR ELEVATIONS ARE VIEWED EXTERNALLY
14. CONTRACTOR TO REVIEW & ENSURE ALL HARDWARE IS APPROPRIATE FOR ITS INTENDED APPLICATION BEFORE PRICING & ORDERING

Enter first colour LRV here
89.36

Enter second colour LRV here
18.24

Luminance Contrast Result 67%

LRV = 67%

Pass | Colour suitability for **Integrated** Tactile Indicators: **30%** contrast required.


Pass | Colour suitability for **Discrete** Tactile Indicators: **45%** contrast required.

Pass | Colour suitability for **Composite** Tactile Indicators: **60%** contrast required.

This Calculator uses the Bowman-Sapolinski Equation as stipulated in AS/NZS 1428.4.1:2009

Luminance Contrast Formula = $125 \frac{(Y2 - Y1)}{(Y1 + Y2 + 25)}$

TYPICAL INTERNAL WALL-DOOR COLOUR CONTRAST

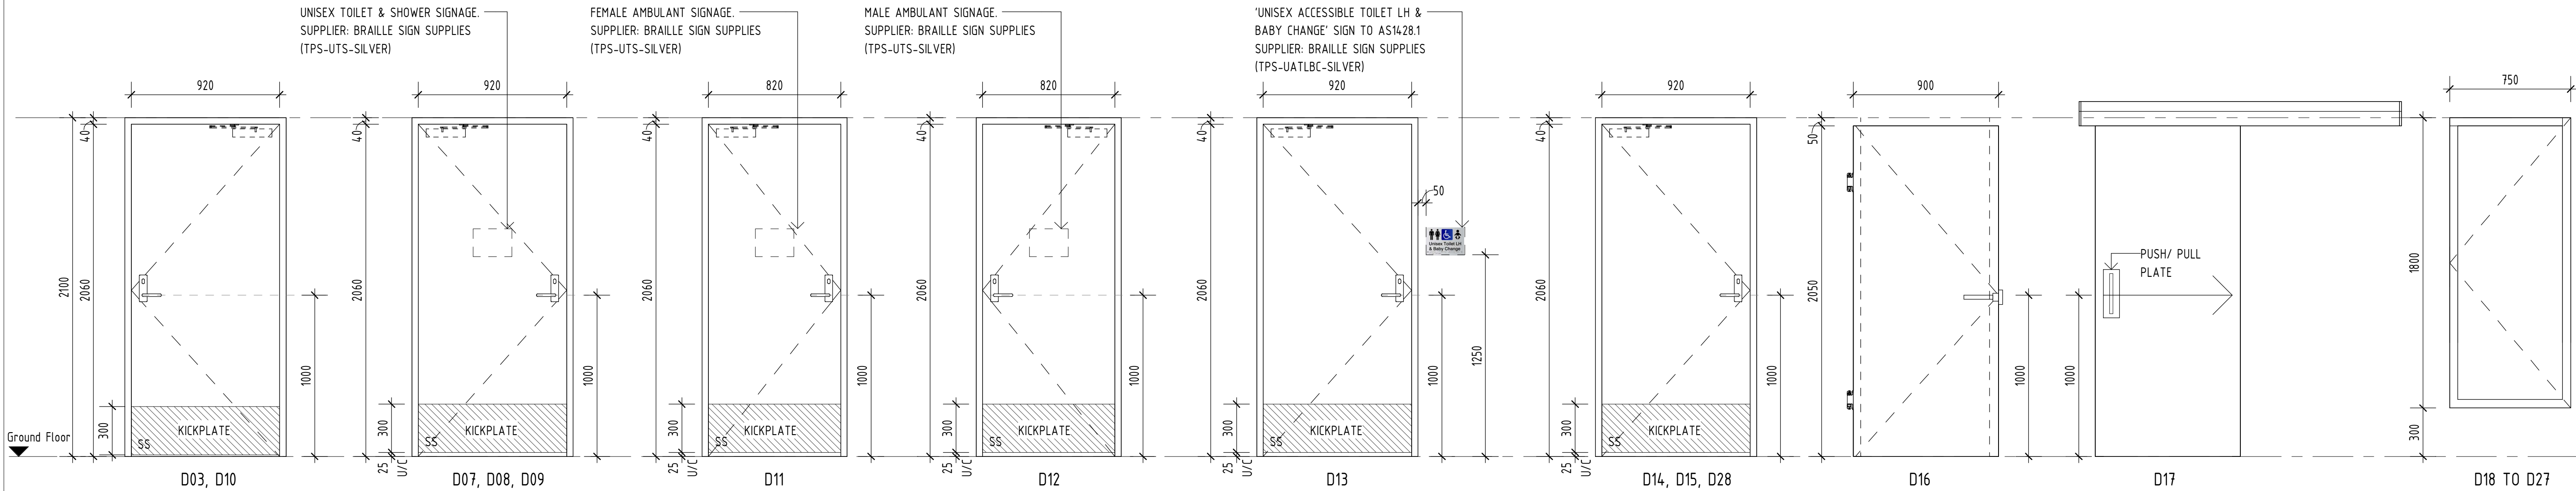

DOOR SCHEDULE

DOOR No.	ROOM NAME	TYPE	DOOR LEAF				DOOR FRAME		HARDWARE					KICK PANEL (BY FACE)		DOOR GRILLE	SECURITY	SIGNAGE	COMMENTS
			WIDTH	HEIGHT	THICKNESS	DESCRIPTION	FINISH	TYPE	FINISH	HINGE	LOCK	HARDWARE/FURNITURE	CLOSER	DOOR STOP	SWING	NON SWING			
D01	SALES	AUTOMATED DOUBLE SLIDING DOOR				ALUMINIUM FRAMED GLASS AUTO-SLIDING DOOR	CLEAR LAMINATED SAFETY GLASS	ALUMINIUM	POWDERCOAT TO MATCH GLAZING SUITE								-	-	
D02	TRUCK DRIVER LOUNGE		900	2050	45	ALUMINIUM FRAMED GLASS DOOR	CLEAR LAMINATED SAFETY GLASS	ALUMINIUM	POWDERCOAT TO MATCH GLAZING SUITE						-	-	-		
D03	AIRLOCK	SINGLE SWING	920	2040	40	SOLID CORE FLUSH FACED TIMBER DOOR	PAINT FINISH: IPF3	ALUMINIUM	NATURAL ANODISED						YES	YES	-	-	
D04	WC & SHOWER	SINGLE SWING	600	1700	19	PARTITION SYSTEM SWING SINGLE DOOR	LAMINEX 'BLACK NUANCE'		LAMINEX 'BLACK NATURAL'			-	-				-	-	
D05	WC & SHOWER	SINGLE SWING	600	1700	19	PARTITION SYSTEM SWING SINGLE DOOR	LAMINEX 'BLACK NUANCE'		LAMINEX 'BLACK NATURAL'			-	-				-	-	
D06	WC & SHOWER	SINGLE SWING	600	1700	19	PARTITION SYSTEM SWING SINGLE DOOR	LAMINEX 'BLACK NUANCE'		LAMINEX 'BLACK NATURAL'			-	-				-	-	
D07	WC & SHOWER	SINGLE SWING	920	2040	40	SOLID CORE FLUSH FACED TIMBER DOOR	PAINT FINISH: IPF3	ALUMINIUM	NATURAL ANODISED						-	-	-	TO AS1428.1	25mm UNDER CUT
D08	WC & SHOWER	SINGLE SWING	920	2040	40	SOLID CORE FLUSH FACED TIMBER DOOR	PAINT FINISH: IPF3	ALUMINIUM	NATURAL ANODISED						-	-	-	TO AS1428.1	25mm UNDER CUT
D09	WC & SHOWER	SINGLE SWING	920	2040	40	SOLID CORE FLUSH FACED TIMBER DOOR	PAINT FINISH: IPF3	ALUMINIUM	NATURAL ANODISED						-	-	-	TO AS1428.1	25mm UNDER CUT
D10	LAUNDRY	SINGLE SWING	920	2040	40	SOLID CORE FLUSH FACED TIMBER DOOR	PAINT FINISH: IPF3	ALUMINIUM	NATURAL ANODISED						YES	YES	-	-	25mm UNDER CUT
D11	F-AMB	SINGLE SWING	820	2040	40	SOLID CORE FLUSH FACED TIMBER DOOR	PAINT FINISH: IPF3	ALUMINIUM	NATURAL ANODISED						YES	YES	-	TO AS1428.1	FITTED WITH "D" TYPE LEVER HANDLES
D12	M-AMB	SINGLE SWING	820	2040	40	SOLID CORE FLUSH FACED TIMBER DOOR	PAINT FINISH: IPF3	ALUMINIUM	NATURAL ANODISED						YES	YES	-	TO AS1428.1	FITTED WITH "D" TYPE LEVER HANDLES
D13	PWD	SINGLE SWING	920	2040	40	SOLID CORE FLUSH FACED TIMBER DOOR	PAINT FINISH: IPF3	ALUMINIUM	NATURAL ANODISED						YES	YES	-		25mm UNDER CUT, FITTED WITH "D" TYPE LEVER HANDLES
D14	DRY STORE	SINGLE SWING	920	2040	40	SOLID CORE FLUSH FACED TIMBER DOOR	PAINT FINISH: IPF3	ALUMINIUM	NATURAL ANODISED						YES	YES	-		
D15	OFFICE	SINGLE SWING	920	2040	40	SOLID CORE FLUSH FACED TIMBER DOOR	PAINT FINISH: IPF3	ALUMINIUM	NATURAL ANODISED						YES	YES	-		
D16	COLD ROOM	SINGLE SWING	800	2000	75	BY COOLROOM CONTRACTOR		-							-	-	-		
D17	FREEZER	SLIDING DOOR	800	2000	75	BY COOLROOM CONTRACTOR									-	-	-		
D18	FREEZER	AS PER MANUFACTURER				BY COOLROOM CONTRACTOR													FREEZER / COLD ROOM DISPLAY SHELVING DOOR - TO BE SUPPLIED & INSTALLED BY LESSEE CONTRACTOR
D19	FREEZER	AS PER MANUFACTURER				BY COOLROOM CONTRACTOR													FREEZER / COLD ROOM DISPLAY SHELVING DOOR - TO BE SUPPLIED & INSTALLED BY LESSEE CONTRACTOR
D20	COLD ROOM	AS PER MANUFACTURER				BY COOLROOM CONTRACTOR													FREEZER / COLD ROOM DISPLAY SHELVING DOOR - TO BE SUPPLIED & INSTALLED BY LESSEE CONTRACTOR
D21	COLD ROOM	AS PER MANUFACTURER				BY COOLROOM CONTRACTOR													FREEZER / COLD ROOM DISPLAY SHELVING DOOR - TO BE SUPPLIED & INSTALLED BY LESSEE CONTRACTOR
D22	COLD ROOM	AS PER MANUFACTURER				BY COOLROOM CONTRACTOR													FREEZER / COLD ROOM DISPLAY SHELVING DOOR - TO BE SUPPLIED & INSTALLED BY LESSEE CONTRACTOR
D23	COLD ROOM	AS PER MANUFACTURER				BY COOLROOM CONTRACTOR													FREEZER / COLD ROOM DISPLAY SHELVING DOOR - TO BE SUPPLIED & INSTALLED BY LESSEE CONTRACTOR
D24	COLD ROOM	AS PER MANUFACTURER				BY COOLROOM CONTRACTOR													FREEZER / COLD ROOM DISPLAY SHELVING DOOR - TO BE SUPPLIED & INSTALLED BY LESSEE CONTRACTOR
D25	COLD ROOM	AS PER MANUFACTURER				BY COOLROOM CONTRACTOR													FREEZER / COLD ROOM DISPLAY SHELVING DOOR - TO BE SUPPLIED & INSTALLED BY LESSEE CONTRACTOR
D26	COLD ROOM	AS PER MANUFACTURER				BY COOLROOM CONTRACTOR													FREEZER / COLD ROOM DISPLAY SHELVING DOOR - TO BE SUPPLIED & INSTALLED BY LESSEE CONTRACTOR
D27	COLD ROOM	AS PER MANUFACTURER				BY COOLROOM CONTRACTOR													FREEZER / COLD ROOM DISPLAY SHELVING DOOR - TO BE SUPPLIED & INSTALLED BY LESSEE CONTRACTOR
D28	FOOD PREP	SINGLE SWING	920	2040	40	SOLID CORE FLUSH FACED TIMBER DOOR	PAINT FINISH: IPF3	ALUMINIUM	NATURAL ANODISED						YES	YES	-		

- VERVE SCHEDULES DISCLAIMER:**
1. ALL SCHEDULES SHOULD BE CHECKED WITH THE REMAINDER OF THE DRAWING SET.
2. SCHEDULED RATES AND AREAS ARE INTENDED FOR ASSISTANCE ONLY. NO RESPONSIBILITY IS TAKEN FOR THE ACCURACY OF QUANTITIES.
3. ANY DISCREPANCIES IN SCHEDULES SHOULD BE IDENTIFIED TO THE AUTHOR NOTED.
4. ALL AREAS ARE GROSS AREAS, UNLESS NOTED OTHERWISE

CONSULTING ENGINEER



- ☐ commercial ☐ service stations ☐ mixed-use ☐ quick service restaurants ☐ self storage ☐ child care centres ☐ industrial ☐ large format retail

© 2011 copyright, all rights reserved.
This drawing is the © copyright & property of VERVE DESIGN GROUP and must not be used or duplicated without authorisation.
Do not scale this drawing.
Check all dimensions on site prior commencement of works

Rev	Date	Drn	Description	Appr
P1	01.05.2026	PC	REVISED PRELIMINARY ISSUE	SS
A	19.06.2026	PC	BA ISSUE	SS

Project Description
PROPOSED SERVICE STATION

22 ENTERPRISE CCT., MARYBOROUGH W.

Scale @A1
As indicated

Date
APRIL 2026

Approved By
SS

Drawing Title
DOOR SCHEDULE

Job Number -- Drawing Number
26024

Revision
A



THIS DRAWING IS NOT
FOR CONSTRUCTION

The image contains two architectural drawings of window elevations, labeled W01 and W02.

W01 ELEVATION: This drawing shows a window unit with a total width of 3600 units, divided into three equal panels. The height is 3000 units, with 1900 units for the glazing and 1100 units for the base. The top of the glazing is at an elevation of 18.50, and the base is at 15.50. The middle panel contains a hexagonal symbol labeled W01. The side panels are labeled FG.

W02 ELEVATION: This drawing shows a window unit with a total width of 4100 units, divided into three equal panels. The height is 3000 units, with 1900 units for the glazing and 1100 units for the base. The top of the glazing is at an elevation of 18.50, and the base is at 15.50. The middle panel contains a hexagonal symbol labeled W02. The side panels are labeled FG. A fourth panel on the right is labeled W03.

Both drawings include a scale of 1:25 and a north arrow pointing towards the top of the page.

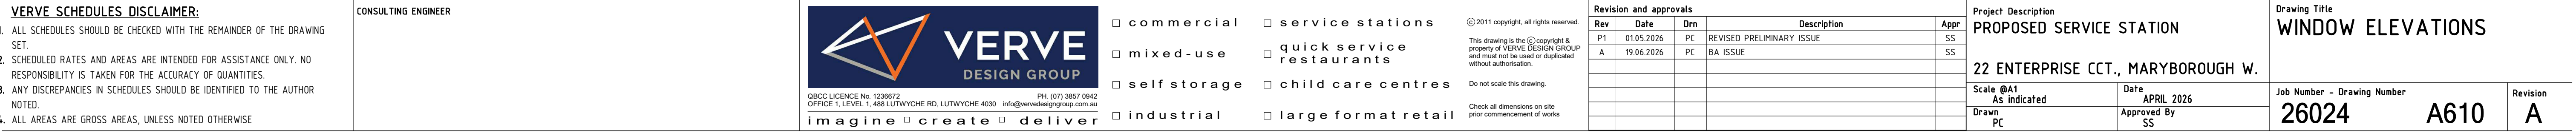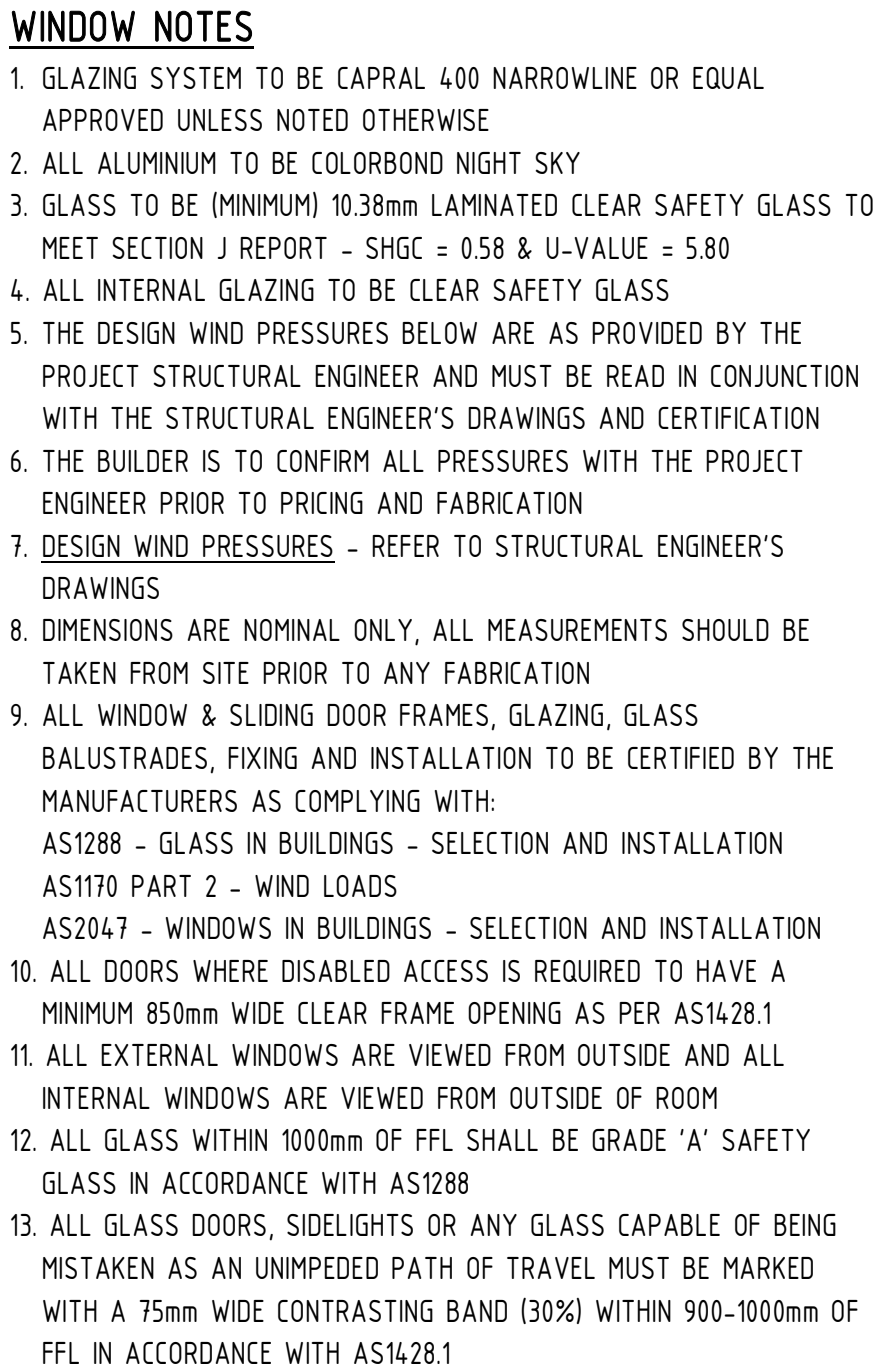

DOCUMENT TRANSMITTAL



PROJECT: PROPOSED SERVICE STATION

PROJECT No.: 26024

CLIENT: Owner

DATE OF ISSUE

DAY	19													
MONTH	6													
YEAR	26													
INITIALS	PC													

DISTRIBUTION LIST

COMPANY	PERSON	No. OF COPIES												
AURORA PROJECT MAN	VAUGHAN REDD	1												

REASON FOR ISSUE

P=PRELIM I=INFORMATION DA=DEVELOPMENT APPROVAL BA=BUILDING APPLICATION T=TENDER C=CONSTRUCTION AB=AS BUILTS	BA													
---	----	--	--	--	--	--	--	--	--	--	--	--	--	--

DOCUMENT FORMAT & SIZE

DOCUMENT FORMAT	DWG PDF													
PAPER SIZE	A1													

METHOD OF ISSUE

M=MAIL H=HAND C=COURIER P=PICKUP E=EMAIL AC=ACONEX	SP													
---	----	--	--	--	--	--	--	--	--	--	--	--	--	--

DOCUMENTATION LIST

TITLE	DWG. No.	REVISION												
TITLE SHEET & DRAWING SCHEDULE	A000	A												
NOTES	A001	A												
GRID SETOUT PLAN	A050	A												
PROP. OVERALL SITE PLAN	A100	A												
PART SITE PLAN - A	A101	A												
PART SITE PLAN - B	A102	A												
PROP. FLOOR PLAN	A110	A												
PROP. ROOF PLAN	A115	A												
PROP. REFLECTED CEILING PLAN	A120	A												
PROP. SLAB SETOUT PLAN	A130	A												
PROP. FLOOR FINISHES & PARTITIONS PLAN	A140	A												
PROP. BUILDING ELEVATIONS	A200	A												
PROP. BUILDING ELEVATIONS	A201	A												
PROP. BUILDING SECTIONS	A210	A												
PROP. CAR & TRUCK FORECOURT CANOPY PLANS	A250	A												

TITLE	DWG. No.	REVISION												
PROP. TRUCK FORECOURT CANOPY ROOF & RCP	A251	A												
PROP. CAR FORECOURT CANOPY ROOF	A252	A												
PROP. CAR FORECOURT CANOPY RCP	A253	A												
PROP. CAR FORECOURT CANOPY ELEVATIONS	A260	A												
PROP. TRUCK FORECOURT CANOPY ELEVATIONS	A261	A												
PROP. FORECOURT TRUCK CANOPY SECTIONS	A262	A												
PROP. FORECOURT CAR CANOPY SECTIONS	A263	A												
WALL SECTIONS	A300	A												
INTERNAL ELEVATIONS - AMENITIES	A500	A												
INTERNAL ELEVATIONS - AMENITIES	A501	A												
INTERNAL ELEVATIONS - AMENITIES	A502	A												
INTERNAL ELEVATIONS - AMENITIES	A503	A												
DOOR SCHEDULE	A600	A												
WINDOW ELEVATIONS	A610	A												