

ELEVATION B

ALL GLASS TO CONFORM WITH AS1288-2006 : GLASS IN BUILDINGS

SELECTED CERAMIC FLOOR TILING

- DENOTES 300mm DEEP BULKHEAD TO PLASTER FACE - UNLESS NOTED OTHERWISE. REFER ALSO INTERNAL ELEVATIONS.
NOTE: DIMENSIONS LOCATING WINDOWS ARE NOMINAL.
NOTE: ALL INTERNAL DOOR HEIGHTS TO BE 2040mm. HIGH UNLESS OTHERWISE NOTED.
NOTE: DIMENSIONS FOR WALL SETOUT ARE NOMINAL & TO FACE OF STUDWORK.
NOTE: BULKHEADS & NIBS ARE NOMINAL SIZES ONLY.
NOTE: LIFT-OFF HINGES TO W.C. DOOR UNLESS DISTANCE TO PAN IS 1.2m OR GREATER
NOTE: DOWN PIPE LOCATIONS ARE INDICATIVE, EXACT LOCATIONS TO BE CONFIRMED PRIOR TO POP PENETRATIONS TO GUTTERING.

ELEVATION A

ELEVATION C

PROVIDE SEALED INSITU WASTE CONNECTION TO GROUND FLOOR BATH & WC, GROUND & FIRST FLOOR SHOWER WASTE POINTS

SMOKE DETECTOR TO A.S 3786 - MULTIPLE POINTS TO BE INTERCONNECTED

MANHOLE

ALL WET AREAS TO COMPLY WITH A.S. 3740
NOTE: ALL SANITARY COMPARTMENTS TO COMPLY WITH CURRENT B.C.A. PART 3.8.3.3.
NOTE: REF. FRE. WM. CD. DW INDICATE POSITION ONLY.

ELEVATION D

Spec:

SIMONDS HOMES RANGE (QLD)

View:

GROUND FLOOR PLAN

(STANDARD)

- DEVELOPMENT DIVISION PURPOSE ONLY -

Customer:

Address:


V1

Sheet No:
2.1

AREAS.

Ground Floor:	123.89	sq.m	13.34	sqrs
First Floor:	121.81	sq.m	13.11	sqrs
Subtotal:	245.71	sq.m	26.45	sqrs
Porch:	4.08	sq.m	0.44	sqrs
Garage:	36.40	sq.m	3.92	sqrs
Alfresco:	12.00	sq.m	1.29	sqrs
Total Area:	298.19	sq.m	32.10	sqrs

House:	ARMSTRONG 32_298-14D		
Facade:	HARLEQUIN		
Drawn:	XNAMEX	Job No:	XX00000XX
Design:	X00X	Mastered:	T.L
		Checked:	X00X

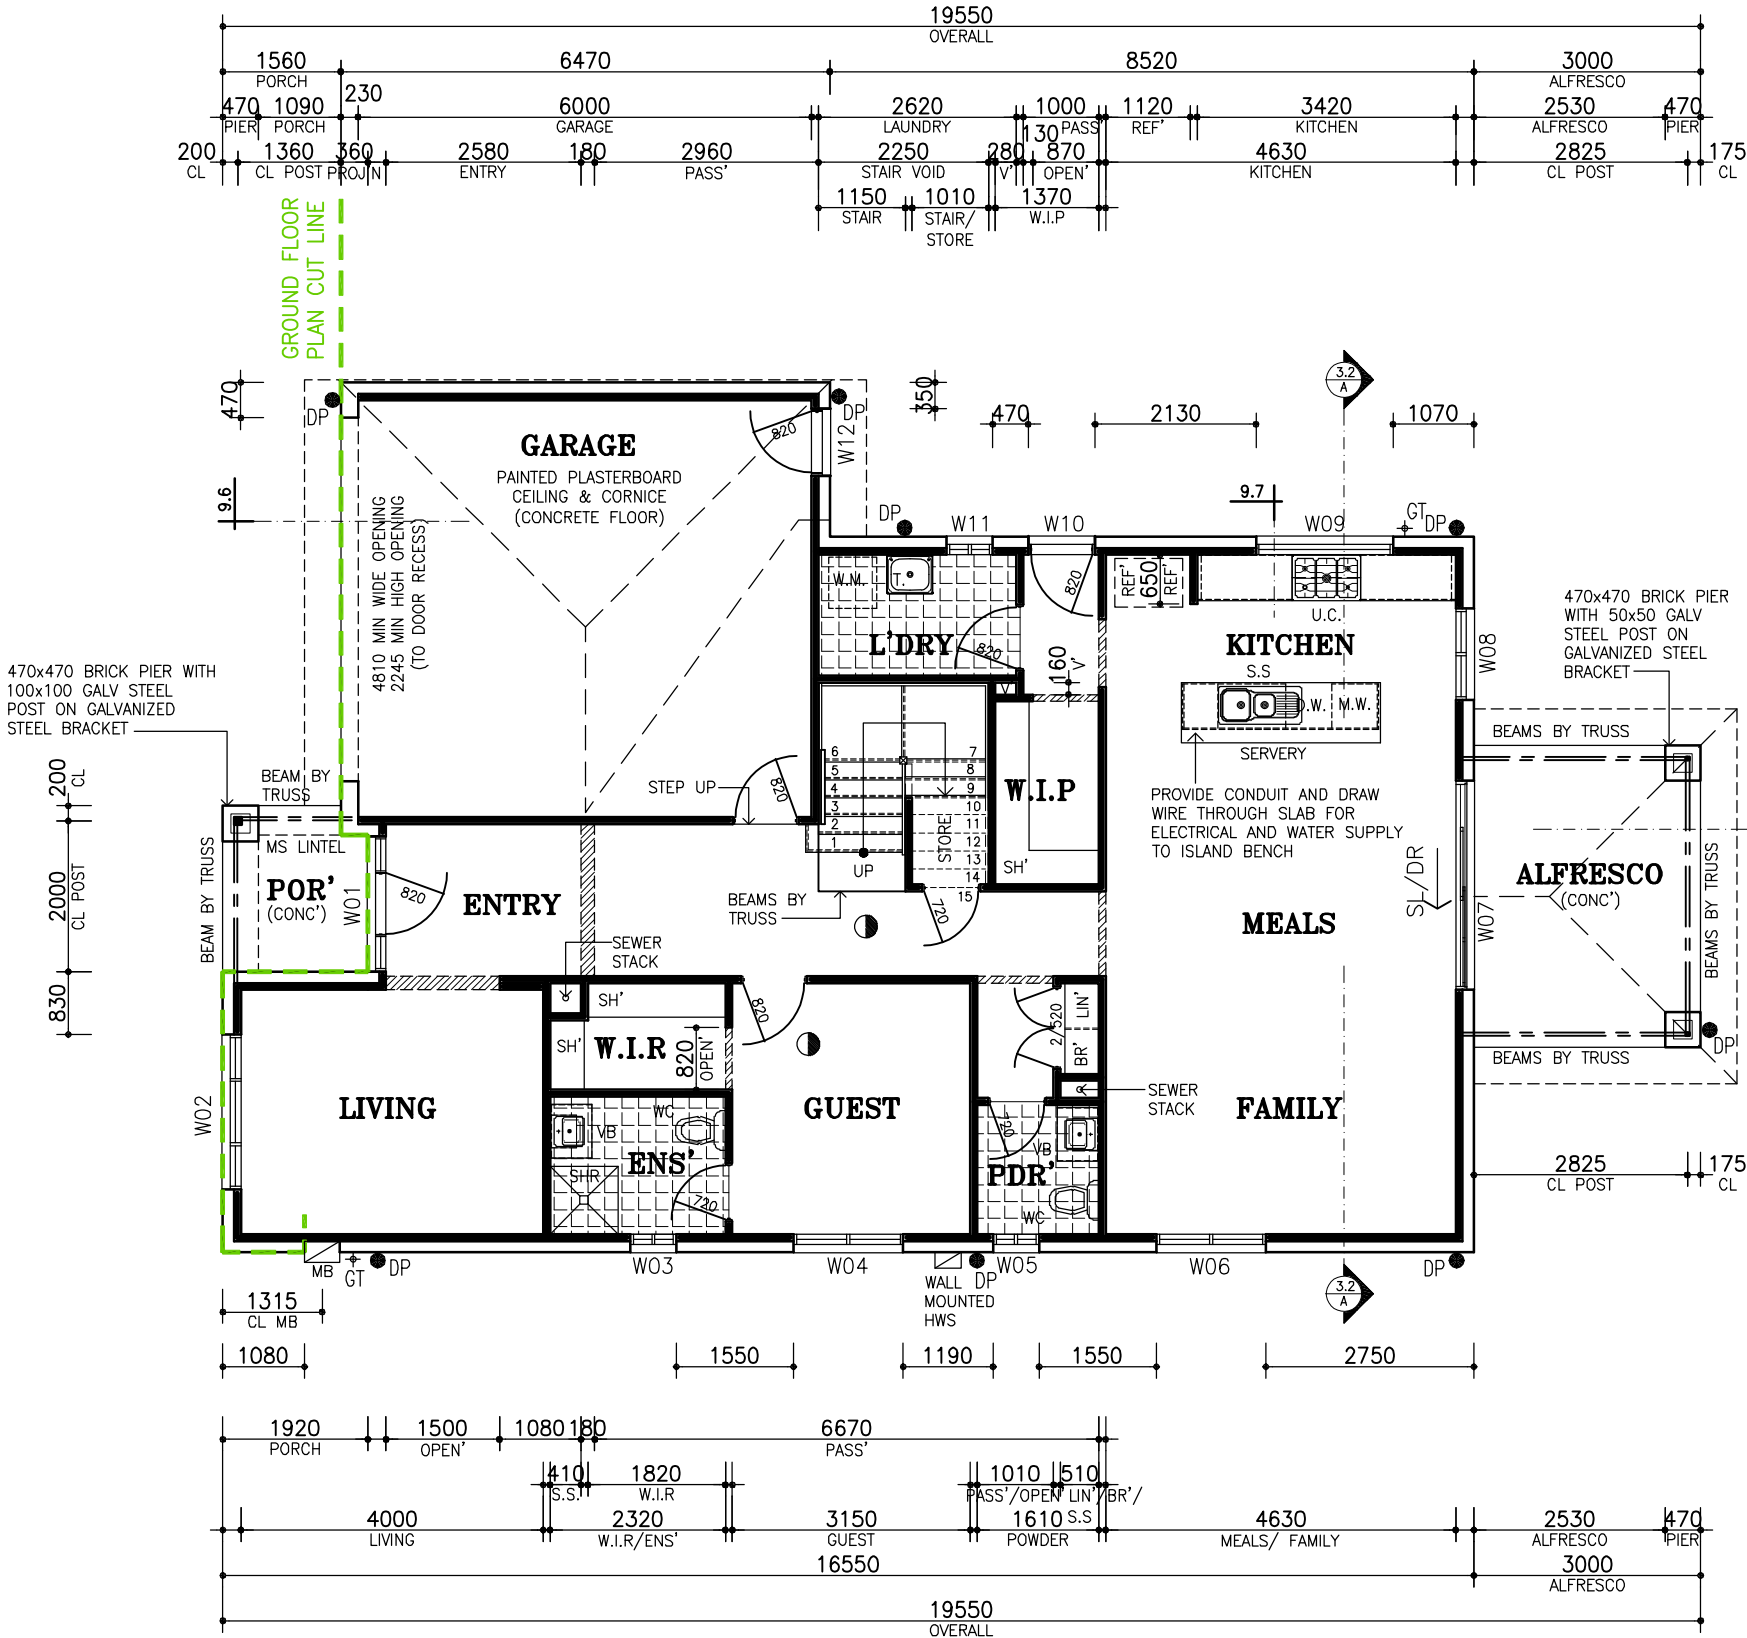


SIMONDS

ELEVATION B

ALL GLASS TO CONFORM WITH AS1288-2006 : GLASS IN BUILDINGS

SELECTED CERAMIC FLOOR TILING

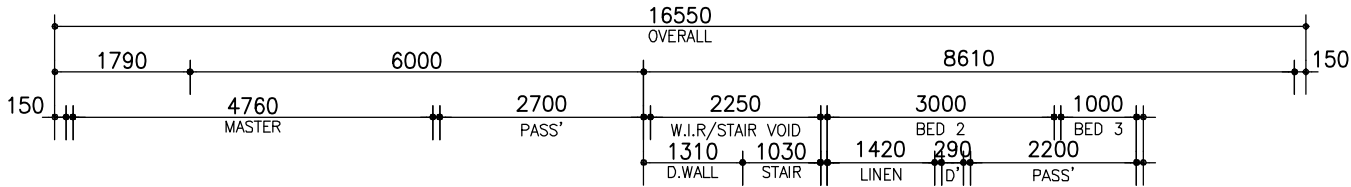

- DENOTES 300mm DEEP BULKHEAD TO PLASTER FACE - UNLESS NOTED OTHERWISE. REFER ALSO INTERNAL ELEVATIONS.

NOTE: DIMENSIONS LOCATING WINDOWS ARE NOMINAL.


NOTE: ALL INTERNAL DOOR HEIGHTS TO BE 2040mm. HIGH UNLESS OTHERWISE NOTED.

NOTE: DIMENSIONS FOR WALL SETOUT ARE NOMINAL & TO FACE OF STUDWORK.



NOTE: BULKHEADS & NIBS ARE NOMINAL SIZES ONLY.

NOTE: LIFT-OFF HINGES TO W.C. DOOR UNLESS DISTANCE TO PAN IS 1.2m OR GREATER

ELEVATION A

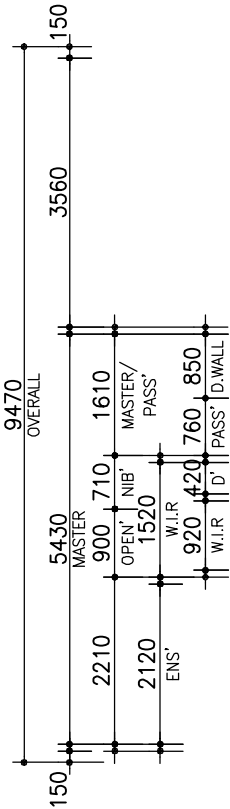

PROVIDE INSULATION TO CANTILEVERED FLOOR SPACE AND FLOOR SPACE BETWEEN PORCH AND F.F.

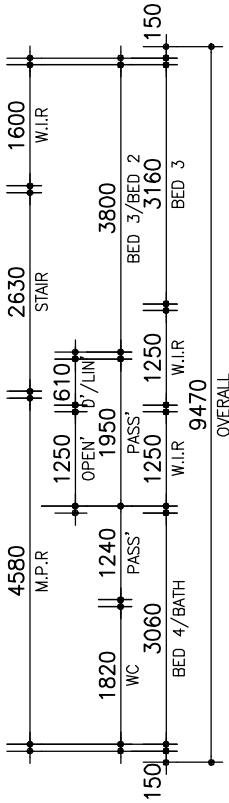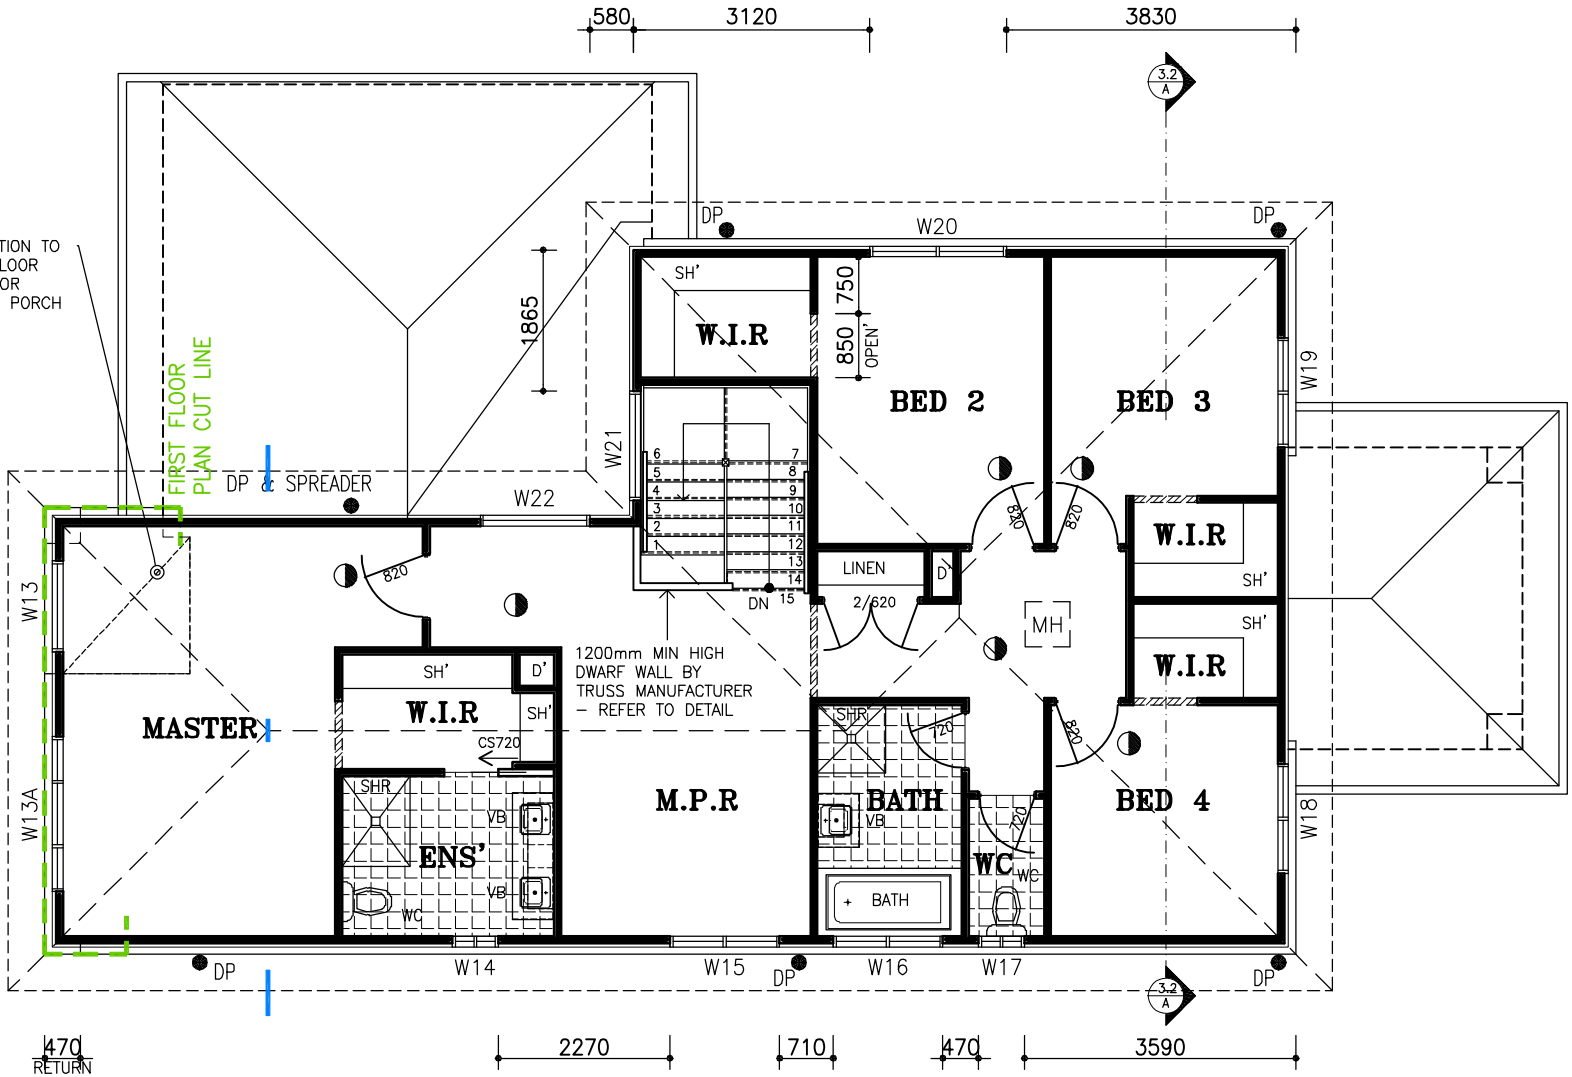

ELEVATION C

PROVIDE SEALED INSITU WASTE CONNECTION TO GROUND FLOOR BATH & WC, GROUND & FIRST FLOOR SHOWER WASTE POINTS

SMOKE DETECTOR TO A.S 3786 - MULTIPLE POINTS TO BE INTERCONNECTED

MANHOLE

ELEVATION D

SIMONDS QLD CONSTRUCTIONS P/L ACN 144 869 643 QBCC LICENCE NUMBER 1192095

HEAD OFFICE 3894 PACIFIC HIGHWAY, LOGANHOLME QLD 4129 INTERNET www.simonds.com.au

TELEPHONE (07) 3457 8000 ENQUIRIES Email: enquiries@simonds.com.au Ph: 1300 SIMONDS

SIMONDS

Spec: SIMONDS HOMES RANGE (QLD)

(STANDARD)

- DEVELOPMENT DIVISION PURPOSE ONLY -

© COPYRIGHT 2003 SIMONDS IP Pty Ltd (ACN 144 839 805) (ABN 56 144 839 805) NOT TO BE REPRODUCED IN PART OR WHOLE WITHOUT EXPRESS PERMISSION.

View: FIRST FLOOR PLAN

Customer:

Address:

V1

Sheet No: 2.2

Scale: 1:100@A3

Date: 00.00.00


House: ARMSTRONG 32_298-14D

Facade: HARLEQUIN

Drawn: XNAMEX Job No: XX000000XX


Design: X00X Mastered: T.L Checked: X00X

ALL GLASS TO CONFORM WITH AS1288-2006 : GLASS IN BUILDINGS

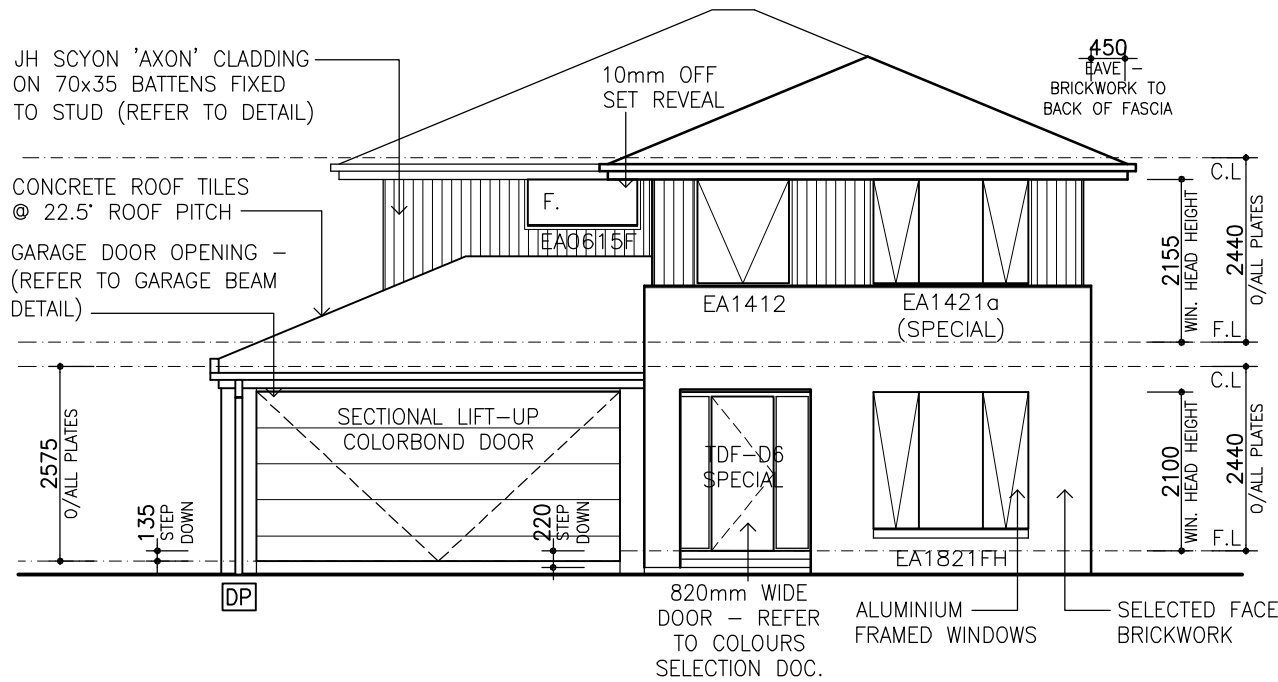


ELEVATION A

NOTE: FACE BRICKWORK ABOVE DOOR HEAD

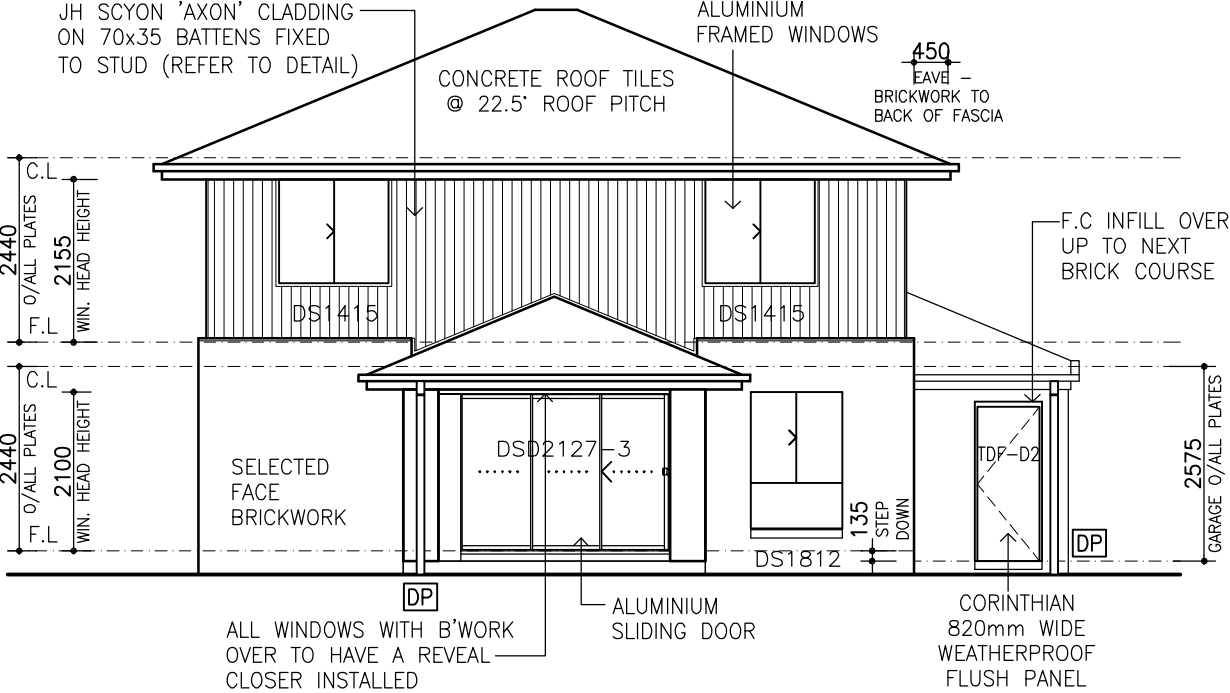

ELEVATION C

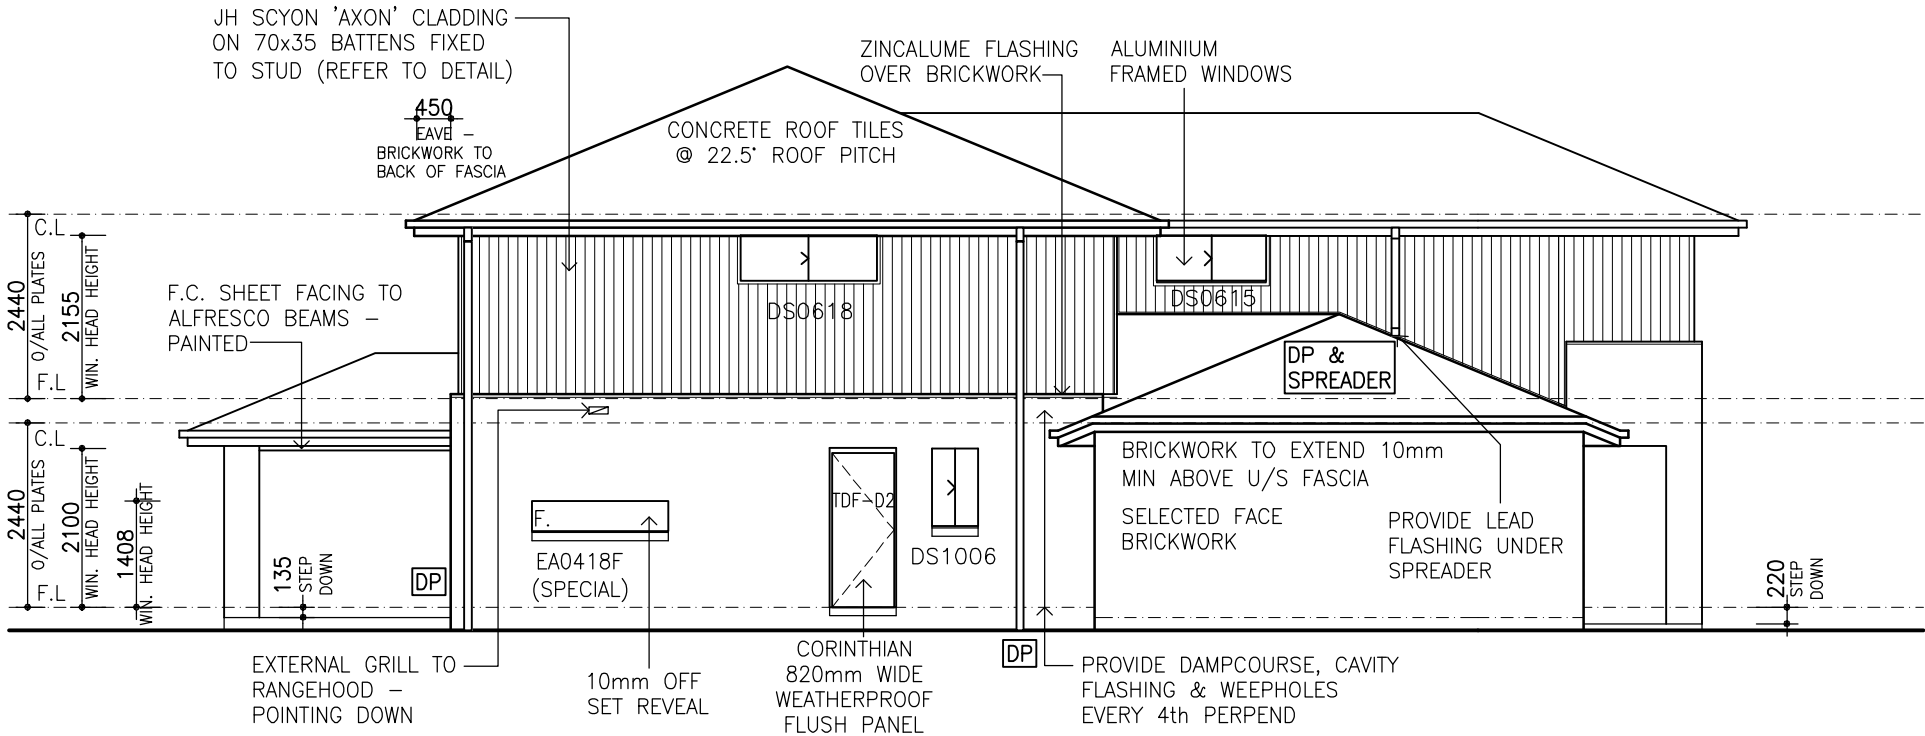

ELEVATION B

- LEGEND
- DENOTES SLIDING WINDOW
 - DENOTES AWNING WINDOW
 - DENOTES LOW-E GLAZING
 - DENOTES DOUBLE GLAZING
 - DENOTES DECOR SATIN GLAZING
 - DENOTES TRANSLUCENT GLAZING
- NOTE: ALL WINDOWS TO BE SET AT 2155mm O/A HEAD UNLESS NOMINATED OTHERWISE/IF BRICKWORK OVER, ADJUST HEAD HEIGHT TO WITHIN 5-10mm OF LINTEL
- NOTE: PROVIDE BACKFILL TO ALL EXTERNAL OPENINGS TO PROVIDE A 190mm MAX. STEP UP INTO HOUSE AS PER BCA REQUIREMENTS.
- NOTE: CONTROL JOINTS TO ENGINEERS RECOMMENDATIONS

SIMONDS OLD CONSTRUCTIONS P/L ACN 144 869 643 QBCC LICENCE NUMBER 1192095
HEAD OFFICE 3894 PACIFIC HIGHWAY, LOGANHOLME QLD 4129 INTERNET www.simonds.com.au
TELEPHONE (07) 3457 8000 ENQUIRIES Email: enquiries@simonds.com.au Ph: 1300 SIMONDS




Spec: SIMONDS HOMES RANGE (QLD)
(STANDARD)
- DEVELOPMENT DIVISION PURPOSE ONLY -
© COPYRIGHT 2003 SIMONDS IP Pty Ltd (ACN 144 839 805) (ABN 56 144 839 805)
NOT TO BE REPRODUCED IN PART OR WHOLE WITHOUT EXPRESS PERMISSION.

View: ELEVATIONS 1
Customer:
Address:

V1
Sheet No: 3.1


Scale: 1:100@A3
Date: 00.00.00

House: ARMSTRONG 32_298-14D
Facade: HARLEQUIN
Drawn: XNAMEX Job No: XX00000XX
Design: X00X Mastered: T.L. Checked: X00X

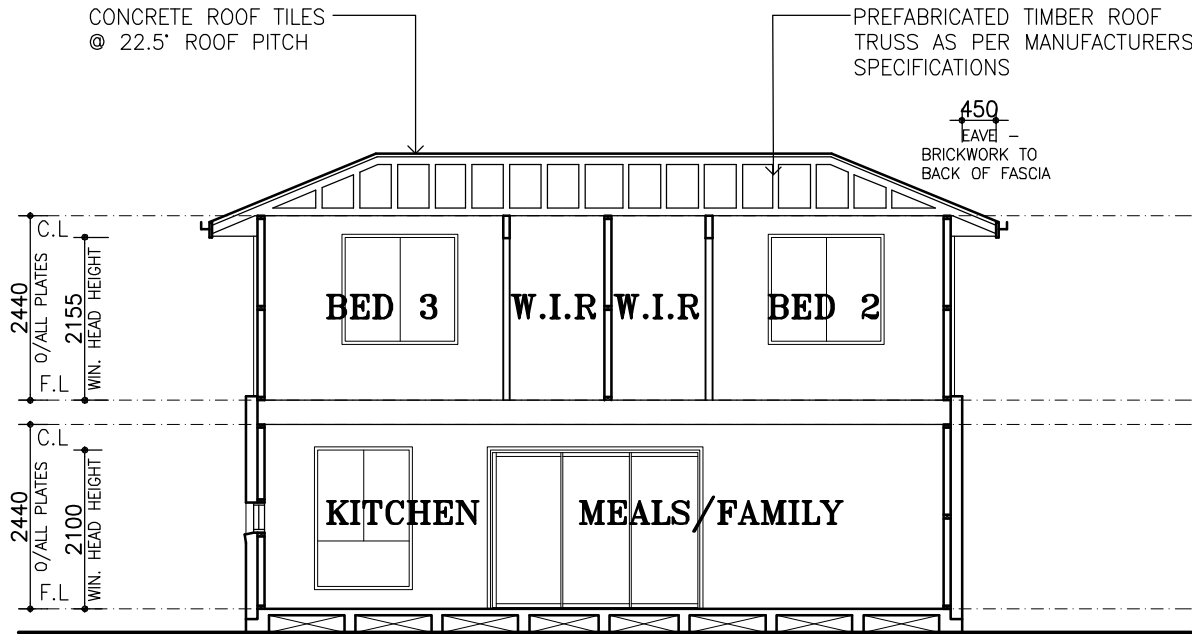

SEE ENGINEERS DETAIL FOR FLOOR SLAB CONSTRUCTION

SECTION A-A

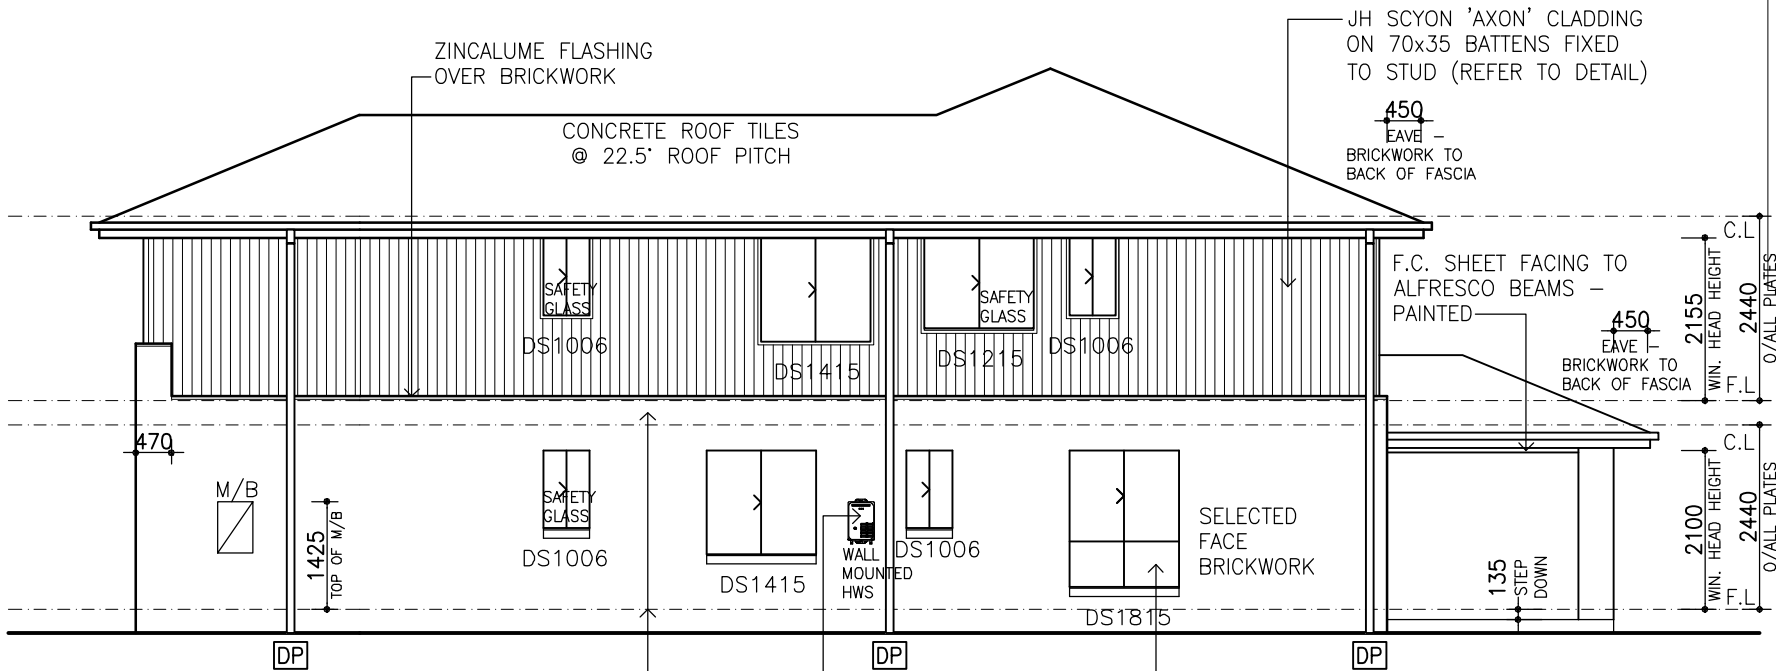

PROVIDE DAMPCOURSE, CAVITY FLASHING
& WEEPHOLES EVERY 4th PERPEND

NO IGNITION
SOURCES ALLOWED
IN THIS AREA

ALUMINIUM
FRAMED WINDOWS

ELEVATION D

ALL GLASS TO CONFORM WITH AS1288-2006 : GLASS IN BUILDINGS

STANDARD INCLUSIONS FOR ENERGY
EFFICIENCY REQUIREMENTS :

- SWEEP FANS TO ALL BEDROOMS
- ALUMINIUM IMPROVED WINDOWS THROUGHOUT
- STANDARD SISALATION WRAP TO EXTERIOR WALLS OF DWELLING
- R 2.5 GLASSWOOL BATTS TO CEILING SPACE (INCLUDING ALFRESCO)

FURTHER INCLUSIONS REQUIRED TO ACHIEVE 6 STAR ENERGY
RATING TO BE CONFIRMED UPON RECEIPT OF APPROVED
REPORT FROM ACCREDITED ENERGY RATER

NOTE:

PROVIDE SISALATION WRAP TO: EXTERNAL DWELLING
WALLS ONLY. PROVIDE INSULATION TO CEILING DIRECTLY
UNDER ROOF SPACE. EXCLUDES INSULATION TO GARAGE
CEILING SPACE, GARAGE EXTERNAL WALLS AND GROUND
FLOOR CEILING UNDER 1ST FLOOR OF DOUBLE STOREY
HOMES.

HEATING AND COOLING DUCTWORK

DUCTWORK FOR HEATING & COOLING SYSTEMS SHALL COMPLY WITH
A.S. 4254 & A.S./N.Z.S. 4859.1- IN ACCORDANCE WITH BCA TABLE
FOR CLIMATE ZONE REQUIREMENTS

N.B. DOUBLE STOREY HOUSE TYPES.

ALL WINDOWS TO BEDROOMS SHALL COMPLY WITH BCA CLAUSE 3.9.2.6.
AND THOSE ON THE FIRST FLOOR WILL BE PERMITTED TO OPEN NOT MORE
THAN 125mm

SLIP RESISTANCE FOR STAIRS & LANDINGS.

STAIRWAY TREADS SHALL HAVE:-

- A SURFACE FINISH OR COVERING WITH SLIP RESISTANCE
RATING IN ACCORDANCE WITH AS 4586 OR,
- NOSING STRIPS IN ACCORDANCE WITH AS 4586.

LANDINGS SHALL HAVE:-

- A FLOOR SURFACE WITH SLIP RESISTANCE RATING IN
ACCORDANCE WITH AS 4586 OR,
- A STRIP AT THE EDGE OF THE LANDING WITH SLIP
RESISTANCE RATING IN ACCORDANCE WITH AS 4586.

NOTE: ALL STRUCTURAL TIMBER SIZES TO BE IN
ACCORDANCE WITH AS1684 NATIONAL TIMBER FRAMING
CODE.

NOTE: ROOF TRUSSES TO MANUFACTURERS DESIGN &
SPECIFICATION.

NOTE: REFER TO ALL ENGINEERS DETAILS FOR
STRUCTURAL MEMBERS.

NOTE: ALL WINDOWS TO BE SET AT 2155mm O/A
HEAD UNLESS NOMINATED OTHERWISE/IF
BRICKWORK OVER, ADJUST HEAD HEIGHT TO WITHIN
5-10mm OF UNTEL.

NOTE: DIMENSIONS TO STRUCTURAL TIMBERS AND FACE
OF BRICKS EXCLUDING BATTENS, PLASTERBOARD, ETC.

NOTE: WRITTEN DIMENSIONS TAKE PRECEDENCE OVER
SCALE - UNLESS OTHERWISE INDICATED ALL WALL
DIMENSIONS, EXTERNAL 240mm B/VENEER -INTERNAL
90mm TIMBER STUD.

NOTE: STEPS/STAIRS TREADS MIN 240mm RISERS MAX
190mm HANDRAILS & BALUSTRADE 1000mm MIN HIGH
BALUSTERS MAX 125mm SPACING.

NOTE: NOMINATED THICKNESS AND SIZE OF MATERIALS
IS INDICATIVE ONLY AND MAY BE VARIED - BUT NOT
REDUCED - AT THE DISCRETION OF SIMONDS HOMES.

NOTE: FINISHED CEILING HEIGHT IS SUBJECT TO CEILING
BATTENS (WHERE APPLICABLE), CEILING LINING AND
FLOOR FINISH.

NOTE: PROVIDE BACKFILL TO ALL EXTERNAL OPENINGS
TO PROVIDE A 190mm MAX. STEP UP INTO HOUSE AS
PER BCA REQUIREMENTS.

NOTE: PROVIDE COMPACTED BACKFILL MIN 1.0m WIDE
WITH MIN. 50mm FALL AWAY FROM PERIMETER OF
FLOOR SLAB

NOTE: SOLAR COLLECTOR PANELS ROOF LOCATION IS
INDICATIVE ONLY, LOCATION & SIZE IS DEPENDANT ON
FINAL SITE ORIENTATION & TO MANUFACTURER'S
RECOMMENDATION.

NOTE: INSTANTANEOUS HWS LOCATION SHOWN ON PLAN
IS INDICATIVE ONLY AND IS SUBJECT TO SITE
CONDITIONS.

NOTE: DOOR PULL HANDLES TO BE SET AT 55mm
FROM THE EDGE OF DOOR.

NOTE: LIFT-OFF HINGES TO W.C. DOOR UNLESS
DISTANCE TO PAN 1.2m OR GREATER.

NOTE: MANHOLE (MH) POSITION SHOWN ON PLAN IS
INDICATIVE ONLY & IS SUBJECT TO LOCATION OF
STRUCTURAL FRAMING.

NOTE: DAMPCOURSE WITH WEEPHOLES & CAVITY
FLASHINGS IN ACCORDANCE WITH AS 4773.2-2015

NOTE: ALL PLIABLE MEMBRANES INSTALLED TO
COMPLY AND BE IN ACCORDANCE WITH NCC CLAUSE
3.8.7.2, AS 4200.1 & AS 4200.2

NOTE: CONDENSATION MANAGEMENT AS PER CLAUSE
3.8.7.3 OF NCC 2019. EXHAUST FROM BATHROOM,
SANITARY COMPARTMENT OR LAUNDRY MUST BE
DISCHARGED DIRECTLY VIA A SHAFT OR DUCT TO
OUTDOOR AIR.



DENOTES LOW-E GLAZING



DENOTES DOUBLE GLAZING



DENOTES DECOR SATIN GLAZING



DENOTES TRANSLUCENT GLAZING

SIMONDS QLD CONSTRUCTIONS P/L ACN 144 869 643 QBCC LICENCE NUMBER 1192095
HEAD OFFICE 3894 PACIFIC HIGHWAY, LOGANHOLME QLD 4129 INTERNET www.simonds.com.au
TELEPHONE (07) 3457 8000 ENQUIRIES Email: enquiries@simonds.com.au Ph: 1300 SIMONDS

SIMONDS

Spec:

SIMONDS HOMES RANGE (QLD)

(STANDARD)

- DEVELOPMENT DIVISION PURPOSE ONLY -

© COPYRIGHT 2003 SIMONDS IP Pty Ltd (ACN 144 839 805) (ABN 56 144 839 805)
NOT TO BE REPRODUCED IN PART OR WHOLE WITHOUT EXPRESS PERMISSION.

View:

ELEVATIONS 2

Customer:

Address:

V1

Sheet No:
3.2

Scale: 1:100@A3
Date: 00.00.00

House:

ARMSTRONG 32_298-14D

Facade:

HARLEQUIN

Drawn:

XNAMEX

Job No:

XX000000XX

Design:


X00X

Mastered:

T.L

Checked:

X00X

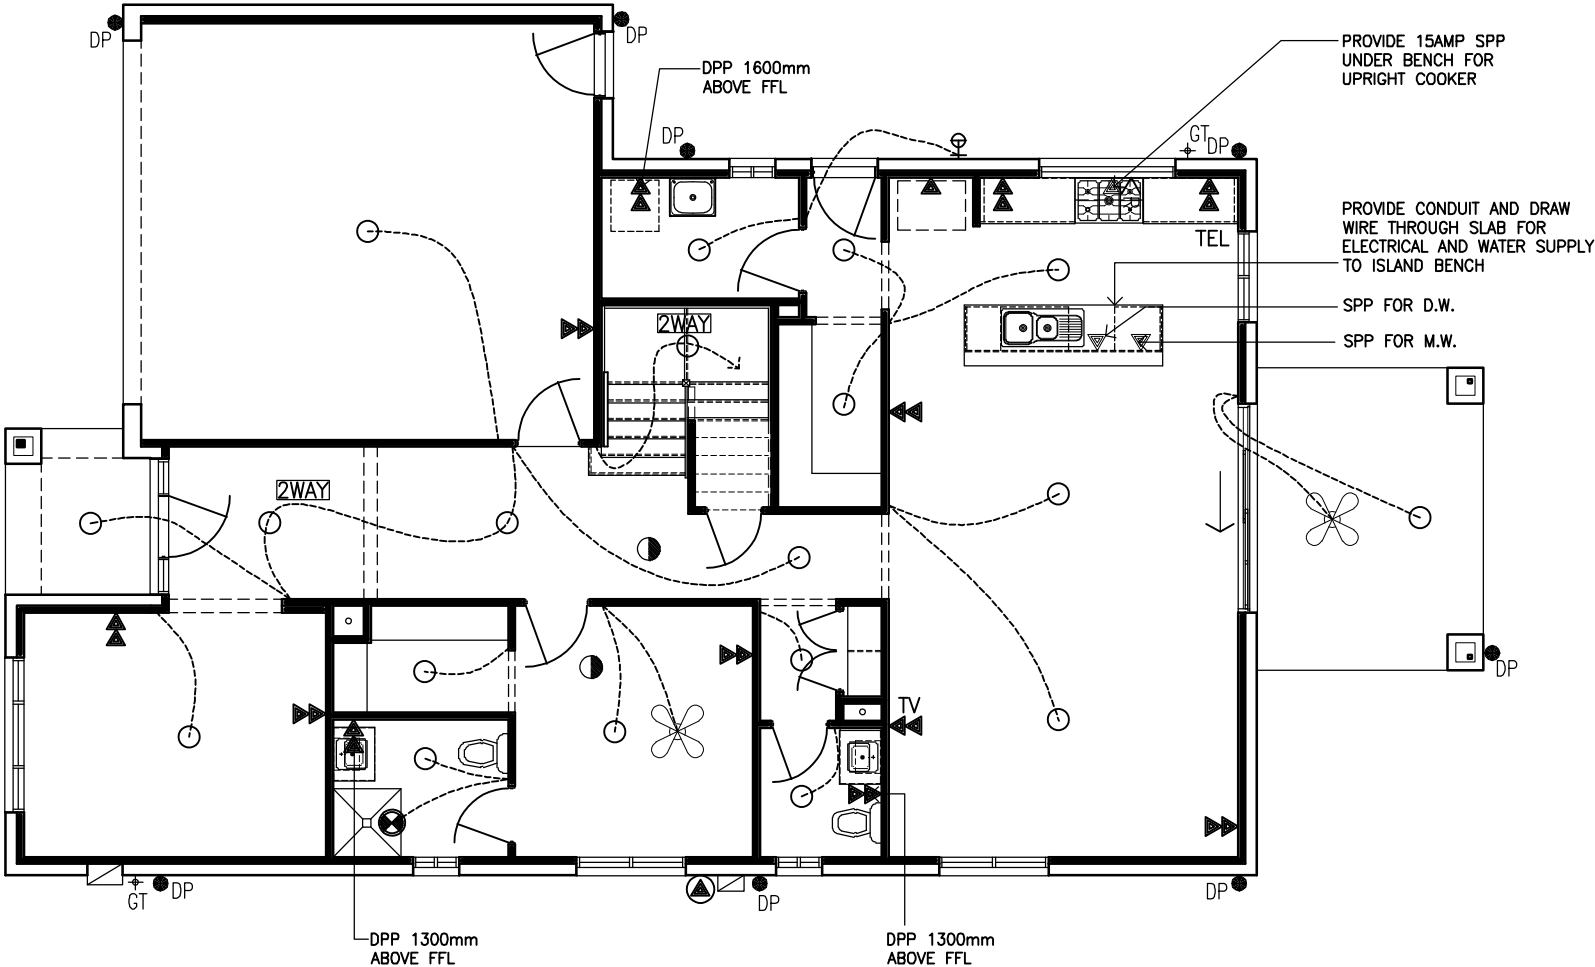

ELECTRICAL LEGEND (QLD)

- - ___ LIGHT POINT
- - ___ DOWNLIGHT POINT
- ◇ - ___ DARWIN HUB
- ⊞ - ___ WALL MOUNTED INTERNAL LIGHT POINT
- ⊕ - ___ WALL MOUNTED EXTERNAL LIGHT POINT
- - ___ FLUORESCENT LIGHT POINT
- ⦿ - ___ DARWIN CIRCADIAN DOWNLIGHT
- - ___ DOWNLIGHT POINT
- ALTERNATIVE GLOBE
- - ___ TRACK LIGHTING
- ⬆ - ___ POWER POINT WITH GREEN SWITCH
- ▲ - ___ SINGLE POWER POINT (SPP)
- ▲▲ - ___ DOUBLE POWER POINT (DPP)
PPs and TV points in living areas, bedrooms, and
passageway to be 300mm A.F.L. and 150mm above all
benchtops unless noted otherwise. Telephone point on wall
1500mm A.F.L, PPs to garage to be 1100mm A.F.L.
- - ___ DATA POINT
- <OV - ___ OVEN DOUBLE POLE ISOLATION SWITCH to kitchen
splashback
- <R - ___ RANGEHOOD POWER SOCKET
- ⦿ - ___ EXTERNAL WEATHERPROOF SINGLE POWER POINT
- ⦿⦿ - ___ EXTERNAL WEATHERPROOF DOUBLE POWER POINT
- - ___ SMOKE DETECTOR – INTERLINKED TO COMPLY WITH
NCC & AS 3786 1993)
- ⦿ - ___ EXHAUST FAN
- TV - ___ TELEVISION POINT
- TEL - ___ TELEPHONE POINT
- ⌚ - ___ DIMMER SWITCH
- Ⓥ - ___ DUCTED VACUUM POINT
- 👁 - ___ FLOODLIGHT WITH SENSOR
- ⦿⦿ - ___ IXL TASTIC UNIT
- ⦿ - ___ SWEEP FAN
- ⦿ - ___ DUCTED HEATING ROUND CEILING REGISTER.
- HEAT - ___ DUCTED HEATING UNIT + POWER POINT & LIGHT
- ⦿ - ___ EVAPORATIVE COOLING CEILING REGISTER
- COOLING UNIT - ___ EVAPORATIVE COOLING UNIT + POWER POINT

NOTE:

- NOTE: LIGHT SWITCHES LOCATED TO BE 1100mm (1300mm TO WET AREAS) ABOVE FLOOR LEVEL – UNLESS NOTED OTHERWISE
- FIRE RATED DUCTWORK TO DUCTED HEATING TO CONFORM WITH NEW STATE GOVERNMENT LEGISLATION
- EXTERNALLY DUCT GROUND FLOOR RANGEHOOD THROUGH FIRST FLOOR SPACE – FOR DOUBLE STOREY ONLY
- EXTERNALLY DUCT EXHAUST FANS THROUGH ROOF & OR FIRST FLOOR SPACE AS REQUIRED
- OUTLET & EXHAUST FAN POSITIONS ARE APPROXIMATE ONLY
- SWITCH FOR ROOF SPACE LIGHT TO BE WITHIN 900MM OF MANHOLE
- WHERE POSSIBLE LIGHT POINTS IN ROOF SPACE SHALL NOT BE CLOSER THAN 1800MM ABOVE PLATFORM
- EXTERNAL WEATHERPROOF POWER SUPPLY FOR REVERSE CYCLE COOLING UNITS SHOULD BE ON AN ISOLATED SWITCH.


SIMONDS QLD CONSTRUCTIONS P/L ACN 144 869 643 QBCC LICENCE NUMBER 1192095
HEAD OFFICE 3894 PACIFIC HIGHWAY, LOGANHOLME QLD 4129 INTERNET www.simonds.com.au
TELEPHONE (07) 3457 8000 ENQUIRIES Email: enquiries@simonds.com.au Ph: 1300 SIMONDS



Spec: SIMONDS HOMES RANGE (QLD)
(STANDARD)
– DEVELOPMENT DIVISION PURPOSE ONLY –
© COPYRIGHT 2003 SIMONDS IP Pty Ltd (ACN 144 839 805) (ABN 56 144 839 805)
NOT TO BE REPRODUCED IN PART OR WHOLE WITHOUT EXPRESS PERMISSION.

View: ELECTRICAL GROUND FLOOR PLAN
Customer:
Address:

V1	Scale: 1:100@A3	Date: 00.00.00	House: ARMSTRONG 32_298–14D		
			Facade: HARLEQUIN		
			Drawn: XNAMEX	Job No: XX000000XX	
			Design: X00X	Mastered: T.L	Checked: X00X

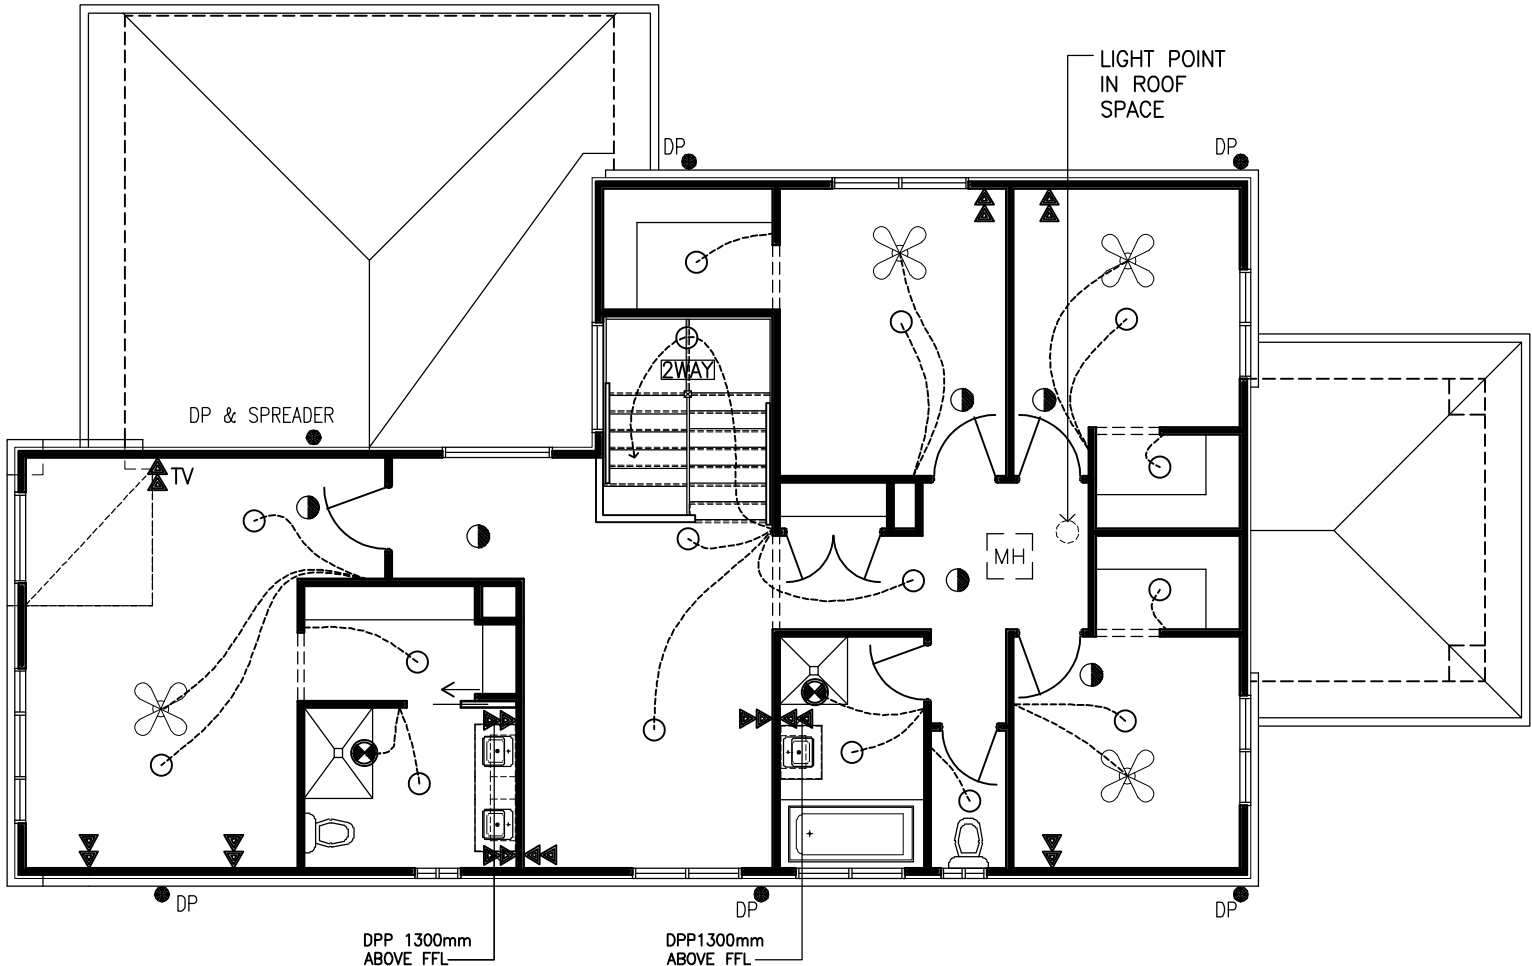

ELECTRICAL LEGEND (QLD)

- - ___ LIGHT POINT
- - ___ DOWNLIGHT POINT
- ◇ - ___ DARWIN HUB
- ⊞ - ___ WALL MOUNTED INTERNAL LIGHT POINT
- ⊕ - ___ WALL MOUNTED EXTERNAL LIGHT POINT
- - ___ FLUORESCENT LIGHT POINT
- - ___ DARWIN CIRCADIAN DOWNLIGHT
- - ___ DOWNLIGHT POINT
- ALTERNATIVE GLOBE
- - ___ TRACK LIGHTING
- ⬆ - ___ POWER POINT WITH GREEN SWITCH
- ▲ - ___ SINGLE POWER POINT (SPP)
- ▲▲ - ___ DOUBLE POWER POINT (DPP)
PPs and TV points in living areas, bedrooms, and
passageway to be 300mm A.F.L. and 150mm above all
benchtops unless noted otherwise. Telephone point on wall
1500mm A.F.L, PPs to garage to be 1100mm A.F.L.
- - ___ DATA POINT
- <OV- ___ OVEN DOUBLE POLE ISOLATION SWITCH to kitchen
splashback
- <R - ___ RANGEHOOD POWER SOCKET
- ⦿ - ___ EXTERNAL WEATHERPROOF SINGLE POWER POINT
- ⦿⦿ - ___ EXTERNAL WEATHERPROOF DOUBLE POWER POINT
- - ___ SMOKE DETECTOR – INTERLINKED TO COMPLY WITH
NCC & AS 3786 1993)
- ⊗ - ___ EXHAUST FAN
- TV - ___ TELEVISION POINT
- TEL - ___ TELEPHONE POINT
- ⚡ - ___ DIMMER SWITCH
- Ⓥ - ___ DUCTED VACUUM POINT
- 🔦 - ___ FLOODLIGHT WITH SENSOR
- ⊞⊞ - ___ IXL TASTIC UNIT
- ⊞ - ___ SWEEP FAN
- ⊕ - ___ DUCTED HEATING ROUND CEILING REGISTER.
- HEAT - ___ DUCTED HEATING UNIT + POWER POINT & LIGHT
- ⊞⊞ - ___ EVAPORATIVE COOLING CEILING REGISTER
- COOLING UNIT - ___ EVAPORATIVE COOLING UNIT + POWER POINT

- NOTE:
- NOTE: LIGHT SWITCHES LOCATED TO BE 1100mm (1300mm TO WET AREAS) ABOVE FLOOR LEVEL – UNLESS NOTED OTHERWISE
 - FIRE RATED DUCTWORK TO DUCTED HEATING TO CONFORM WITH NEW STATE GOVERNMENT LEGISLATION
 - EXTERNALLY DUCT GROUND FLOOR RANGEHOOD THROUGH FIRST FLOOR SPACE – FOR DOUBLE STOREY ONLY
 - EXTERNALLY DUCT EXHAUST FANS THROUGH ROOF & OR FIRST FLOOR SPACE AS REQUIRED
 - OUTLET & EXHAUST FAN POSITIONS ARE APPROXIMATE ONLY
 - SWITCH FOR ROOF SPACE LIGHT TO BE WITHIN 900MM OF MANHOLE
 - WHERE POSSIBLE LIGHT POINTS IN ROOF SPACE SHALL NOT BE CLOSER THAN 1800MM ABOVE PLATFORM
 - EXTERNAL WEATHERPROOF POWER SUPPLY FOR REVERSE CYCLE COOLING UNITS SHOULD BE ON AN ISOLATED SWITCH.


SIMONDS QLD CONSTRUCTIONS P/L ACN 144 869 643 QBCC LICENCE NUMBER 1192095
HEAD OFFICE 3894 PACIFIC HIGHWAY, LOGANHOLME QLD 4129 INTERNET www.simonds.com.au
TELEPHONE (07) 3457 8000 ENQUIRIES Email: enquiries@simonds.com.au Ph: 1300 SIMONDS



Spec: SIMONDS HOMES RANGE (QLD)
(STANDARD)
– DEVELOPMENT DIVISION PURPOSE ONLY –
© COPYRIGHT 2003 SIMONDS IP Pty Ltd (ACN 144 839 805) (ABN 56 144 839 805)
NOT TO BE REPRODUCED IN PART OR WHOLE WITHOUT EXPRESS PERMISSION.


View: ELECTRICAL FIRST FLOOR PLAN
Customer:
Address:

V1	Scale: 1:100@A3	Date: 00.00.00	House: ARMSTRONG 32_298–14D		
			Facade: HARLEQUIN		
			Drawn: XNAMEX	Job No: XX000000XX	
			Design: X00X	Mastered: T.L	Checked: X00X

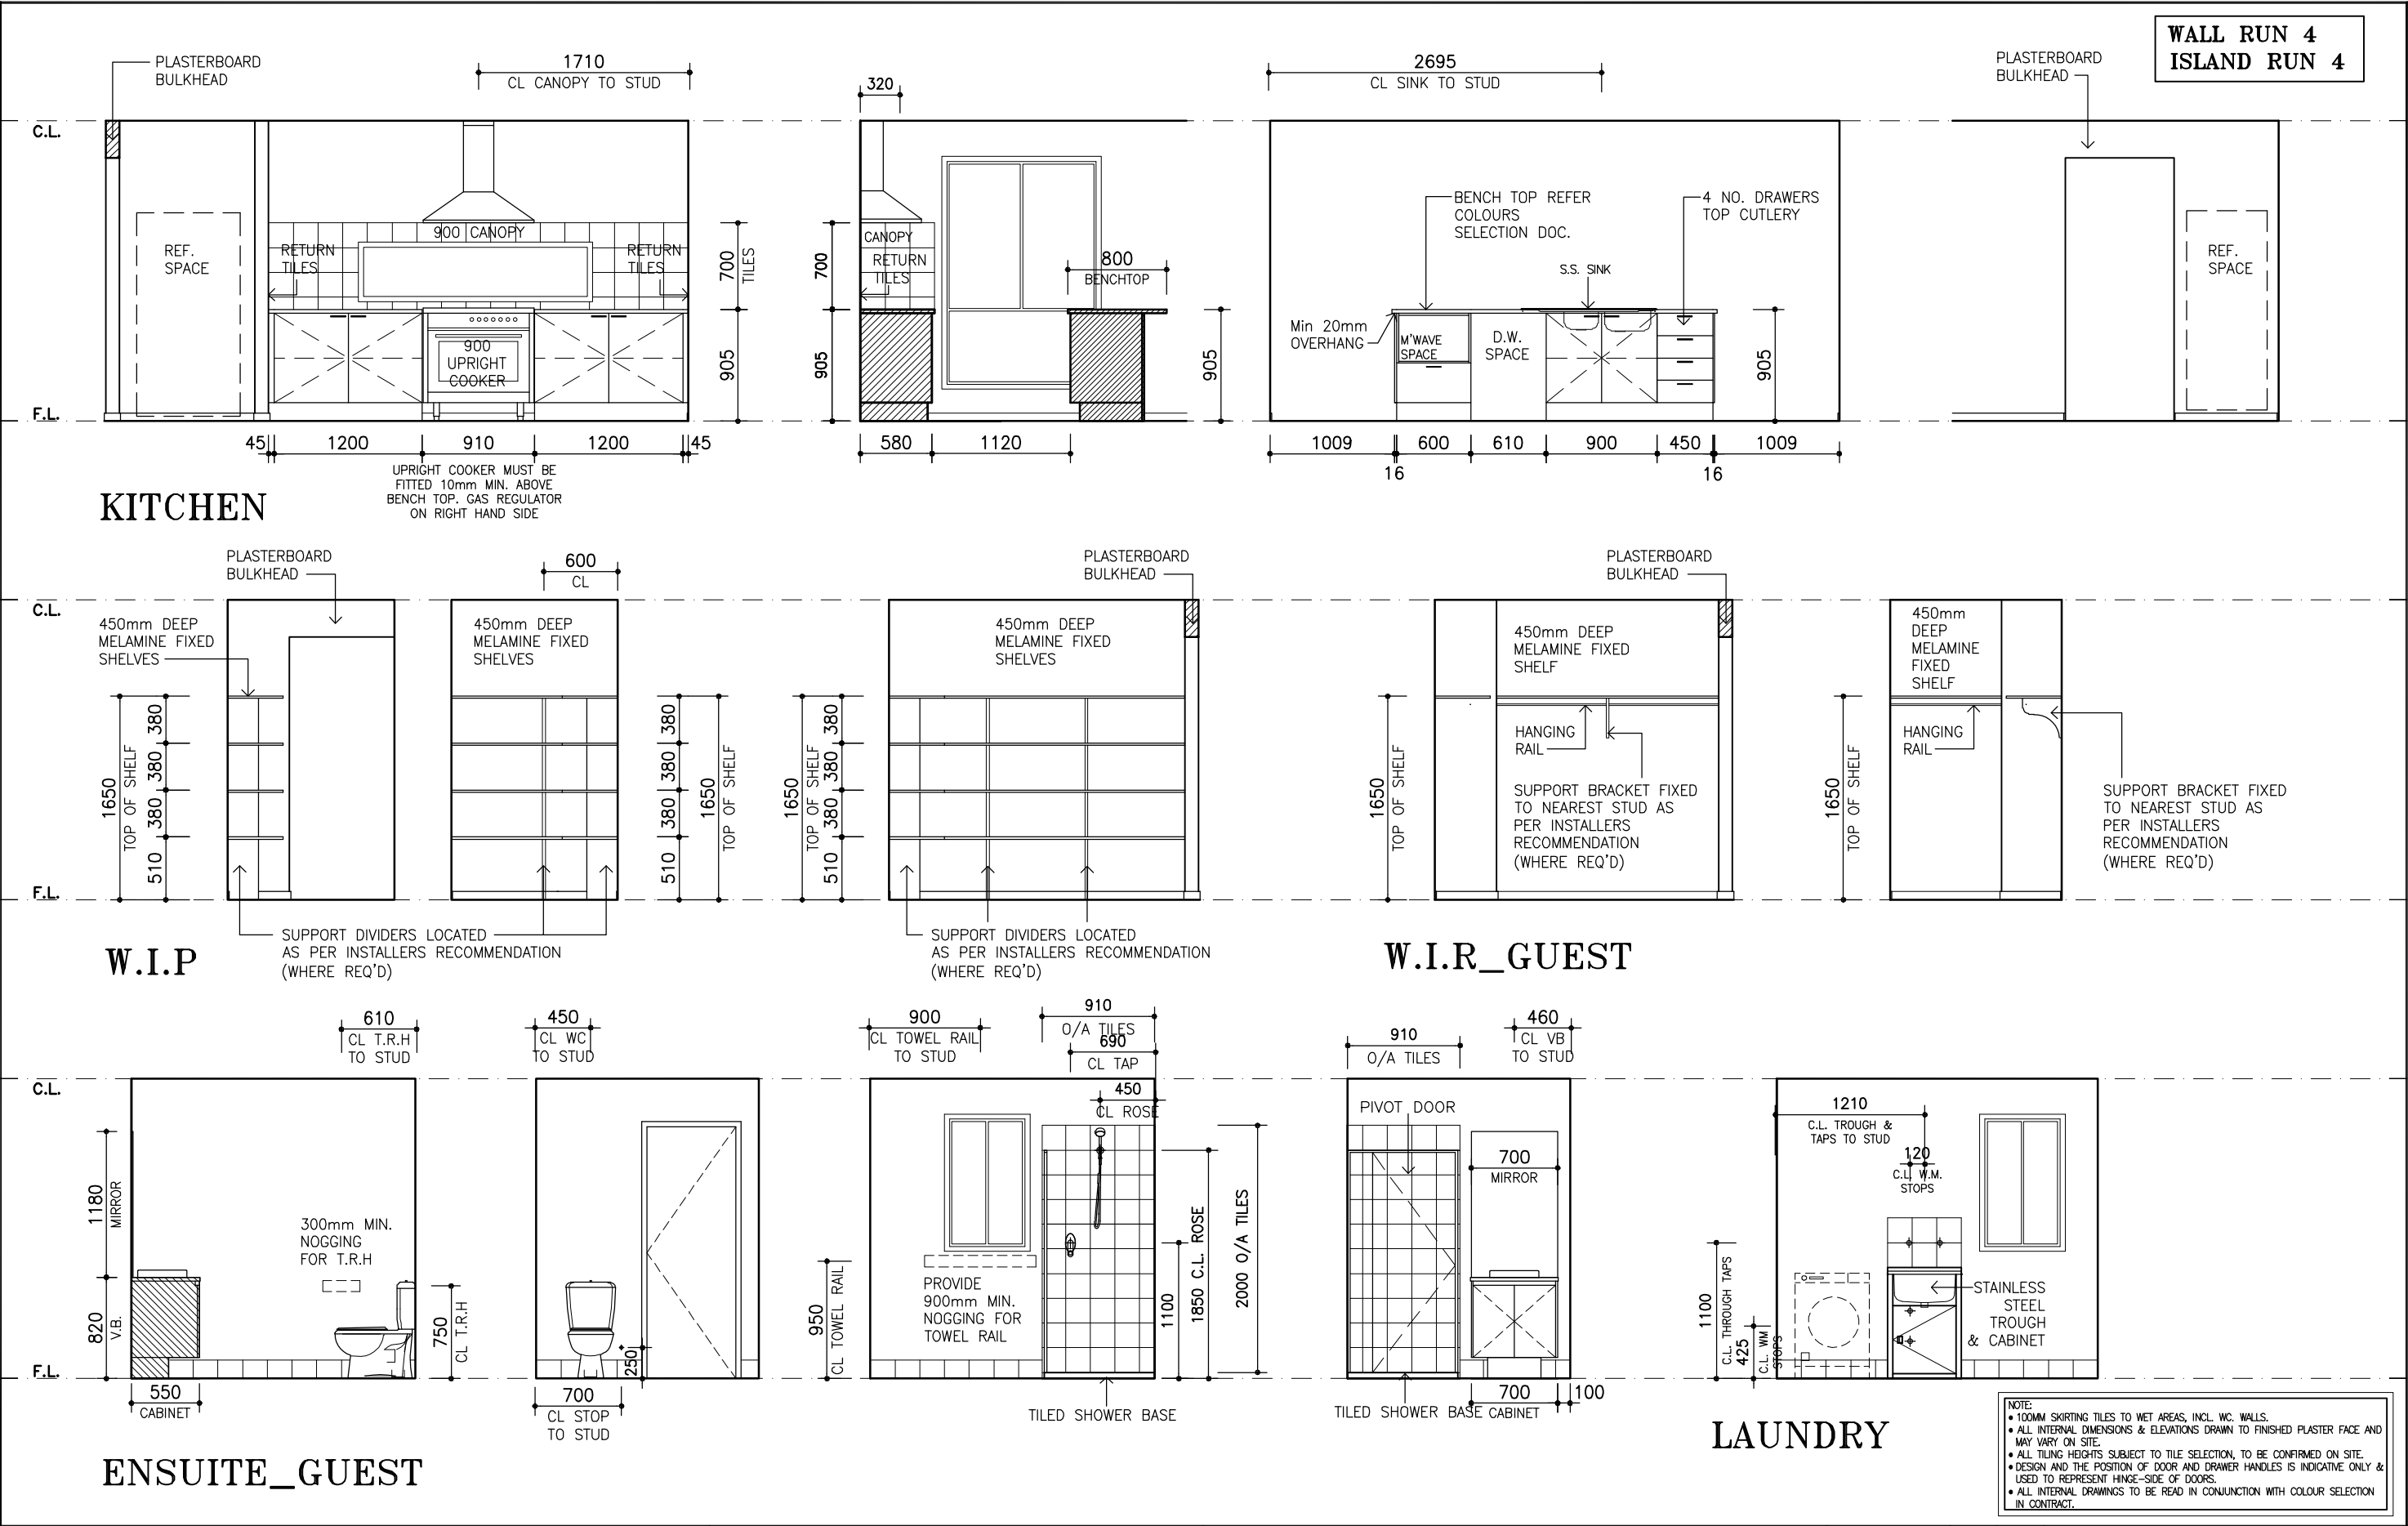


SIMONDS QLD CONSTRUCTIONS P/L ACN 144 869 643 QBCC LICENCE NUMBER 1192095 HEAD OFFICE 3894 PACIFIC HIGHWAY, LOGANHOLME QLD 4129 INTERNET www.simonds.com.au TELEPHONE (07) 3457 8000 ENQUIRIES Email: enquiries@simonds.com.au Ph: 1300 SIMONDS SIMONDS	Spec: SIMONDS HOMES RANGE (QLD) (STANDARD) – DEVELOPMENT DIVISION PURPOSE ONLY –  COPYRIGHT 2003 SIMONDS IP Pty Ltd (ACN 144 839 805) (ABN 56 144 839 805) NOT TO BE REPRODUCED IN PART OR WHOLE WITHOUT EXPRESS PERMISSION.	View: INTERNAL ELEVATIONS 1 Customer: Address:	V1 Sheet No: 8.1	Scale: 1:50@A3 Date: 00.00.00	House: ARMSTRONG 32_298–14D Facade: HARLEQUIN Drawn: XNAMEX Job No: XX00000XX Design: X00X Mastered: T.L Checked: X00X
--	---	---	--	---	--

WC

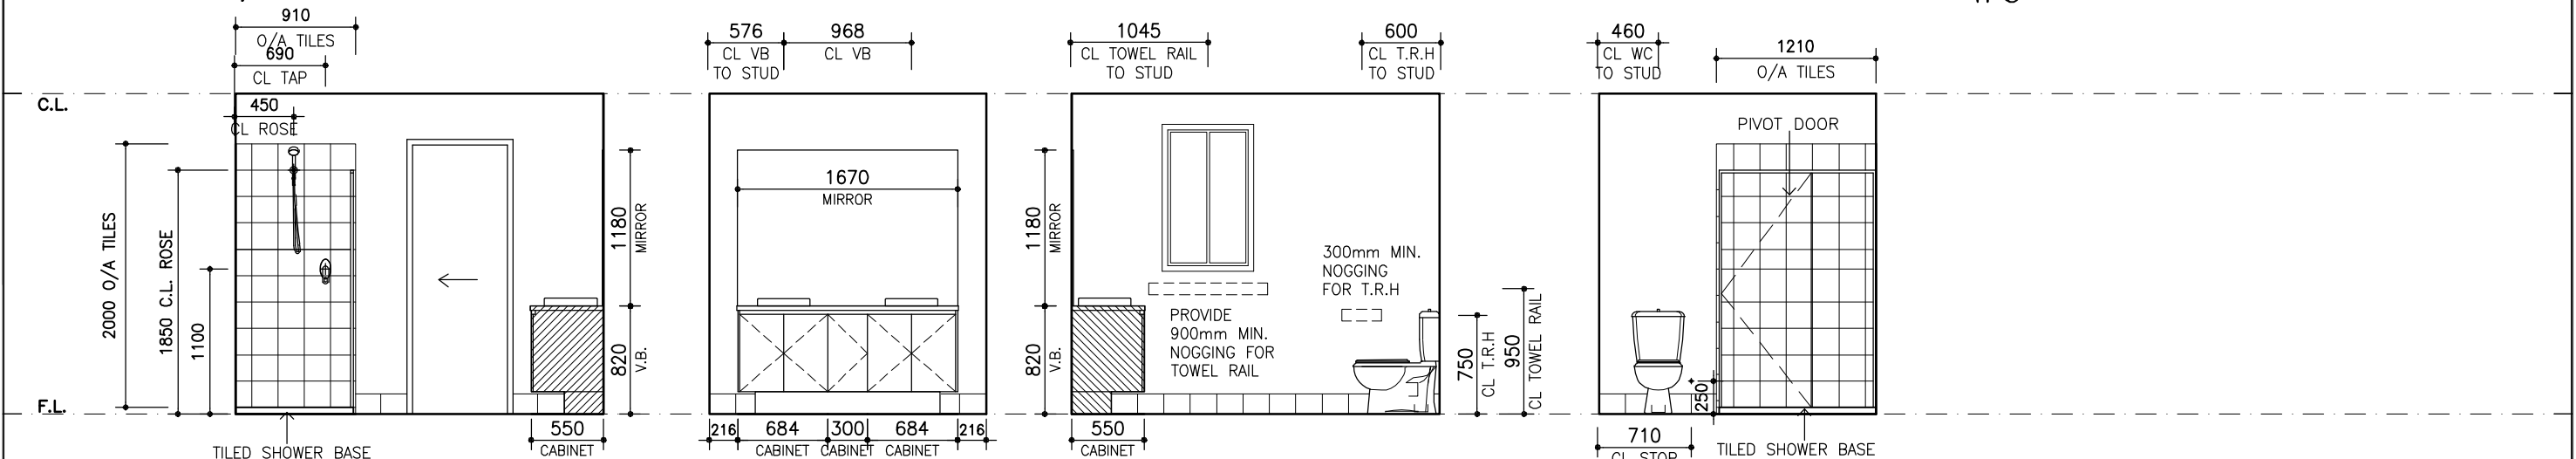

ENSUITE_MASTER

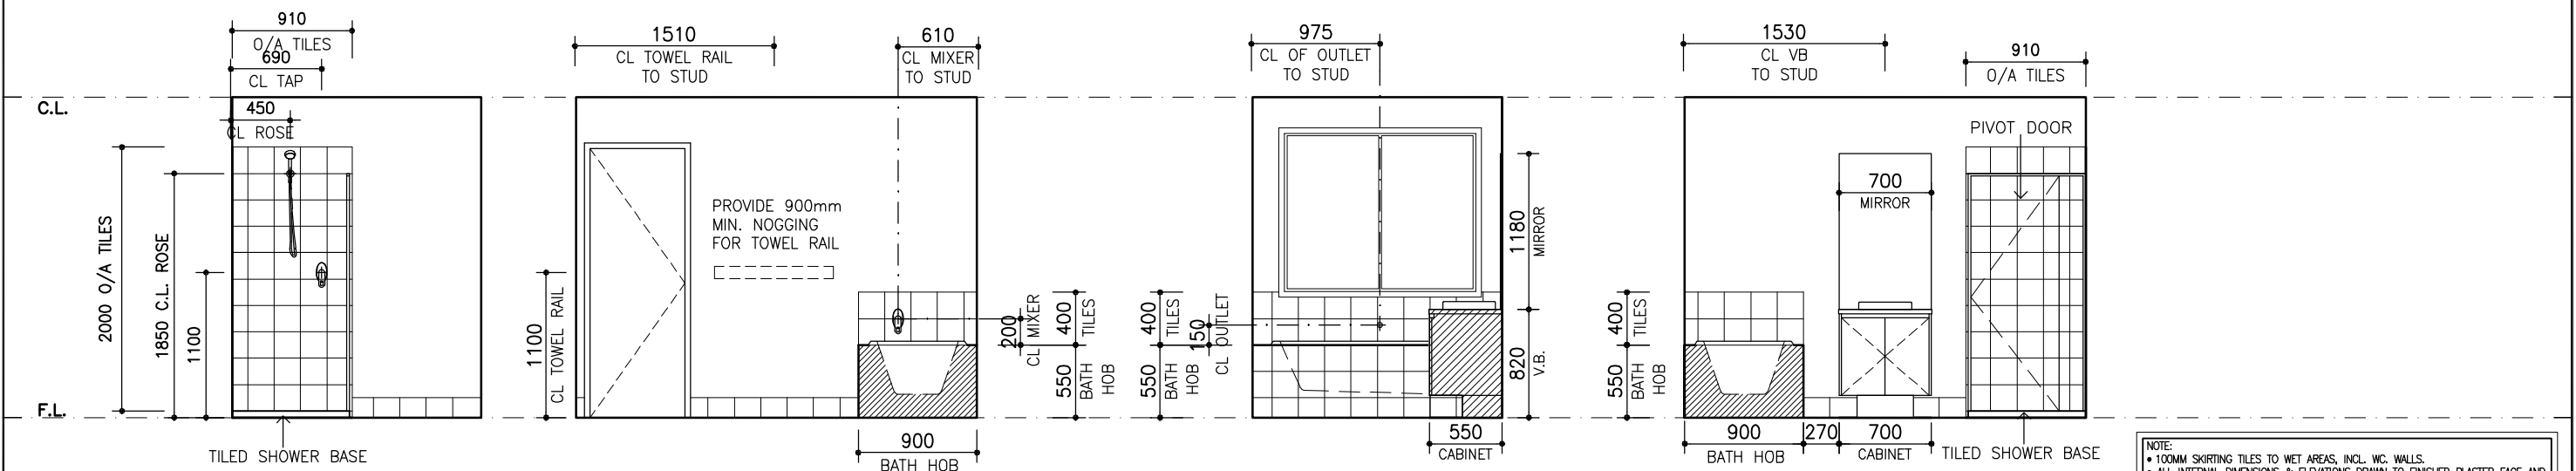

BATH

NOTE:

- 100MM SKIRTING TILES TO WET AREAS, INCL. WC. WALLS.
- ALL INTERNAL DIMENSIONS & ELEVATIONS DRAWN TO FINISHED PLASTER FACE AND MAY VARY ON SITE.
- ALL TILING HEIGHTS SUBJECT TO TILE SELECTION, TO BE CONFIRMED ON SITE.
- DESIGN AND THE POSITION OF DOOR AND DRAWER HANDLES IS INDICATIVE ONLY & USED TO REPRESENT HINGE-SIDE OF DOORS.
- ALL INTERNAL DRAWINGS TO BE READ IN CONJUNCTION WITH COLOUR SELECTION IN CONTRACT.

Ph: 1300 SIMONDS

SIMONDS

Spec: **SIMONDS HOMES RANGE (QLD)**
(STANDARD)
— DEVELOPMENT DIVISION PURPOSE ONLY —


© COPYRIGHT 2003 SIMONDS IP Pty Ltd (ACN 144 839 805) (ABN 56 144 839 805)
NOT TO BE REPRODUCED IN PART OR WHOLE WITHOUT EXPRESS PERMISSION.

View:	INTERNAL ELEVATIONS 2
Customer:	
Address:	

V1
Sheet No:
8.2

Scale: 1:50@A3

00000000	House: ARMSTRONG 32_298-14D		
	Facade: HARLEQUIN		
	Drawn: XNAMEX	Job No: XX000000XX	
	Design: X00X	Mastered: TJ	Checked: X00X

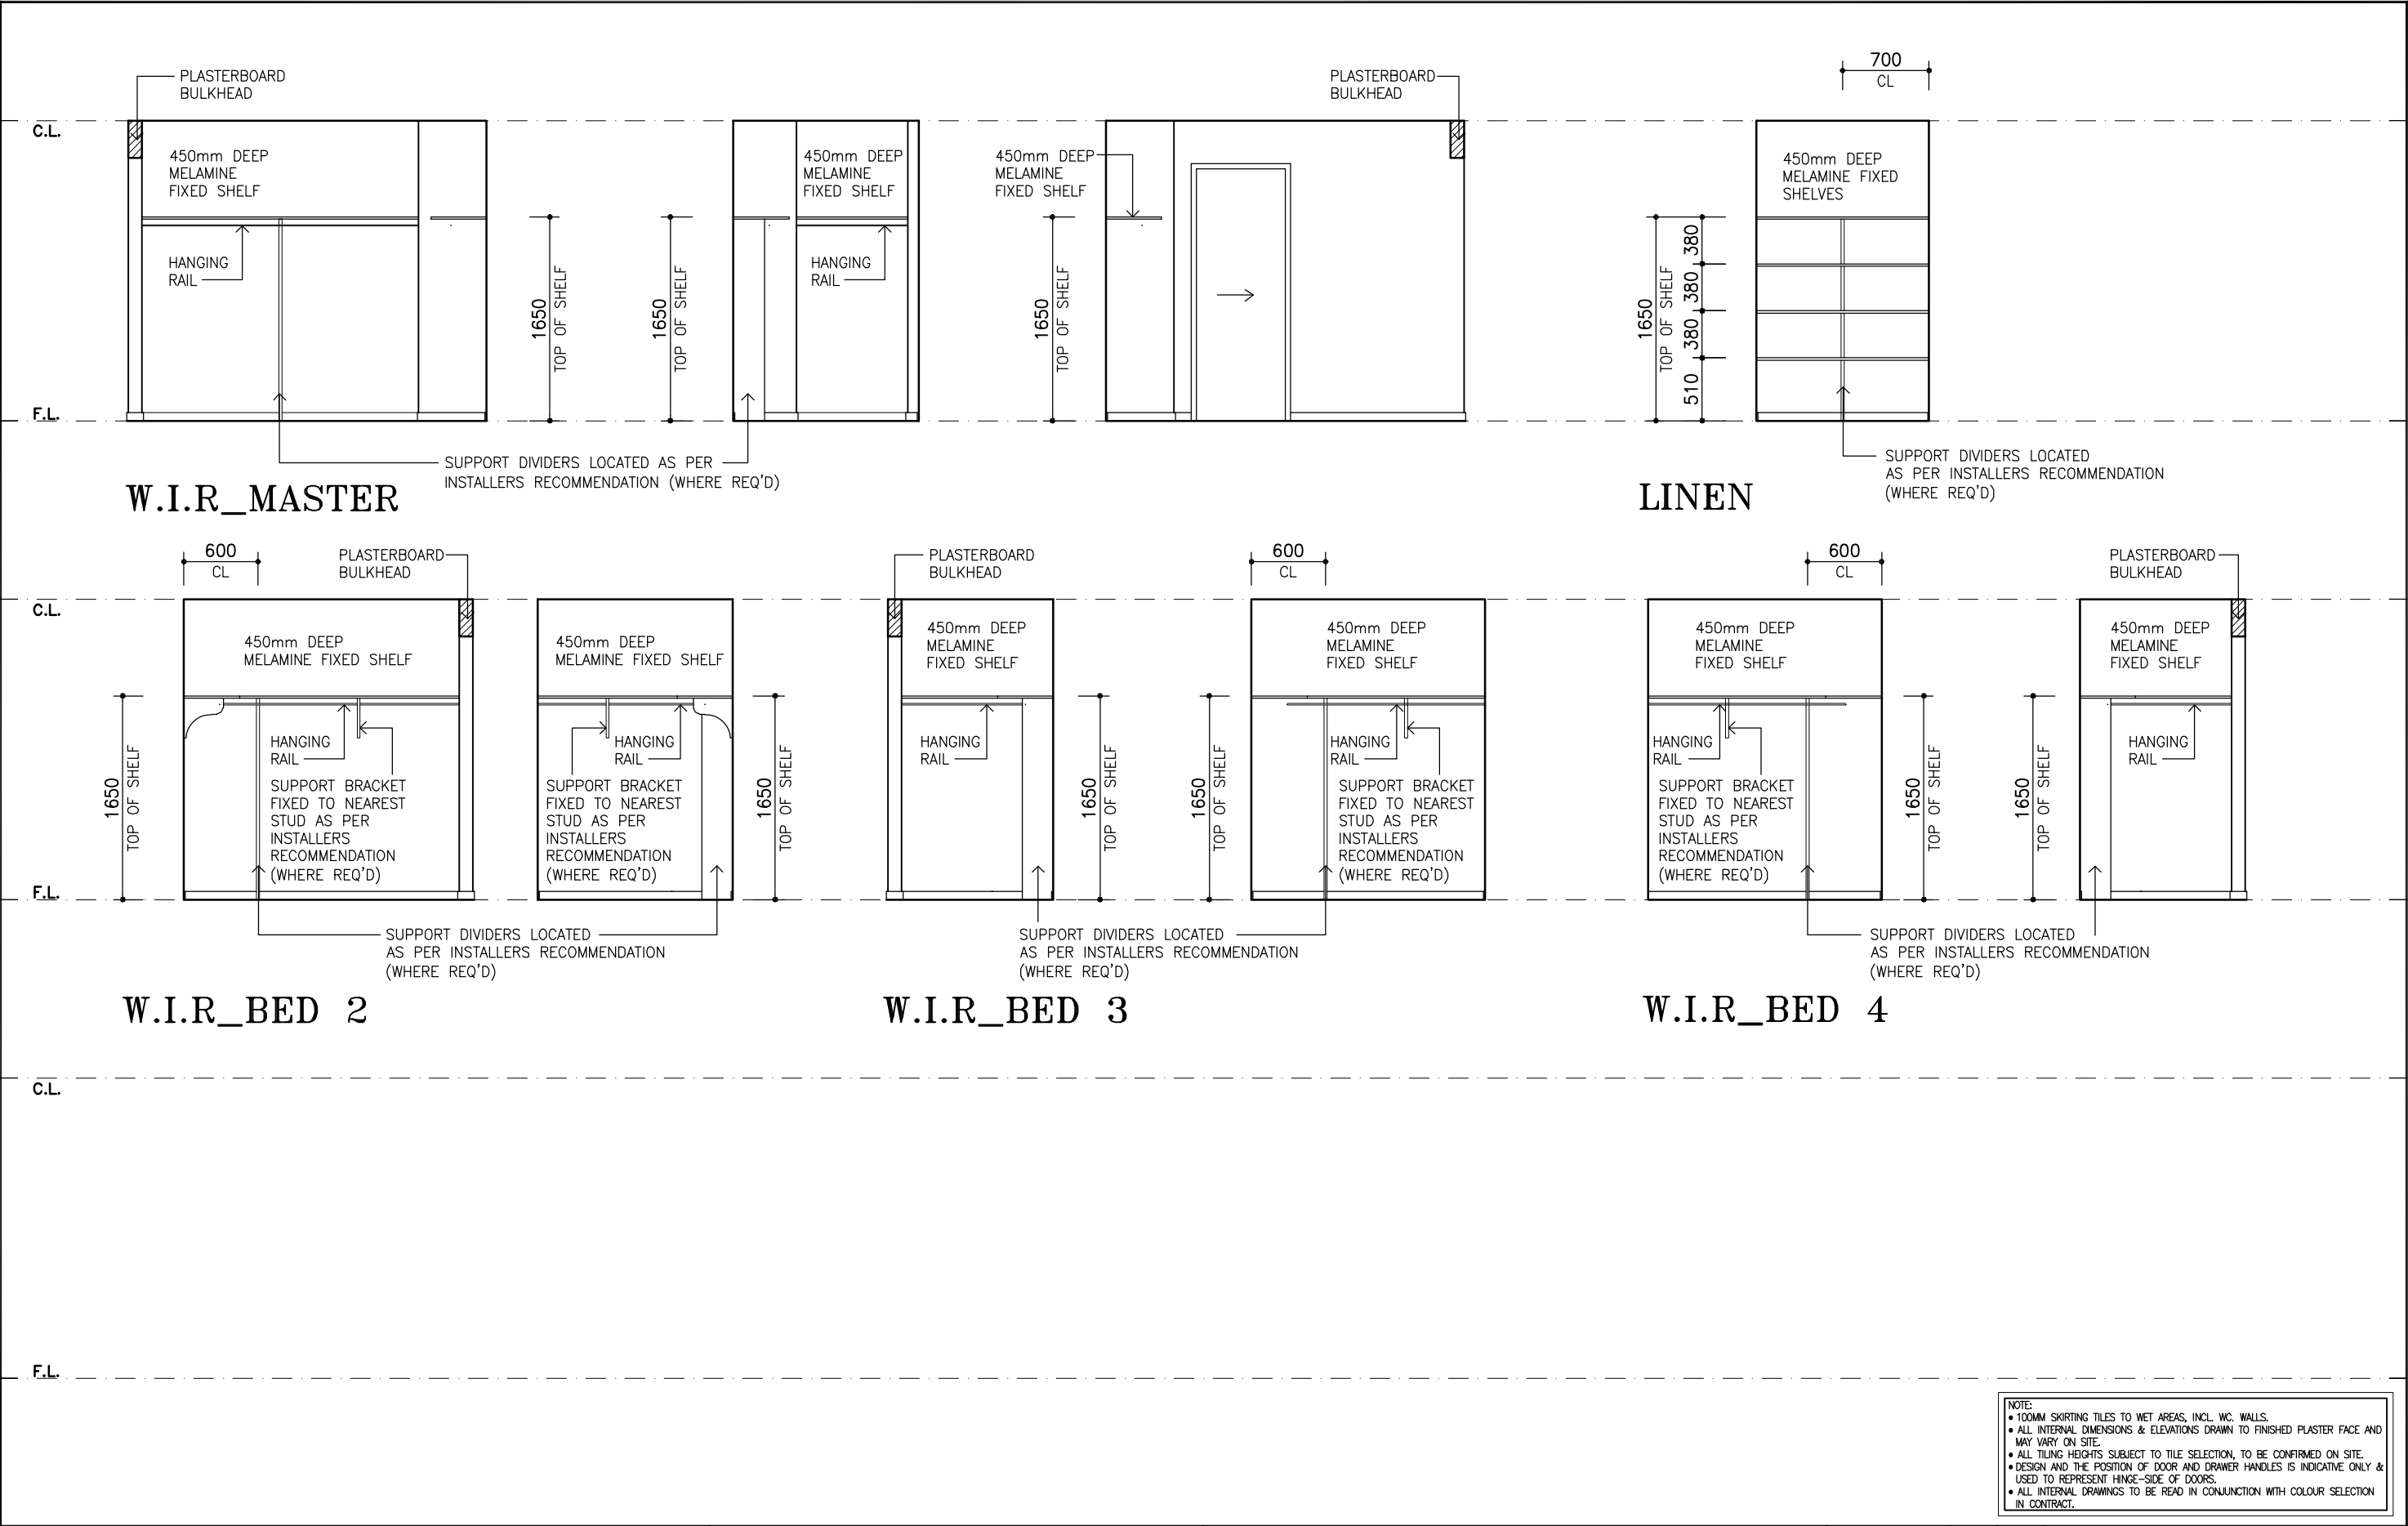

SIMONDS QLD CONSTRUCTIONS P/L ACN 144 869 643 QBCC LICENCE NUMBER 1192095 HEAD OFFICE 3894 PACIFIC HIGHWAY, LOGANHOLME QLD 4129 INTERNET www.simonds.com.au TELEPHONE (07) 3457 8000 ENQUIRIES Email: enquiries@simonds.com.au Ph: 1300 SIMONDS SIMONDS COPYRIGHT 2003 SIMONDS IP Pty Ltd (ACN 144 839 805) (ABN 56 144 839 805) NOT TO BE REPRODUCED IN PART OR WHOLE WITHOUT EXPRESS PERMISSION.	Spec:	SIMONDS HOMES RANGE (QLD)		View:	INTERNAL ELEVATIONS 3		V1	Scale: 1:50@A3	Date: 00.00.00	House: ARMSTRONG 32_298-14D					
		(STANDARD)		Customer:						Facade: HARLEQUIN					
		- DEVELOPMENT DIVISION PURPOSE ONLY -		Address:						Drawn: XNAMEX	Job No: XX00000XX				
										Design: X00X	Mastered: T.L	Checked: X00X			



CAD FILE: JOB NAME: TAG	PLOT DRWG FILE: CHF-FILENAME/PGE1	NOTES: ARMSTRONG 32_298-14D HARLEQUIN		
		CLIENT: NAME		
		JOB ADDRESS: NO. STREET. SUBURB		
		Drawn: XNAMEX	Date: 00.00.00	Job No: X0000X
		Scale: 1:200	Checked:	Sheet No: 11.1